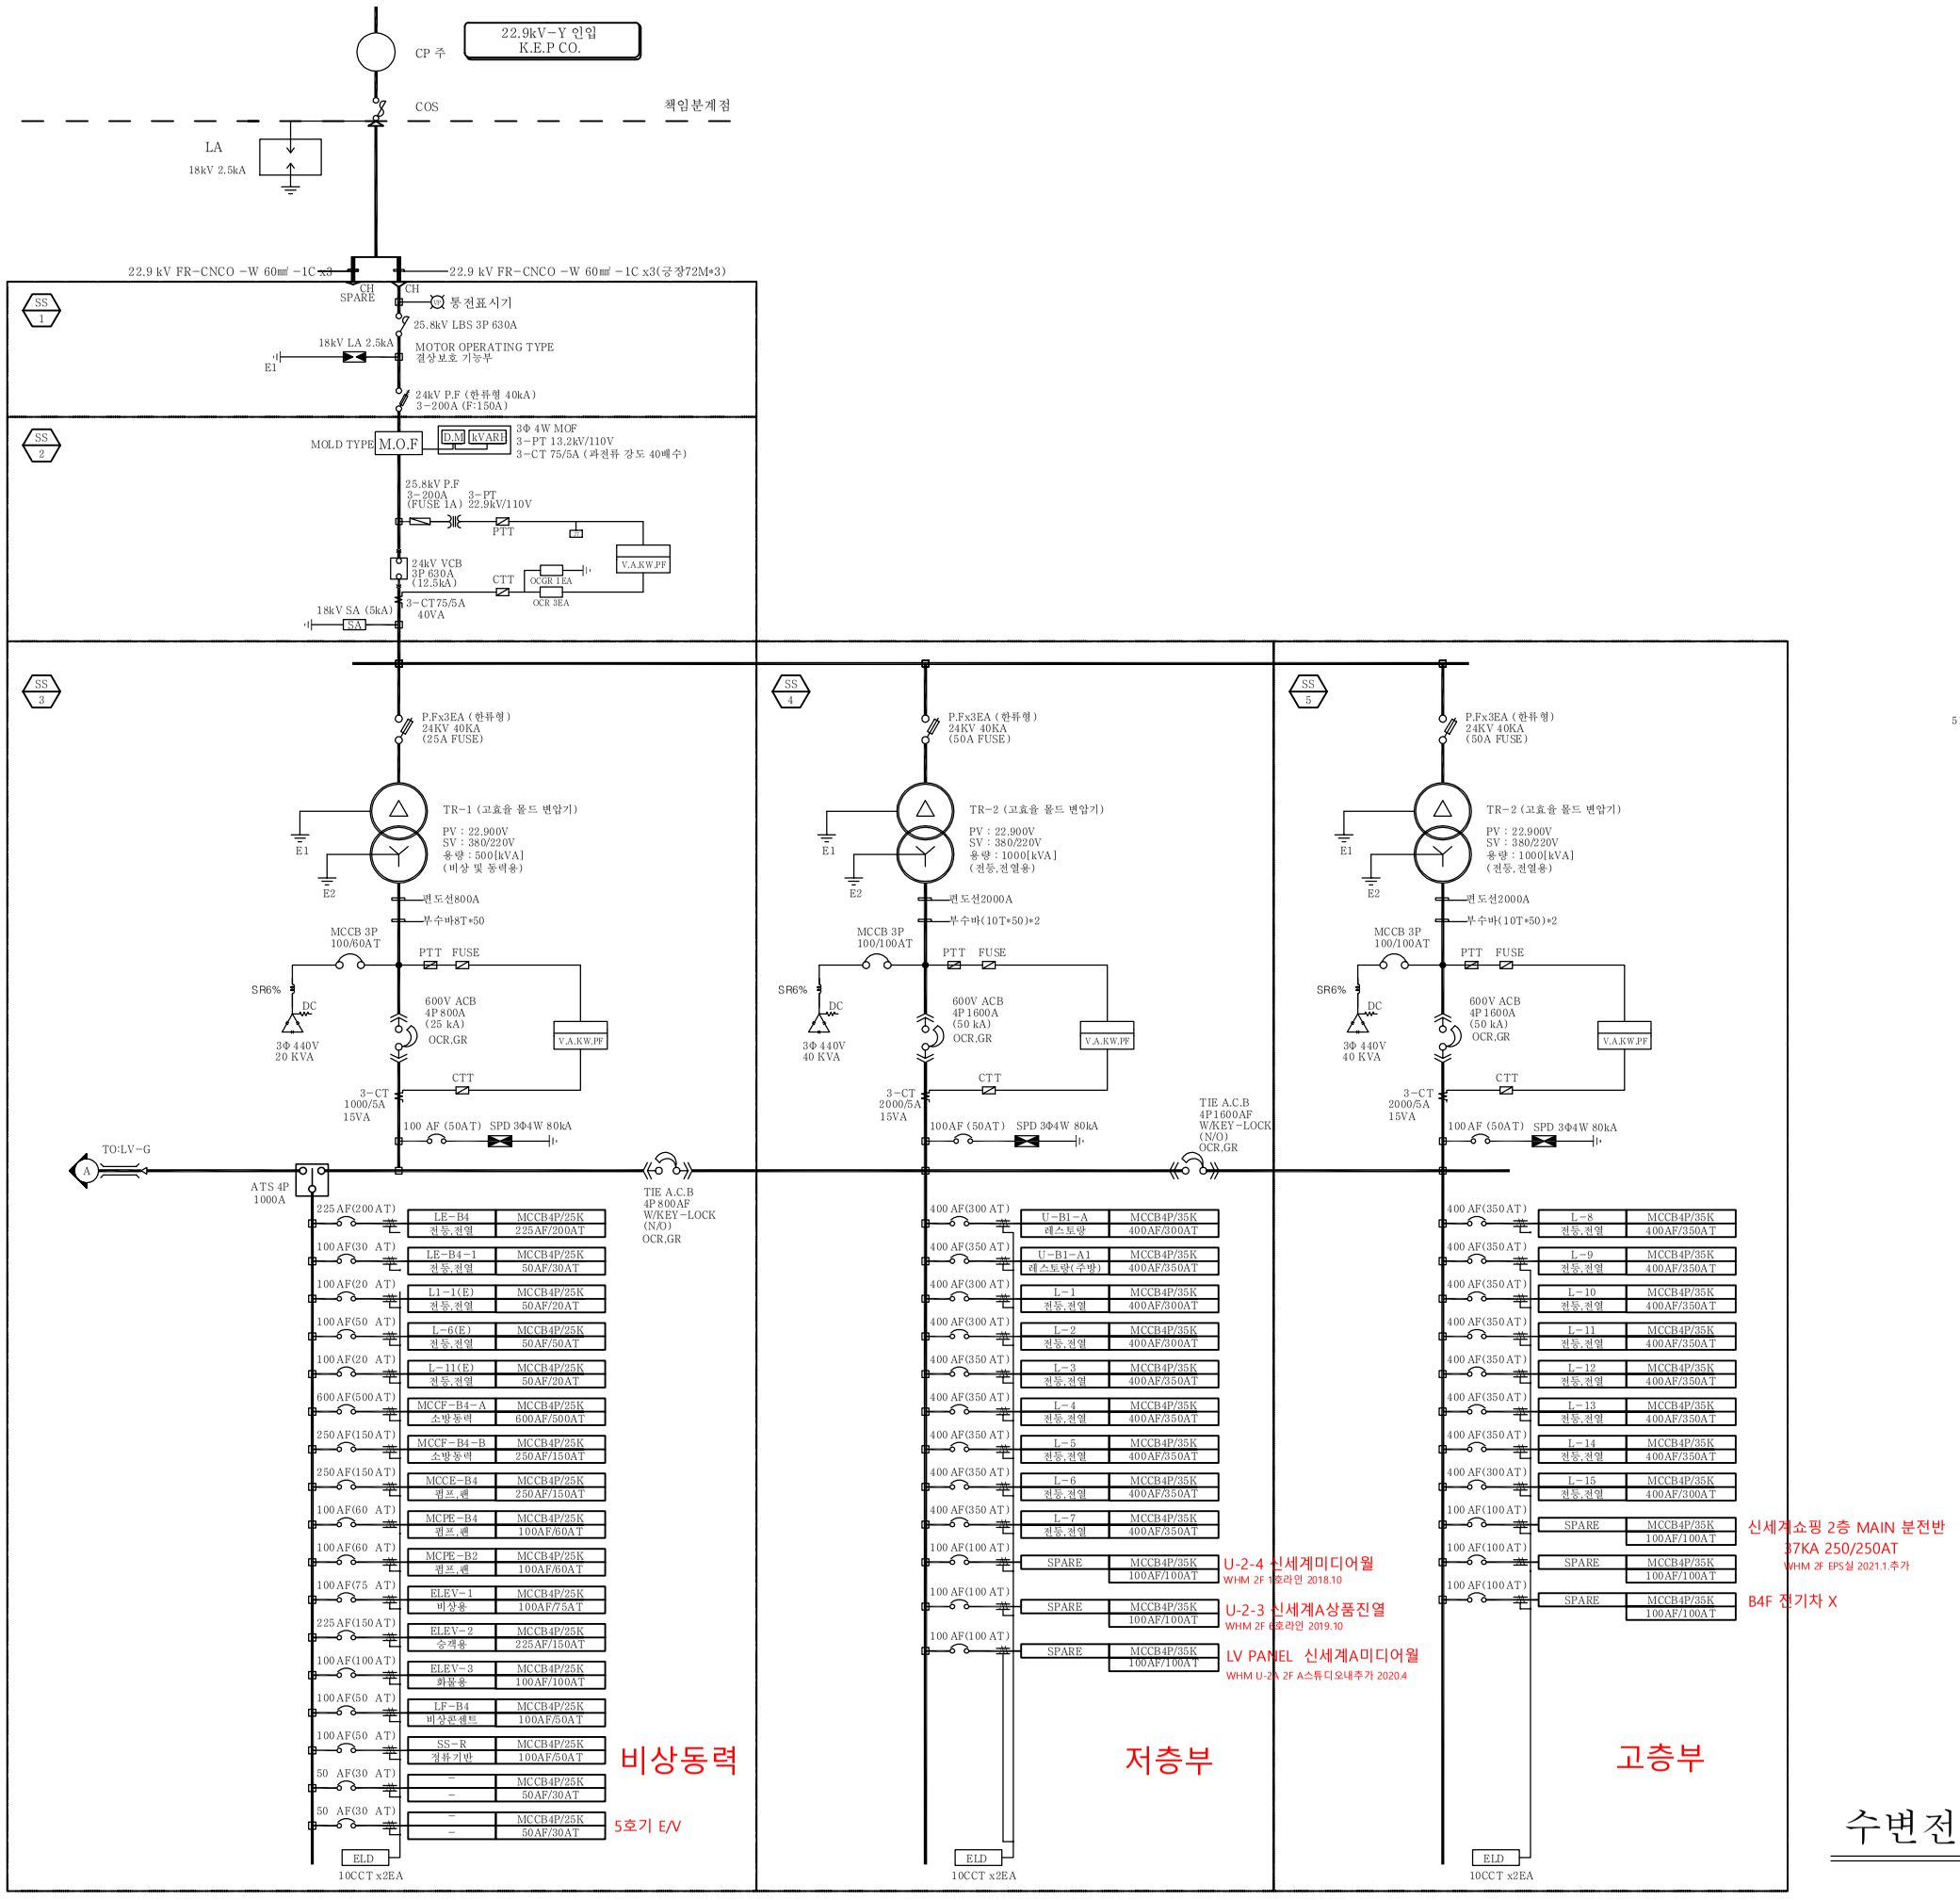

1. ACB는 인출형으로 OCR, OCGR 내장형을 사용할 것.(TIE ACB 제외)
2. 특기없는 한 CT (계기용 변류기)의 정격부담은 40VA이상
   PT (계기용 변압기)의 정격부담은 50VA 이상의 것을 사용한다.
3. 부하명칭 표기 — PANEL명 / 부 하 명
4. SYMBOL
   - ELD : Digital 누전 경보기
   - SPD : Surge Protection Device
     - M.O.V TYPE
     - CLASS I I_{imp} 150kA (10~350 μs)
5. 변압기는 고효율에너지기자재 인증제품사용할 것.
6. 배전반 내의 MCCB는 특기없는 한 4P 규격의 것을 사용할 것.
7. 배전반 내의 MCCB 차단용량

Tr \ MCCB	100AF	225AF	400AF
3Φ 500kVA	25kA이상	25kA이상	25kA이상
3Φ 1000kVA	35kA이상	35kA이상	35kA이상

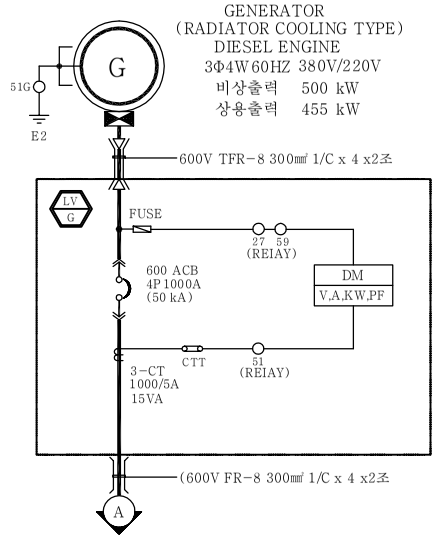

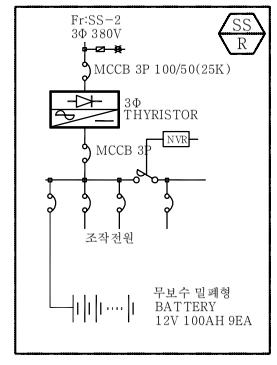

수변전설비 결선도

SCALE:NONE

녹색 에너지 설계 약정업체

종합 전기 설계업체 서울E-1-002호
종합 전기 감리업체 서울S-1-006호
엔지니어링활동주체(정보통신) 10-104호
주식회사 전기설계· **협인**

PROJECT TITLE

성수동1가 지식산업센터 신축공사

■NOTES

REVISION	DESCRIPTION	DATE

ORDER ORGAN
티티벤처인베스트먼트
TT VENTURE INVESTMENT
대표전화(02)579-8361
팩시밀리(02)579-8364

PROJECT OFFICE
(주)에이텍종합건축사사무소
ATEC ARCHITECTS & ASSOCIATES
대표전화(02)3462-6366
팩시밀리(02)3462-6329

DRAWING TITLE
수변전설비 결선도

SCALE	APPROVED
A1 : NONE A3 : NONE	
ARCHITECT: 김 상 길	
DRAWN: 강 봉 구	DATE: 2014. 03
CHECKED	DATE: 2014. 03

CONSULTANT

DRAWING NO.
E-004