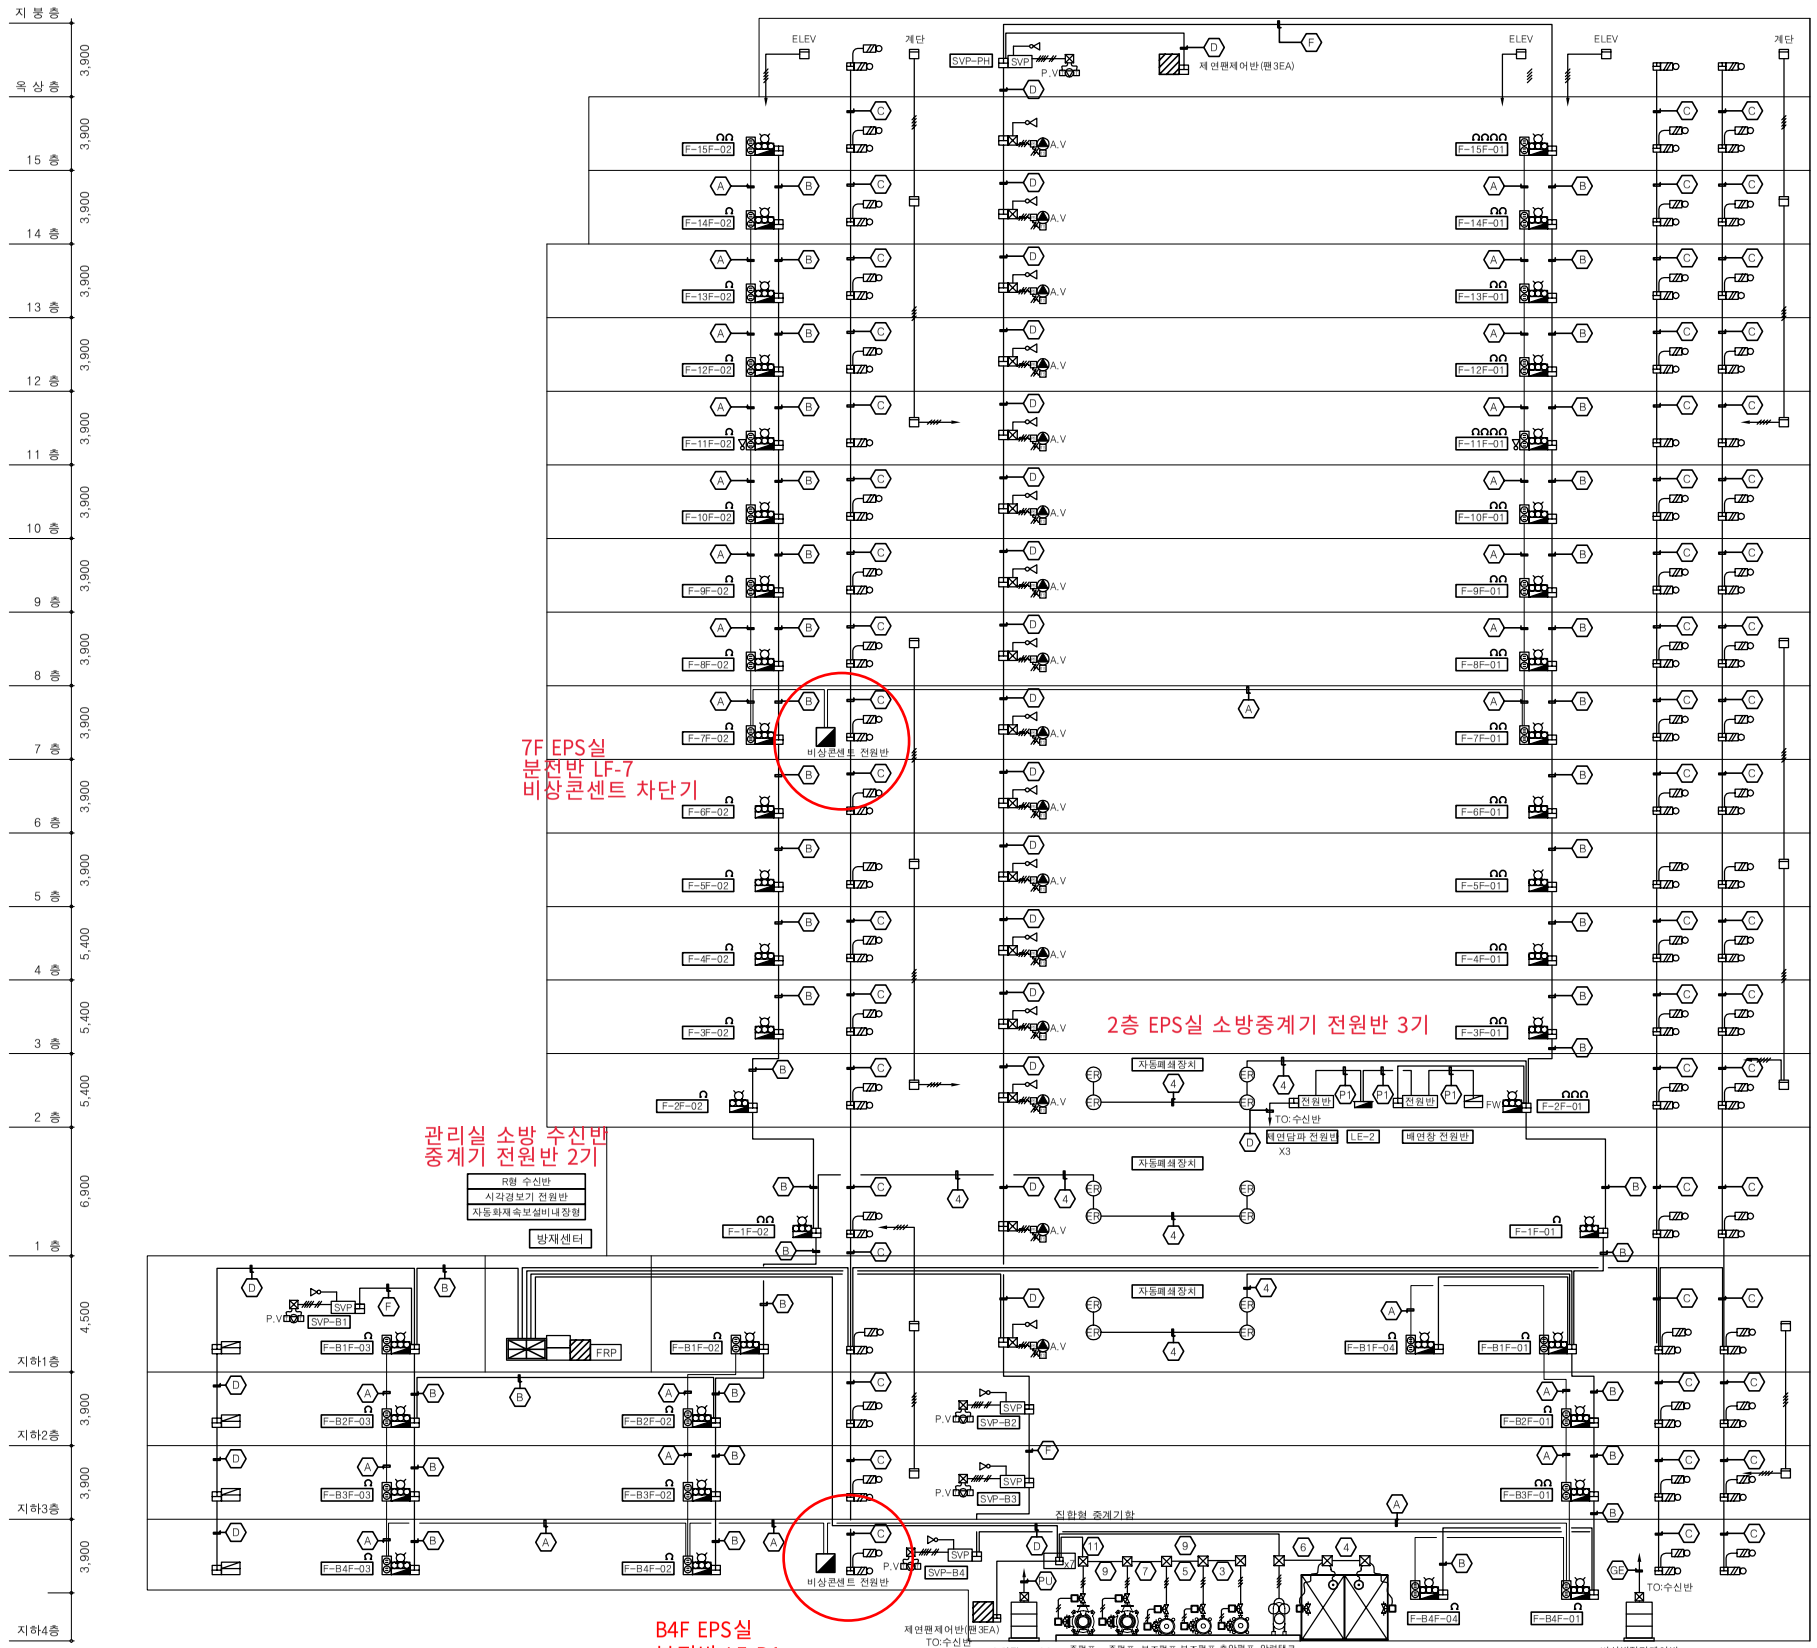

전선관 및 전선규격

기 호	Cable Schedule	비 고
A	HFIX 6" x 2 E 6" (28)	비상콘센트
B	FR-CVV-SB 1.5"-2C (16) HFIX 2.5" -8 (28) HFIX 2.5" -4 (22)	통신선2, 중계기전원2, 발신기응답1, 전화1, 위치표시등2, 소화전펌프작동확인2, 시각경보기전원2
C	FR-CVV-SB 1.5"-2C (16) HFIX 2.5" -2 HFIX 4.0" -2] (22)	통신선2, 중계기전원2, 댐파전원2
D	FR-CVV-SB 1.5"-2C (16) HFIX 2.5" -2 (16)	통신선2, 중계기전원2
E	FR-CVV-SB 1.5"-2C (16) HFIX 2.5" -2 HFIX 4.0" -2] (22)	통신선2, 중계기전원2, 배연창전원2
F	FR-CVV-SB 1.5"-2C (16) HFIX 2.5" -4 (22)	통신선2, 중계기전원2, 전화2
G	FR-CVV-SB 1.5"-2C (16)	통신선2
M	HFIX 2.5" -2 (16)	중계기전원2,
SE	FR-3 2.5"-4C (28)	발전기 감시반
PU	FR-3 2.5"-8C (36) FR-3 2.5"-12C (36)	소화펌프 기동반
PA	HFIX 6㎟-2, E6 (28)	전원반 전원

HFIX 1.5" x 2 (16)
HFIX 1.5" x 4 (16)
HFIX 1.5" x 8 (22)

번 호	전선수및전선관굵기	번 호	전선수및전선관굵기
1	HFIX 2.5" x 1 (16)	7	HFIX 2.5" x 7 (28)
2	HFIX 2.5" x 2 (16)	8	HFIX 2.5" x 8 (28)
3	HFIX 2.5" x 3 (16)	9	HFIX 2.5" x 9 (28)
4	HFIX 2.5" x 4 (22)	10	HFIX 2.5" x 10 (28)
5	HFIX 2.5" x 5 (22)	11	HFIX 2.5" x 11 (36)
6	HFIX 2.5" x 6 (22)	12	HFIX 2.5" x 12 (36)

화재수신반(R형 508회로)

번 호	회로명	회로수
1	자동화재탐지설비	57
2	계단	6
3	EV	3
4	방화샷다	8
5	SVP	10
6	AV	16
7	배연창	1
8	자동폐쇄장치	6
9	저수위경보	2
10	제연복합담파	3
11	제연담파	59
12	제연급기	59
13	제연배기	59
14	수동조작확인 S/W	59
15	댐 퍼S/W(SVP)	5
16	댐 퍼S/W(AV)	16
17	댐 퍼S/W(펌프)	7
18	댐 퍼S/W(저수위)	2
소 계		378
여 유		130
합 계		508

비고
- 비상측전지 내장
- 오작동 방지장치 내장
- 청각장애인용시각경보기와연동
- 배연창과연동
- 제연담파와연동
- 자동폐쇄장치와연동

자동화재탐지설비 계통도

SCALE : NONE

녹색 에너지 설계 약정업체

종합 전기 설계업체 서울E-1-002호
종합 전기 감리업체 서울S-1-006호
엔지니어링활동주체(정보통신) 10-104호
주식회사 전기설계· **협인**

PROJECT TITLE

성수동1가 지식산업센터 신축공사

■NOTES

REVISION	DESCRIPTION	DATE

ORDER ORGAN
티티벤처인베스트먼트
VENTURE INVESTMENTS
대 표전 화(02)579-8361
팩시밀리(02)579-8364

PROJECT OFFICE
(주)에이텍종합건축사사무소
ATEC ARCHITECTS & ASSOCIATES
대 표전 화(02)3462-6366
팩시밀리(02)3462-6332

DRAWING TITLE
자동화재탐지설비 계통도

SCALE	APPROVED
A1 : NONE A3 : NONE	
ARCHITECT	김 상 길
DRAWN 남 창 모	DATE 2014. 03
CHECKED	DATE 2014. 03

CONSULTANT

DRAWING NO.
EF-003