

PROJECT TITLE


성수동1가
지식산업센터
신축공사

NOTES

주기사항			
심볼	품 명	기 호	비 고
	자동 차단기	CG	자립형
	주차권 발행기	TD	자립형
	차량번호 인식기/전광판	LPR/DR	자립형
	유인요금계산기	FC	탁상형
	차량 검지기	D	벽매입형
	LOOP COIL	LC	바닥매입형
	주차관리 컴퓨터	HC	탁상형
	장내경광등	AS	천정형
	출차주의등	COW	자립형
	단면유도등	S	천칭형
	양면유도등	SS	천칭형

배관 및 배선		
번호	배 선	배 관
(A)	HFIX 2.5Q/3C - 접지선 포함	(16C)
(B)	CV 6SQ/3C - 접지선 포함	(28C)
(C)	CV 4SQ/3C - 접지선 포함	(28C)
(D)	FTP (CAT.5e) CABLE 4P	(16C)
(E)	UTP (CAT.5e) CABLE 4P	(16C)
(F)	UTP (CAT.5e) CABLE 4P X2	(16C)
(G)	UTP (CAT.5e) CABLE 4P X3	(22C)
—는 AC 220V IN		
—는 HFIX 2.5Q/3C (16C) 임.		

LAYOUT-A 주출입구

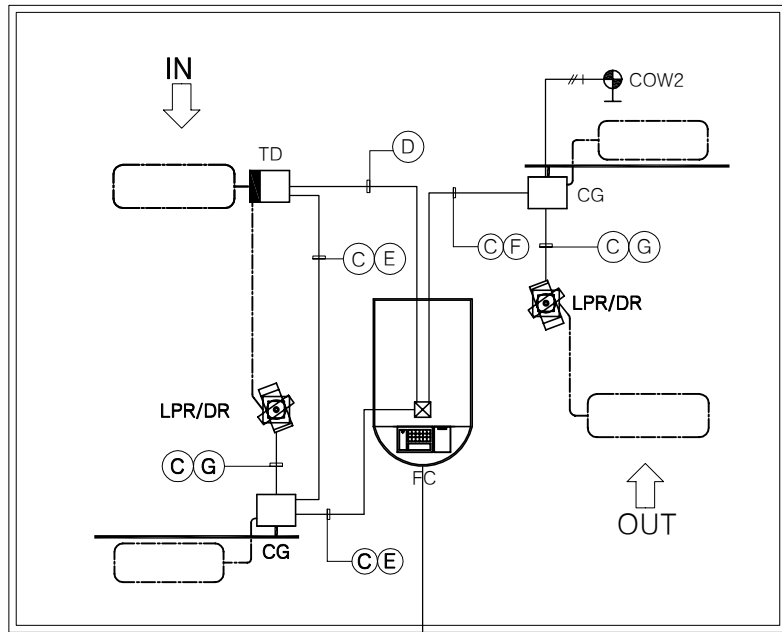

*주차안내판
층별 EPS실 분전반 - ELB 주차안내


*주차관재경광등
B1F EPS실 분전반 메인연결 - ELB 주차관재

지상1층

주차관재 경광등

방재실


주차안내판

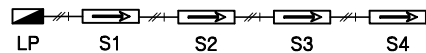

지하1층


아이파크1F 주차관제

주차안내판

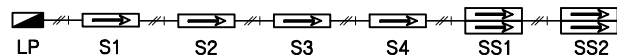


지하2층

주차안내판

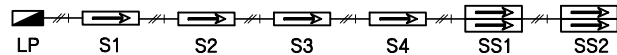


지하3층

주차안내판

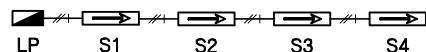

지하4층

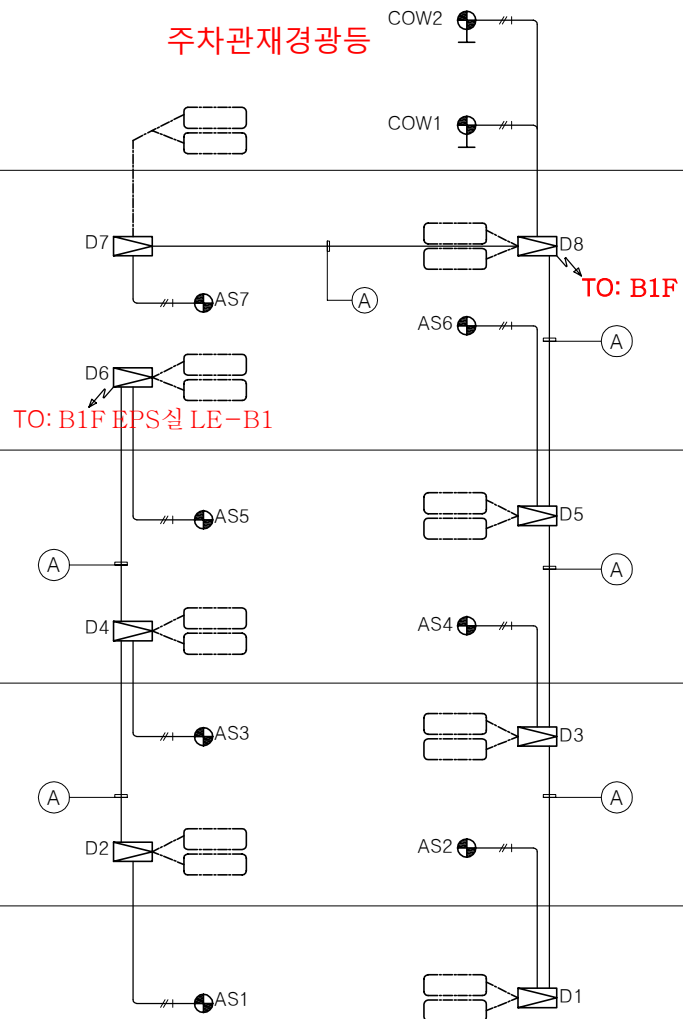

주차관제설비 계통도

SCALE:NONE

녹색 에너지 설계 약정업체
종합 전기 설계업체 서울E-1-0023
종합 전기 관리업체 서울S-1-0063
연지니어링플랫폼주제(정보통신) 10-104호
주식회사 전기설계. 협인


REVISION	DESCRIPTION	DATE
ORDER ORGAN		
T 터티벤처인베스트먼트		
INVESTMENT		
PROJECT OFFICE		
ATEC (주)에이텍종합건축사사무소		
ARCHITECTS & ASSOCIATES		
DRAWING TITLE		
주차관제설비 계통도		
SCALE	APPROVED	
A1 : NONE A3 : NONE	ARCHITECT 김 상 길	
DRAWN	강 봉 구	DATE 2014. 03
CHECKED		DATE 2014. 03
CONSULTANT		
DRAWING NO.	T-301	

PROJECT TITLE

성수동1가
지식산업센터
신축공사

NOTES

- 객석 유도등 전환반
○ 객석 유도등

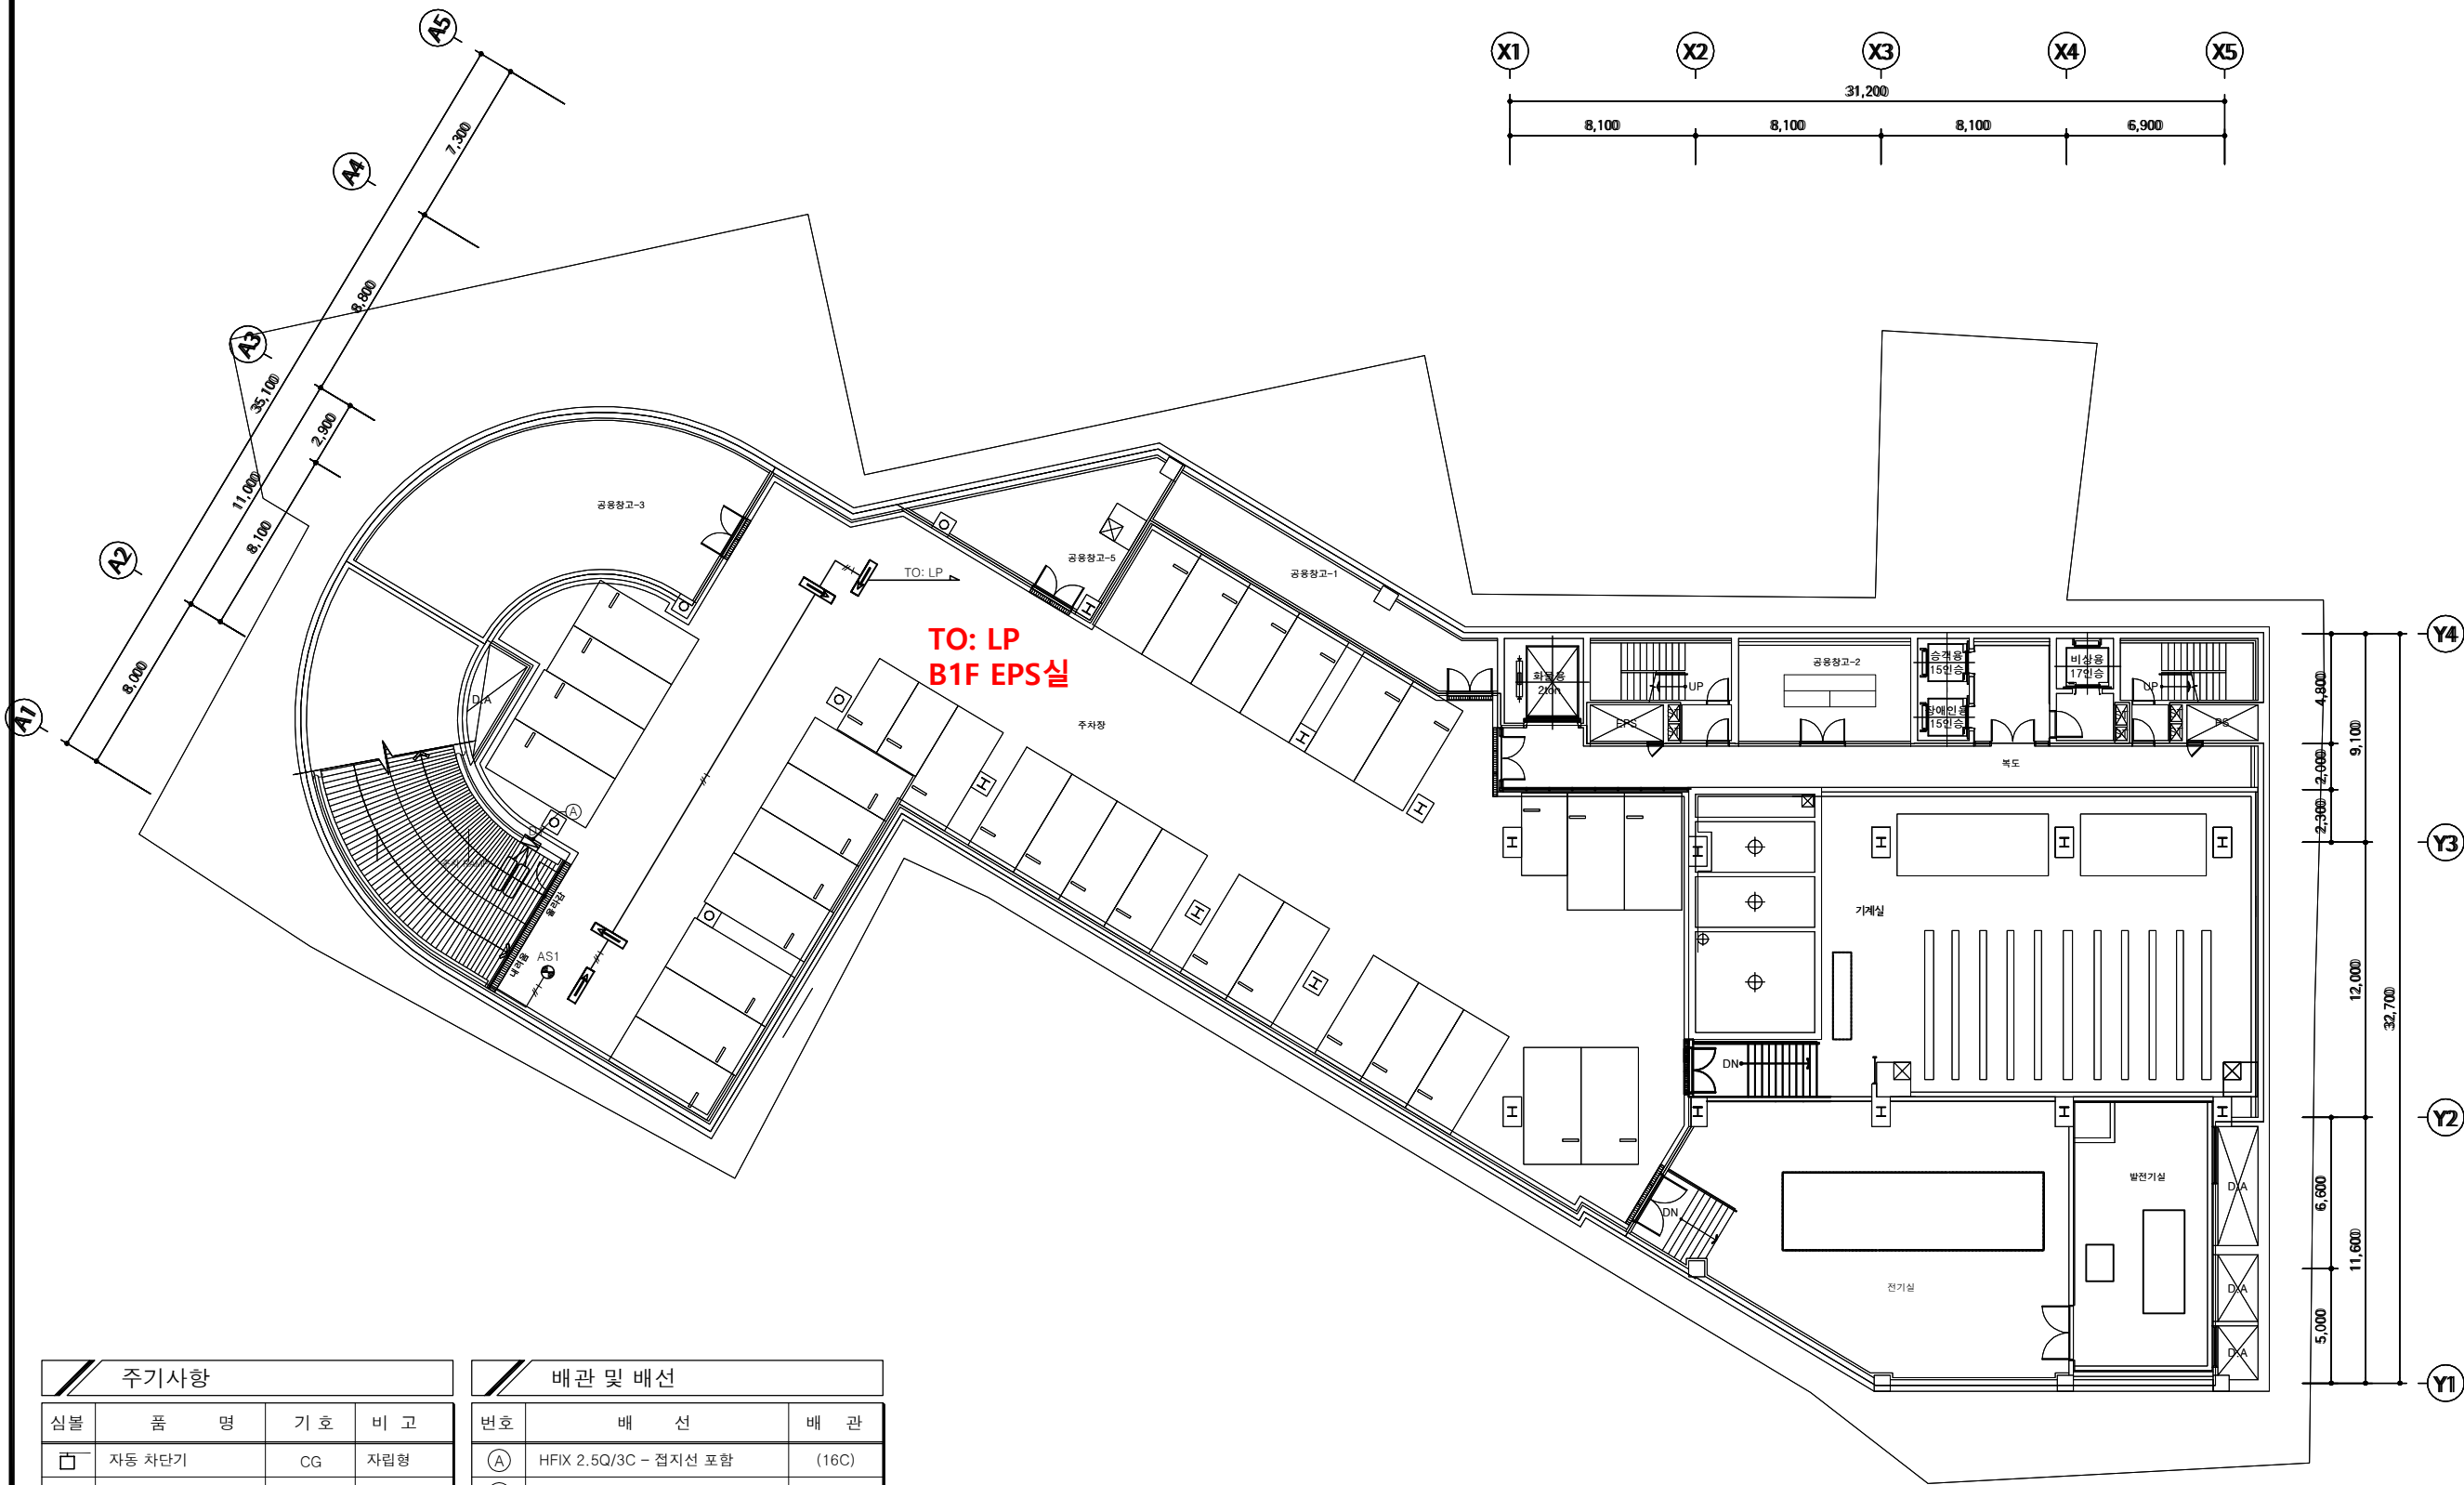

주기사항			
심볼	품 명	기 호	비 고
	자동 차단기	CG	자립형
	주차권 발행기	TD	자립형
	차량번호 인식기/전광판	LPR/DR	자립형
	유연요금계산기	FC	탁상형
	차량 검지기	D	벽매입형
	LOOP COIL	LC	바닥매입형
	주차관리 컴퓨터	HC	탁상형
	장내경광등	AS	천정형
	출차주의등	COW	자립형
	단면유도등	S	천청형
	양면유도등	SS	천청형

배관 및 배선		
번호	배 선	배 관
(A)	HFIX 2.5Q/3C - 접지선 포함	(16C)
(B)	CV 6SQ/3C - 접지선 포함	(28C)
(C)	CV 4SQ/3C - 접지선 포함	(28C)
(D)	FTP (CAT.5e) CABLE 4P	(16C)
(E)	UTP (CAT.5e) CABLE 4P	(16C)
(F)	UTP (CAT.5e) CABLE 4P X2	(16C)
(G)	UTP (CAT.5e) CABLE 4P X3	(22C)
—□— 는 AC 220V IN		
—//— 는 HFIX 2.5Q/3C (16C) 임.		

지하 4층 주차관제설비 평면도

SCALE:1/150

녹색 에너지 설계 약정업체
종합 전기 설계업체 서울E-1-0023
종합 전기 관리업체 서울S-1-0063
연지니어링플랫폼주제(정보통신) 10-104호
주식회사 전기설계. 협인

REVISION DESCRIPTION DATE

ORDER ORGAN

INVESTMENT
T 터티벤치인베스트먼트
대표전화021579-8361
팩시밀리021579-8364

PROJECT OFFICE

ATEC(주)에이텍종합건축사사무소
ARCHITECTS & ASSOCIATES
대표전화0213462-6366
팩시밀리0213462-6368

DRAWING TITLE

지하 4층 주차관제설비 평면도

SCALE

A1 : 1 / 150

A3 : 1 / 300

APPROVED

ARCHITECT 김 상 길

DRAWN

강 봉 구

DATE

2014. 03

CHECKED

DATE

2014. 03

CONSULTANT

DRAWING NO.

T-302

PROJECT TITLE

성수동1가
지식산업센터
신축공사

NOTES

REVISION	DESCRIPTION	DATE

ORDER ORGAN
TT 터티벤처인베스트먼트
INVESTMENT
대표전화 021579-8361
팩시밀리 021579-8364

PROJECT OFFICE
ATEC (주)에이텍종합건축사사무소
ARCHITECTS & ASSOCIATES
대표전화 0213462-6366
팩시밀리 0213462-6368


DRAWING TITLE

1층 주차관제설비 평면도

SCALE	APPROVED
A1 : 1 / 150 A3 : 1 / 300	ARCHITECT 김 상 길
DRAWN	DATE
강 봉 구	2014. 03
CHECKED	DATE
	2014. 03
CONSULTANT	

DRAWING NO.

T-306

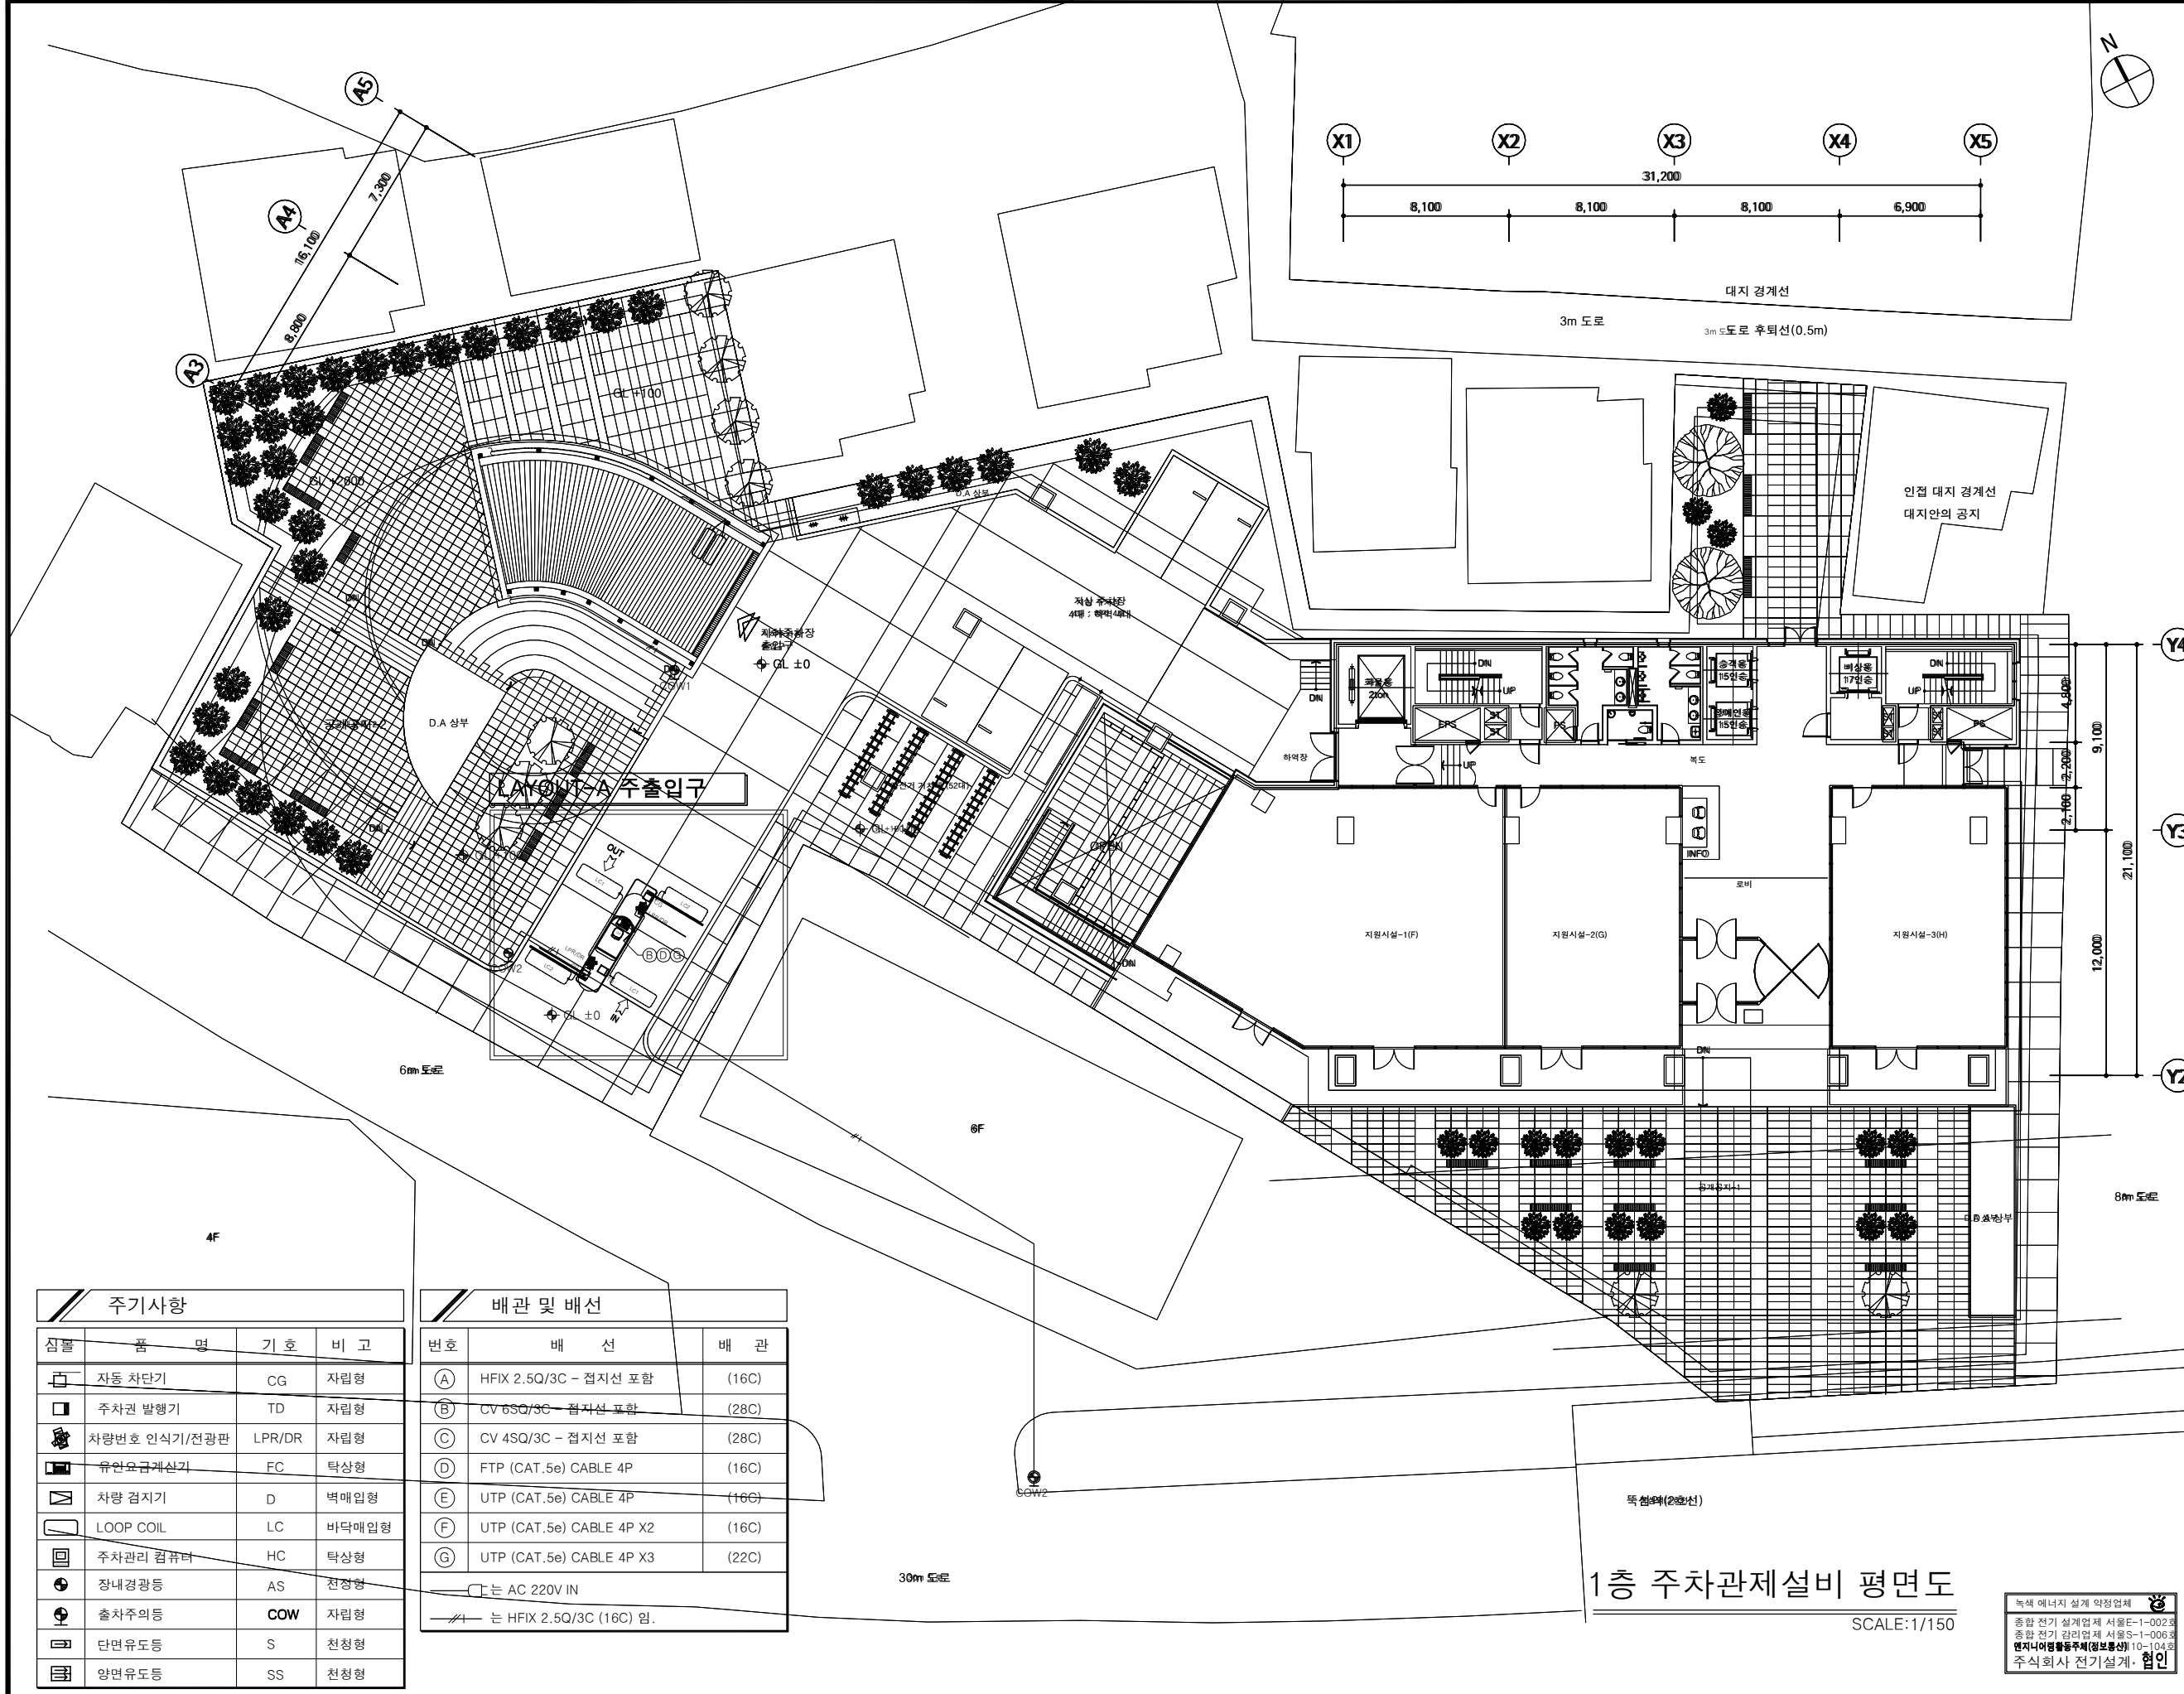

주기사항			
심볼	품 명	기 호	비 고
	자동차 단기	CG	자립형
	주차권 발행기	TD	자립형
	차량번호 인식기/전광판	LPR/DR	자립형
	유안요금계산기	FC	탁상형
	차량 검지기	D	벽매입형
	LOOP COIL	LC	바닥매입형
	주차관리 컴퓨터	HC	탁상형
	장내경광등	AS	천장형
	출차주의등	COW	자립형
	단면유도등	S	천장형
	양면유도등	SS	천장형

배관 및 배선		
번호	배 선	배 관
(A)	HFIX 2.5Q/3C - 접지선 포함	(16C)
(B)	CV 6SQ/3C - 접지선 포함	(28C)
(C)	CV 4SQ/3C - 접지선 포함	(28C)
(D)	FTP (CAT.5e) CABLE 4P	(16C)
(E)	UTP (CAT.5e) CABLE 4P	(16C)
(F)	UTP (CAT.5e) CABLE 4P X2	(16C)
(G)	UTP (CAT.5e) CABLE 4P X3	(22C)
— 는 AC 220V IN		
— 는 HFIX 2.5Q/3C (16C) 임.		

1층 주차관제설비 평면도


SCALE:1/150

녹색 에너지 설계 약정업체
종합 전기 설계업체 서울E-1-002호
종합 전기 감리업체 서울S-1-006호
연지니아명물동주세(정보통신) 10-104호
주식회사 전기설계. 협인

PROJECT TITLE

성수동1가
지식산업센터
신축공사

NOTES

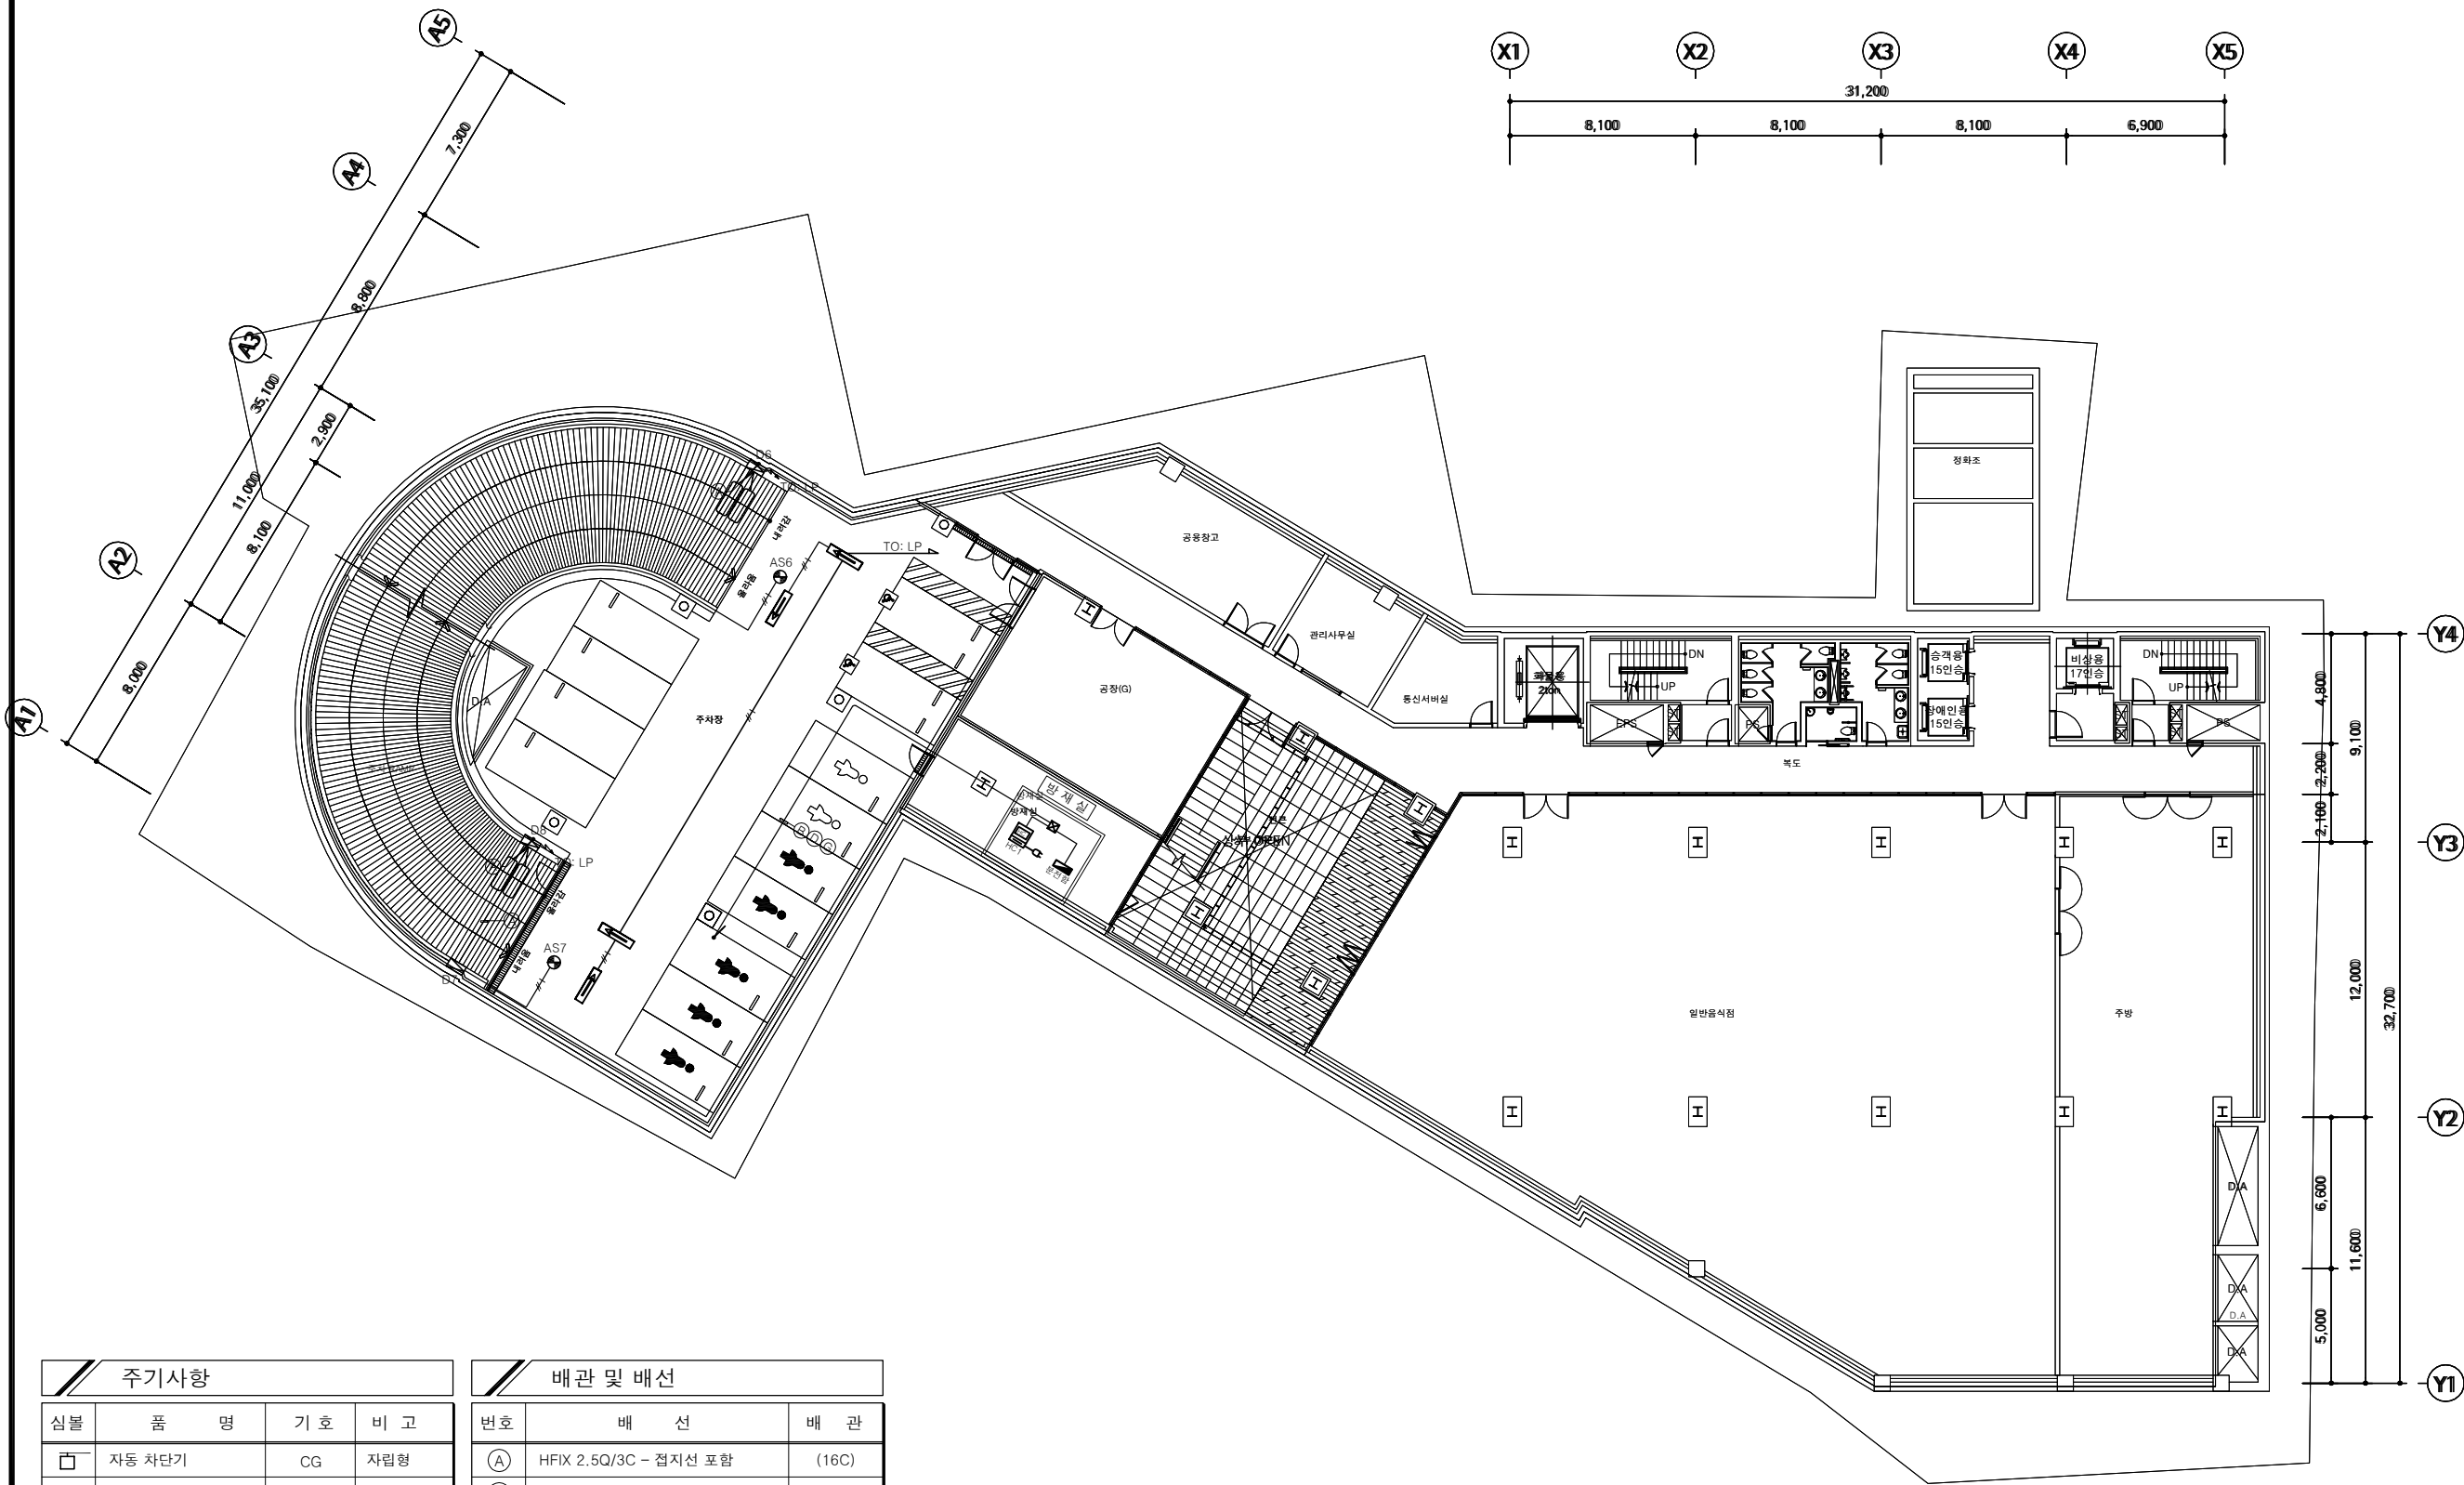

주기사항			
심볼	품명	기호	비고
	자동 차단기	CG	자립형
	주차권 발행기	TD	자립형
	차량번호 인식기/전광판	LPR/DR	자립형
	유인요금계산기	FC	탁상형
	차량 검지기	D	벽매입형
	LOOP COIL	LC	바닥매입형
	주차관리 컴퓨터	HC	탁상형
	장내경광등	AS	천정형
	출차주의등	COW	자립형
	단면유도등	S	천정형
	양면유도등	SS	천정형

배관 및 배선		
번호	배선	배관
(A)	HFIX 2.5Q/3C - 접지선 포함	(16C)
(B)	CV 6SQ/3C - 접지선 포함	(28C)
(C)	CV 4SQ/3C - 접지선 포함	(28C)
(D)	FTP (CAT.5e) CABLE 4P	(16C)
(E)	UTP (CAT.5e) CABLE 4P	(16C)
(F)	UTP (CAT.5e) CABLE 4P X2	(16C)
(G)	UTP (CAT.5e) CABLE 4P X3	(22C)
—□— 는 AC 220V IN		
—//— 는 HFIX 2.5Q/3C (16C) 임.		

지하 1층 주차관제설비 평면도
SCALE:1/150

녹색 에너지 설계 약정업체
종합 전기 설계업체 서울E-1-0023
종합 전기 감리업체 서울S-1-0063
연지니어링공동주제(정보통신) 10-104호
주식회사 전기설계 협인

REVISION DESCRIPTION DATE

ORDER ORGAN

INVESTMENT
터티벤처인베스트먼트
대표전화021579-8361
팩시밀리021579-8364

PROJECT OFFICE

ATEC(주)에이텍종합건축사사무소
ARCHITECTS & ASSOCIATES
대표전화021462-6366
팩시밀리021462-6368

DRAWING TITLE

지하 1층 주차관제설비 평면도

SCALE

A1 : 1 / 150
A3 : 1 / 300

APPROVED

ARCHITECT 김 상 길

DRAWN 강 봉 구

DATE 2014. 03

CHECKED

DATE 2014. 03


CONSULTANT

DRAWING NO. T-305

PROJECT TITLE

성수동1가
지식산업센터
신축공사

NOTES

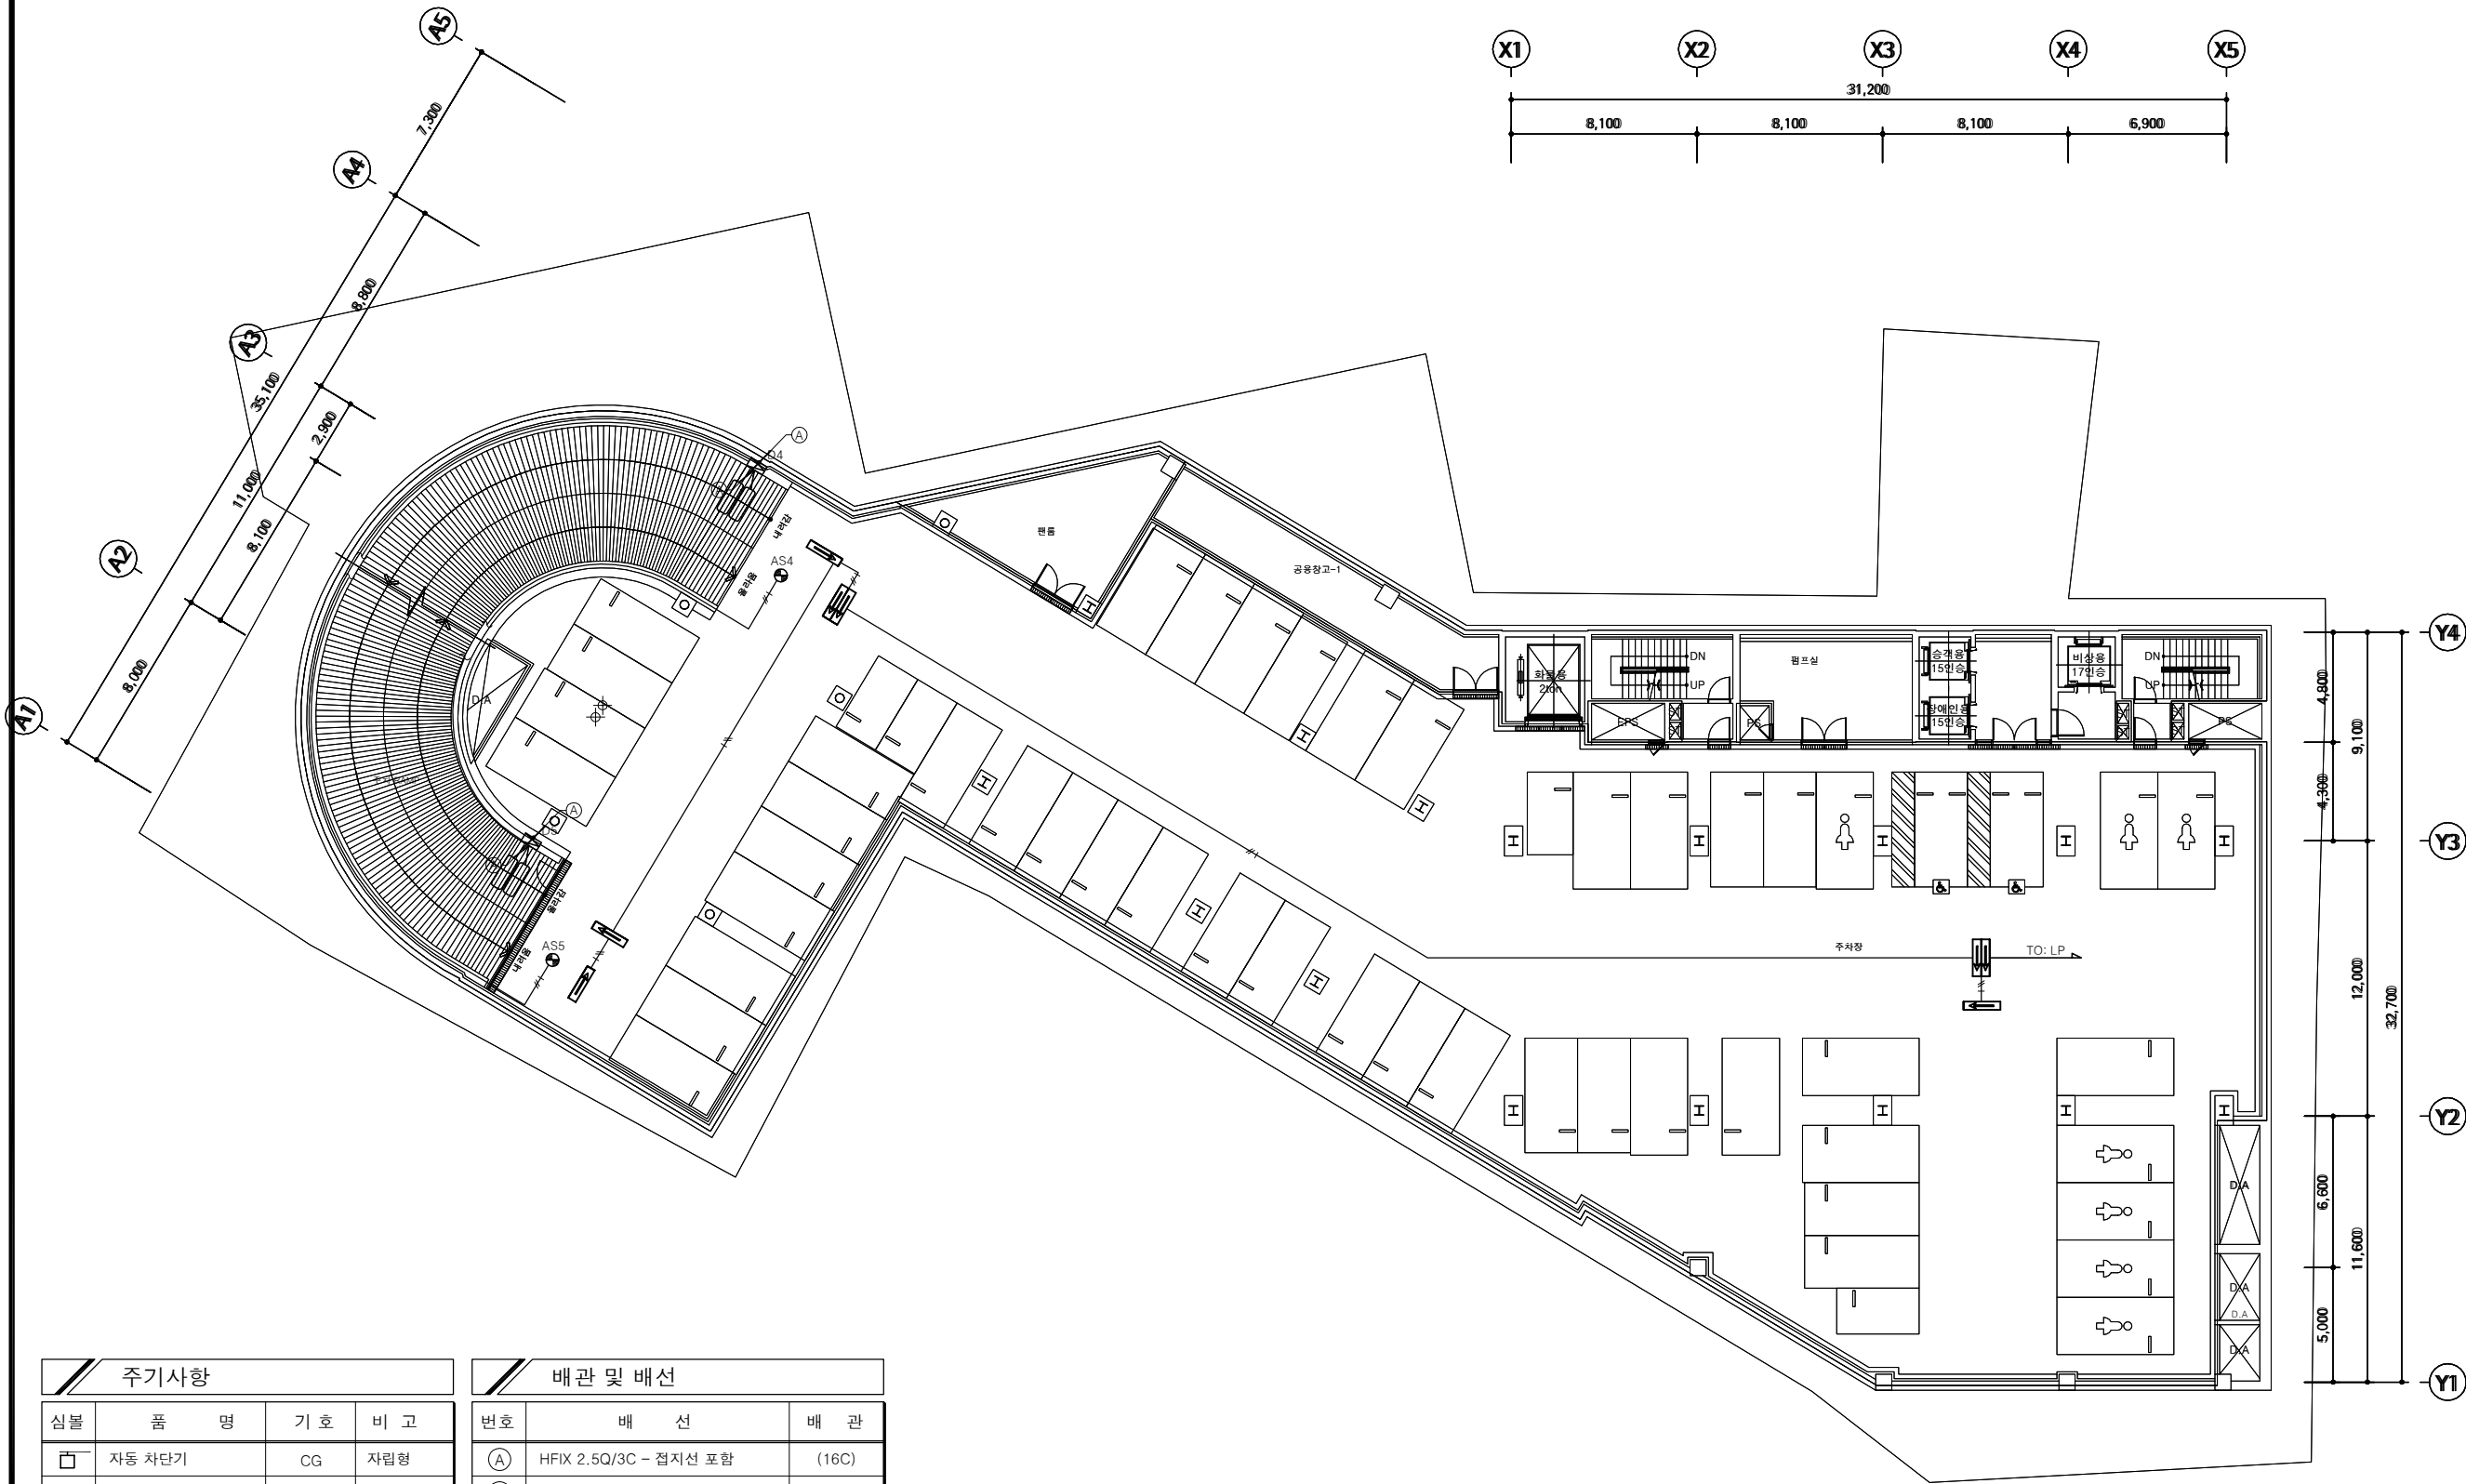

주기사항			
심볼	품 명	기 호	비 고
	자동 차단기	CG	자립형
	주차권 발행기	TD	자립형
	차량번호 인식기/전광판	LPR/DR	자립형
	유연요금계산기	FC	탁상형
	차량 검지기	D	벽매입형
	LOOP COIL	LC	바닥매입형
	주차관리 컴퓨터	HC	탁상형
	장내경광등	AS	천정형
	출차주의등	COW	자립형
	단면유도등	S	천청형
	양면유도등	SS	천청형

배관 및 배선		
번호	배 선	배 관
(A)	HFIX 2.5Q/3C - 접지선 포함	(16C)
(B)	CV 6SQ/3C - 접지선 포함	(28C)
(C)	CV 4SQ/3C - 접지선 포함	(28C)
(D)	FTP (CAT.5e) CABLE 4P	(16C)
(E)	UTP (CAT.5e) CABLE 4P	(16C)
(F)	UTP (CAT.5e) CABLE 4P X2	(16C)
(G)	UTP (CAT.5e) CABLE 4P X3	(22C)
—□— 는 AC 220V IN		
—//— 는 HFIX 2.5Q/3C (16C) 임.		

지하 2층 주차관제설비 평면도
SCALE:1/150

녹색 에너지 설계 약정업체
종합 전기 설계업체 서울E-1-0023
종합 전기 감리업체 서울S-1-0063
연지니아종합건축(정보통선) 10-104호
주식회사 전기설계. 협인

REVISION DESCRIPTION DATE

ORDER ORGAN

INVESTMENT
티티벤처인베스트먼트
대표전화021579-8361
팩시밀리021579-8364

PROJECT OFFICE

ATEC(주)에이텍종합건축사사무소
ARCHITECTS & ASSOCIATES
대표전화0213462-6366
팩시밀리0213462-6368

DRAWING TITLE

지하 2층 주차관제설비 평면도

SCALE

A1 : 1 / 150
A3 : 1 / 300

APPROVED

ARCHITECT 김 상 길

DRAWN

강 봉 구

DATE

2014. 03

CHECKED

DATE

2014. 03

CONSULTANT


DRAWING NO.

T-304

PROJECT TITLE

성수동1가
지식산업센터
신축공사

NOTES

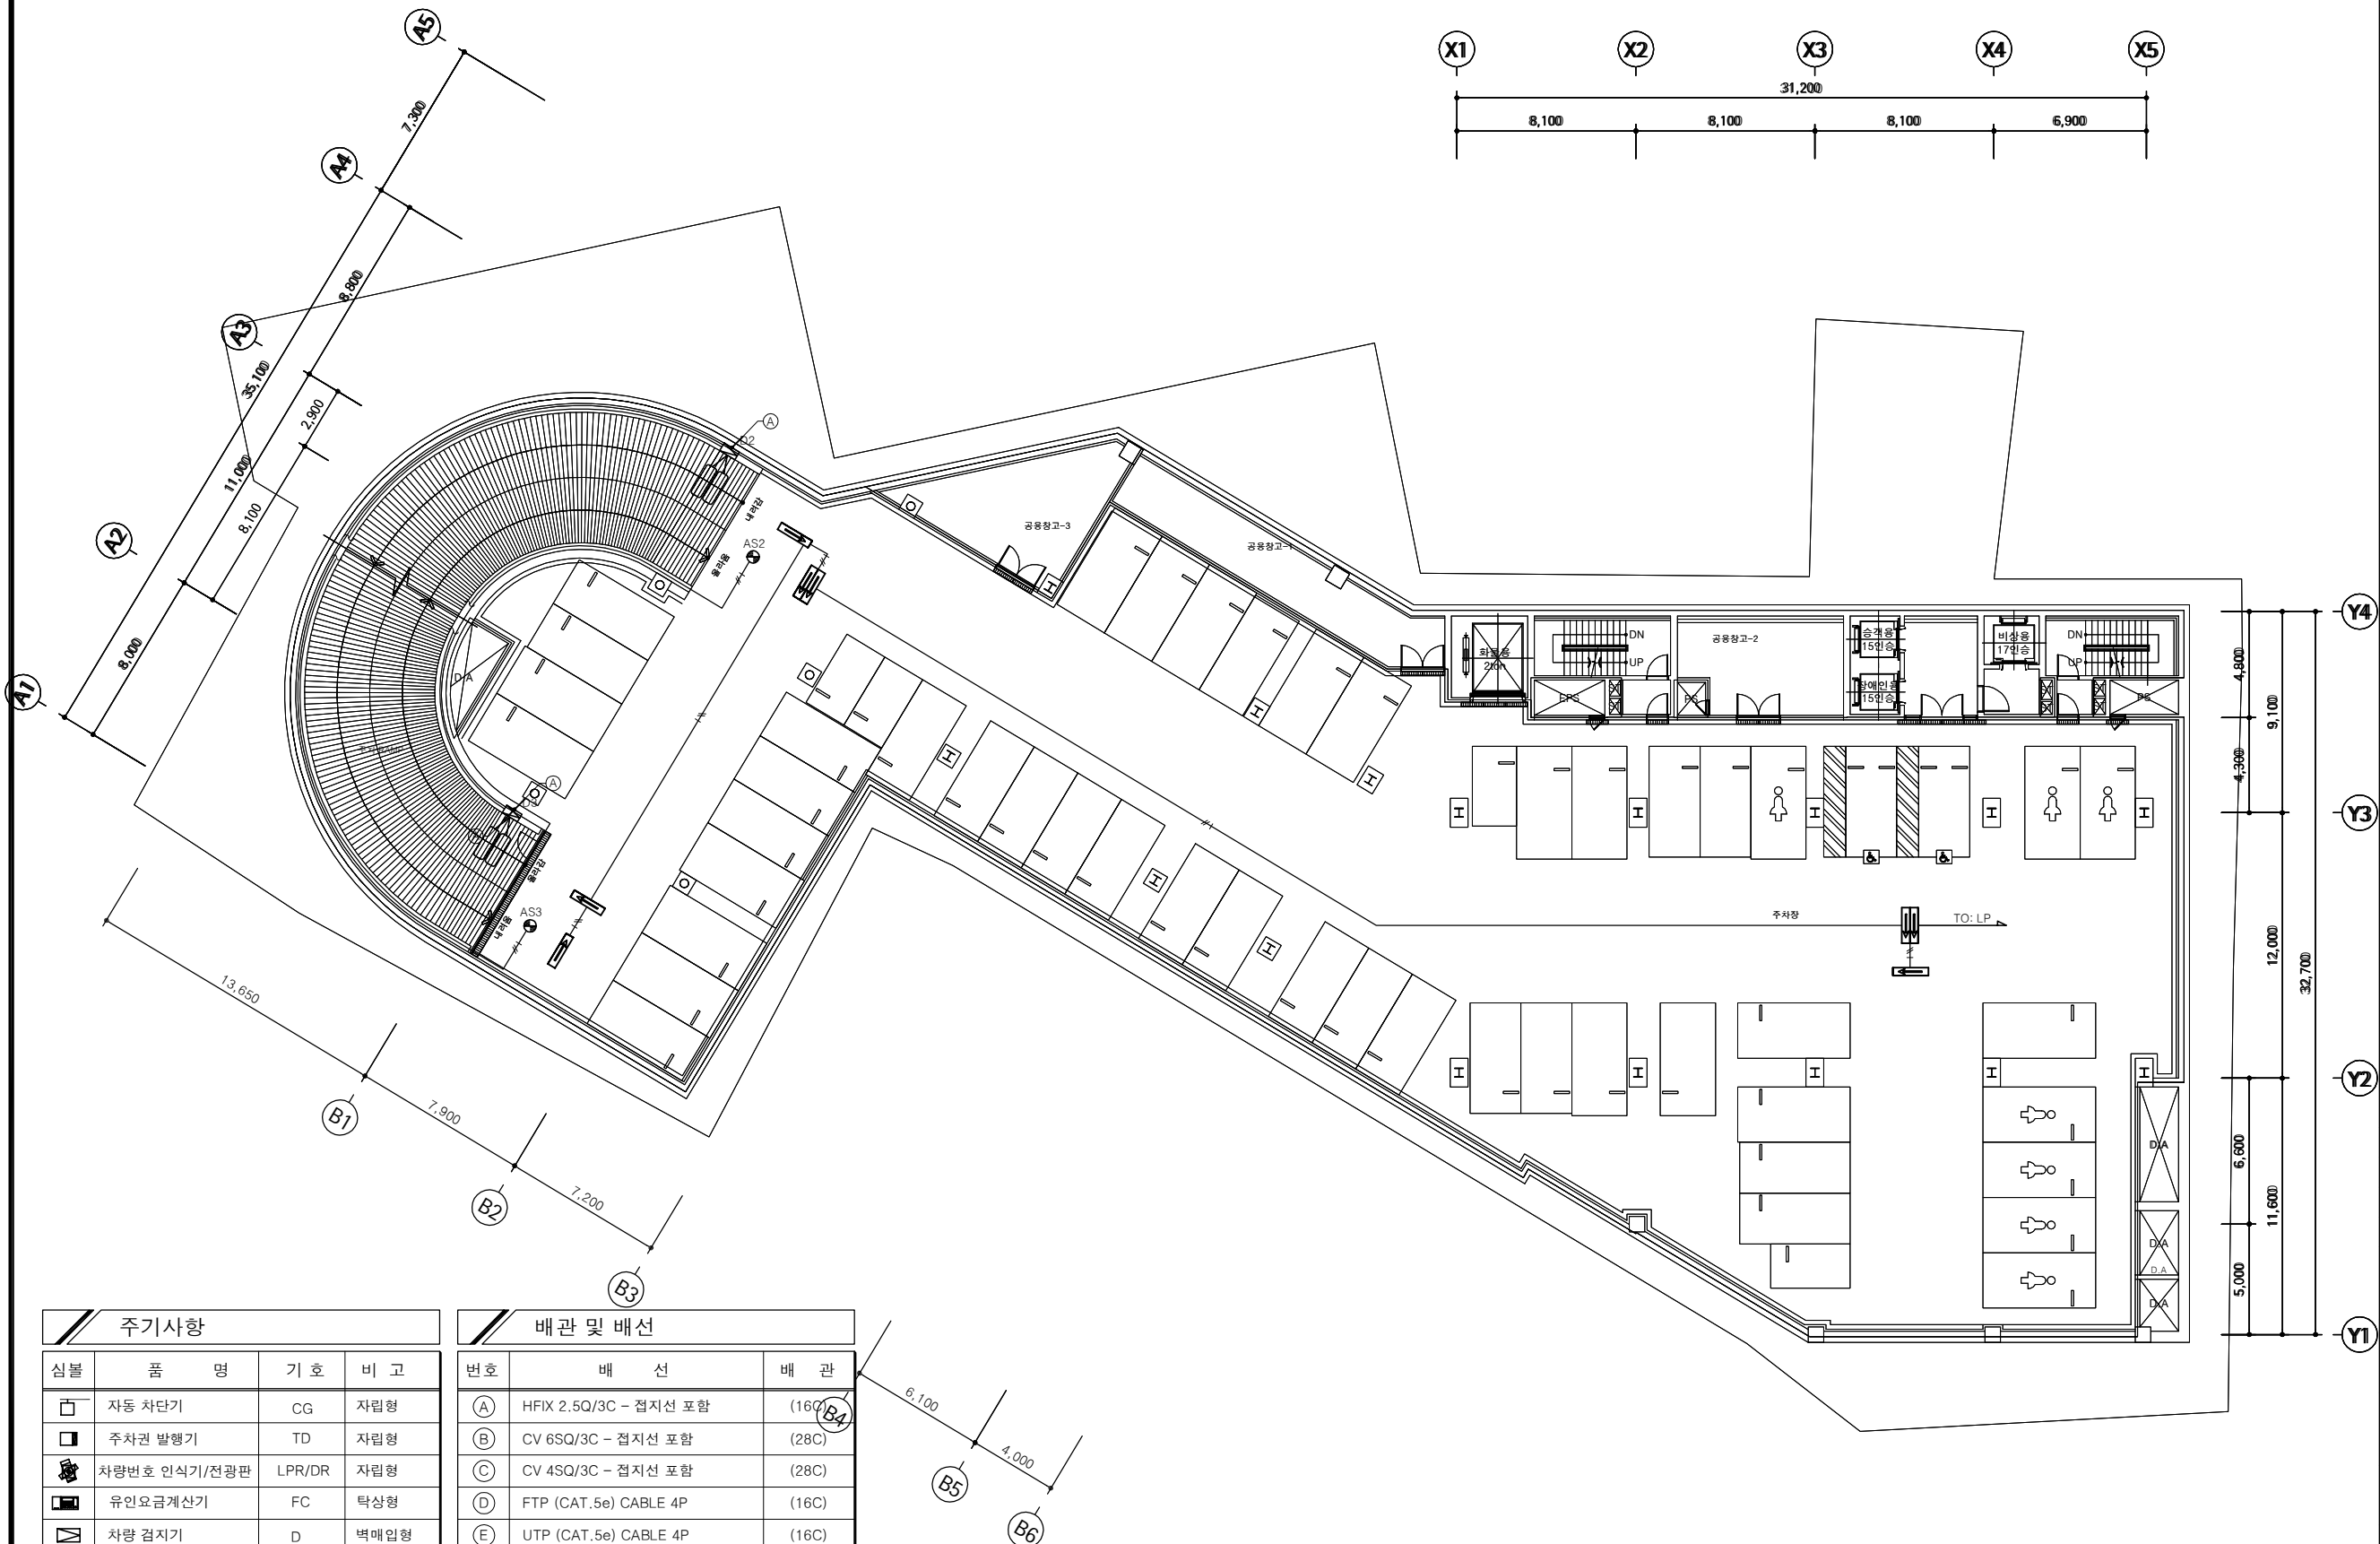

주기사항			
심볼	품명	기호	비고
	자동 차단기	CG	자립형
	주차권 발행기	TD	자립형
	차량번호 인식기/전광판	LPR/DR	자립형
	유인요금계산기	FC	탁상형
	차량 검지기	D	벽매입형
	LOOP COIL	LC	바닥매입형
	주차관리 컴퓨터	HC	탁상형
	장내경광등	AS	천정형
	출차주의등	COW	자립형
	단면유도등	S	천칭형
	양면유도등	SS	천칭형

배관 및 배선		
번호	배선	배관
(A)	HFIX 2.5Q/3C - 접지선 포함	(16C)
(B)	CV 6SQ/3C - 접지선 포함	(28C)
(C)	CV 4SQ/3C - 접지선 포함	(28C)
(D)	FTP (CAT.5e) CABLE 4P	(16C)
(E)	UTP (CAT.5e) CABLE 4P	(16C)
(F)	UTP (CAT.5e) CABLE 4P X2	(16C)
(G)	UTP (CAT.5e) CABLE 4P X3	(22C)
□ 는 AC 220V IN		
/// 는 HFIX 2.5Q/3C (16C) 임.		

지하 3층 주차관제설비 평면도

SCALE:1/150

녹색 에너지 설계 약정업체
종합 전기 설계업체 서울E-1-002호
종합 전기 관리업체 서울S-1-006호
연지니아명물동주세(정보통신) 10-104호
주식회사 전기설계. 협인

REVISION DESCRIPTION DATE

ORDER ORGAN

INVESTMENT

PROJECT OFFICE

ATEC(주)에이텍종합건축사사무소

ARCHITECTS & ASSOCIATES

DRAWING TITLE

지하 3층 주차관제설비 평면도

SCALE

A1 : 1 / 150

A3 : 1 / 300

APPROVED

ARCHITECT

DATE

2014. 03

CHECKED

DATE

2014. 03

CONSULTANT

DRAWING NO.

T-303