


옥탑층
옥상층
15층
14층
13층
12층
11층
10층
9층
8층
7층
6층
5층
4층
3층
2층
1층
지하1층
지하2층
지하3층
지하4층

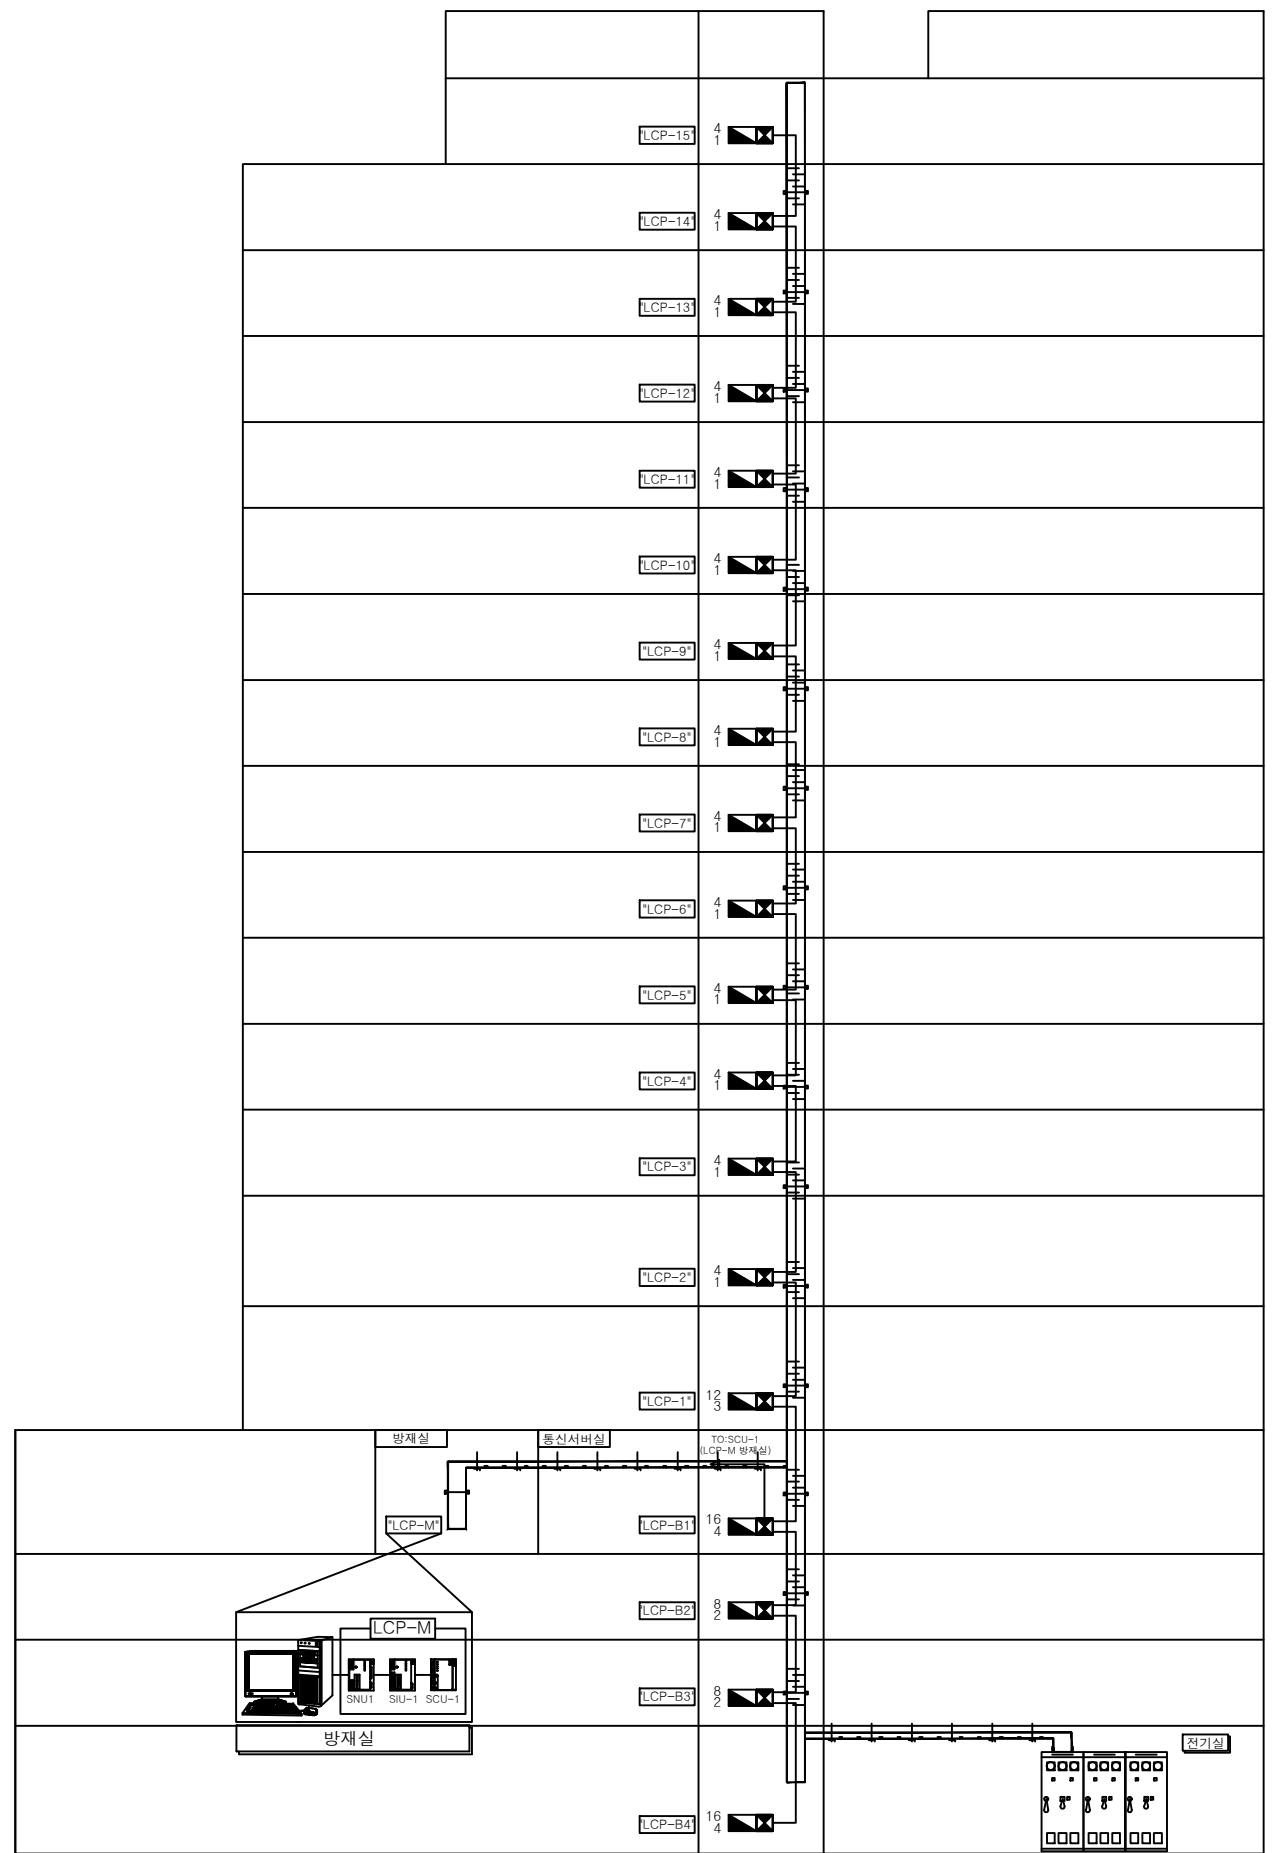

LEGEND			
DESCRIPTION	분전반	LCP PANEL	
SYMBOL			
주 기 사 항			
n — 20A RELAY 수량 n — 20A CTU 수량			
CONDUIT & CABLE SCHEDULE			
FROM	TO	WIRE	REMARK
LCP	중앙제어반	F-CVWS 1.5" -2C (22C)	전기공사분
LCP	LCP	F-CVWS 1.5" -2C (22C)	전기공사분
LCP	L	HIV 2.5" x 2 + n (n: 회로수)	전기공사분
LCP	PS	F-CVWS 1.5" -2C (22C)	전기공사분

조명제어 계통도
SCALE : NONE

녹색 에너지 설계 역량업체

종합 전기 설계업체 서울E-1-0023
종합 전기 감리업체 서울S-1-0063
원지니어링활동주체(정보통산제10-104호)
주식회사 전기설계·협인

PROJECT TITLE

성수동1가
지식산업센터
신축공사

NOTES

REVISION

ORDER ORGAN

INVESTMENT

PROJECT OFFICE

ATEC

DRAWING TITLE

조명제어 계통도

SCALE

A1 : 1 / 150
A3 : 1 / 300

APPROVED

ARCHITECT

DRAWN

강 봉 구

CHECKED

DATE

2014. 03

CONSULTANT

DRAWING NO.

E-313

PROJECT TITLE

NOTES

CENTRAL CONTROL

LIGHTING CONTROL SYSTEM

조명제어 장비 및 관제점 일람표

녹색 에너지 설계 악정업체 
 종합 전기 설계업체 서울E-1-002호
 종합 전기 감리업체 서울S-1-006호
 엔지니어링활동주체(정보통신) 제10-104호
 주식회사 전기설계. 

REVISION	DESCRIPTION	DATE
----------	-------------	------

ORDER ORGAN

ORDER ORGAN

TT VENTURE
INVESTMENT

티티벤처인베스트먼트

대표전화(02)579-8361
팩시밀리(02)579-8364

PROJECT OFFICE
A TEC (주)에이텍종합건축사사무소
ARCHITECTS &
ASSOCIATES
대표전화(02)3462-6366
팩시밀리(02)3462-6320

조명제어 장비 일람표
조명제어 관제점 일람표

SCALE	APPROVED
A1 : 1 / 150	ARCHITECT

RAWN	DATE
강 봉 구	2014. 03


HECKED	DATE
	2014. 03

CONSULTANT

DRAWING NO. E-314

조명제어 BLOCK DIAGRAM


SYSTEM INTERFACE UNIT

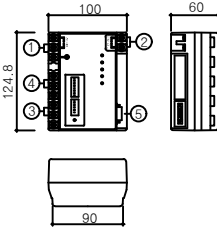

* SNU와 SCU간의 제어 명령을 변환, 상호전달

- ① 전원단자(AC24V)
- ② E/F2-BUS 신호단자
- ③ NETWORK SIGNAL OUTPUT 단자
- ④ NETWORK SIGNAL INPUT 단자
- ⑤ SETTING UNIT 연결단자


■ 20A HID RELAY

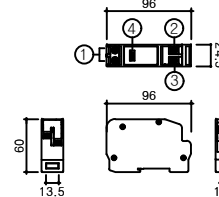

- * CTU로 부터 데이터를 받아 전등회로를 ON/OFF 시켜주는 LATCH TYPE의 접점 RELAY
- * 120,000회 동작에 대한 국내 공인시험기관 시험성적서 취득 제품


- ① 전등 부하 단자
- ② 24V TR에 연결
- ③ 20A CTU에 연결
- ④ 수동 ON/OFF 레바

■ TRANSFORMER

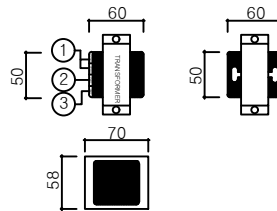

- * 20A HID RELAY에 AC24V 전원 공급
- * 정격 용량(25VA)

- ① 1차 전원(220V AC)
- ② 20A CTU에 연결(24V AC)
- ③ 20A RELAY에 연결(24V AC)

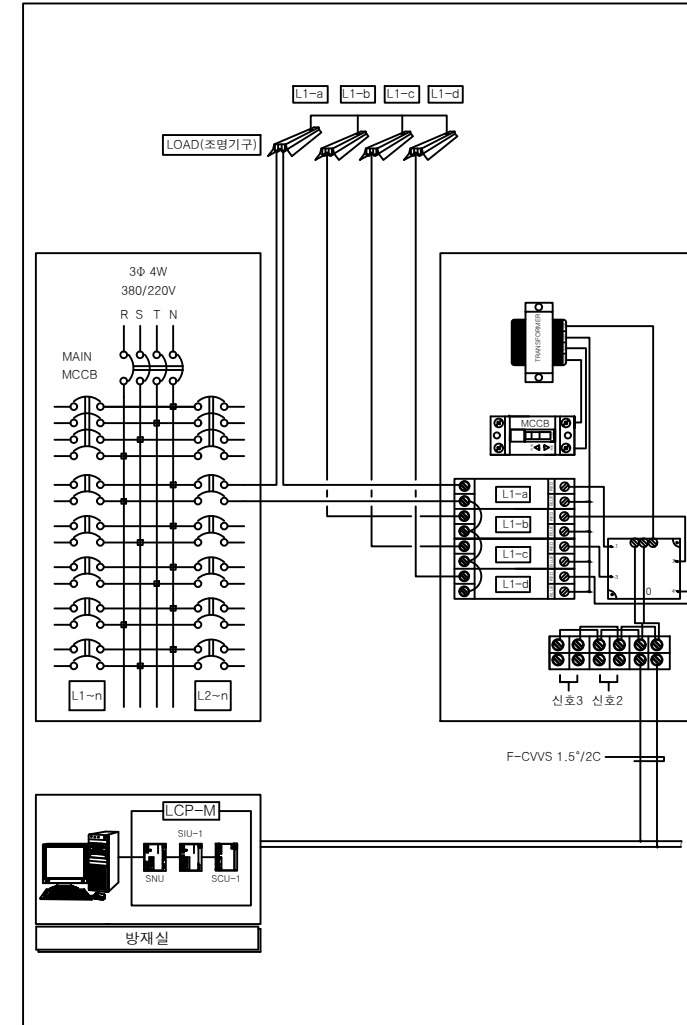

조명제어 공사 SCOPE

NO	공 사 구 분	전기공사	조명제어공사	전력제어공사
1	조명제어 패널간 신호선 배관,배선	○	—	—
2	RELAY와 BREAKER/부하 간의 배선 및 결선	○	—	—
3	속판 RELAY 및 조절기 조립	—	○	—
4	조명기기 조립후 속판 취부	○	—	—
5	조명제어 기기 셋팅	—	○	—
6	조명제어 기기 신호선 결선	—	○	—
7	조명제어 시운전	—	○	—
8	조명제어반 및 중앙제어반 취부	○	—	—
9	조명제어 패널 전원공사	○	—	—
10	조명용 PC공급	—	○	—

SCALE : NONE