

성수동1가 지식산업센터 신축공사

기계 / 기계소방

도면 목록표

도 면 번 호	도 면 명	측 척	비 고
M-001	도면목록표	NONE	
M-002	법례표	NONE	
M-003	장비일람표-1	NONE	
M-004	장비일람표-2	NONE	
M-005	위생기구일람표	NONE	
M-006	기계실장비배치도	1/80	
M-007	기계실확대배관평면도	1/80	
M-101	환기덕트계통도	NONE	
M-102	지하4층환기덕트평면도	1/150	
M-103	지하3층환기덕트평면도	1/150	
M-104	지하2층환기덕트평면도	1/150	
M-105	지하1층환기덕트평면도	1/150	
M-106	지상1층환기덕트평면도	1/150	
M-107	지상2층환기덕트평면도	1/150	
M-108	지상3층환기덕트평면도	1/150	
M-109	지상4층환기덕트평면도	1/150	
M-110	지상5~7층환기덕트평면도	1/150	
M-111	지상8~10층환기덕트평면도	1/150	
M-112	지상11~12층환기덕트평면도	1/150	
M-113	지상13~14층환기덕트평면도	1/150	
M-114	지상15층환기덕트평면도	1/150	
M-115	지붕층환기덕트평면도	1/150	
M-201	위생배관계통도	NONE	
M-202	지하4층위생배관평면도	1/150	
M-203	지하3층위생배관평면도	1/150	
M-204	지하2층위생배관평면도	1/150	
M-205	지하1층위생배관평면도	1/150	
M-206	지상1층위생배관평면도	1/150	
M-207	지상2층위생배관평면도	1/150	
M-208	지상3층위생배관평면도	1/150	
M-209	지상4층위생배관평면도	1/150	
M-210	지상5~7층위생배관평면도	1/150	
M-211	지상8~10층위생배관평면도	1/150	
M-212	지상11~12층위생배관평면도	1/150	
M-213	지상13~14층위생배관평면도	1/150	
M-214	지상15층위생배관평면도	1/150	
M-215	옥탑층위생배관평면도	1/150	
M-216	화장실확대위생배관평면도	1/50	
M-301	지하1층냉·난방배관평면도	1/150	
M-302	지상1층냉·난방배관평면도	1/150	
M-401	지하1층가스배관평면도	1/150	
M-402	지상1층가스배관평면도	1/150	
M-403	지상2층가스배관평면도	1/150	
M-404	지상3층가스배관평면도	1/150	
M-405	지상4층가스배관평면도	1/150	

[illegible]

PROJECT TITLE

성수동1가
지식산업센터
신축공사

NOTES

REVISION	DESCRIPTION	DATE

ORDER ORGAN

T T 티티벤처인베스트먼트
INVESTMENT

대표전화(02)579-8361
팩시밀리(02)579-8364

PROJECT OFFICE

A T E C (주)에이텍종합건축사사무소
ARCHITECTS & ASSOCIATES

대표전화(02)3462-6361
팩시밀리(02)3462-6321

DRAWING TITLE

도면 목록표

SCALE	APPROVED
A1 : 1 / NONE A3 : 1 / NONE	ARCHITECT 김 상 길
DRAWN 하 진 태	DATE 2014. 03

CHECKED	DATE 2014. 03

CONSULTANT	
------------	--

DRAWING NO. M - 001

범례표

[illegible]

PROJECT TITLE

성수동1가
지식산업센터
신축공사

NOTES

REVISION	DESCRIPTION	DATE

ORDER ORGAN
T T 티티벤처인베스트먼트
 INVESTMENT VENTURE
 대표전화 (02) 579-8361
 팩시밀리 (02) 579-8364

PROJECT OFFICE
ATEC(주)에이텍종합건축사사무소
ARCHITECTS & ASSOCIATES
대표전화(02)3462-6362
팩시밀리(02)3462-6322

DRAWING TITLE

범례표

SCALE	APPROVED
A1 : 1 / NONE A3 : 1 / NONE	ARCHITECT 김 상 길
DRAWN 하 진 태	DATE 2014. 03

CHECKED	DATE 2014. 03

CONSULTANT

DRAWING NO. M - 002

장비 일람표 - 1

탱크

[illegible]

폼 프

[illegible]

* 펌프는 고효율 에너지 기자재 인증 전동기 사용, KS규격에서 정해진 기준 효율의 1.12배 적용.

송 풍 기

[illegible]

* 전동기는 고효율에너지기자재로 인증받은 제품을 사용 * KS 인증제품 또는 KS규격에서 정해진 효율의 1.12배이상의 제품 채택

PROJECT TITLE

성수동1가
지식산업센터
신축공사

■NOTES

REVISION	DESCRIPTION	DATE

ORDER ORGAN

TT **티티벤처인베스트먼트**

INVESTMENT VENTURE

대표전화 (02) 579-8361
팩시밀리 (02) 579-8364

PROJECT OFFICE
ATEC (주)에이텍종합건축사사무소
ARCHITECTS &
ASSOCIATES
대표전화 (02) 3462-6366
팩시밀리 (02) 3462-8322

DRAWING TITLE

장비 일람표 - 1

SCALE	APPROVED
A1 : NONE A3 : NONE	ARCHITECT 김 상 길
DRAWN 하 진 태	DATE 2014. 03

CHECKED	DATE 2014. 03

CONDUCTIVITY

DRAWING NO. **M-003**

장 비 일 랑 표 - 2

■ 전 기 방 열 기								
장 비 번 호	수 량	용 도	형 식	설치위치	난방능력	동 력	전 원	비 고
					kcal/h	kW	Ph - V - Hz	
ER - 01	35	화장실 동파 방지용	벽걸이형	각층 화장실	1,032	1.2	1-220-60	표준 부속품 일체포함

■ 저 장 식 온 수 기								
장 비 번 호	수 량	용 도	형 식	설치위치	용 량	전 원	전 원	비 고
					(LIT)	kW	Ph - V - Hz	
ET - 01	17	화장실 장애인,2층여자화장실 세면기 급탕용	벽걸이형	각층 장애인용 화장실상부,2층여자화장실세면기 하부	15	1.5	1-220-60	표준 부속품 일체포함 (방수처리제품)
ET - 02	33	화장실 세면기 및 샤워기 급탕용	벽걸이형	각층 화장실 세면기 상부	30	2.5	1-220-60	표준 부속품 일체포함 (방수처리제품)

장비번호	수량(대)	형식	냉방용량		난방용량		냉매	배관			외형치수 (mm) (W x H x D)			중량 (kg)			소비전력(kW)			차단기(A)	통선선(mm²)	전원선(mm²)		전원(φ, #, V, Hz)	비고
			(kW)	(kcal/h)	(kW)	(kcal/h)		액관 (mm)	가스관 (mm)	드레인	외경치수 (mm)		실외기	중량 (kg)		실외기	냉방	난방	조건			20m 이하	20m 이상		
											실내기	관내		실외기	관내										
040 실내기 외기 015 3	1	1 WAY 카세트	4.00	3,440	-	-	R410A	6.35	12.70	VP20	970x135x410	-	880x638x310	9.90	-	50.00	1.4	-	-	20.0	VCTF 0.75~1.5	2.5	4.0	1,2,220,60(접지선 별도)	기타 표준 부속품 일체구비
052 실내기 외기 018 2	1	1 WAY 카세트	5.20	4,470	6.00	5,160	R410A	6.35	12.70	VP25	1,200x135x450	-	880x638x310	14.00	-	47.00	1.8	2.0	2.6 (-10℃)	20.0	VCTF 0.75~1.5	2.5	4.0	1,2,220,60(접지선 별도)	기타 표준 부속품 일체구비
100 실내기 외기 100 1	1	4 WAY 카세트	10.00	8,600	12.00	10,320	R410A	9.52	15.88	VP25	840x248x440	-	940x998x330	17.00	-	81.00	3.0	3.5	4.9 (-10℃)	15.0	VCTF 0.75~1.5	2.5	-	3,4,380,60(접지선 별도)	기타 표준 부속품 일체구비
총계	3																								

PROJECT TITLE

성수동1가
지식산업센터
신축공사

■NOTES

REVISION	DESCRIPTION	DATE

ORDER ORGAN
티티벤처인베스트먼트
INVESTMENT
대표전화(02)579-8361
팩시밀리(02)579-8364

PROJECT OFFICE
ATEC(주)에이텍종합건축사사무소
ARCHITECTS & ASSOCIATES
대표전화(02)3462-6361
팩시밀리(02)3462-6362

장 비 일 랑 표 - 2	
SCALE A1 : NONE A3 : NONE	APPROVED ARCHITECT 김 상 길
DRAWN 하 진 태	DATE 2014. 03
CHECKED	DATE 2014. 03
CONSULTANT	
DRAWING NO. M-004	

위생기구일람표

위생기구 일람표

명 칭	규 격	수 량																합 계	접 속 구 경			비 고
		지하 1 층	1 층	2 층	3 층	4 층	5 층	6 층	7 층	8 층	9 층	10 층	11 층	12 층	13 층	14 층	15 층		냉수	온수	오배수	
양변기(F.V TYPE)	-	6	6	12	6	6	6	6	6	6	6	6	6	6	6	6	6	102	25	-	100	절수형 F.V, 기타 표준 부속품 일체 구비
양변기(L.T TYPE)	-	-	-	2	-	-	-	-	-	-	-	-	-	-	-	-	-	2	25	-	100	절수형 LOW TANK형, 기타 표준 부속품 일체 구비
양변기(장애인용)	KS규격동등이상품	1	1	1	1	1	1	1	1	1	1	1	1	1	1	1	1	16	25	-	100	절수형 F.V, 장애인 안전가대 포함, 기타 표준 부속품 일체 구비
소변기	KS규격동등이상품	2	2	4	2	2	2	2	2	2	2	2	2	2	2	2	2	34	15	-	50	전자 감응식 (전기식), 표준부속품 일체구비
소변기(장애인용)	KS규격동등이상품	1	1	1	1	1	1	1	1	1	1	1	1	1	1	1	1	16	15	-	50	전자 감응식 (전기식), 장애인 안전가대 포함, 표준부속품 일체구비
원형 세면기	KS규격동등이상품	4	4	6	4	4	4	4	4	4	4	4	4	4	4	4	4	66	15	15	40	절수형 수전 사용
각형 세면기	KS규격동등이상품	-	-	2	-	-	-	-	-	-	-	-	-	-	-	-	-	2	15	15	40	절수형 수전 사용
코너형 세면기(장애인용)	KS규격동등이상품	1	1	1	1	1	1	1	1	1	1	1	1	1	1	1	1	16	15	15	40	절수형 수전 사용, 장애인 안전가대 포함
청소싱크	KS규격동등이상품	1	1	1	1	1	1	1	1	1	1	1	1	1	1	1	1	16	20	-	75	절수형 수전 사용
샤워수전	KS규격동등이상품	-	-	2	-	-	-	-	-	-	-	-	-	-	-	-	-	2	15	15	-	절수형 수전 사용
* NOTE : "수도법 제15조 및 수도법시행규칙 제6조에 따른 절수형설비 적용"																						

REVISION

DESCRIPTION

DATE

ORDER ORGAN

티티벤처인베스트먼트

INVESTMENT

대표전화(02)579-8361
팩시밀리(02)579-8364

PROJECT OFFICE

ATEC(주)에이텍종합건축사사무소

ARCHITECTS & ASSOCIATES

대표전화(02)3462-6366
팩시밀리(02)3462-6362

DRAWING TITLE

위생기구일람표

SCALE

A1 : NONE
A3 : NONE

APPROVED

ARCHITECT 김 상 길

DRAWN

하진태

CHECKED

DATE 2014. 03

CONSULTANT



DRAWING NO.

M-005

PROJECT TITLE

성수동1가
지식산업센터
신축공사

NOTES

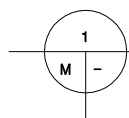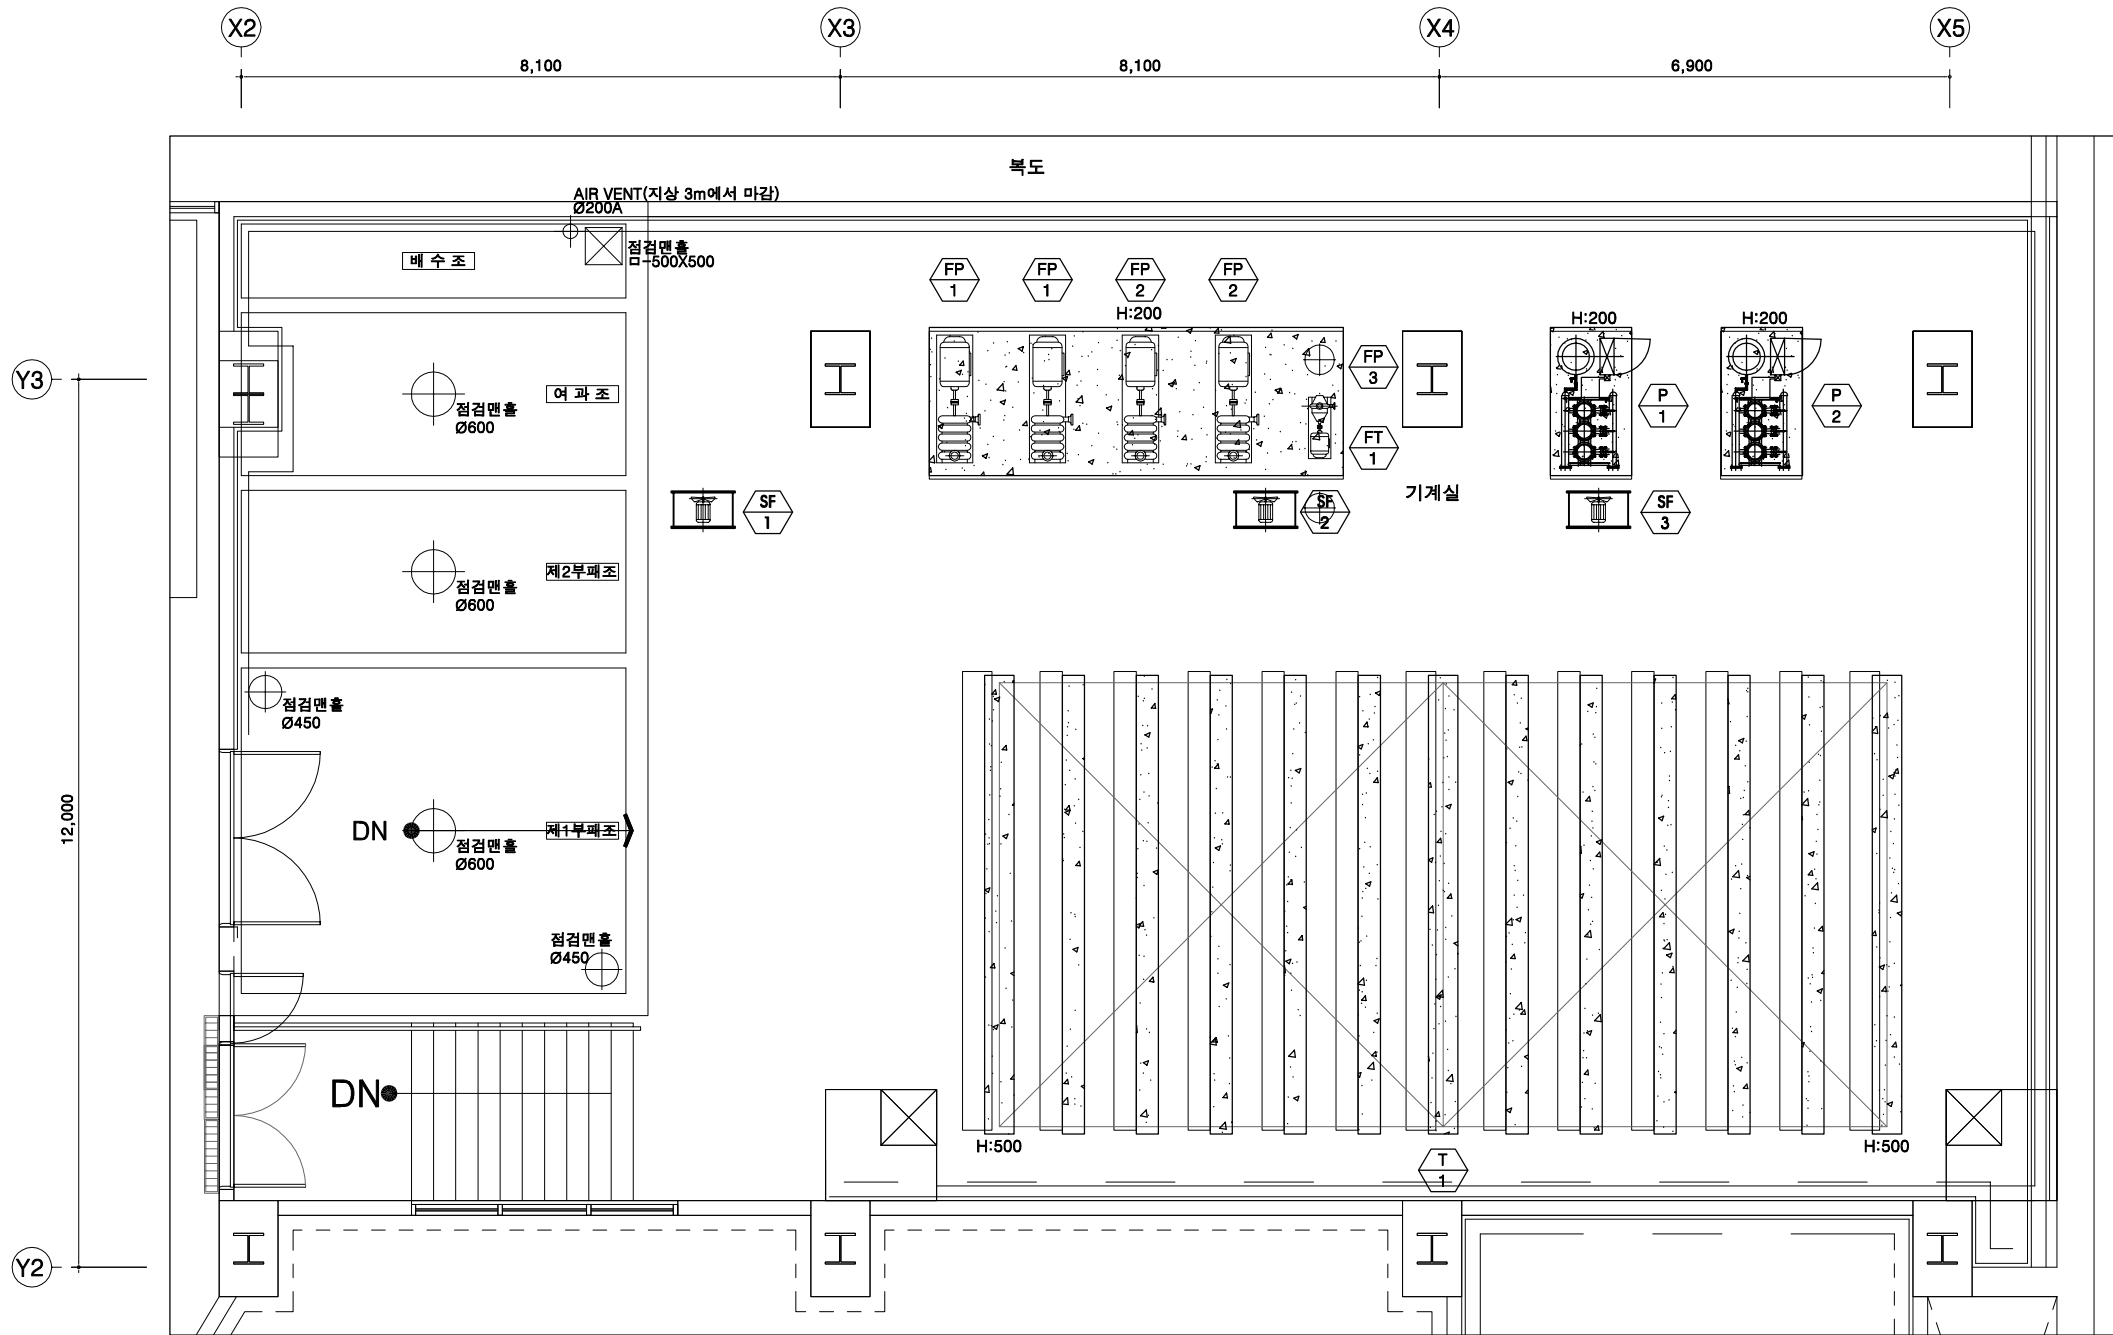

기계실 장비배치도

축척 : A1:1/50, A3:1/100

REVISION DESCRIPTION DATE

ORDER ORGAN

INVESTMENT

PROJECT OFFICE

ARCHITECTS & ASSOCIATES

DRAWING TITLE

SCALE

APPROVED

DATE

CHECKED

CONSULTANT

DRAWING NO.

M-006