


LAYOUT-A 주출입구

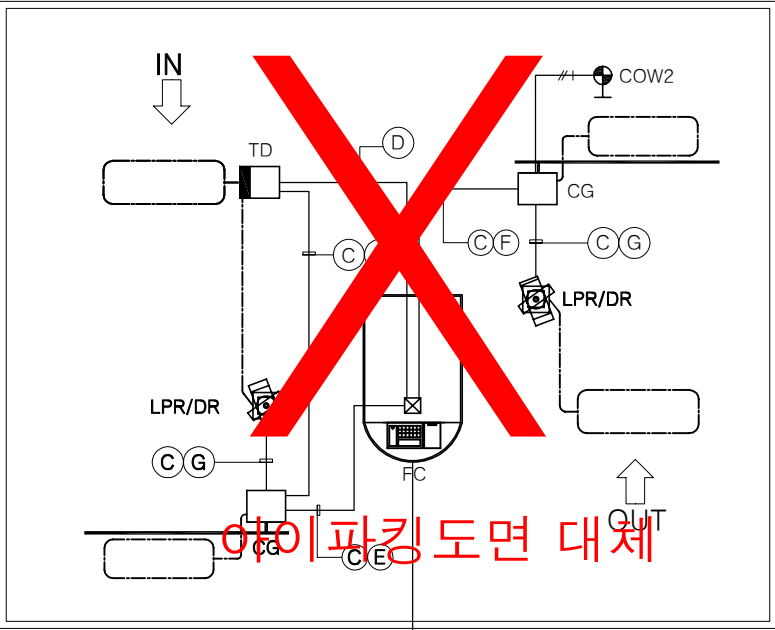

아이파킹도면 대체

\*주차안내판  
층별 EPS실 분전반 - ELB 주차안내

\*주차관재경광등  
B1F EPS실 분전반 메인연결 - ELB 주차관재

| 주기사항 |              |        |       |
|------|--------------|--------|-------|
| 심볼   | 품명           | 기호     | 비고    |
|      | 자동 차단기       | CG     | 자립형   |
|      | 주차권 발행기      | TD     | 자립형   |
|      | 차량번호 인식기/전광판 | LPR/DR | 자립형   |
|      | 유인요금계산기      | FC     | 탁상형   |
|      | 차량 검지기       | D      | 벽매입형  |
|      | LOOP COIL    | LC     | 바닥매입형 |
|      | 주차관리 컴퓨터     | HC     | 탁상형   |
|      | 장내경광등        | AS     | 천정형   |
|      | 출차주의등        | COW    | 자립형   |
|      | 단면유도등        | S      | 천칭형   |
|      | 양면유도등        | SS     | 천칭형   |

| 배관 및 배선                  |                          |       |
|--------------------------|--------------------------|-------|
| 번호                       | 배선                       | 배관    |
| (A)                      | HFIX 2.5Q/3C - 접지선 포함    | (16C) |
| (B)                      | CV 6SQ/3C - 접지선 포함       | (28C) |
| (C)                      | CV 4SQ/3C - 접지선 포함       | (28C) |
| (D)                      | FTP (CAT.5e) CABLE 4P    | (16C) |
| (E)                      | UTP (CAT.5e) CABLE 4P    | (16C) |
| (F)                      | UTP (CAT.5e) CABLE 4P X2 | (16C) |
| (G)                      | UTP (CAT.5e) CABLE 4P X3 | (22C) |
| —는 AC 220V IN            |                          |       |
| —는 HFIX 2.5Q/3C (16C) 임. |                          |       |

지상1층

지하1층

지하2층

지하3층

지하4층

주차안내판

주차안내판

주차안내판

주차안내판

아이파킹1F 주차관제

주차관재경광등

TO: B1F EPS실 LE-B1

TO: B1F EPS실 LE-B1

주차관제설비 계통도

SCALE:NONE

녹색 에너지 설계 약정업체  
종합 전기 설계업체 서울E-1-0023  
종합 전기 강리업체 서울S-1-0063  
연지니아명물동주세(정보통신) 10-104호  
주식회사 전기설계. 협인

PROJECT TITLE

성수동1가  
지식산업센터  
신축공사

NOTES

REVISION DESCRIPTION DATE

ORDER ORGAN

INVESTMENT  
터티벤처인베스트먼트  
대표전화021579-8361  
팩시밀리021579-8364

PROJECT OFFICE

ATEC(주)에이텍종합건축사사무소  
ARCHITECTS & ASSOCIATES  
대표전화0213462-6366  
팩시밀리0213462-6368

DRAWING TITLE

주차관제설비 계통도

SCALE A1 : NONE A3 : NONE


APPROVED ARCHITECT 김 상 길

DRAWN 강 봉 구 DATE 2014. 03

CHECKED DATE 2014. 03

CONSULTANT

DRAWING NO. T-301

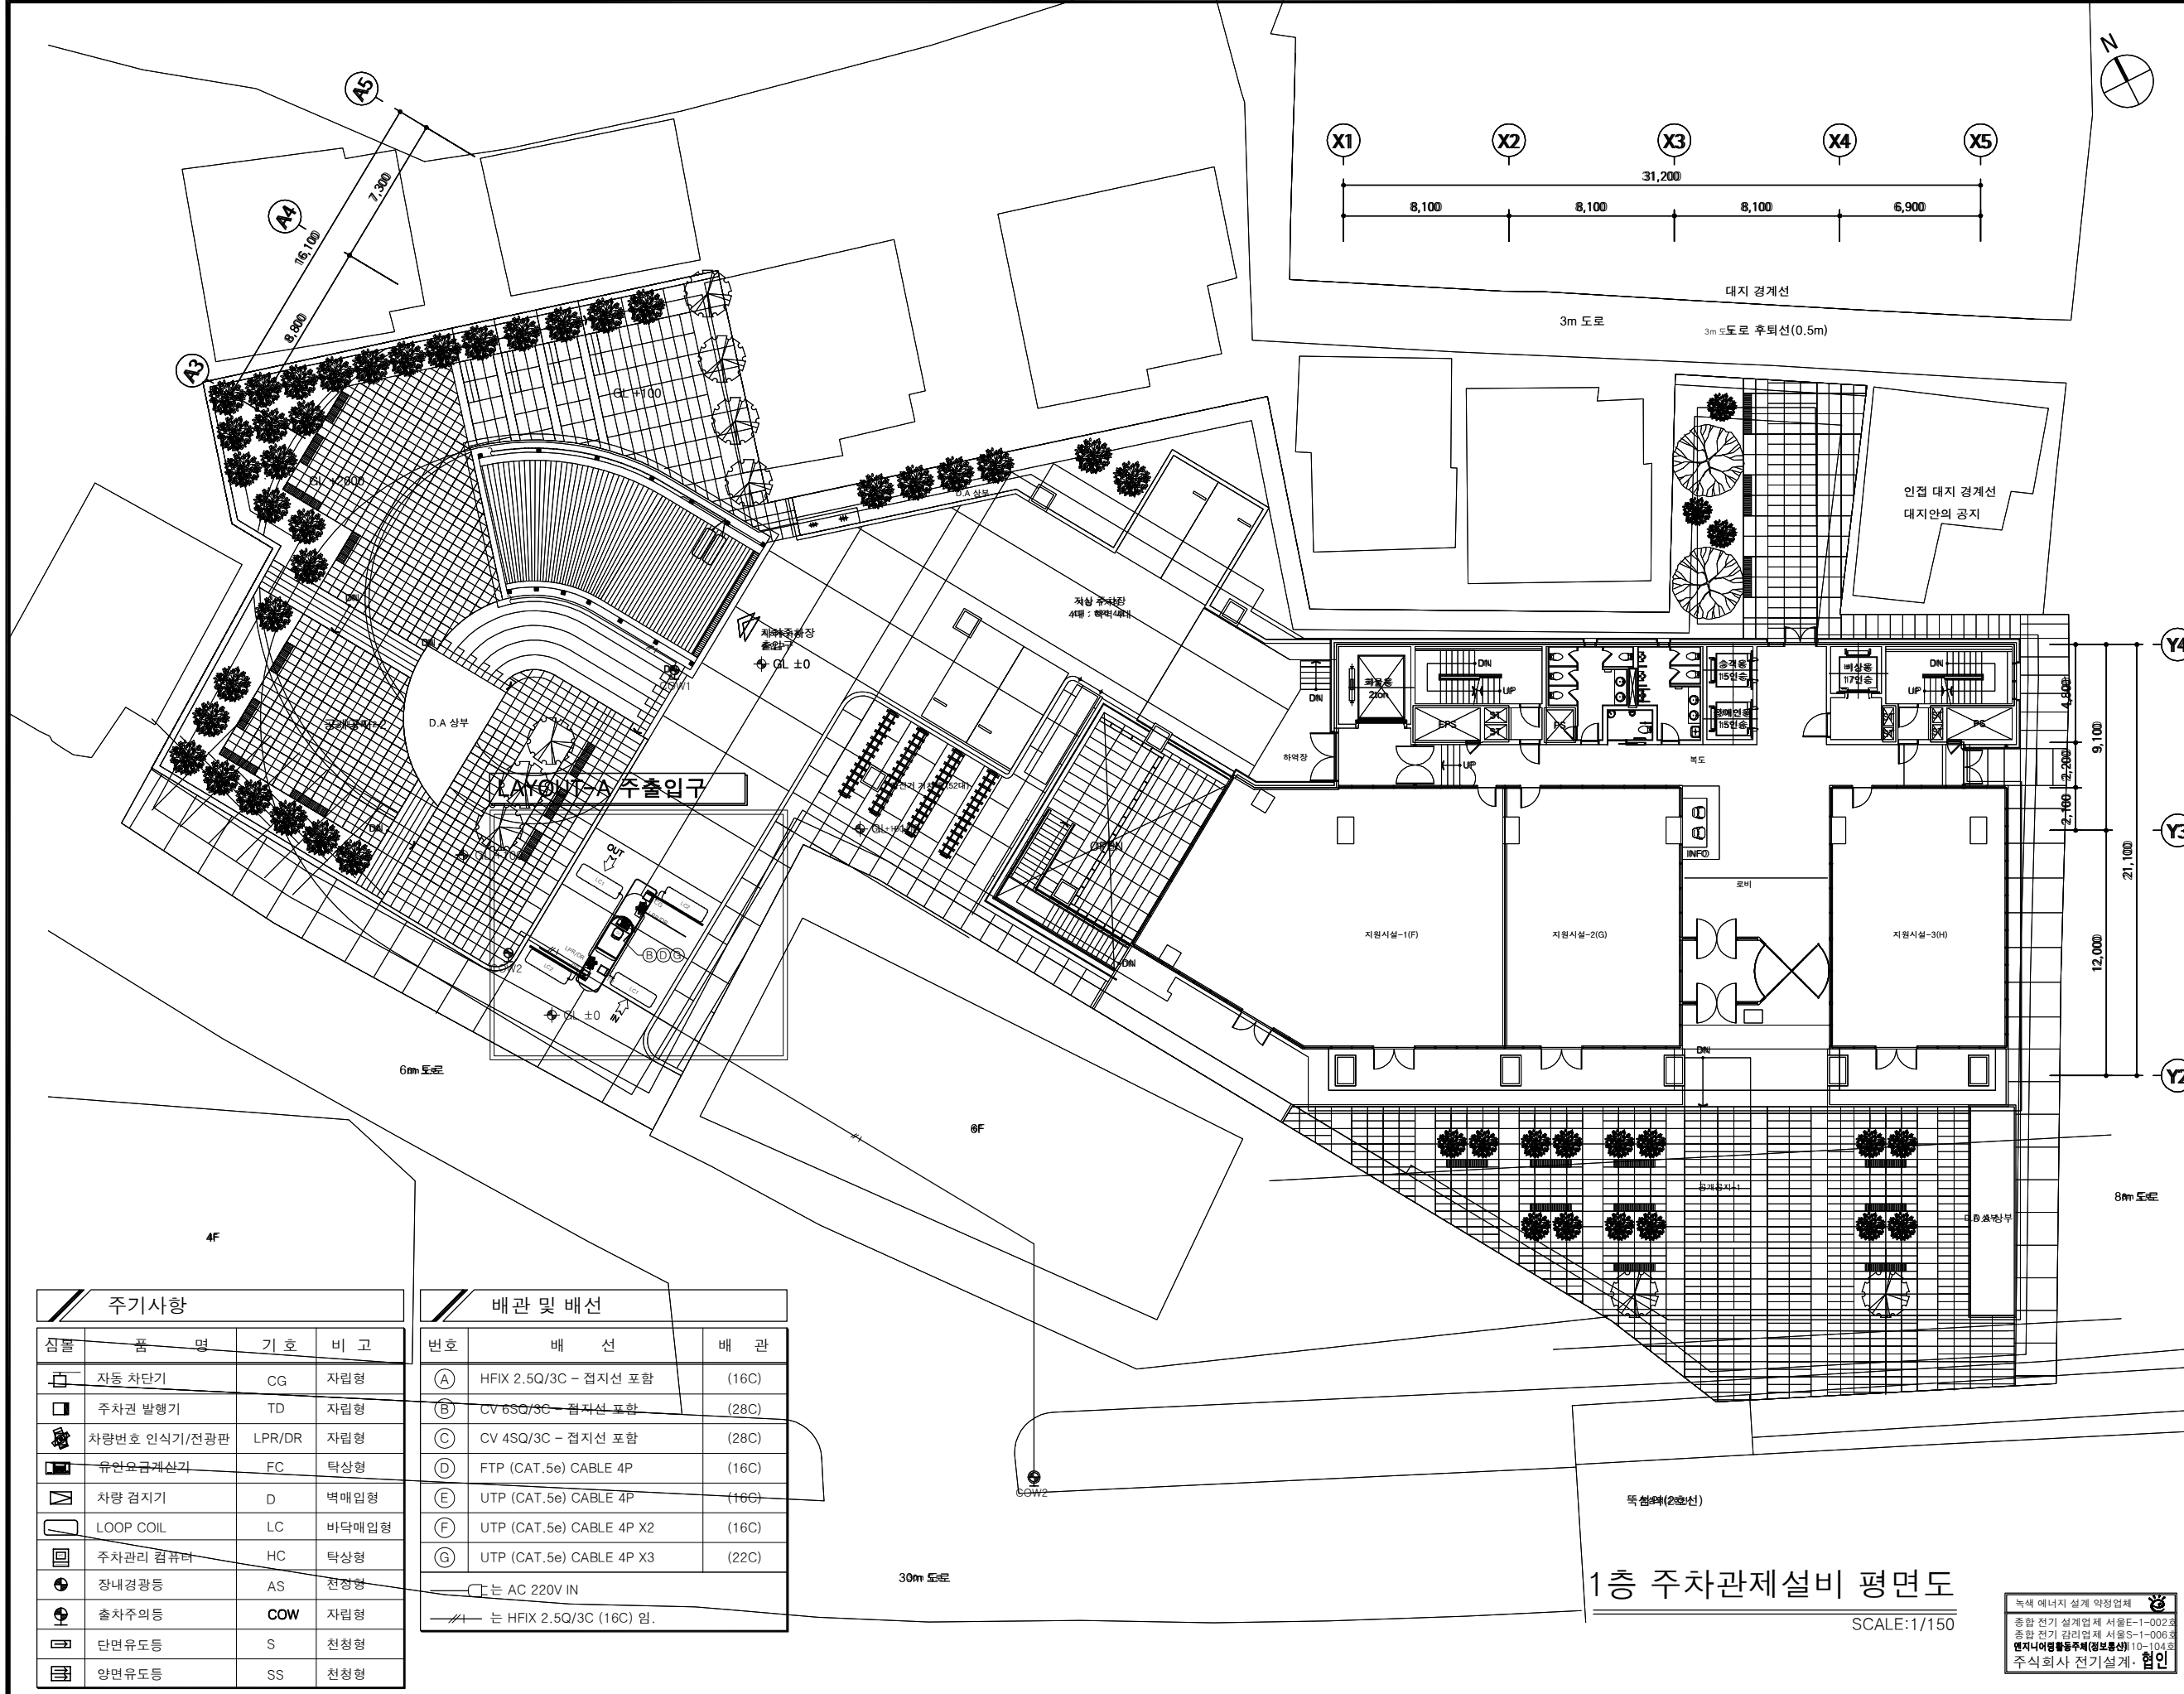

PROJECT TITLE

# 성수동1가 지식산업센터 신축공사

NOTES

| REVISION | DESCRIPTION | DATE |
|----------|-------------|------|
|          |             |      |
|          |             |      |
|          |             |      |

ORDER ORGAN  
**터티벤처인베스트먼트**  
INVESTMENT  
대표전화(02)579-8361  
팩시밀리(02)579-8364

PROJECT OFFICE  
**ATEC**(주)에이텍종합건축사사무소  
ARCHITECTS & ASSOCIATES  
대표전화(02)3462-6366  
팩시밀리(02)3462-6368

DRAWING TITLE

## 1층 주차관제설비 평면도

| SCALE                        | APPROVED        |
|------------------------------|-----------------|
| A1 : 1 / 150<br>A3 : 1 / 300 | ARCHITECT 김 상 길 |
| DRAWN                        | DATE            |
| 강 봉 구                        | 2014. 03        |
| CHECKED                      | DATE            |
|                              | 2014. 03        |
| CONSULTANT                   |                 |

DRAWING NO. T-306


| 주기사항 |              |        |       |
|------|--------------|--------|-------|
| 심볼   | 품 명          | 기 호    | 비 고   |
|      | 자동차 차단기      | CG     | 자립형   |
|      | 주차권 발행기      | TD     | 자립형   |
|      | 차량번호 인식기/전광판 | LPR/DR | 자립형   |
|      | 유안요금계산기      | FC     | 탁상형   |
|      | 차량 검지기       | D      | 벽매입형  |
|      | LOOP COIL    | LC     | 바닥매입형 |
|      | 주차관리 컴퓨터     | HC     | 탁상형   |
|      | 장내경광등        | AS     | 천장형   |
|      | 출차주의등        | COW    | 자립형   |
|      | 단면유도등        | S      | 천장형   |
|      | 양면유도등        | SS     | 천장형   |

| 배관 및 배선                 |                          |       |
|-------------------------|--------------------------|-------|
| 번호                      | 배 선                      | 배 관   |
| (A)                     | HFIX 2.5Q/3C - 접지선 포함    | (16C) |
| (B)                     | CV 6SQ/3C - 접지선 포함       | (28C) |
| (C)                     | CV 4SQ/3C - 접지선 포함       | (28C) |
| (D)                     | FTP (CAT.5e) CABLE 4P    | (16C) |
| (E)                     | UTP (CAT.5e) CABLE 4P    | (16C) |
| (F)                     | UTP (CAT.5e) CABLE 4P X2 | (16C) |
| (G)                     | UTP (CAT.5e) CABLE 4P X3 | (22C) |
| — AC 220V IN            |                          |       |
| — HFIX 2.5Q/3C (16C) 임. |                          |       |

## 1층 주차관제설비 평면도

SCALE:1/150

녹색 에너지 설계 약정업체  
종합 전기 설계업체 서울E-1-0023  
종합 전기 관리업체 서울S-1-0063  
연지니아명물동주세(정보통신) 10-104호  
주식회사 전기설계. 협인

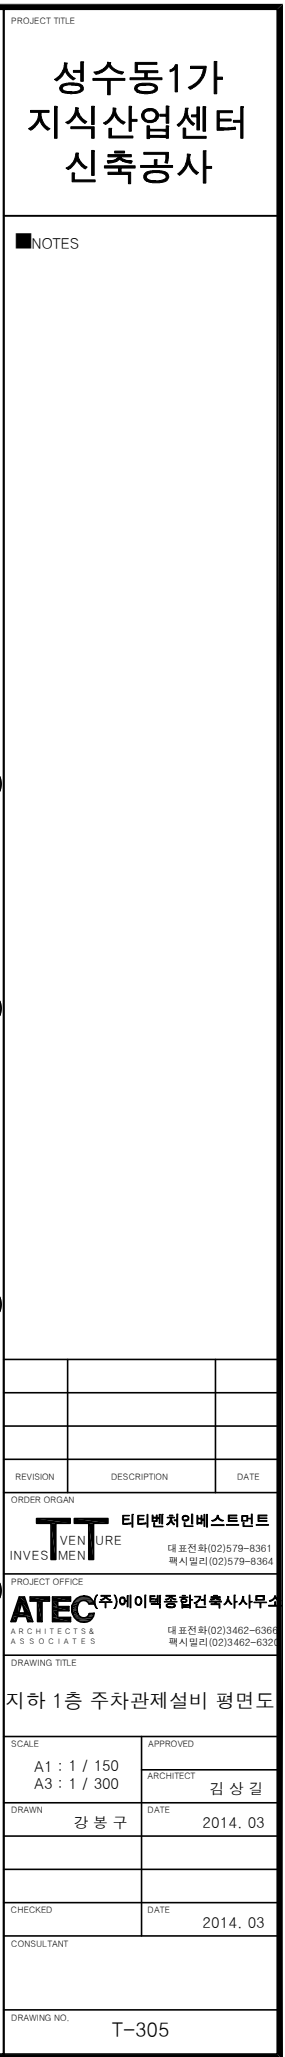

| 배관 및 배선 |                          |       |
|---------|--------------------------|-------|
| 번호      | 배 선                      | 배 관   |
| (A)     | HFIX 2.5Q/3C - 접지선 포함    | (16C) |
| (B)     | CV 6SQ/3C - 접지선 포함       | (28C) |
| (C)     | CV 4SQ/3C - 접지선 포함       | (28C) |
| (D)     | FTP (CAT.5e) CABLE 4P    | (16C) |
| (E)     | UTP (CAT.5e) CABLE 4P    | (16C) |
| (F)     | UTP (CAT.5e) CABLE 4P X2 | (16C) |
| (G)     | UTP (CAT.5e) CABLE 4P X3 | (22C) |

 는 AC 220V IN  
 는 HFIX 2.5Q/3C (16C) 임.

지하 1층 주차관제설비 평면도

SCALE:1/150


녹색 에너지 설계 약정업체 

종합 전기 설계업체 서울E-1-002호  
종합 전기 감리업체 서울S-1-006호  
엔지니어링활동주체(정보통신) 10-104호  
주식회사 전기설계. 협인

PROJECT TITLE

성수동1가  
지식산업센터  
신축공사

NOTES

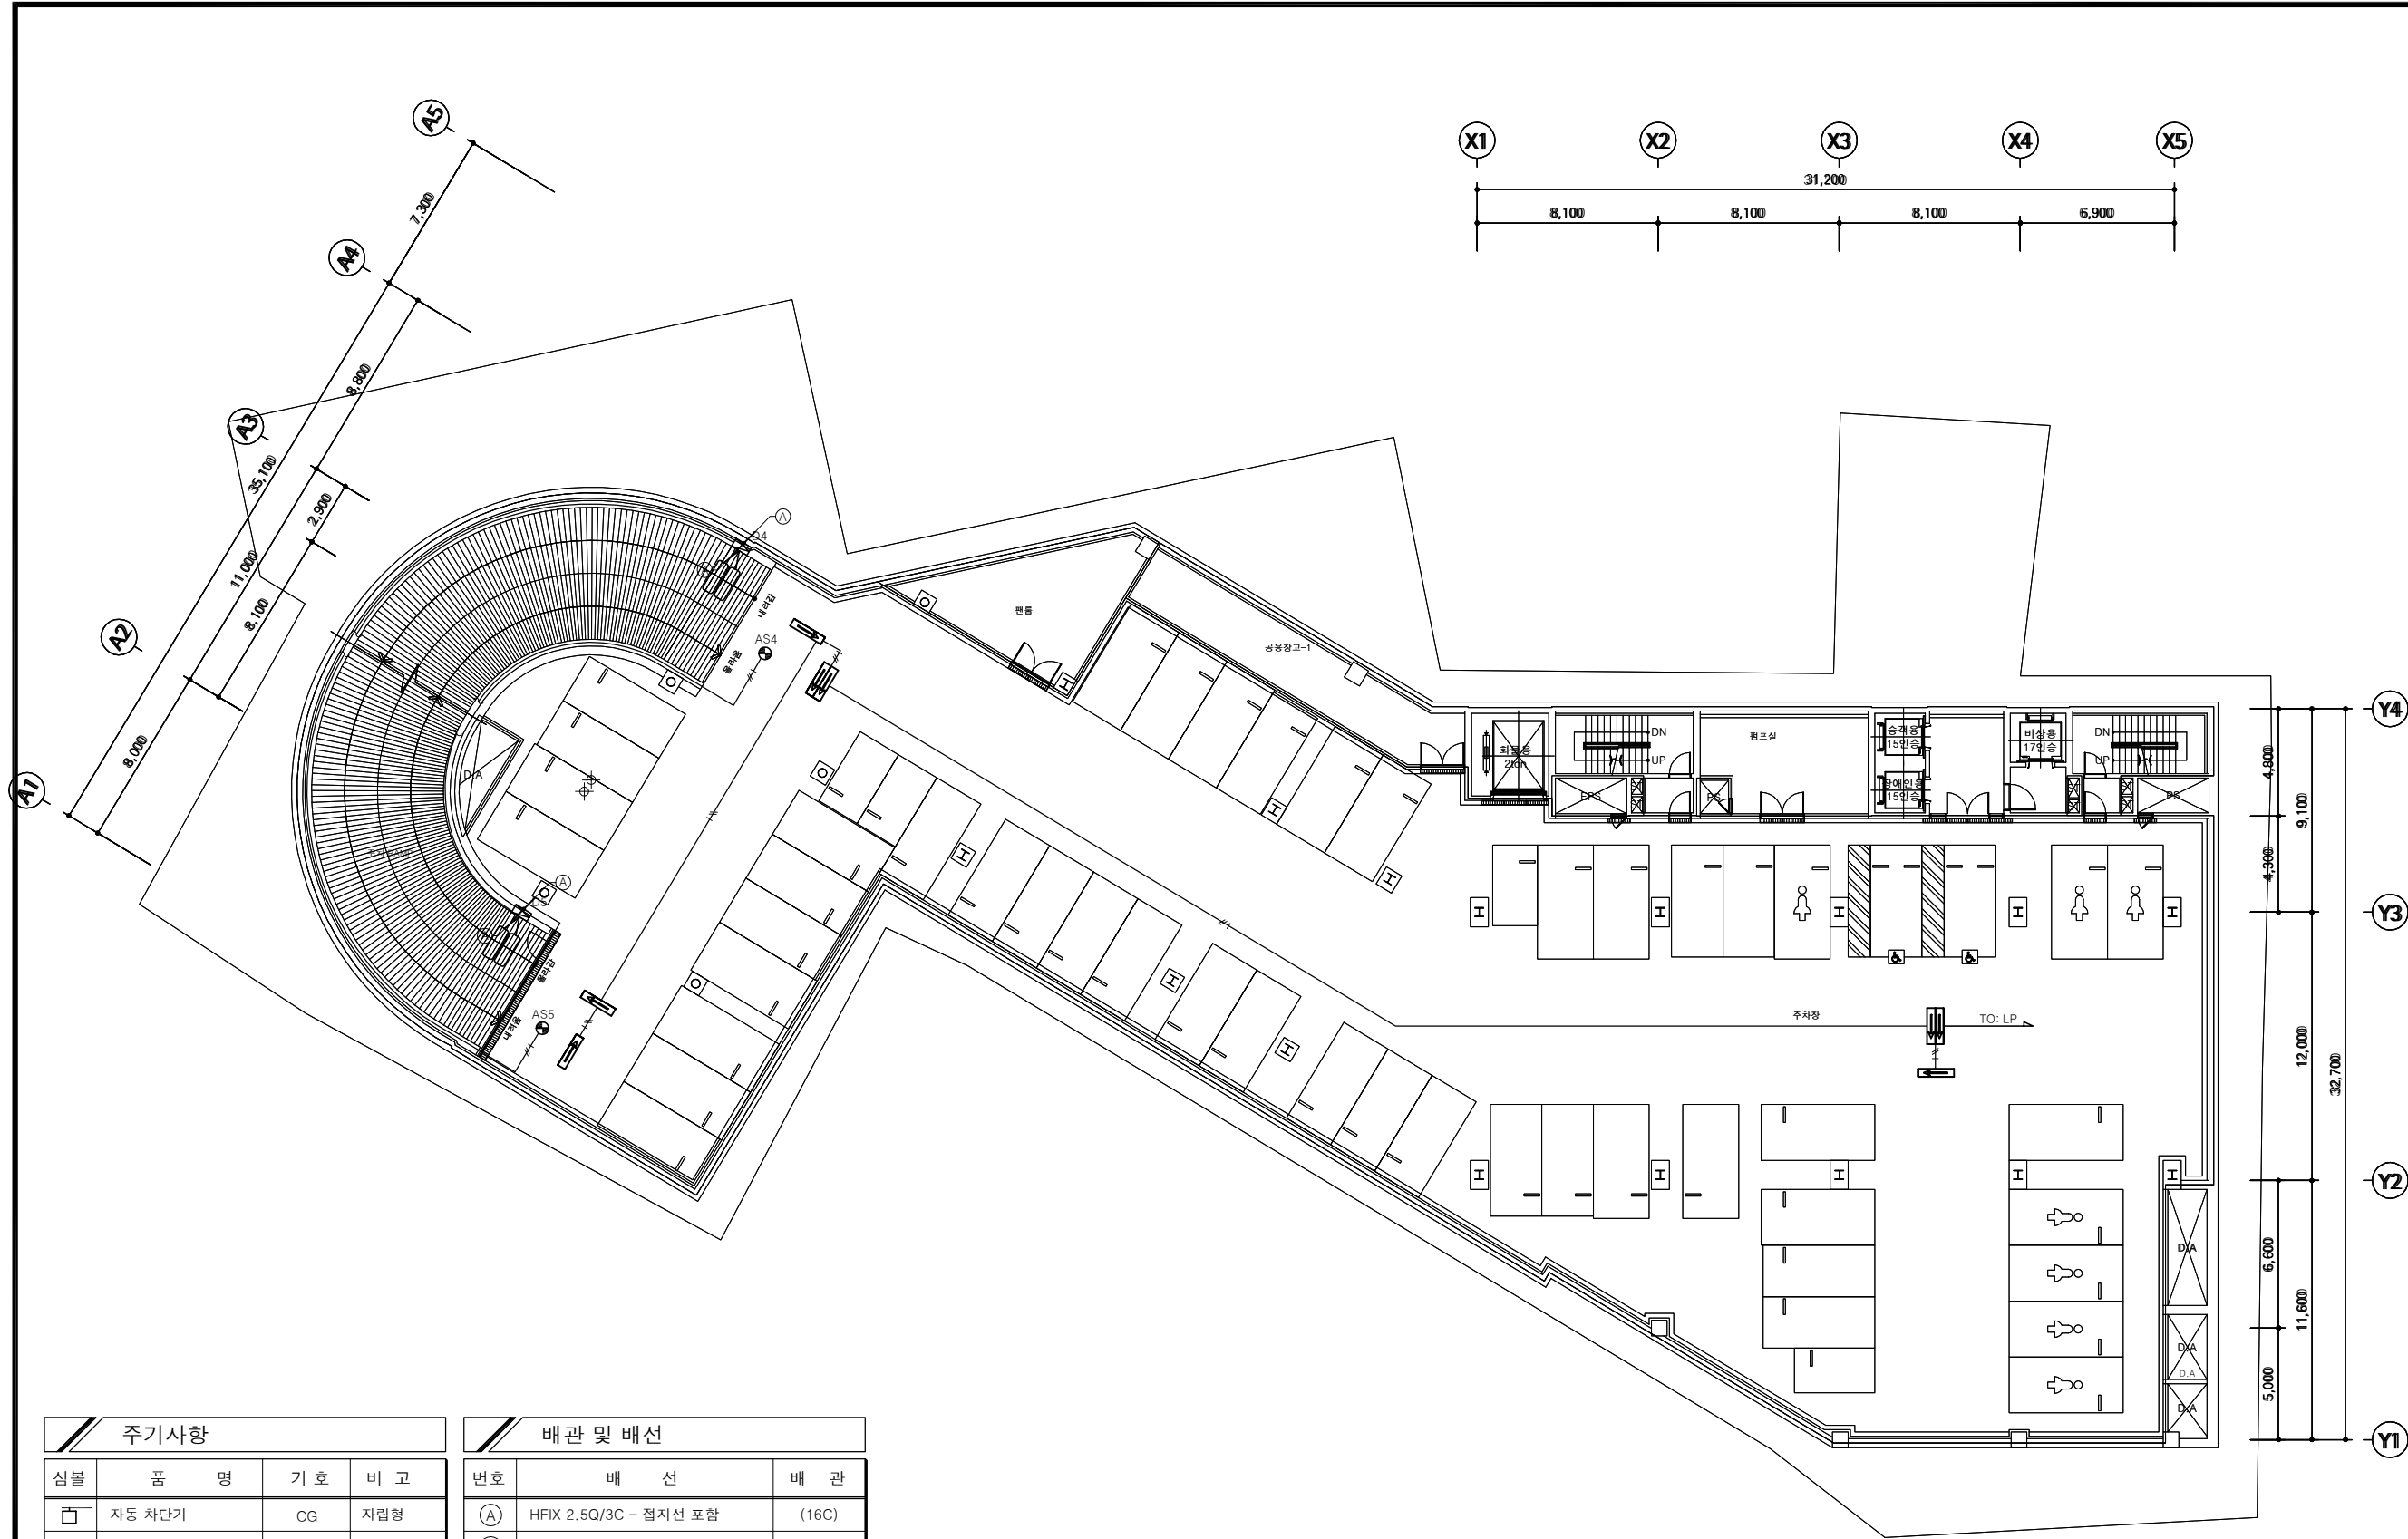

| 주기사항 |              |        |       |
|------|--------------|--------|-------|
| 심볼   | 품 명          | 기 호    | 비 고   |
|      | 자동 차단기       | CG     | 자립형   |
|      | 주차권 발행기      | TD     | 자립형   |
|      | 차량번호 인식기/전광판 | LPR/DR | 자립형   |
|      | 유연요금계산기      | FC     | 탁상형   |
|      | 차량 검지기       | D      | 벽매입형  |
|      | LOOP COIL    | LC     | 바닥매입형 |
|      | 주차관리 컴퓨터     | HC     | 탁상형   |
|      | 장내경광등        | AS     | 천정형   |
|      | 출차주의등        | COW    | 자립형   |
|      | 단면유도등        | S      | 천청형   |
|      | 양면유도등        | SS     | 천청형   |

| 배관 및 배선                      |                          |       |
|------------------------------|--------------------------|-------|
| 번호                           | 배 선                      | 배 관   |
| (A)                          | HFIX 2.5Q/3C - 접지선 포함    | (16C) |
| (B)                          | CV 6SQ/3C - 접지선 포함       | (28C) |
| (C)                          | CV 4SQ/3C - 접지선 포함       | (28C) |
| (D)                          | FTP (CAT.5e) CABLE 4P    | (16C) |
| (E)                          | UTP (CAT.5e) CABLE 4P    | (16C) |
| (F)                          | UTP (CAT.5e) CABLE 4P X2 | (16C) |
| (G)                          | UTP (CAT.5e) CABLE 4P X3 | (22C) |
| —□— 는 AC 220V IN             |                          |       |
| —//— 는 HFIX 2.5Q/3C (16C) 임. |                          |       |

지하 2층 주차관제설비 평면도  
SCALE:1/150

녹색 에너지 설계 약정업체  
종합 전기 설계업체 서울E-1-0023  
종합 전기 감리업체 서울S-1-0063  
연지니아종합건축(정보통선) 10-104호  
주식회사 전기설계. 협인

REVISION DESCRIPTION DATE

ORDER ORGAN

INVESTMENT  
티티벤처인베스트먼트  
대표전화021579-8361  
팩시밀리021579-8364

PROJECT OFFICE

ATEC(주)에이텍종합건축사사무소  
ARCHITECTS & ASSOCIATES  
대표전화0213462-6366  
팩시밀리0213462-6368

DRAWING TITLE

지하 2층 주차관제설비 평면도

SCALE

A1 : 1 / 150  
A3 : 1 / 300

APPROVED

ARCHITECT 김 상 길

DRAWN

강 봉 구

DATE

2014. 03

CHECKED

DATE

2014. 03

CONSULTANT


DRAWING NO.

T-304

PROJECT TITLE

성수동1가  
지식산업센터  
신축공사

NOTES

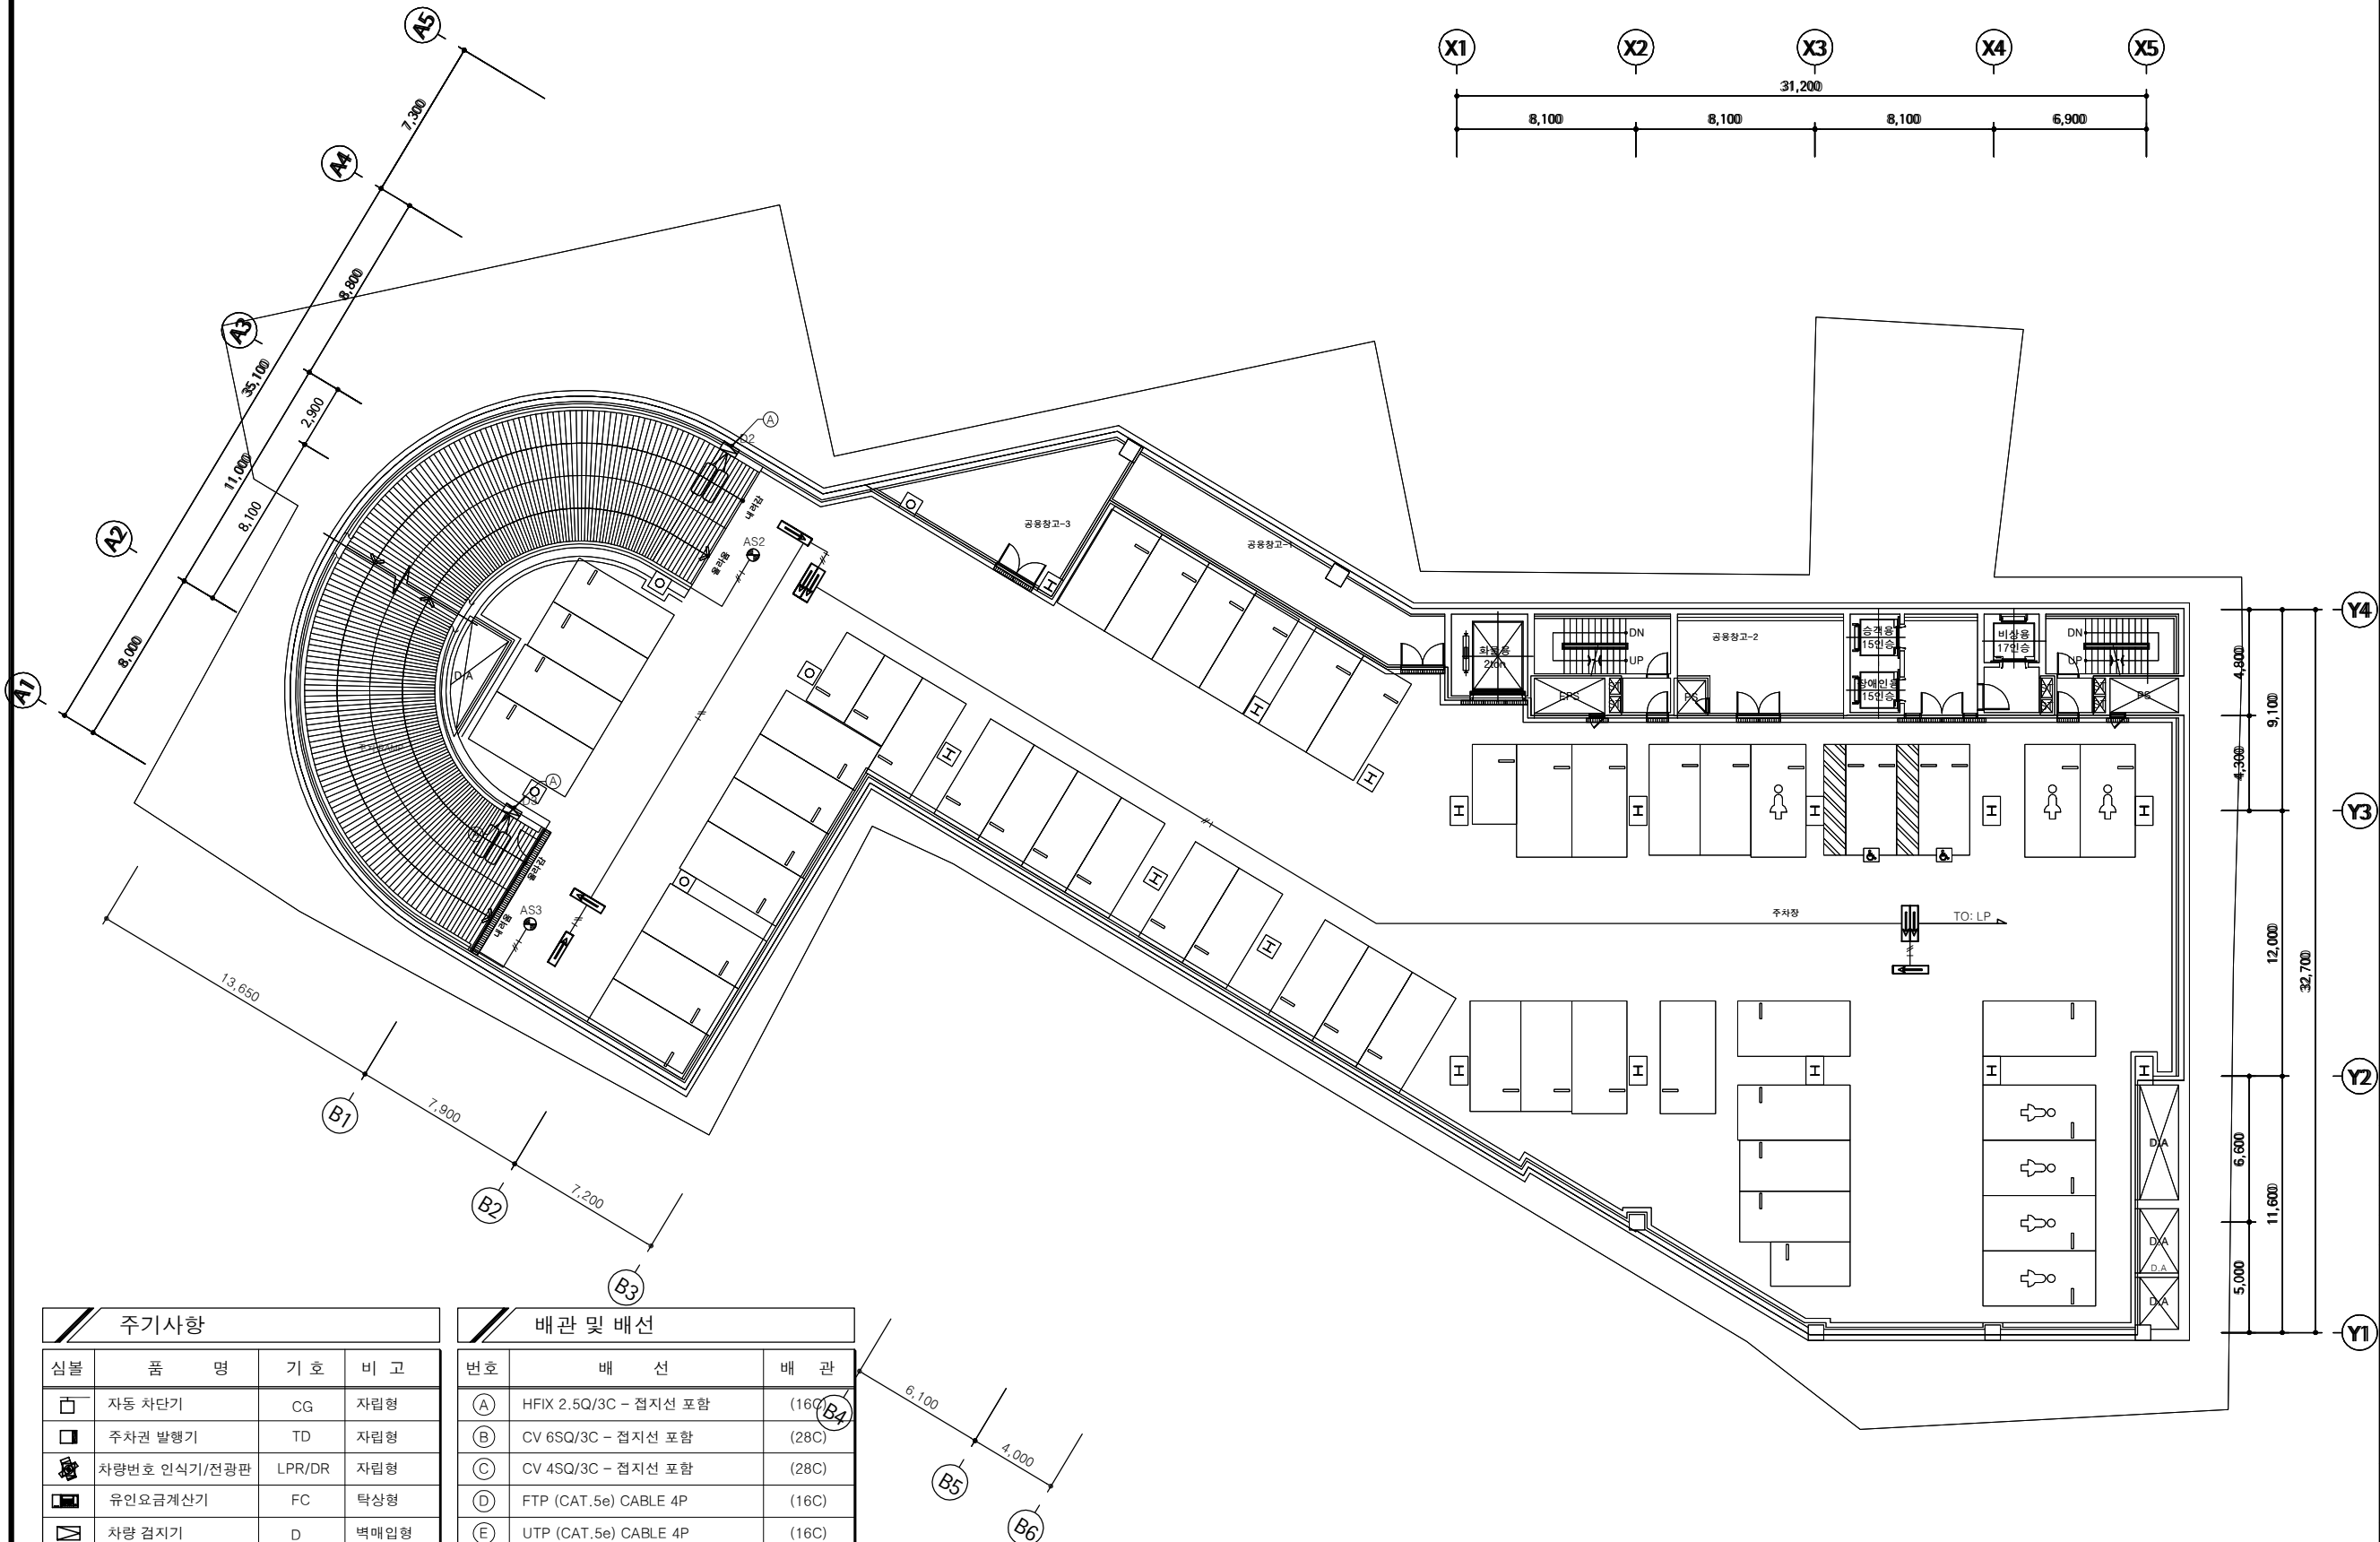

| 주기사항 |              |        |       |
|------|--------------|--------|-------|
| 심볼   | 품명           | 기호     | 비고    |
|      | 자동 차단기       | CG     | 자립형   |
|      | 주차권 발행기      | TD     | 자립형   |
|      | 차량번호 인식기/전광판 | LPR/DR | 자립형   |
|      | 유인요금계산기      | FC     | 탁상형   |
|      | 차량 검지기       | D      | 벽매입형  |
|      | LOOP COIL    | LC     | 바닥매입형 |
|      | 주차관리 컴퓨터     | HC     | 탁상형   |
|      | 장내경광등        | AS     | 천정형   |
|      | 출차주의등        | COW    | 자립형   |
|      | 단면유도등        | S      | 천칭형   |
|      | 양면유도등        | SS     | 천칭형   |

| 배관 및 배선                   |                          |       |
|---------------------------|--------------------------|-------|
| 번호                        | 배선                       | 배관    |
| (A)                       | HFIX 2.5Q/3C - 접지선 포함    | (16C) |
| (B)                       | CV 6SQ/3C - 접지선 포함       | (28C) |
| (C)                       | CV 4SQ/3C - 접지선 포함       | (28C) |
| (D)                       | FTP (CAT.5e) CABLE 4P    | (16C) |
| (E)                       | UTP (CAT.5e) CABLE 4P    | (16C) |
| (F)                       | UTP (CAT.5e) CABLE 4P X2 | (16C) |
| (G)                       | UTP (CAT.5e) CABLE 4P X3 | (22C) |
| □ 는 AC 220V IN            |                          |       |
| / 는 HFIX 2.5Q/3C (16C) 임. |                          |       |

지하 3층 주차관제설비 평면도  
SCALE:1/150

녹색 에너지 설계 약정업체  
종합 전기 설계업체 서울E-1-002호  
종합 전기 관리업체 서울S-1-006호  
연지니아명물동주세(정보통신) 10-104호  
주식회사 전기설계. 협인

REVISION DESCRIPTION DATE

ORDER ORGAN

INVESTMENT  
티티벤처인베스트먼트  
대표전화021579-8361  
팩시밀리021579-8364

PROJECT OFFICE

ATEC(주)에이텍종합건축사사무소  
ARCHITECTS & ASSOCIATES  
대표전화021462-6366  
팩시밀리021462-6368

DRAWING TITLE

지하 3층 주차관제설비 평면도

SCALE

A1 : 1 / 150  
A3 : 1 / 300

APPROVED

ARCHITECT 김상길

DRAWN 강봉구

DATE 2014. 03

CHECKED

DATE 2014. 03

CONSULTANT


DRAWING NO. T-303

PROJECT TITLE

성수동1가  
지식산업센터  
신축공사

NOTES

- 객석 유도등 전환반  
⊖ 객석 유도등

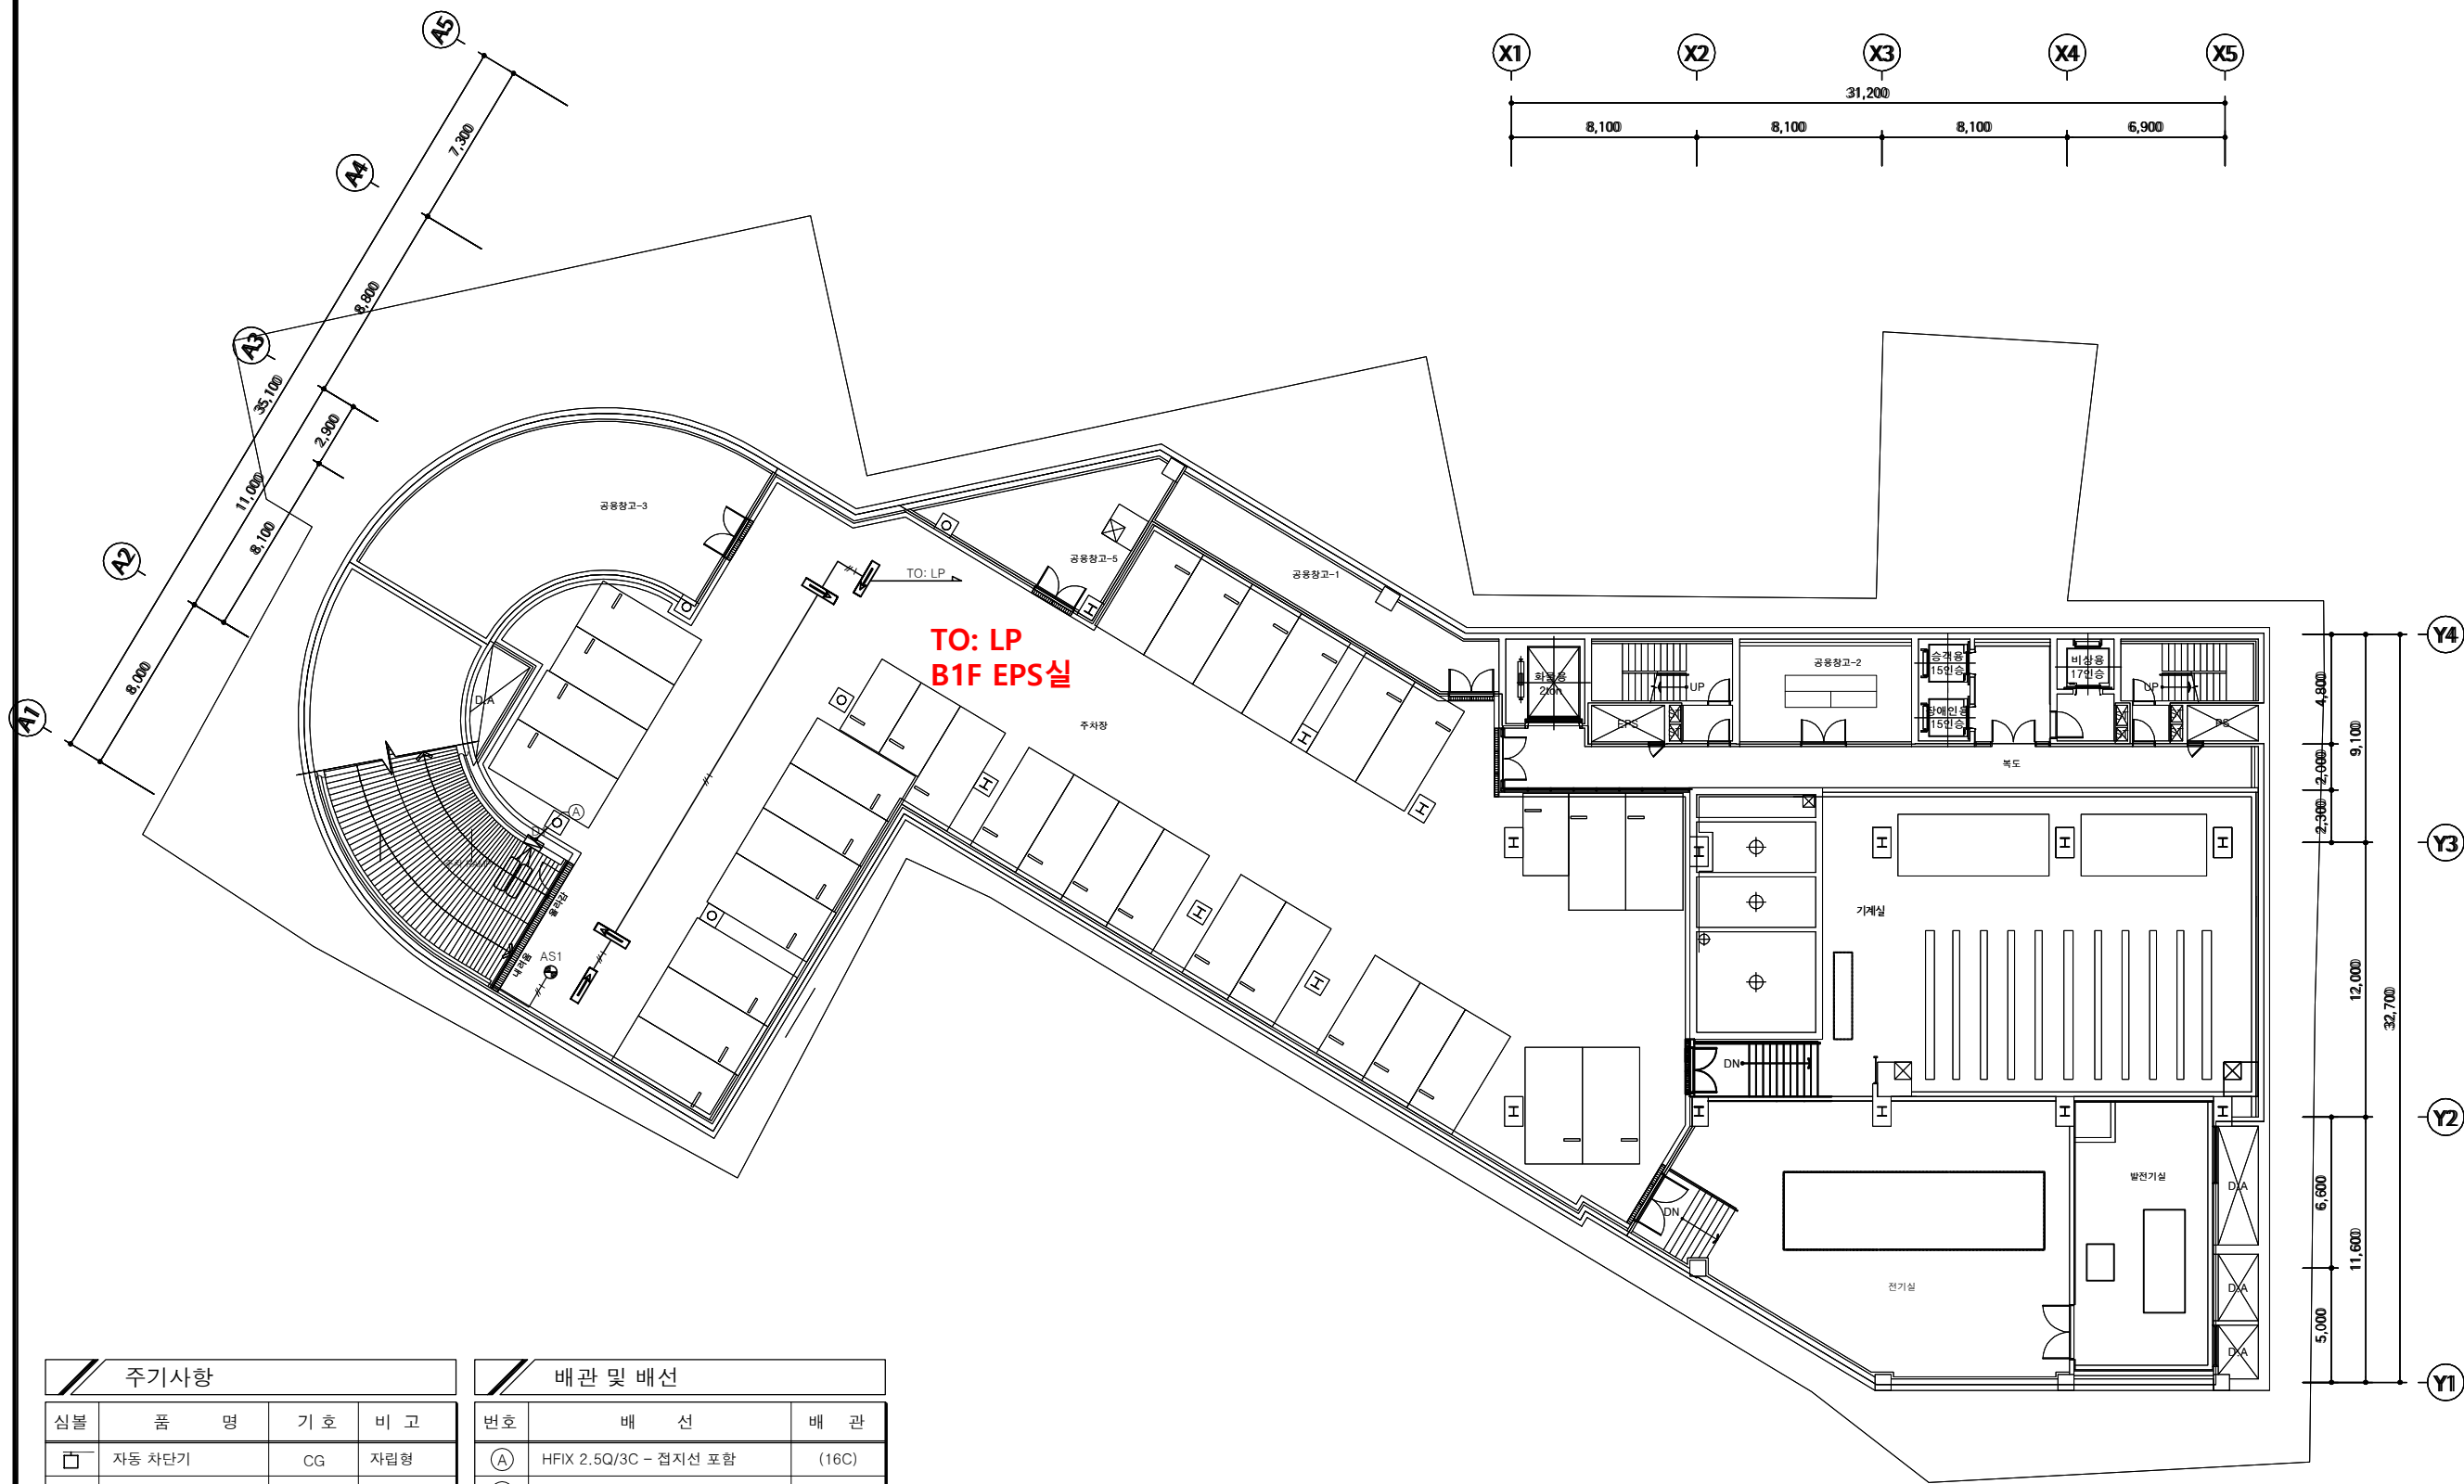

| 주기사항 |              |        |       |
|------|--------------|--------|-------|
| 심볼   | 품 명          | 기 호    | 비 고   |
|      | 자동 차단기       | CG     | 자립형   |
|      | 주차권 발행기      | TD     | 자립형   |
|      | 차량번호 인식기/전광판 | LPR/DR | 자립형   |
|      | 유인요금계산기      | FC     | 탁상형   |
|      | 차량 검지기       | D      | 벽매입형  |
|      | LOOP COIL    | LC     | 바닥매입형 |
|      | 주차관리 컴퓨터     | HC     | 탁상형   |
|      | 장내경광등        | AS     | 천정형   |
|      | 출차주의등        | COW    | 자립형   |
|      | 단면유도등        | S      | 천칭형   |
|      | 양면유도등        | SS     | 천칭형   |

| 배관 및 배선                      |                          |       |
|------------------------------|--------------------------|-------|
| 번호                           | 배 선                      | 배 관   |
| (A)                          | HFIX 2.5Q/3C - 접지선 포함    | (16C) |
| (B)                          | CV 6SQ/3C - 접지선 포함       | (28C) |
| (C)                          | CV 4SQ/3C - 접지선 포함       | (28C) |
| (D)                          | FTP (CAT.5e) CABLE 4P    | (16C) |
| (E)                          | UTP (CAT.5e) CABLE 4P    | (16C) |
| (F)                          | UTP (CAT.5e) CABLE 4P X2 | (16C) |
| (G)                          | UTP (CAT.5e) CABLE 4P X3 | (22C) |
| —□— 는 AC 220V IN             |                          |       |
| —//— 는 HFIX 2.5Q/3C (16C) 임. |                          |       |

지하 4층 주차관제설비 평면도  
SCALE:1/150

녹색 에너지 설계 약정업체  
종합 전기 설계업체 서울E-1-0023  
종합 전기 관리업체 서울S-1-0063  
연지니이링플로잉주제(정보통신) 10-104호  
주식회사 전기설계. 협인

REVISION DESCRIPTION DATE

ORDER ORGAN

INVESTMENT  
터티벤처인베스트먼트  
대표전화(02)579-8361  
팩시밀리(02)579-8364

PROJECT OFFICE

ATEC(주)에이텍종합건축사사무소  
ARCHITECTS & ASSOCIATES  
대표전화(02)3462-6366  
팩시밀리(02)3462-6368

DRAWING TITLE

지하 4층 주차관제설비 평면도

SCALE

A1 : 1 / 150  
A3 : 1 / 300

APPROVED

ARCHITECT 김 상 길

DRAWN

강 봉 구

DATE

2014. 03

CHECKED

DATE

2014. 03

CONSULTANT

DRAWING NO.

T-302