


[illegible][illegible][illegible]

SCALE:NONE

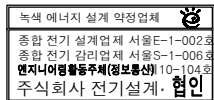

성수동1가
지식산업센터
신축공사

NOTES

REVISION	DESCRIPTION	DATE
ORDER ORIGIN		
TT INVESTMENT 티티벤처인베스트먼트 대표전화(02)579-8361 팩시밀리(02)579-8364		
PROJECT OFFICE		
Atec ARCHITECTS ASSOCIATES (주)에이텍종합건축사사무소 대표전화(02)3462-6366 팩시밀리(02)3462-6326		
DRAWING TITLE		
도면목록 (소방)		
SCALE		APPROVED
A1 : NONE		ARCHITECT 김 상 길
A3 : NONE		
DRAWN	DATE	
남 창 모	2014. 03	
CHECKED	DATE	
	2014. 03	
CONSULTANT		
DRAWING NO.		
F-001		

FIRE ALARM LEGEND

(방 재 FIRE PROTECTION SYSTEM)

	천 정 형 피 난 구 유 도 등 EXIT LIGHTING, CEILING TYPE	대형 L LARGE	중형 M MIDDLE	
	벽 부 형 피 난 구 유 도 등 EXIT LIGHTING, WALL TYPE	대형 L LARGE	중형 M MIDDLE	
	바 닥 매 입 객 석 유 도 등 RECESSED IN FLOOR TYPE ESCAPE LIGHTING FOR SEAT AREA			
	화 재 경 보 정 온 식 스 포 트 형 감 지 기 FIXED TEMPERATURE TYPE HEAT DETECTOR			
	화 재 경 보 차 동 식 스 포 트 형 감 지 기 FLUORESCENT LIGHTING FIXTURE, WALL TYPE			
	화 재 경 보 연 기 식 스 포 트 형 감 지 기 SMOKE DETECTOR	제3종 3RD DEGREE	아나로그형 연기식 감지기 ANALOG TYPE SMOKE DETECTOR	
	소 화 전 내 수 동 발 신 기 S E T COMBINATION PANEL OUTDOOR HYDRANT BOX	발신기 SET내 분산형 중계기 내장 표시 WITH REPEATERS		
	단 독 형 수 동 발 신 기 S E T COMBINATION PANEL	발신기 SET내 분산형 중계기 내장 표시 WITH REPEATERS		
	프 리 액 션 발 브 위 치 표 시 SPRINKLER PREACTION VALVE			기계 소방 제원 참조 REFER TO DETAILS PRESENTED ON FIRE PROTECTION SYSTEM DRAWINGS
	알 램 발 브 위 치 표 시 SPRINKLER ALARM VALVE			기계 소방 제원 참조 REFER TO DETAILS PRESENTED ON FIRE PROTECTION SYSTEM DRAWINGS
	배 연 창 표 시 SMOKE WINDOW			건축 설계 제원 참조 REFER TO DETAILS PRESENTED ON ARCHITECT DRAWINGS
	배 연 창 수 동 조 작 함 CONTROL BOX FOR SMOKE WINDOW			건축 설계 제원 참조 REFER TO DETAILS PRESENTED ON ARCHITECT DRAWINGS
	배 연 창 연 동 제 어 반 SMOKE WINDOW CONTROL PANEL			건축 설계 제원 참조 REFER TO DETAILS PRESENTED ON ARCHITECT DRAWINGS
	소 화 가 스 방 출 표 시 등 HALON or CO ² , NAF-III DISCHARGE LIGHTING			
	소 화 가 스 방 출 싸 이 렌 SIREN FOR FIREGAS DISCHARGE			
	소 화 가 스 수 동 조 작 함 HALON or CO ² , NAF-III MANUAL LIGHTING			
	알 램 발 브 동 작 싸 이 렌 SIREN FOR ALARM VALVE OPERATION			
	방 화 D O O R 릴 리 즈 FIRE DOOR RELEASE			건축 설계 제원 참조 REFER TO DETAILS PRESENTED ON ARCHITECT DRAWINGS
	제 연 답 파 위 치 표 시 SMOKE DAMPER			기계 소방 제원 참조 REFER TO DETAILS PRESENTED ON FIRE PROTECTION SYSTEM DRAWINGS
	제 연 답 파 수 동 조 작 함 SMOKE MOTOR DAMPER CONTROL PANEL			
	방 화 샷 다 연 동 제 어 반 FIRE SHUTTER CONTROL PANEL			건축 설계 제원 참조 REFER TO DETAILS PRESENTED ON ARCHITECT DRAWINGS
	전 동 기 및 샷 다 수 동 조 작 스 위 치 MANUAL SWITCH FOR MOTOR OR SHUTTER			건축 설계 제원 참조 REFER TO DETAILS PRESENTED ON ARCHITECT DRAWINGS
	방 재 설 비 용 중 계 기 REPEATER FOR FIRE PROTECTION SYSTEM	집합형 중계기함 BOX FOR GROUPING REPEATERS		
	화 재 경 보 설 비 수 신 반 FIRE ALARM CONTROL PANEL			상 세 참 조 REFER TO DETAIL
	비 상 콘 센 트 함 EMERGENCY RECEPTACLE BOX			상 세 참 조 REFER TO DETAIL
	무 선 통 신 보 조 설 비 접 속 단 자 TERMINAL FOR CONCEIVER			
	청 각 장 에 인 용 시 각 경 보 장 치 VISUAL ALARM FOR HEARING DISABLED			높이 : 바닥에서 2,500 이하 H : FL + 2,500 BELOW
	휴대용 비상조명등			

	천 정 스 라 브 매 입 또는 천 정 은 폐 배 관 배 선 CONDUIT & WIRE EMBED IN CEILING SLAB OR CONCEALED IN CEILING	
	바 닥 스 라 브 매 입 배 관 배 선 CONDUIT & WIRE EMBED IN FLOOR SLAB	
	천 정 노 출 배 관 배 선 CONDUIT & WIRE EXPOSED ON CEILING	
	1 종 가 요 전 선 관 배 관 배 선 FLEXIBLE CONDUIT & WIRE	
	귀 로 표 시 RUN TO TERMINAL BOX	
	전 선 관 입 상, 입 하, 통과 표시 DIRECTION OF CONDUIT UPWARD, DOWNWARD, THROUGH	

◆ 배관배선 (특기없는한 강제 주장 전선관을 사용한다) 1. 자동 화재 탐지 설비 <table><tr><td></td><td>HFIX 1.5" x 2</td><td>(16) : 감지기</td><td rowspan="5"> ① 전선 중첩 ② 도체 규격 :1등급 (단선) 사용 ③ 전선 가닥수 ④ 전선관 규격 </td></tr><tr><td></td><td>HFIX 1.5" x 4</td><td>(16) : 감지기</td></tr><tr><td></td><td>HFIX 4" x 2 E4"</td><td>(16) : 유도등</td></tr><tr><td></td><td>HFIX 4" x 2</td><td>(16) : D.C등</td></tr><tr><td></td><td>HFIX 2.5" x 2</td><td>(16) : 시각경보장치</td></tr><tr><td></td><td>① ② ③ ④</td><td></td><td></td></tr> 2. 특기 없는 한 접지선(E)은 녹색 HIV 전선임. EXCEPT SPECIAL MARK EARTH WIRE IS GREEN HIV WIRE ◆ PULL BOX 규격 <table><tr><th>SYMBOL</th><th>규격</th><th>비고</th></tr><tr><td></td><td>150 x 150 x 100</td><td></td></tr><tr><td></td><td>200 x 200 x 100</td><td></td></tr><tr><td></td><td>300 x 300 x 100</td><td></td></tr><tr><td></td><td>400 x 400 x 200</td><td></td></tr></table> ◆ SYMBOL은 공중별 해당 사항만 적용한다. </table>		HFIX 1.5" x 2	(16) : 감지기	① 전선 중첩 ② 도체 규격 :1등급 (단선) 사용 ③ 전선 가닥수 ④ 전선관 규격		HFIX 1.5" x 4	(16) : 감지기		HFIX 4" x 2 E4"	(16) : 유도등		HFIX 4" x 2	(16) : D.C등		HFIX 2.5" x 2	(16) : 시각경보장치		① ② ③ ④			SYMBOL	규격	비고		150 x 150 x 100			200 x 200 x 100			300 x 300 x 100			400 x 400 x 200		◆ 설치높이 · 백부형 배선기구 및 기기 설치 높이는 아래와 같다 <table><tr><th>구분</th><th>내용</th><th>설치높이(기준)</th></tr><tr><td rowspan="2">유도등 설비</td><td>백부형 피난구 유도등</td><td>출입문상단+100</td></tr><tr><td>통로유도등</td><td>H-FL+500 (바닥)</td></tr><tr><td rowspan="5">경보 설비</td><td>수동 발신기 SET</td><td>H-FL+1,500 (층상)</td></tr><tr><td>소화가스 방출 싸이렌</td><td>H-FL+2,500 (층상)</td></tr><tr><td>알람발브 동작 싸이렌</td><td>H-FL+2,500 (층상)</td></tr><tr><td>소화가스 방출 싸이렌</td><td>출입문상단+100</td></tr><tr><td>시각 경보장치</td><td>H-FL+2,500 이하</td></tr><tr><td rowspan="5">소화활동 설비</td><td>배연창 수동 조작함</td><td>H-FL+1,200 (층상)</td></tr><tr><td>배연창 연동 제어반</td><td>H-FL+1,200 (층상)</td></tr><tr><td>제연답파 수동 조작함</td><td>H-FL+1,500 (층상)</td></tr><tr><td>방화샷다 연동 제어반</td><td>H-FL+1,500 (층상)</td></tr><tr><td>방화샷다 수동 스위치</td><td>H-FL+1,200 (층상)</td></tr><tr><td rowspan="2">비상전원 콘센트함</td><td>무선통신보조설비 접속단자</td><td>H-FL+1,500 (층상)</td></tr><tr><td></td><td>H-FL+1,200 (층상)</td></tr></table> 백부형 기기의 설치 높이가 표기가 없는 경우에는 불면 및 상세 참조 유도등은 11층 이상인 경우 60분 이상, 11층 이하인 경우 20분 이상 동작 가능한 축전지 사용	구분	내용	설치높이(기준)	유도등 설비	백부형 피난구 유도등	출입문상단+100	통로유도등	H-FL+500 (바닥)	경보 설비	수동 발신기 SET	H-FL+1,500 (층상)	소화가스 방출 싸이렌	H-FL+2,500 (층상)	알람발브 동작 싸이렌	H-FL+2,500 (층상)	소화가스 방출 싸이렌	출입문상단+100	시각 경보장치	H-FL+2,500 이하	소화활동 설비	배연창 수동 조작함	H-FL+1,200 (층상)	배연창 연동 제어반	H-FL+1,200 (층상)	제연답파 수동 조작함	H-FL+1,500 (층상)	방화샷다 연동 제어반	H-FL+1,500 (층상)	방화샷다 수동 스위치	H-FL+1,200 (층상)	비상전원 콘센트함	무선통신보조설비 접속단자	H-FL+1,500 (층상)		H-FL+1,200 (층상)
	HFIX 1.5" x 2	(16) : 감지기	① 전선 중첩 ② 도체 규격 :1등급 (단선) 사용 ③ 전선 가닥수 ④ 전선관 규격	
	HFIX 1.5" x 4	(16) : 감지기	
	HFIX 4" x 2 E4"	(16) : 유도등	
	HFIX 4" x 2	(16) : D.C등	
	HFIX 2.5" x 2	(16) : 시각경보장치	
	① ② ③ ④	
SYMBOL	규격	비고	
	150 x 150 x 100	
	200 x 200 x 100	
	300 x 300 x 100	
	400 x 400 x 200	
구분	내용	설치높이(기준)	
유도등 설비	백부형 피난구 유도등	출입문상단+100	
	통로유도등	H-FL+500 (바닥)	
경보 설비	수동 발신기 SET	H-FL+1,500 (층상)	
	소화가스 방출 싸이렌	H-FL+2,500 (층상)	
	알람발브 동작 싸이렌	H-FL+2,500 (층상)	
	소화가스 방출 싸이렌	출입문상단+100	
	시각 경보장치	H-FL+2,500 이하	
소화활동 설비	배연창 수동 조작함	H-FL+1,200 (층상)	
	배연창 연동 제어반	H-FL+1,200 (층상)	
	제연답파 수동 조작함	H-FL+1,500 (층상)	
	방화샷다 연동 제어반	H-FL+1,500 (층상)	
	방화샷다 수동 스위치	H-FL+1,200 (층상)	
비상전원 콘센트함	무선통신보조설비 접속단자	H-FL+1,500 (층상)	
		H-FL+1,200 (층상)	

PROJECT TITLE

성수동1가
지식산업센터
신축공사

NOTES

REVISION	DESCRIPTION	DATE


ORDER ORGAN	티티벤처인베스트먼트
INVESTMENT	대 표 전 화 021579-8361 팩 시 밀 리 021579-8364
PROJECT OFFICE	ATEC(주)에이텍종합건축사사무소
ARCHITECTS & ASSOCIATES	대 표 전 화 0213462-6366 팩 시 밀 리 0213462-6368

DRAWING TITLE	
범례 (소방)	
SCALE	APPROVED
A1 : NONE A3 : NONE	ARCHITECT 김 상 길
DRAWN 남 창 모	DATE 2014. 03
CHECKED	DATE 2014. 03
CONSULTANT	
DRAWING NO.	EF-002

범례 (소방)
SCALE : NONE

녹색 에너지 설계 약정업체
종합 전기 설계업체 서울E-1-002호
종합 전기 감리업체 서울S-1-006호
연지니아평화동주세(정보통신) 10-104호
주식회사 전기설계 협인

지하4층 3,900
지하3층 3,900
지하2층 3,900
지하1층 4,500
1층 6,900
2층 5,400
3층 5,400
4층 5,400
5층 3,900
6층 3,900
7층 3,900
8층 3,900
9층 3,900
10층 3,900
11층 3,900
12층 3,900
13층 3,900
14층 3,900
15층 3,900
16층 3,900
지상층

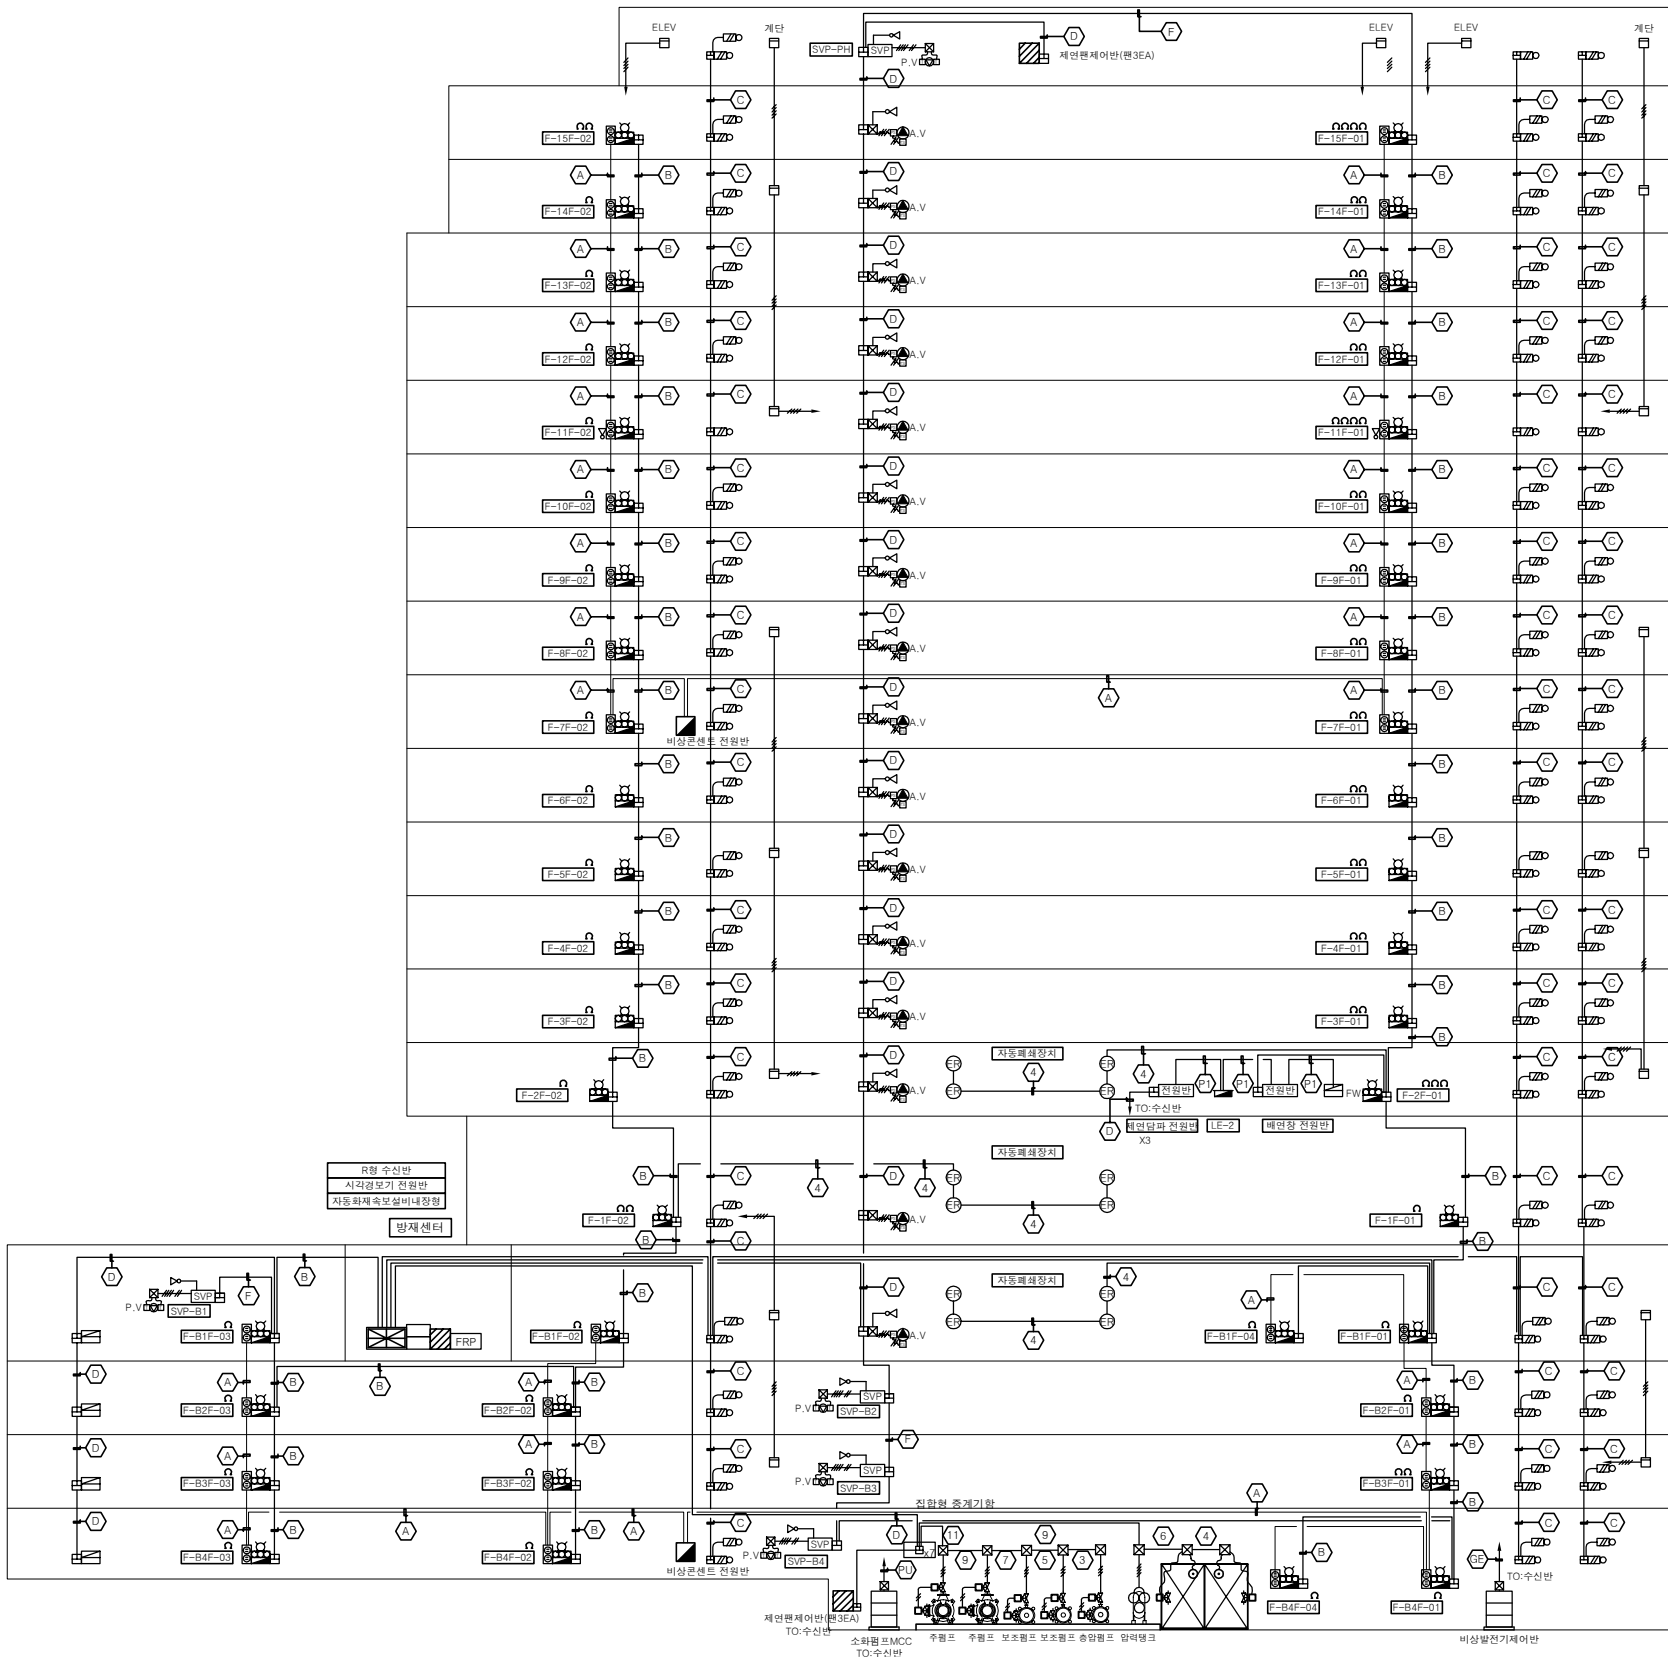

전선관 및 전선규격			
기 호	Cable Schedule	비 고	
A	HFIX 6" x 2 E 6" (28)	비상콘센트	
B	FR-CVV-SB 1.5"-2C (16) HFIX 2.5" -8 (28) HFIX 2.5" -4 (22)	통신선2, 중계기전원2, 발신기응답1, 전화1, 위치표시등2, 소화차범프작동 확인2, 시각경보기전원2	
C	FR-CVV-SB 1.5"-2C (16) HFIX 2.5" -2 HFIX 4.0" -2 (22)	통신선2, 중계기전원2, 담판전원2	
D	FR-CVV-SB 1.5"-2C (16) HFIX 2.5" -2 (16)	통신선2, 중계기전원2	
E	FR-CVV-SB 1.5"-2C (16) HFIX 2.5" -2 HFIX 4.0" -2 (22)	통신선2, 중계기전원2, 배연장치전원2	
F	FR-CVV-SB 1.5"-2C (16) HFIX 2.5" -4 (22)	통신선2, 중계기전원2, 전화2	
G	FR-CVV-SB 1.5"-2C (16) HFIX 2.5" -2 (16)	통신선2	
H	FR-3 2.5"-4C (28)	중계기전원2,	
I	FR-3 2.5"-8C (36) FR-3 2.5"-12C (36)	발전기 감시반	
J	HFIX 6mm-2, E6 (28)	소화차범프 기동반	
		전원반 전원	
 HFIX 1.5" x 2 (16)  HFIX 1.5" x 4 (16)  HFIX 1.5" x 8 (22)			
번호	전선수 및 전선관 규격	번호	전선수 및 전선관 규격
1	HFIX 2.5" x 1 (16)	7	HFIX 2.5" x 7 (28)
2	HFIX 2.5" x 2 (16)	8	HFIX 2.5" x 8 (28)
3	HFIX 2.5" x 3 (16)	9	HFIX 2.5" x 9 (28)
4	HFIX 2.5" x 4 (22)	10	HFIX 2.5" x 10 (28)
5	HFIX 2.5" x 5 (22)	11	HFIX 2.5" x 11 (36)
6	HFIX 2.5" x 6 (22)	12	HFIX 2.5" x 12 (36)

화재수신반(R형 508회로)		
번 호	회로명	회로수
1	자동화재탐지설비	57
2	계단	6
3	EV	3
4	방화샷다	8
5	SVP	10
6	AV	16
7	배연창	1
8	자동화재탐지	6
9	저수위경보	2
10	제연복합담파	3
11	제연담파	59
12	제연급기	59
13	제연배기	59
14	수동조작확인 S/W	59
15	텔 파S/W(SVP)	5
16	텔 파S/W(AV)	16
17	텔 파S/W(람프)	7
18	텔 파S/W(저수위)	2
소 계		378
여 유		130
합 계		508
비고 비상축전지 내장 오작동 방지장치 내장 청각경보인용시각경보기와연동 배연창과연동 제연담파와연동 자동화재탐지와연동		

자동화재탐지설비 계통도

SCALE : NONE

녹색 에너지 설계 약정업체
종합 전기 설계업체 서울E-1-0023
종합 전기 강리업체 서울S-1-0063
연지니엔지니어링주식(정보통상) 10-104호
주식회사 전기설계 협인

PROJECT TITLE

성수동1가
지식산업센터
신축공사

NOTES

REVISION

DESCRIPTION

DATE

ORDER ORGAN

티티벤처인베스트먼트

INVESTMENT

대표전화(02)579-8361
팩시밀리(02)579-8364

PROJECT OFFICE

ATEC(주)에이텍종합건축사사무소

ARCHITECTS & ASSOCIATES

대표전화(02)3462-6366
팩시밀리(02)3462-6366

DRAWING TITLE

자동화재탐지설비 계통도

SCALE

A1 : NONE
A3 : NONE

APPROVED

ARCHITECT

김 상 길

DRAWN

남 창 모

DATE

2014. 03

CHECKED

DATE

2014. 03

CONSULTANT


DRAWING NO.

EF-003

PROJECT TITLE

성수동1가
지식산업센터
신축공사

NOTES

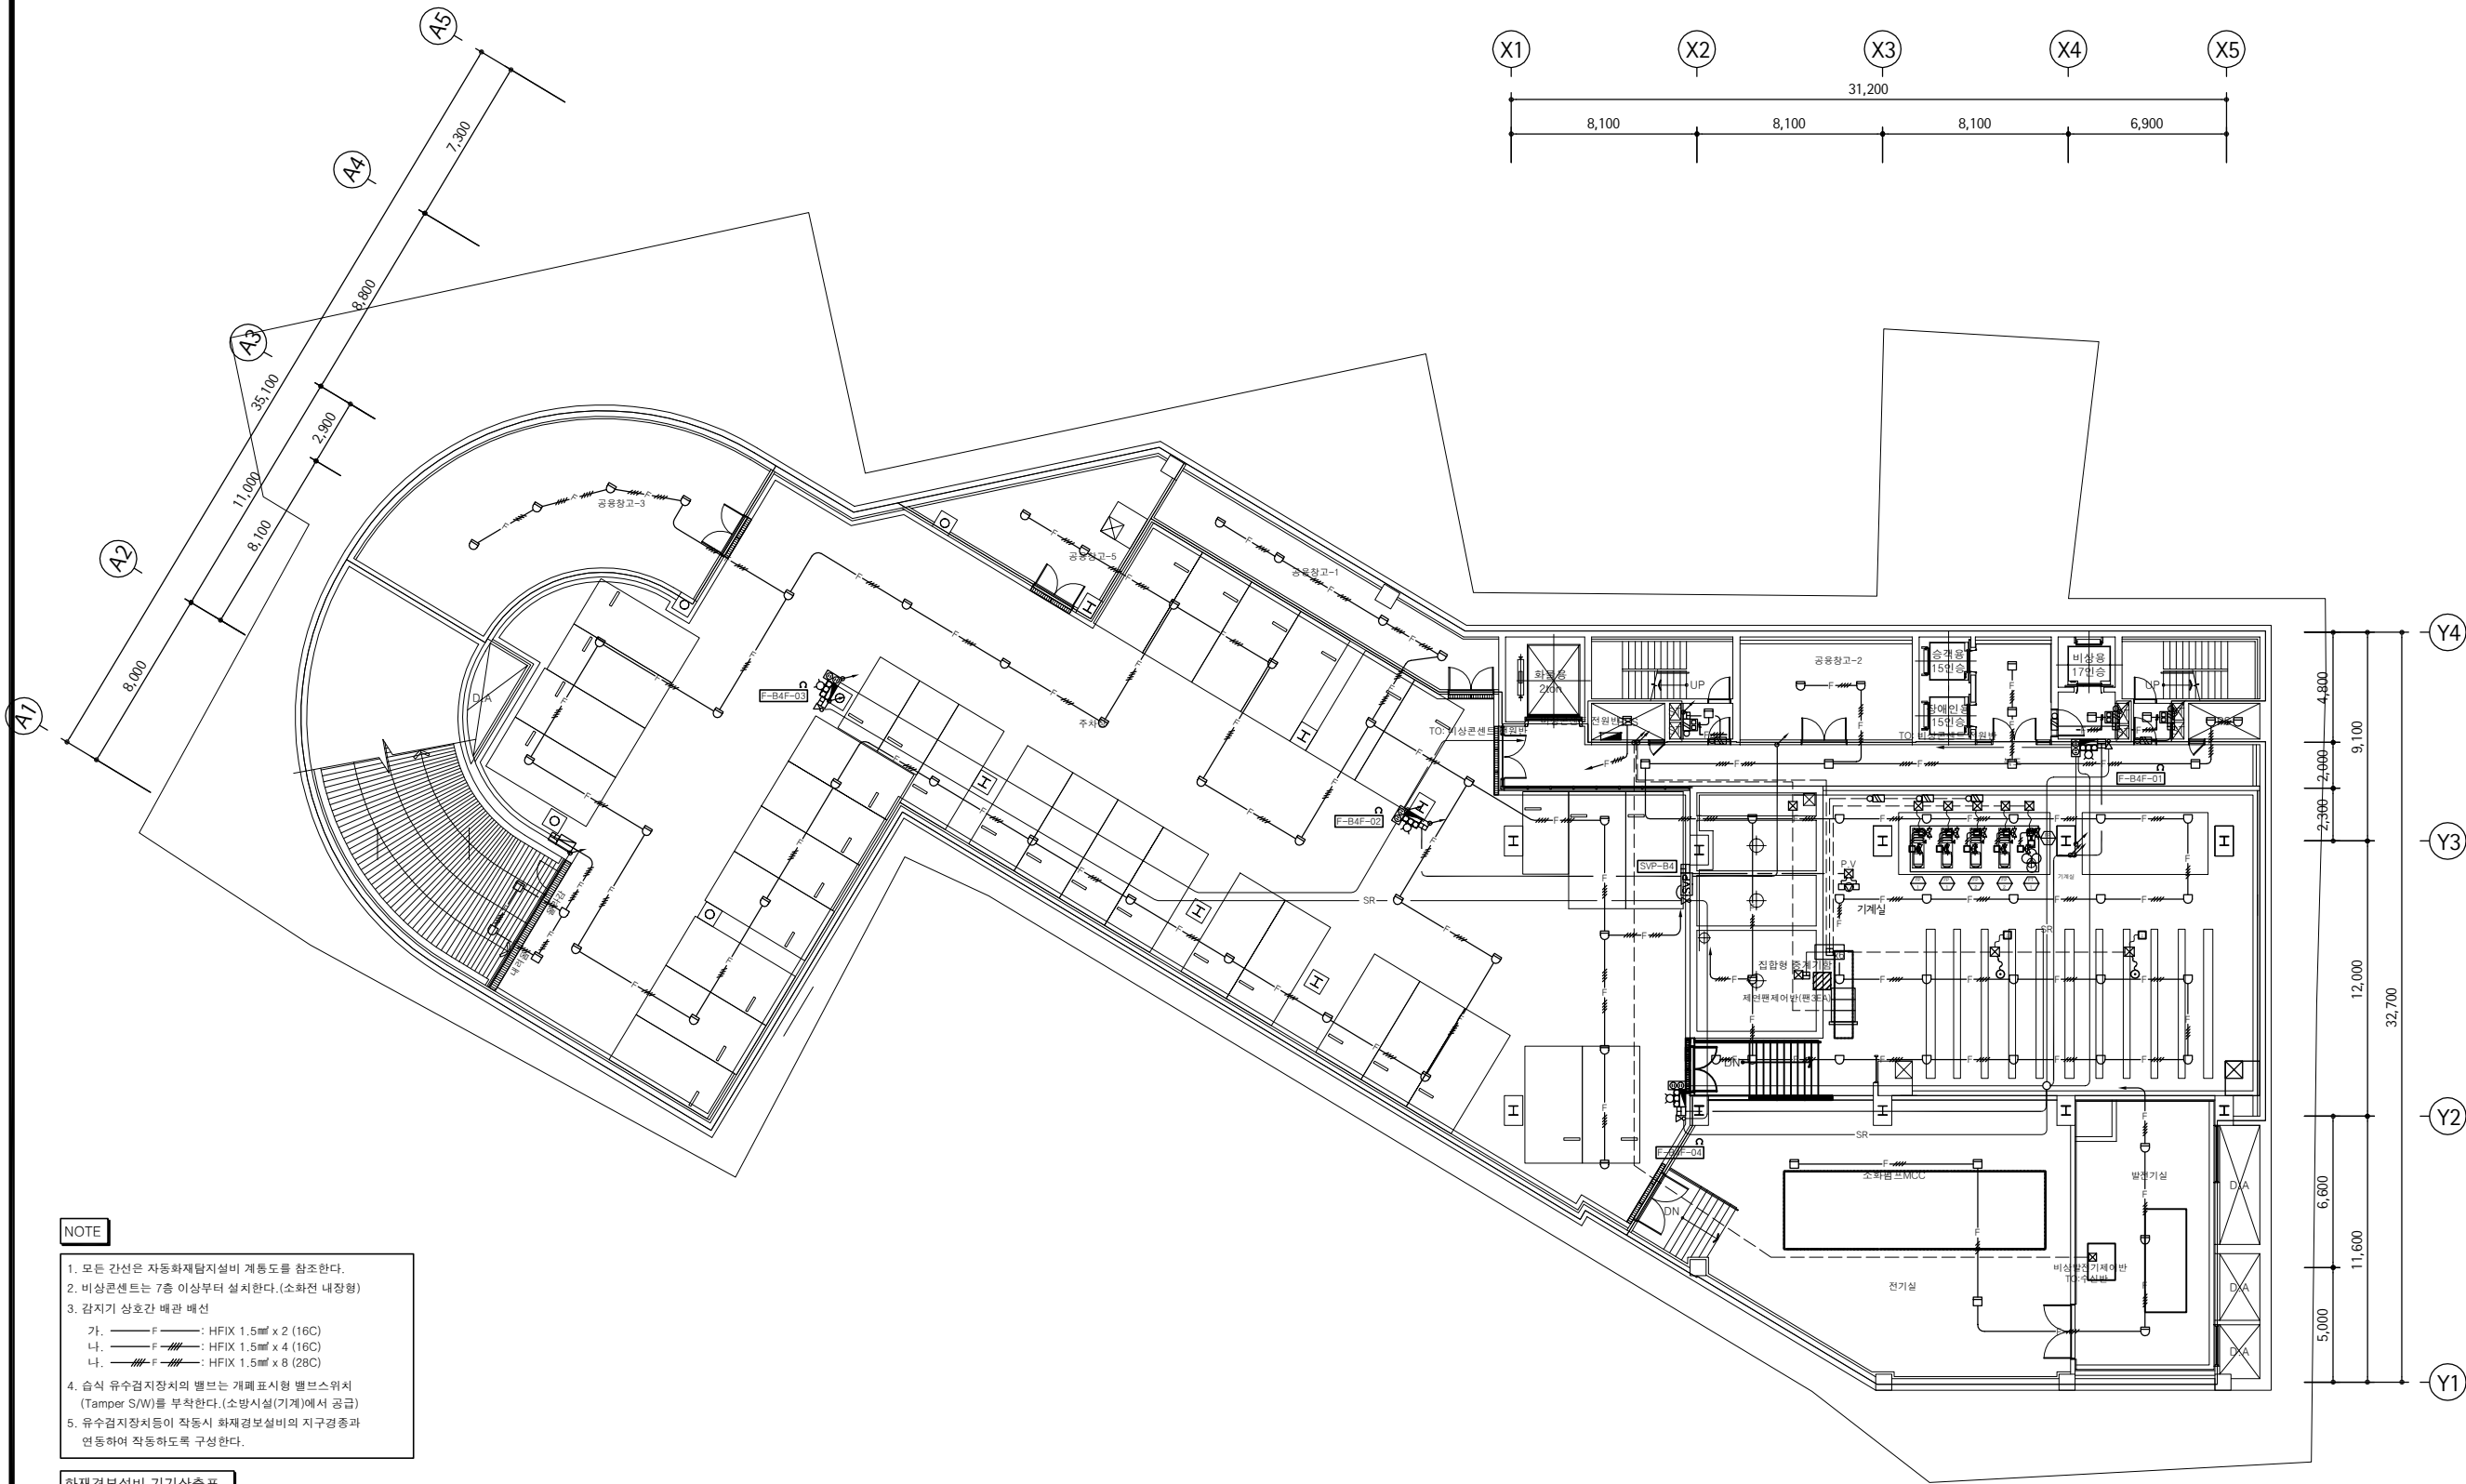

NOTE

- 모든 간선은 자동화재탐지설비 계통도를 참조한다.
- 비상콘센트는 7층 이상부터 설치한다.(소화전 내장형)
- 감지기 상호간 배관 배선
가. — F — : HFIX 1.5mm x 2 (16C)
나. — F — : HFIX 1.5mm x 4 (16C)
다. — F — : HFIX 1.5mm x 8 (28C)
- 습식 유수검지장치의 밸브는 개폐표시형 밸브스위치 (Tammer S/W)를 부착한다.(소방시설(기계)에서 공급)
- 유수검지장치들이 작동시 화재경보설비의 지구경종과 연동하여 작동하도록 구성한다.

화재경보설비 기기산출표

내역구분	설비명	수량	비고
발신기(SET (소화전부착형))		4	P형1급발신기
감지기	준비작동식용	74	
	방화샷다용	4	
	자동화재탐지용	10	
	계단용		
휴대용 비상조명등			
전자사이렌		4	
전설재연		3	
시각경보기		4	
비상콘센트		4	
슈퍼비조리판넬		1	
알람벨브	A.V		
자동폐쇄장치	O		

지하4층 자동화재탐지설비 평면도

SCALE : 1/150

녹색 에너지 설계 약정업체
종합 전기 설계업체 서울E-1-0023
종합 전기 관리업체 서울S-1-0063
엔지니어링활동주제(정보통신) 10-104호
주식회사 전기설계. 협인

REVISION

DESCRIPTION

DATE

ORDER ORGAN

티티벤처인베스트먼트
INVESTMENT
대표전화021579-8361
팩시밀리021579-8364

PROJECT OFFICE

ATEC(주)에이텍종합건축사사무소
ARCHITECTS & ASSOCIATES
대표전화0213462-6366
팩시밀리0213462-6368

DRAWING TITLE

지하4층 자동화재탐지설비 평면도

SCALE

A1 : 1/150

A3 : 1/300

APPROVED

ARCHITECT

김상길

DRAWN

남창모

DATE

2014. 03

CHECKED

DATE

2014. 03

CONSULTANT


DRAWING NO.

EF-004

PROJECT TITLE

성수동1가
지식산업센터
신축공사

NOTES

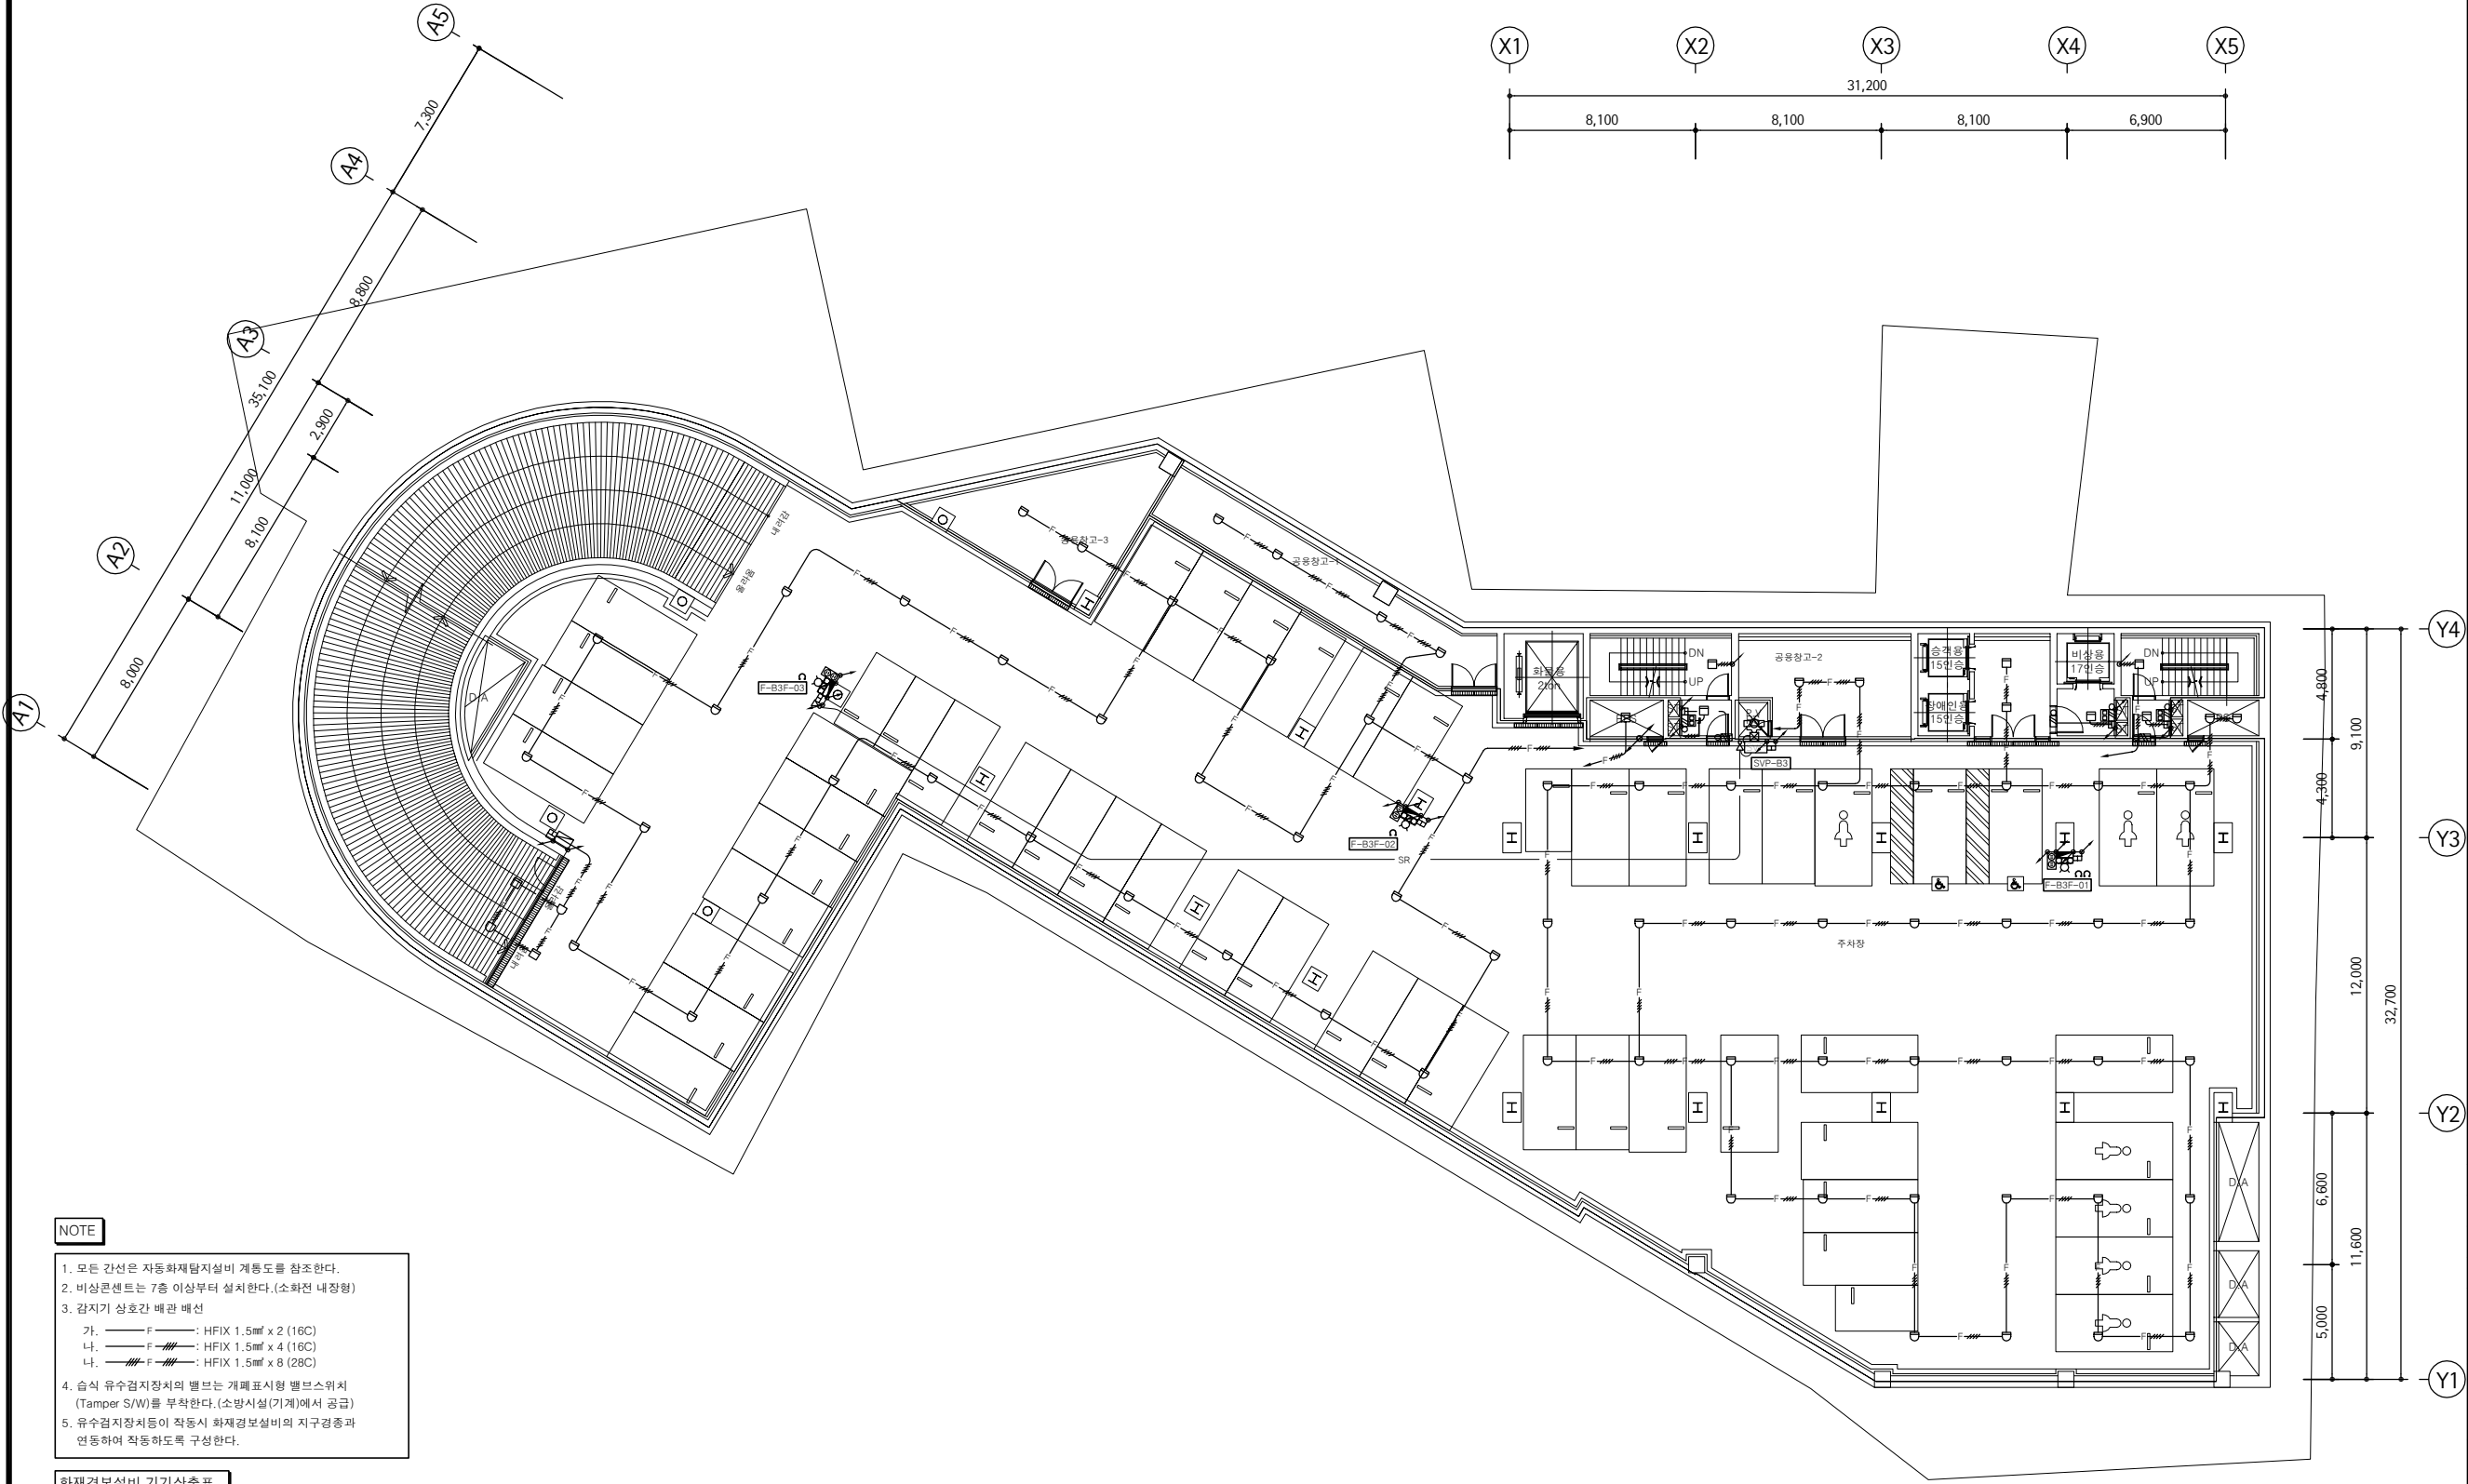

- NOTE
- 모든 간선은 자동화재탐지설비 계통도를 참조한다.
 - 비상콘센트는 7층 이상부터 설치한다.(소화전 내장형)
 - 감지기 상호간 배관 배선
가. — F — : HFIX 1.5mm x 2 (16C)
나. — F — : HFIX 1.5mm x 4 (16C)
나. — F — : HFIX 1.5mm x 8 (28C)
 - 습식 유수검지장치의 밸브는 개폐표시형 밸브스위치 (Tammer S/W)를 부착한다.(소방시설(기계)에서 공급)
 - 유수검지장치들이 작동시 화재경보설비의 지구경종과 연동하여 작동하도록 구성한다.

화재경보설비 기기산출표			
내역구분	심별	수량	비고
발신기SET (소화전부착형)		3	P형1급발신기
감지기	준비작동식용	72	
	방화샷다용	4	
	자동화재탐지용	4	
	계단용	2	
휴대용 비상조명등			
전자사이렌		2	
전실제연		3	
시각경보기		3	
비상콘센트		3	
슈퍼비조리판넬		1	
알람벨브	A.V		
자동폐쇄장치	O		

지하3층 자동화재탐지설비 평면도

SCALE : 1/150

녹색 에너지 설계 약정업체
종합 전기 설계업체 서울E-1-002호
종합 전기 감리업체 서울S-1-006호
연지니아엔지니어링(정보통선) 10-104호
주식회사 전기설계. 협인

REVISION	DESCRIPTION	DATE
ORDER ORGAN		
티티벤처인베스트먼트		
INVESTMENT		
대표전화021579-8361		
팩시밀리021579-8364		
PROJECT OFFICE		
ATEC(주)에이텍종합건축사사무소		
ARCHITECTS & ASSOCIATES		
대표전화0213462-6366		
팩시밀리0213462-6368		
DRAWING TITLE		


지하3층 자동화재탐지설비 평면도

SCALE	APPROVED
A1 : 1/150 A3 : 1/300	ARCHITECT 김 상 길
DRAWN	DATE
남 창 모	2014. 03
CHECKED	DATE
	2014. 03
CONSULTANT	
DRAWING NO. EF-005	

PROJECT TITLE

성수동1가
지식산업센터
신축공사

NOTES

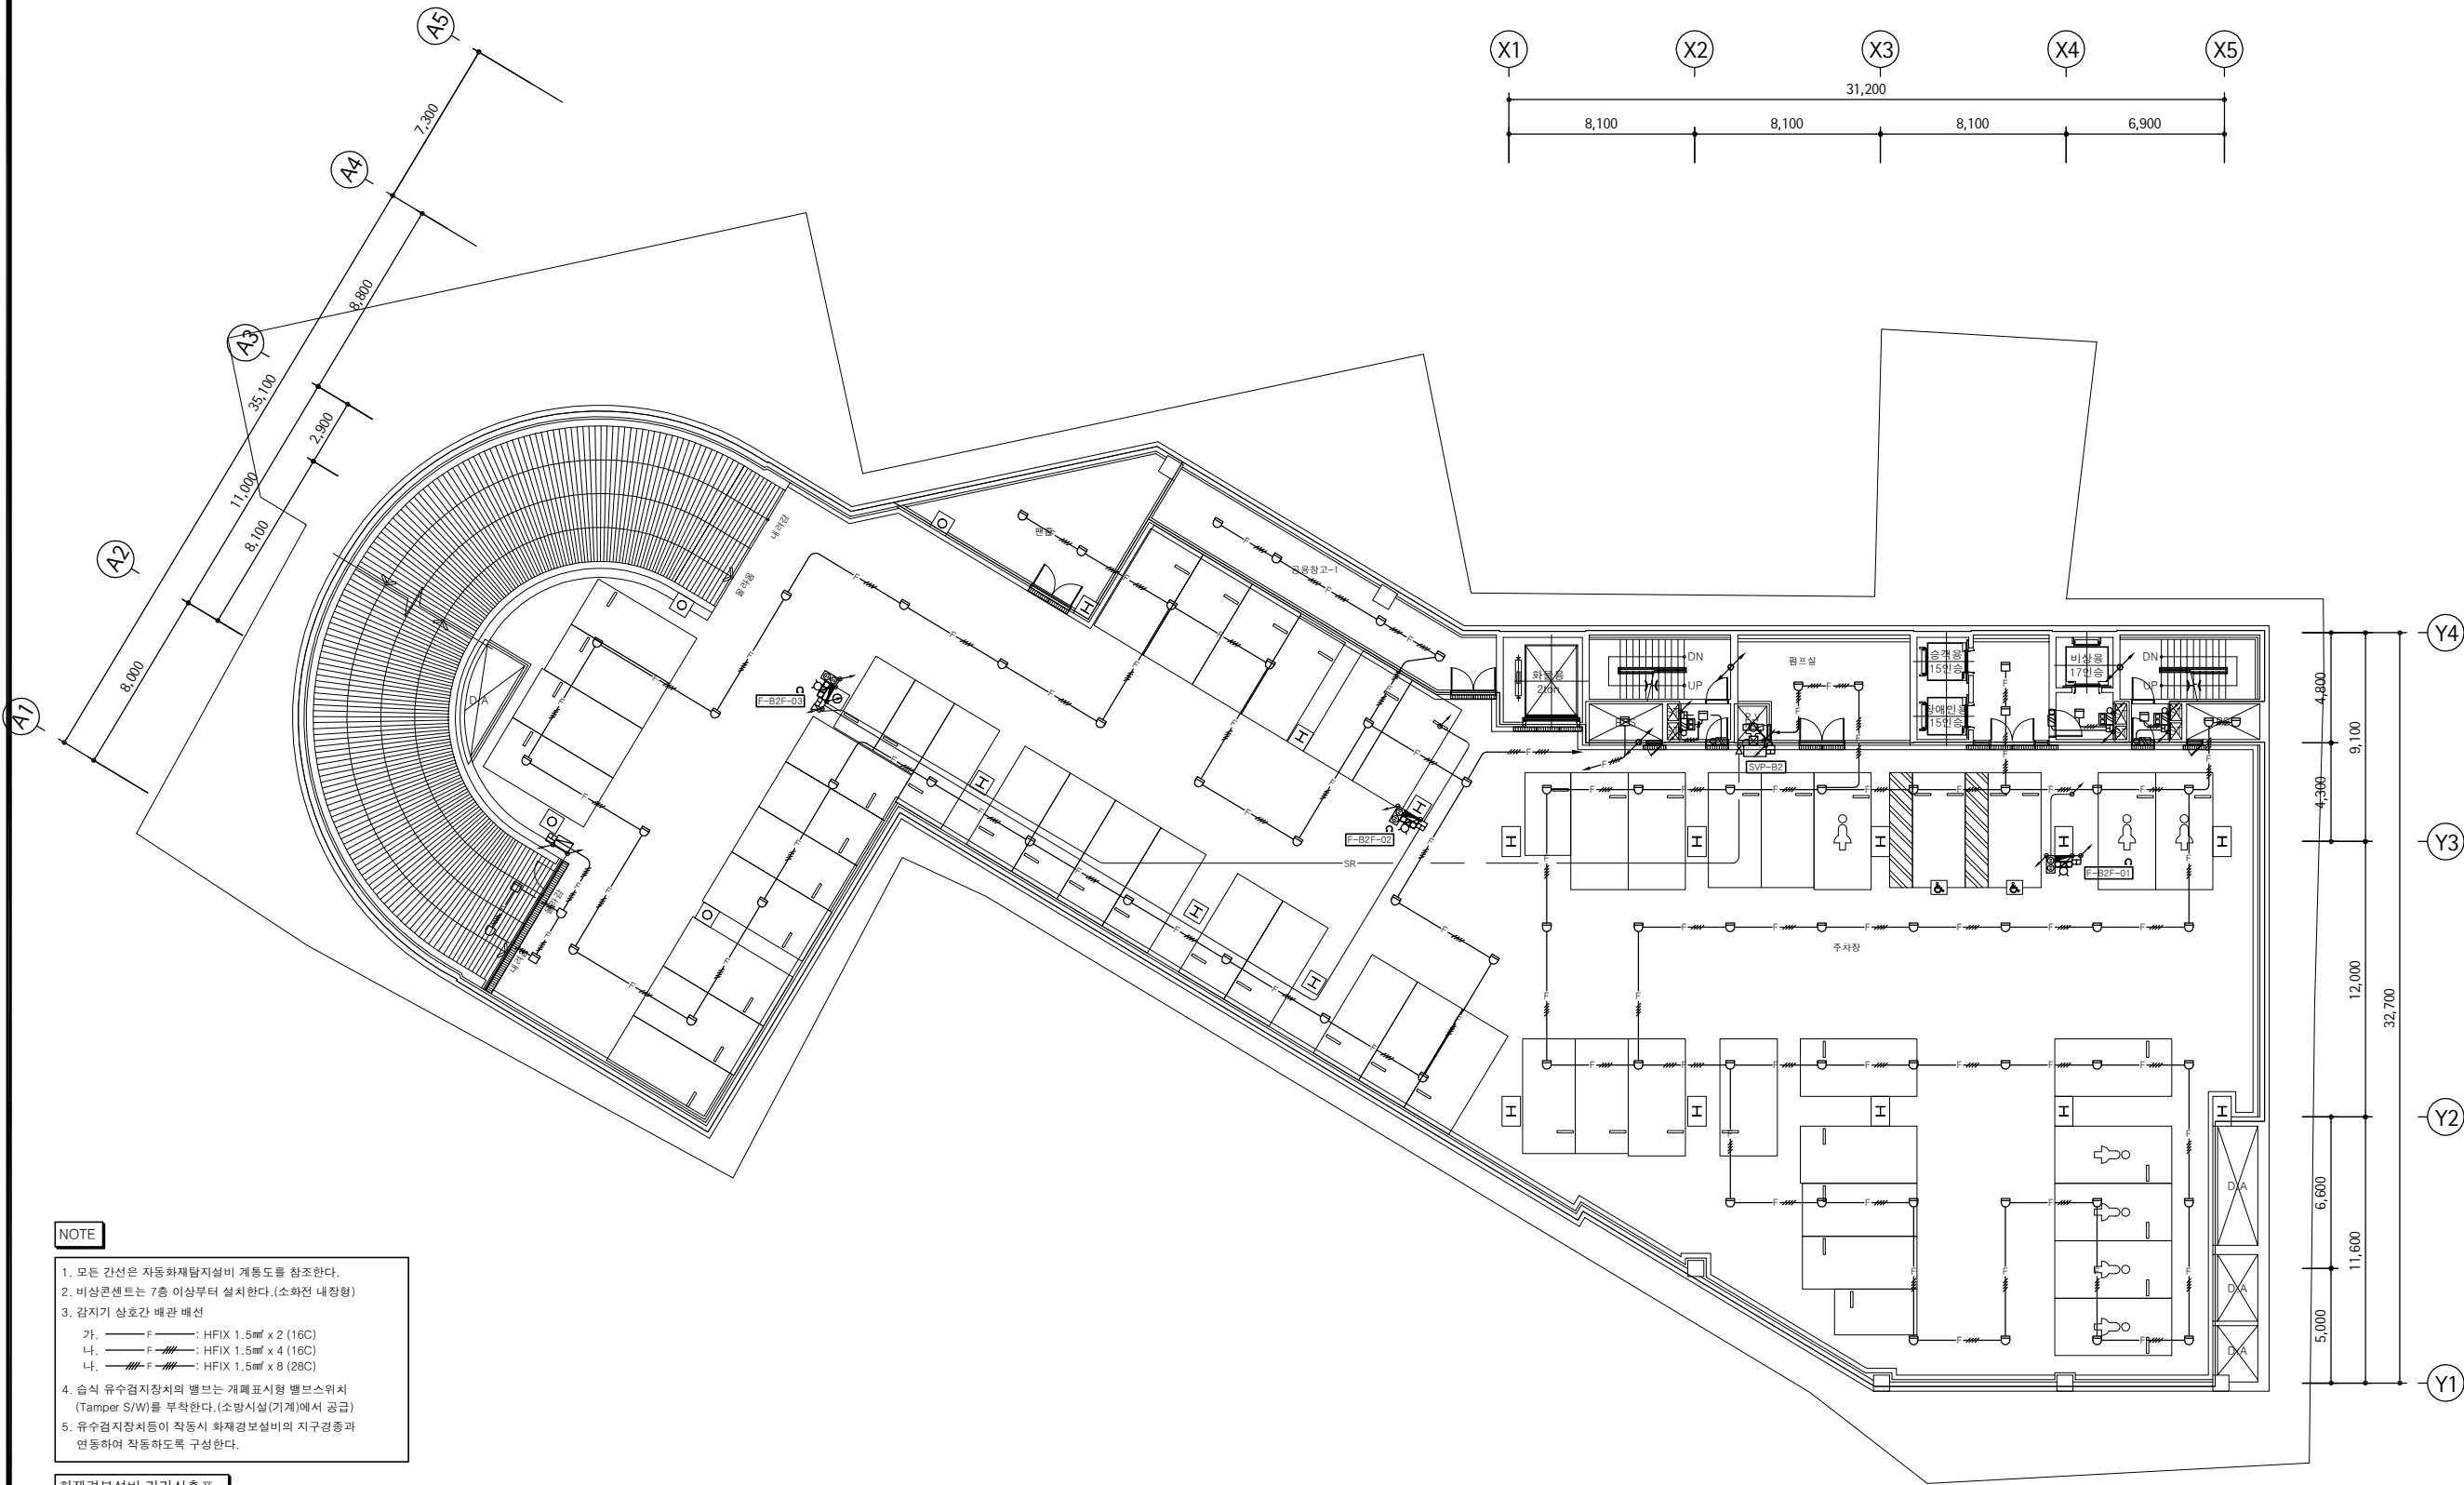

NOTE

- 모든 간선은 자동화재탐지설비 계통도를 참조한다.
- 비상콘센트는 7층 이상부터 설치한다.(소화전 내장형)
- 감지기 상호간 배관 배선
가. — F — : HFIX 1.5㎡ x 2 (16C)
나. — F — : HFIX 1.5㎡ x 4 (16C)
나. — F — : HFIX 1.5㎡ x 8 (28C)
- 습식 유수검지장치의 밸브는 개폐표시형 밸브스위치 (Tammer S/W)를 부착한다.(소방시설(기계)에서 공급)
- 유수검지장치들이 작동시 화재경보설비의 지구경종과 연동하여 작동하도록 구성한다.

화재경보설비 기기산출표

내역구분	심별	수량	비고
발신기SET (소화전부착형)		3	P형1급발신기
감지기	준비작동식용	72	
	방화샷다용	4	
	자동화재탐지용	4	
	계단용		
휴대용 비상조명등			
전자사이렌		2	
전실제연		3	
시각경보기		3	
비상콘센트		3	
슈퍼비조리판넬		1	
알람벨브	A.V		
자동폐쇄장치			

지하2층 자동화재탐지설비 평면도

SCALE : 1/150

녹색 에너지 설계 약정업체
종합 전기 설계업체 서울E-1-002호
종합 전기 감리업체 서울S-1-006호
연지니어링플랫폼주제(정보통신) 10-104호
주식회사 전기설계. 협인

REVISION DESCRIPTION DATE

ORDER ORGAN

티티벤처인베스트먼트
INVESTMENT
대표전화021579-8361
팩시밀리021579-8364

PROJECT OFFICE

ATEC(주)에이텍종합건축사사무소
ARCHITECTS & ASSOCIATES
대표전화0213462-6366
팩시밀리0213462-6368

DRAWING TITLE

지하2층 자동화재탐지설비 평면도

SCALE

A1 : 1/150
A3 : 1/300

ARCHITECT 김 상 길

DRAWN 남 창 모

DATE 2014. 03

CHECKED

DATE 2014. 03

CONSULTANT


DRAWING NO.

EF-006

PROJECT TITLE

성수동1가
지식산업센터
신축공사

NOTES

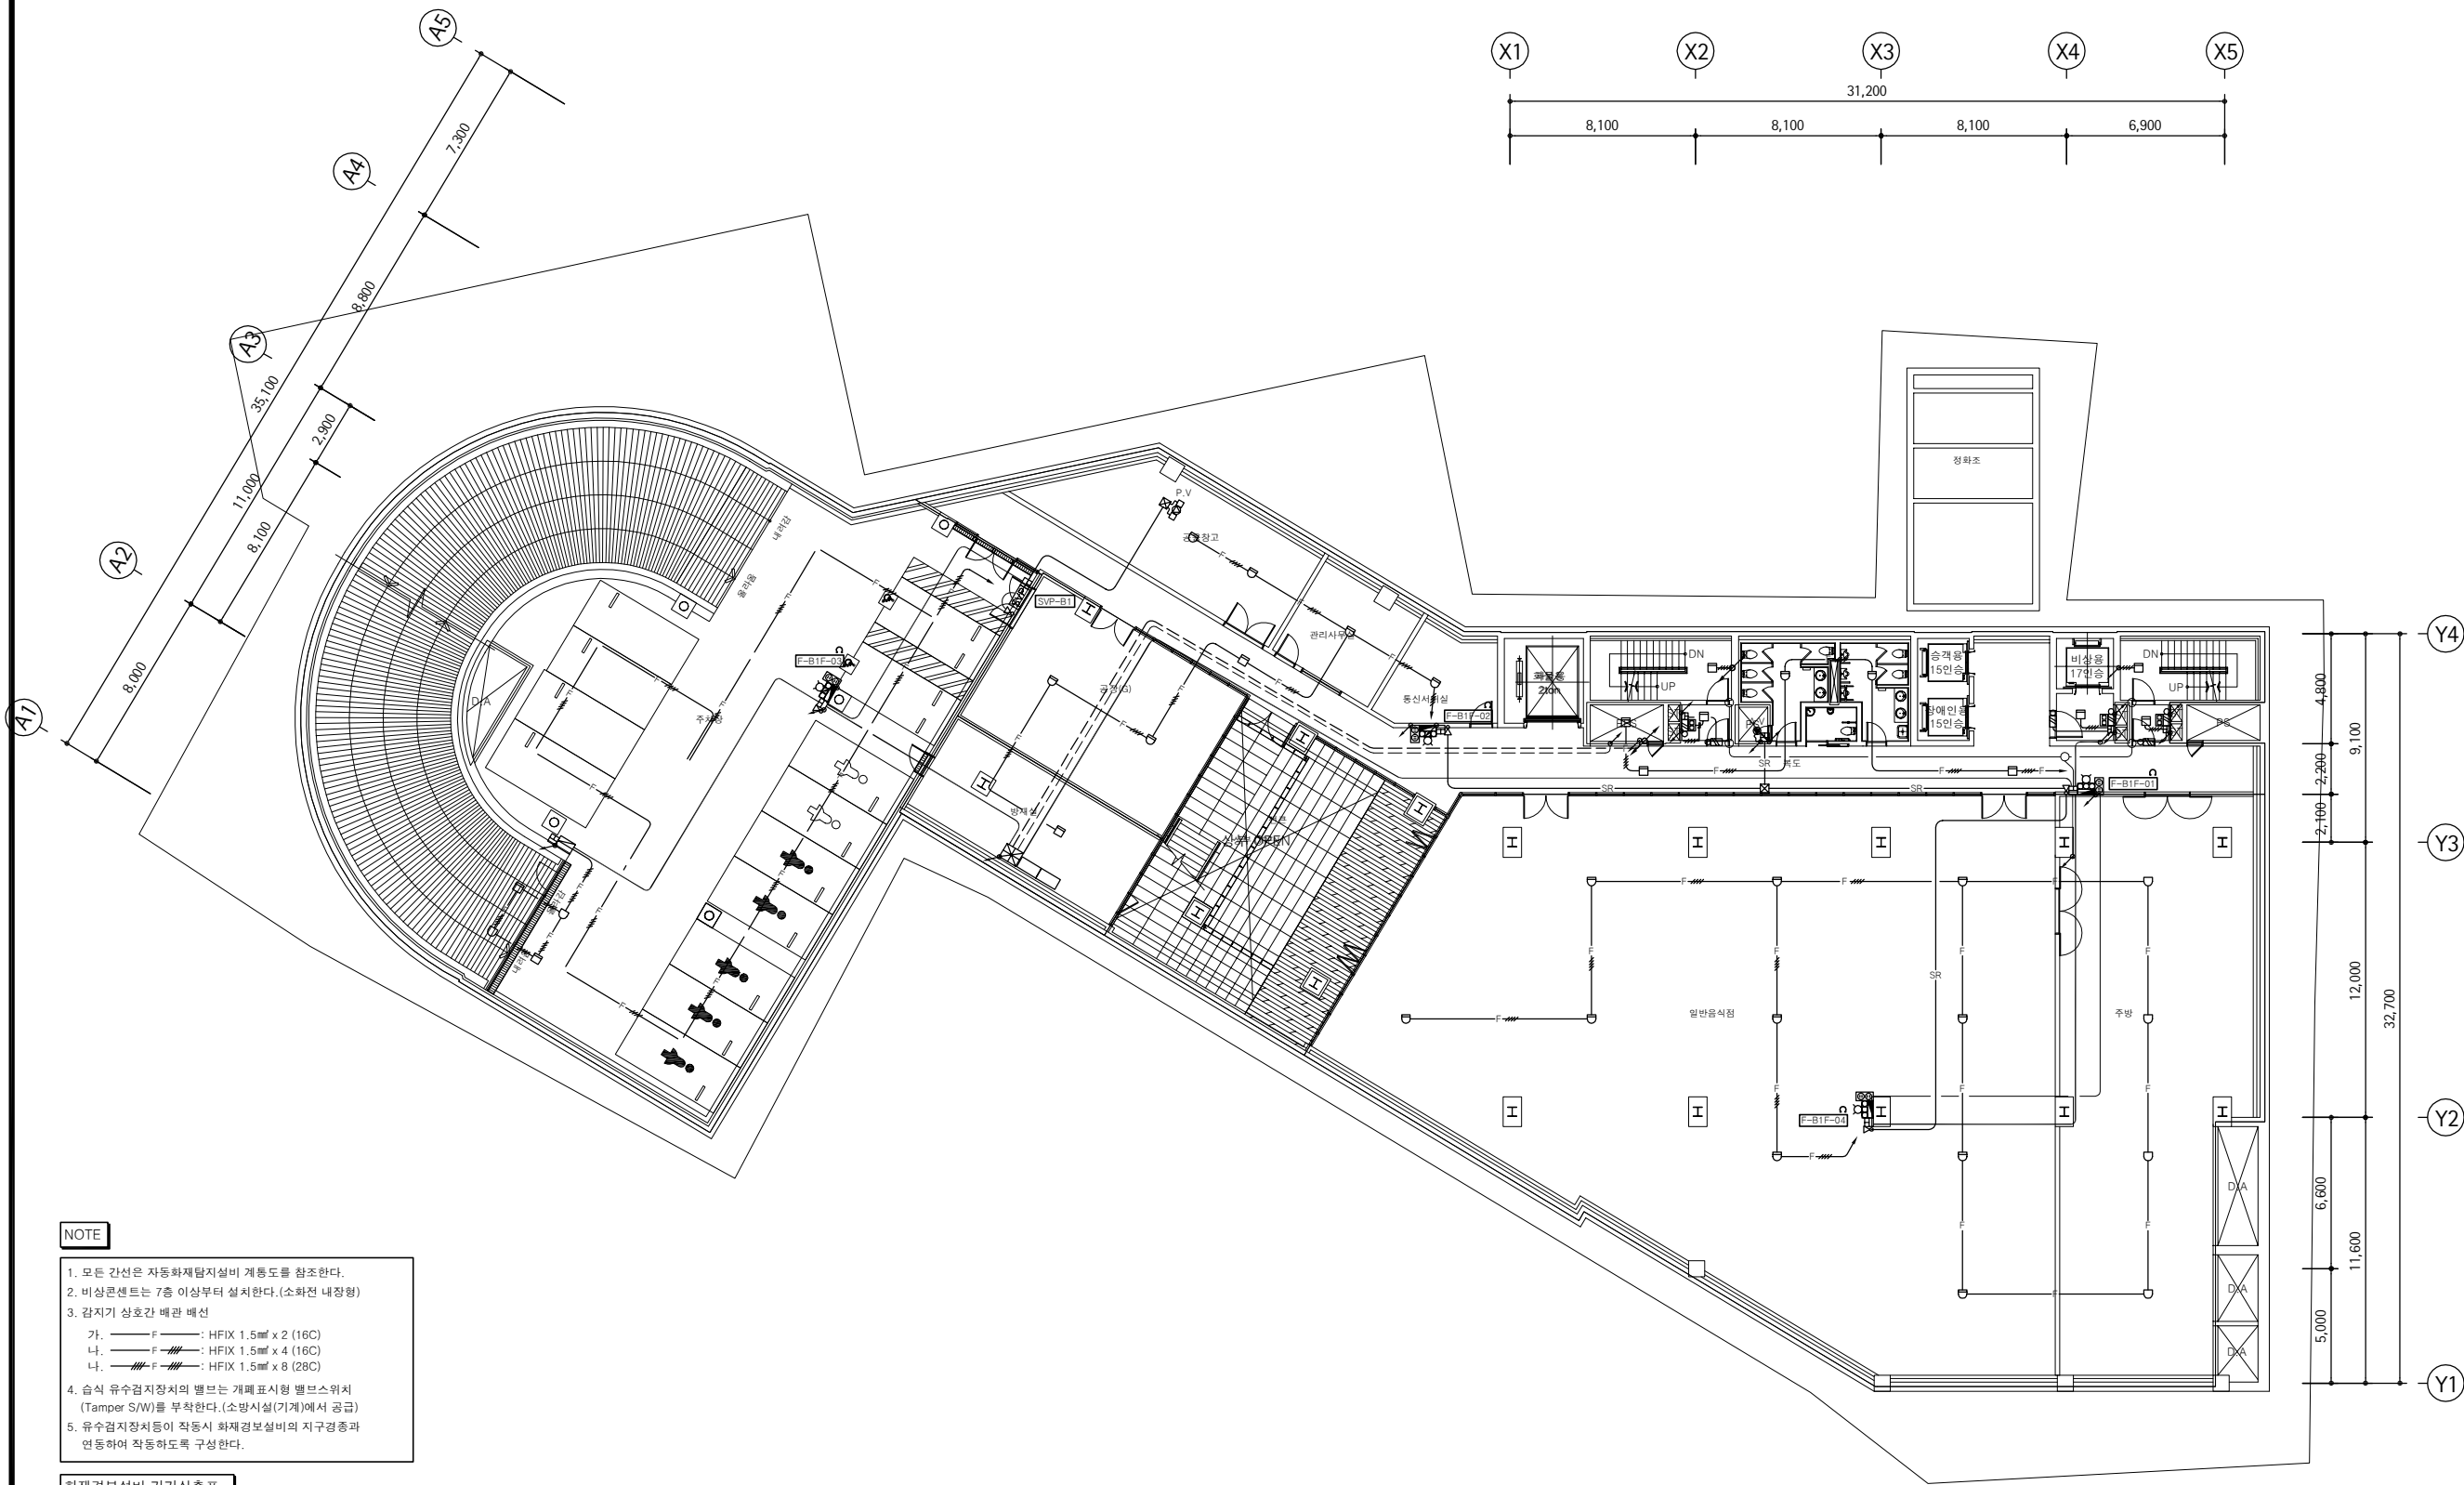

NOTE

- 모든 간선은 자동화재탐지설비 계통도를 참조한다.
- 비상콘센트는 7층 이상부터 설치한다.(소화전 내장형)
- 감지기 상호간 배관 배선
가. — F — : HFIX 1.5mm x 2 (16C)
나. — F — : HFIX 1.5mm x 4 (16C)
다. — F — : HFIX 1.5mm x 8 (28C)
- 습식 유수검지장치와 밸브는 개폐표시형 밸브스위치 (Tammer S/W)를 부착한다.(소방시설(기계)에서 공급)
- 유수검지장치등이 작동시 화재경보설비의 지구경종과 연동하여 작동하도록 구성한다.

화재경보설비 기기산출표

내역구분	심별	수량	비고
발신기SET (소화전부착형)		4	P형1급발신기
감지기	준비작동식용	12	
	방화샷다용	4	
	자동화재탐지용	30	
	계단용	2	
휴대용 비상조명등		1	
전자사이렌		5	
전실제연		3	
시각경보기		4	
비상콘센트		4	
슈퍼비조리판넬		1	
알람벨브	A.V	1	
자동폐쇄장치		4	

지하1층 자동화재탐지설비 평면도

SCALE : 1/150

녹색 에너지 설계 약정업체
종합 전기 설계업체 서울E-1-0023
종합 전기 감리업체 서울S-1-0063
연지니어링플랜트(정보통신) 10-104호
주식회사 전기설계. 협인

REVISION DESCRIPTION DATE

ORDER ORGAN

INVESTMENT
터티벤처인베스트먼트
대표전화021579-8361
팩시밀리021579-8364

PROJECT OFFICE

ATEC(주)에이텍종합건축사사무소
ARCHITECTS & ASSOCIATES
대표전화0213462-6366
팩시밀리0213462-6368

DRAWING TITLE

지하1층 자동화재탐지설비 평면도

SCALE

A1 : 1/150
A3 : 1/300

DRAWN

남창모

CHECKED

DATE

2014. 03

CONSULTANT

DATE

2014. 03


DRAWING NO.

EF-007

PROJECT TITLE

성수동1가
지식산업센터
신축공사

NOTES

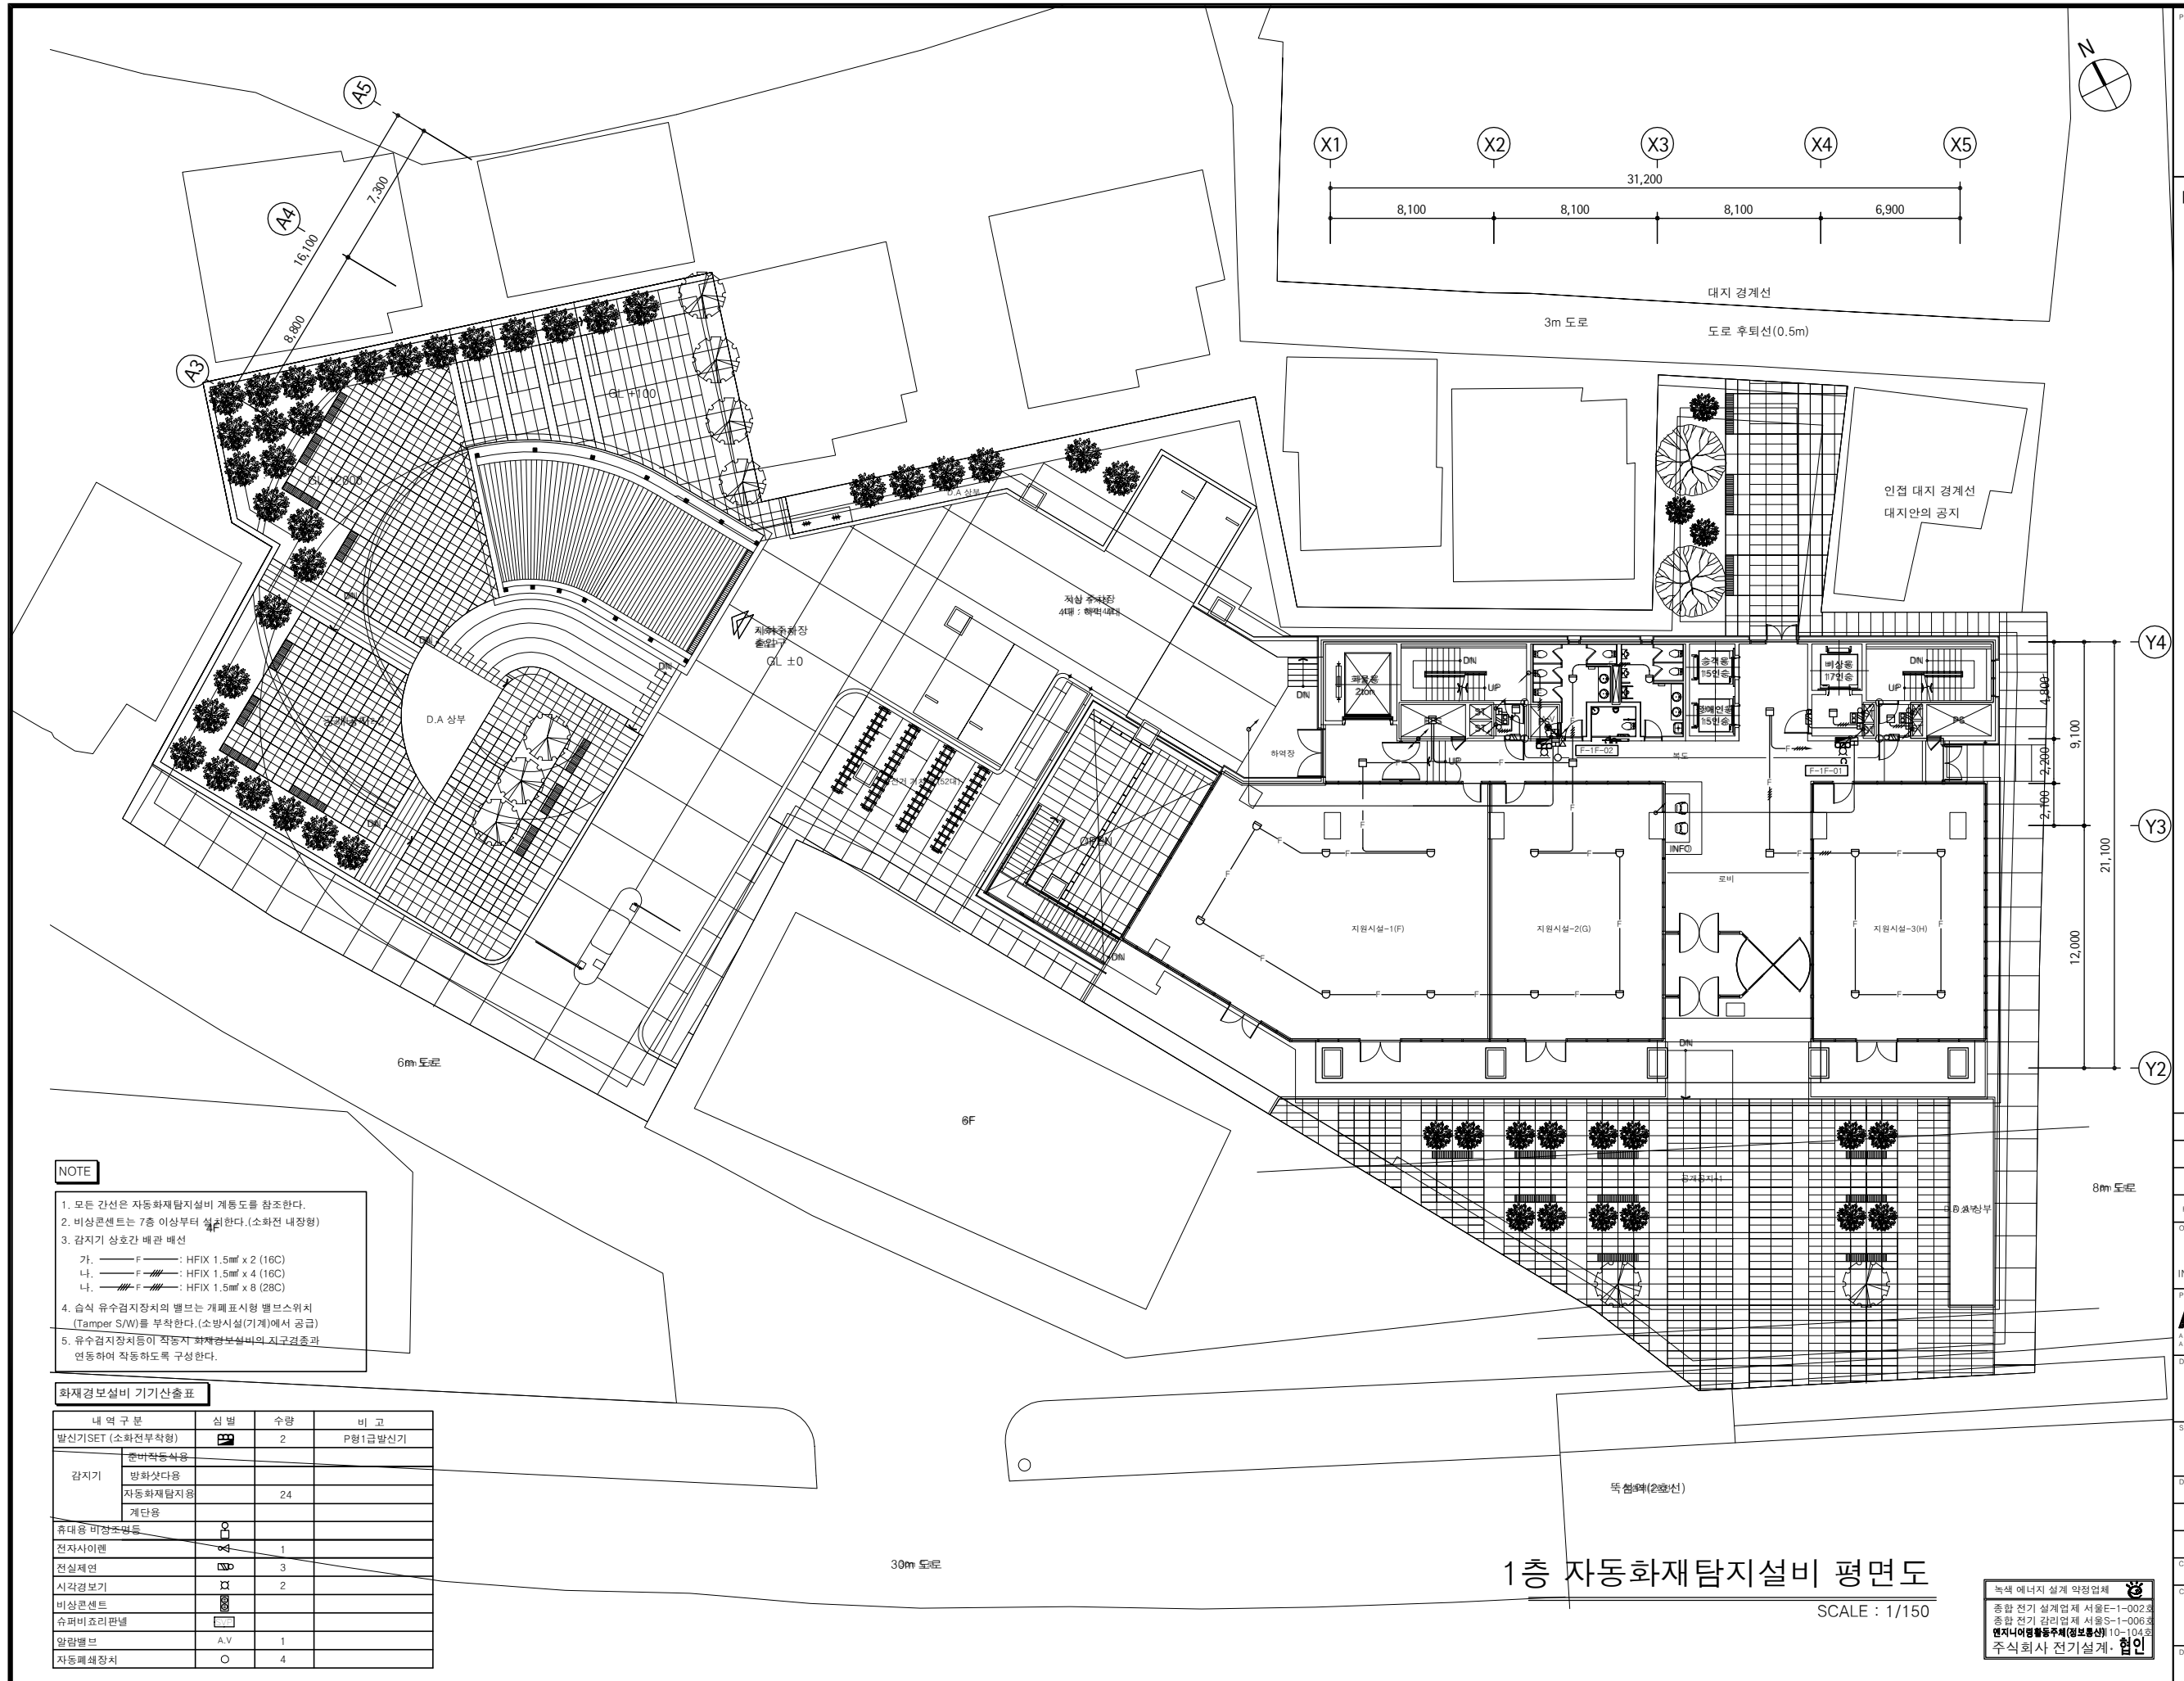

REVISION	DESCRIPTION	DATE

TT 티티벤처인베스트먼트
 VENTURE
 INVESTMENT
 대표전화(02)579-8361
 팩시밀리(02)579-8364
 PROJECT OFFICE
ATEC (주)에이텍종합건축사사무소
 ARCHITECTS & ASSOCIATES
 대표전화(02)3462-6366
 팩시밀리(02)3462-6320

1층 자동화재탐지설비 평면도

SCALE	APPROVED
A1 : 1/150	ARCHITECT 김 상 길
A3 : 1/300	
RAWN	DATE
남 창 모	2014. 03
CHECKED	DATE
	2014. 03

CONSULTANT	
DRAWING NO.	EF-008

PROJECT TITLE

[illegible]

- | | |
|--------------|------|
| 화재경보설비 기기산출표 | 3,4층 |
|--------------|------|

2층 자동화재탐지설비 평면도

녹색 에너지 설계 약정업체 
 종합 전기 설계업체 서울E-1-002호
 종합 전기 감리업체 서울S-1-006호
 연지니어링활동주체(정보통신) 10-104호
 주식회사 전기설계. 협인

녹색 에너지 설계 약정업체

종합 전기 설계업체 서울E-1-002호
종합 전기 감리업체 서울S-1-006호
엔지니어링활동주체(정보통신) 10-104호
주식회사 전기설계. 협의

형

DRAWING NO. FF-009

PROJECT TITLE

성수동1가
지식산업센터
신축공사

NOTES

REVISION DESCRIPTION DATE

ORDER ORGAN
INVESTMENT
TERI 벤처인베스트먼트
대표전화 021579-8361
팩시밀리 021579-8364

PROJECT OFFICE
ATEC(주)에이텍종합건축사사무소
ARCHITECTS & ASSOCIATES
대표전화 0213462-6366
팩시밀리 0213462-6368



DRAWING TITLE
3~6층 자동화재탐지설비 평면도

SCALE
A1 : 1/150
A3 : 1/300
DRAWN 남 창 모
DATE 2014. 03

CHECKED DATE 2014. 03

CONSULTANT

DRAWING NO. EF-010

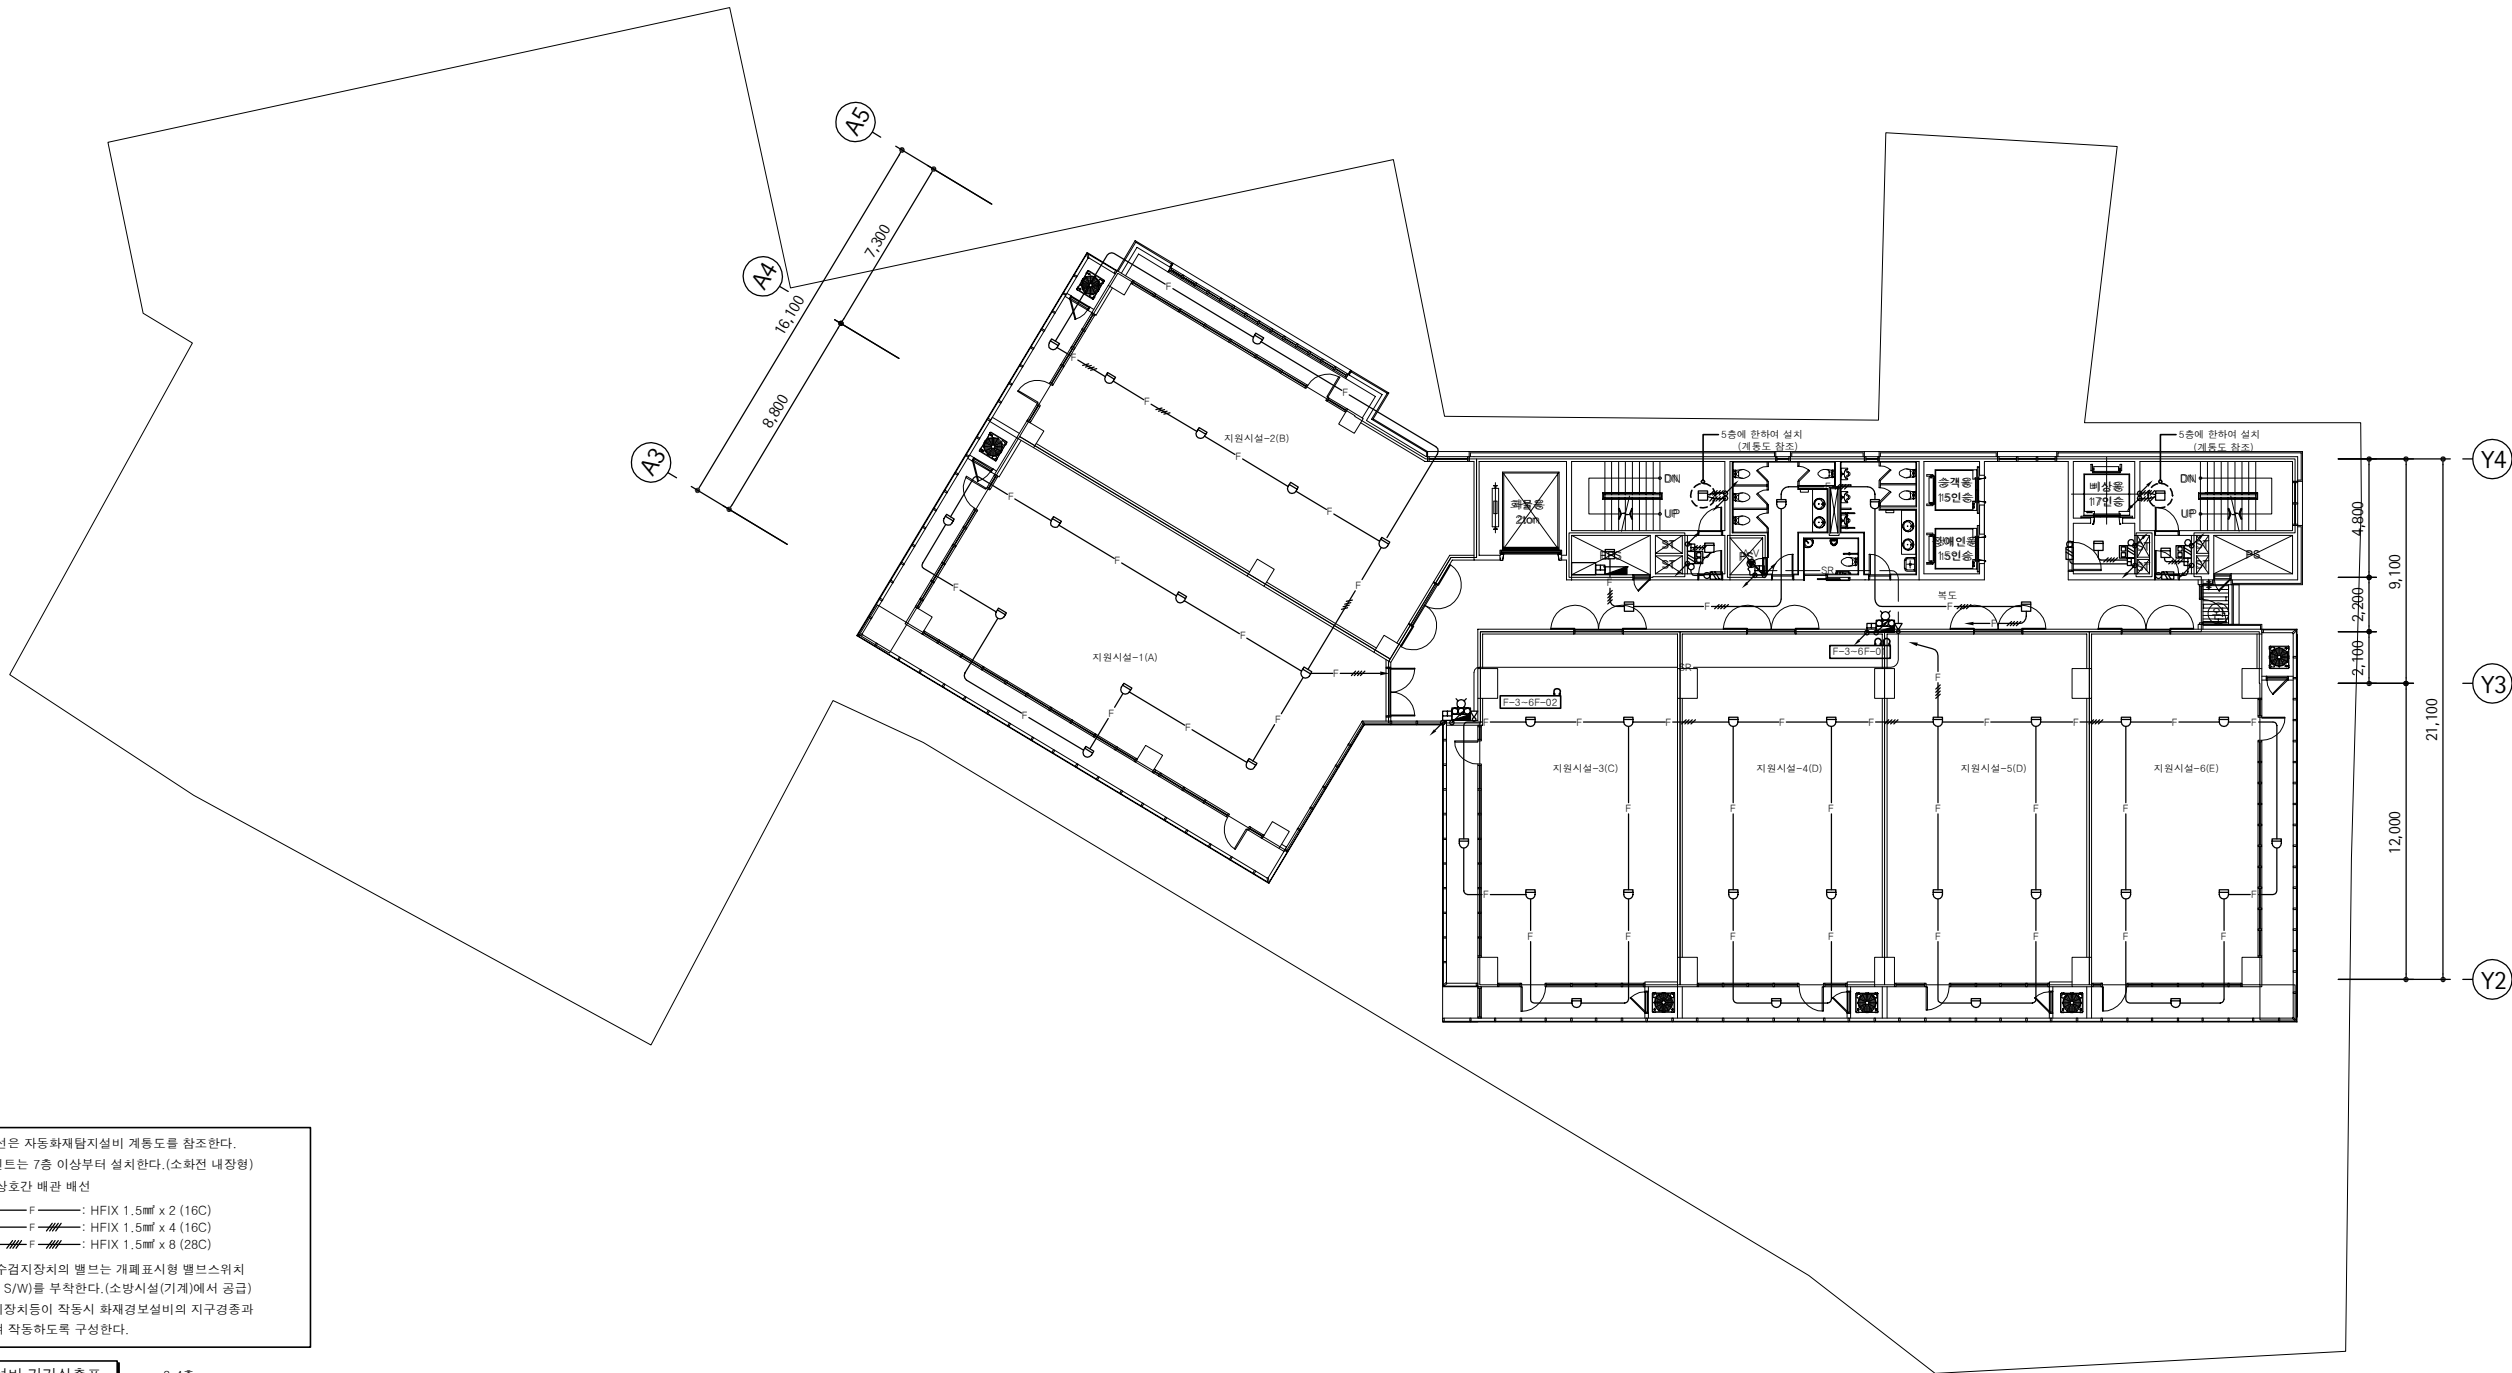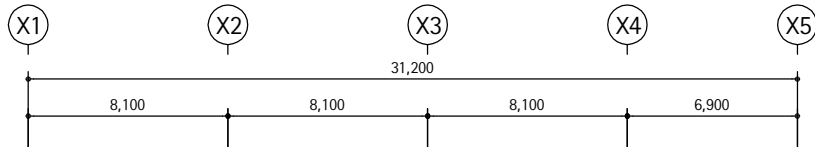

NOTE

- 모든 간선은 자동화재탐지설비 계통도를 참조한다.
- 비상콘센트는 7층 이상부터 설치한다. (소화전 내장형)
- 감지기 상호간 배관 배선
가. — F — : HFIX 1.5mm² x 2 (16C)
나. — F — : HFIX 1.5mm² x 4 (16C)
다. — F — : HFIX 1.5mm² x 8 (28C)
- 습식 유수검지장치와 밸브는 개폐표시형 밸브스위치 (Tamper S/W)를 부착한다. (소방시설(기계)에서 공급)
- 유수검지장치들이 작동시 화재경보설비의 지구경종과 연동하여 작동하도록 구성한다.

화재경보설비 기기산출표 3,4층

내역구분	설비명	수량	비고
발신기(SET (소화전부착형))		2	P형1급발신기
감지기	준비작동식용		
	방화샷다용		
	자동화재탐지용	44	
	계단용		
휴대용 비상조명등			
전자사이렌		2	
전실제연		3	
시각경보기		2	
비상콘센트			
슈퍼비요리판넬			
알람벨브	A.V	1	
자동폐쇄장치			

3,4층 자동화재탐지설비 평면도

SCALE : 1/150

녹색 에너지 설계 약정업체
종합 전기 설계업체 서울E-1-002호
종합 전기 감리업체 서울S-1-006호
연지니아엔지니어링(정보통신) 10-104호
주식회사 전기설계 협인



PROJECT TITLE

성수동1가
지식산업센터
신축공사

NOTES

REVISION	DESCRIPTION	DATE
ORDER ORGAN	INVESTMENT	PROJECT OFFICE
터티벤처인베스트먼트	대표전화021579-8361 팩시밀리021579-8364	ATEC(주)에이텍종합건축사사무소 ARCHITECTS & ASSOCIATES 대표전화0213462-6366 팩시밀리0213462-6368
DRAWING TITLE	7~14층 자동화재탐지설비 평면도	

SCALE	APPROVED
A1 : 1/150 A3 : 1/300	ARCHITECT 김 상 길
DRAWN 남 창 모	DATE 2014. 03
CHECKED	DATE 2014. 03
CONSULTANT	
DRAWING NO.	EF-011

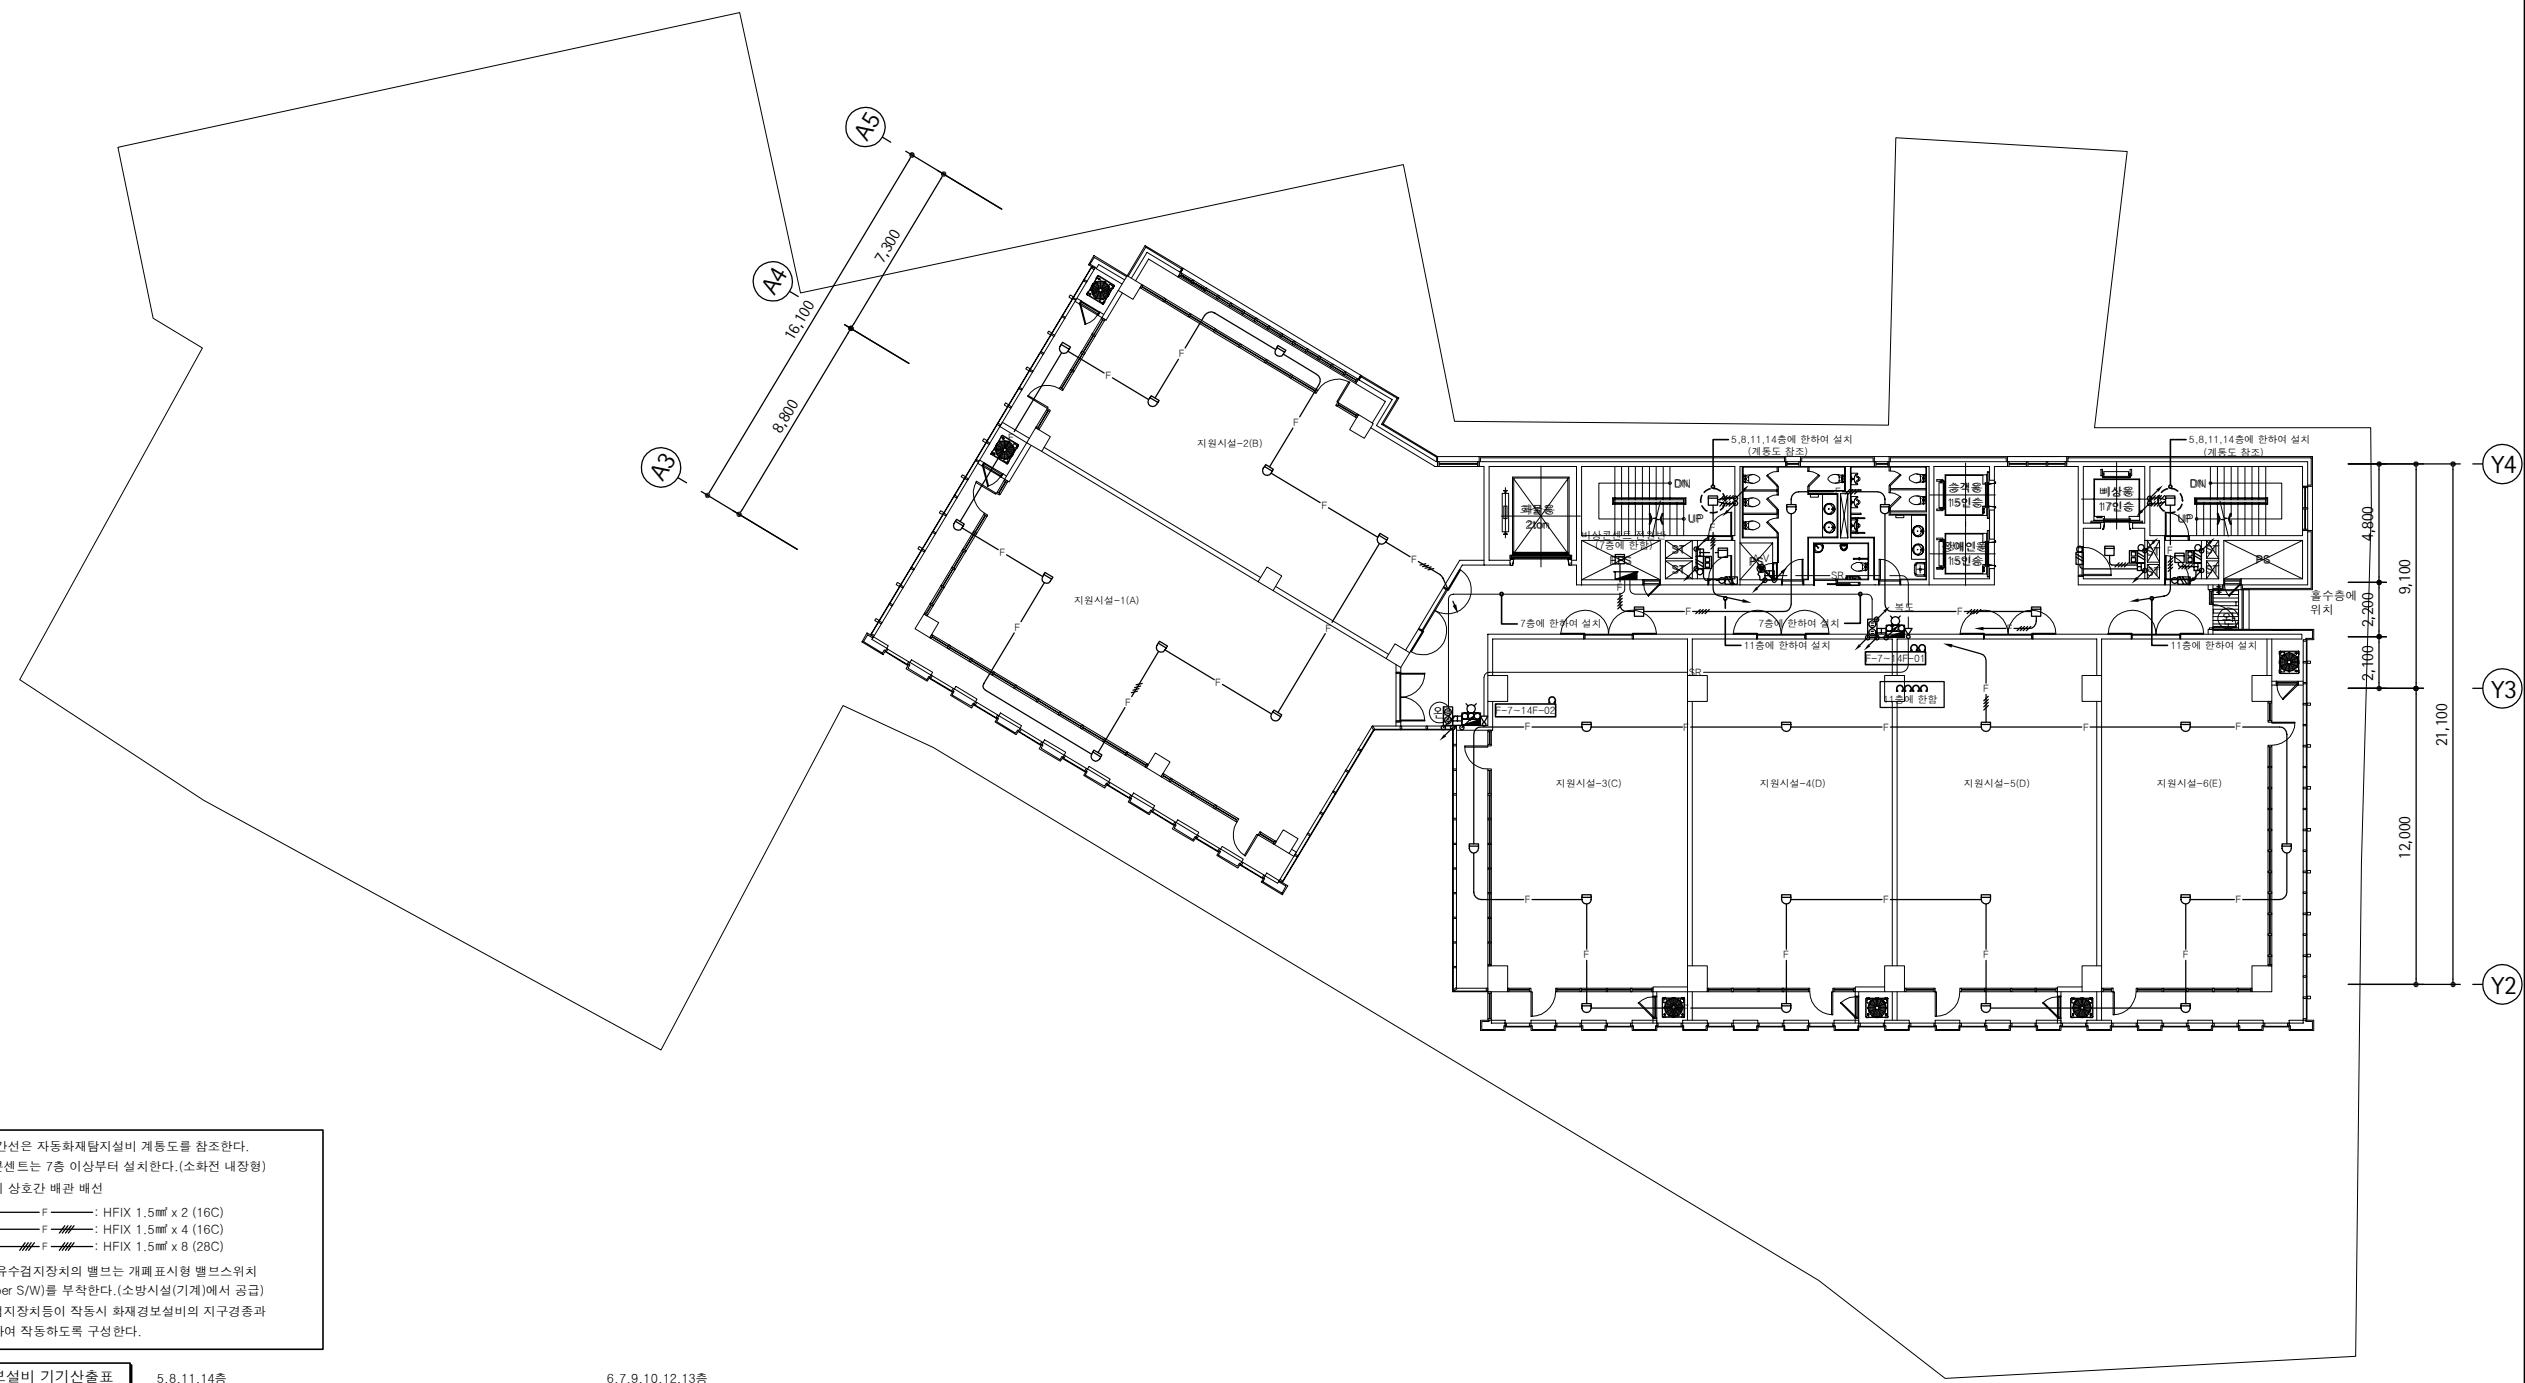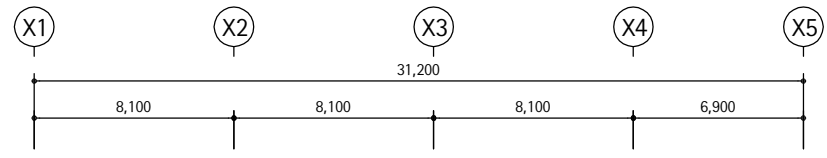

- NOTE
- 모든 간선은 자동화재탐지설비 계통도를 참조한다.
 - 비상콘센트는 7층 이상부터 설치한다.(소화전 내장형)
 - 감지기 상호간 배관 배선
가. — F — : HFIX 1.5mm x 2 (16C)
나. — F — : HFIX 1.5mm x 4 (16C)
나. — F — : HFIX 1.5mm x 8 (28C)
 - 습식 유수검지장치와 벨르는 개폐표시형 벨브스위치 (Tamper S/W)를 부착한다.(소방시설(기계)에서 공급)
 - 유수검지장치들이 작동시 화재경보설비의 지구경종과 연동하여 작동하도록 구성한다.

화재경보설비 기기산출표		5, 8, 11, 14층	6, 7, 9, 10, 12, 13층
내역구분	설비	수량	비고
발신기SET (소화전부착형)		2	P형1급발신기
감지기	준비작동식용		
	방화샷다용		
	자동화재탐지용	32	
	계단용	2	
휴대용 비상조명등			
전자사이렌		2	
전실제연		3	
시각경보기		2	
비상콘센트		2	8, 11, 14층만설치
슈퍼비조리판넬			
알람벨브	A.V	1	
자동폐쇄장치			

내역구분	설비	수량	비고
발신기SET (소화전부착형)		2	P형1급발신기
감지기	준비작동식용		
	방화샷다용		
	자동화재탐지용	32	
	계단용		
휴대용 비상조명등			
전자사이렌		2	
전실제연		3	
시각경보기		2	
비상콘센트		2	7, 9, 10, 12, 13층만설치
슈퍼비조리판넬			
알람벨브	A.V	1	
자동폐쇄장치			

5~14층 자동화재탐지설비 평면도


SCALE : 1/150

녹색 에너지 설계 약정업체
종합 전기 설계업체 서울E-1-0023
종합 전기 감리업체 서울S-1-0063
연지니아평화동주세(정보통신) 10-104호
주식회사 전기설계. 협인

PROJECT TITLE

성수동1가
지식산업센터
신축공사

NOTES

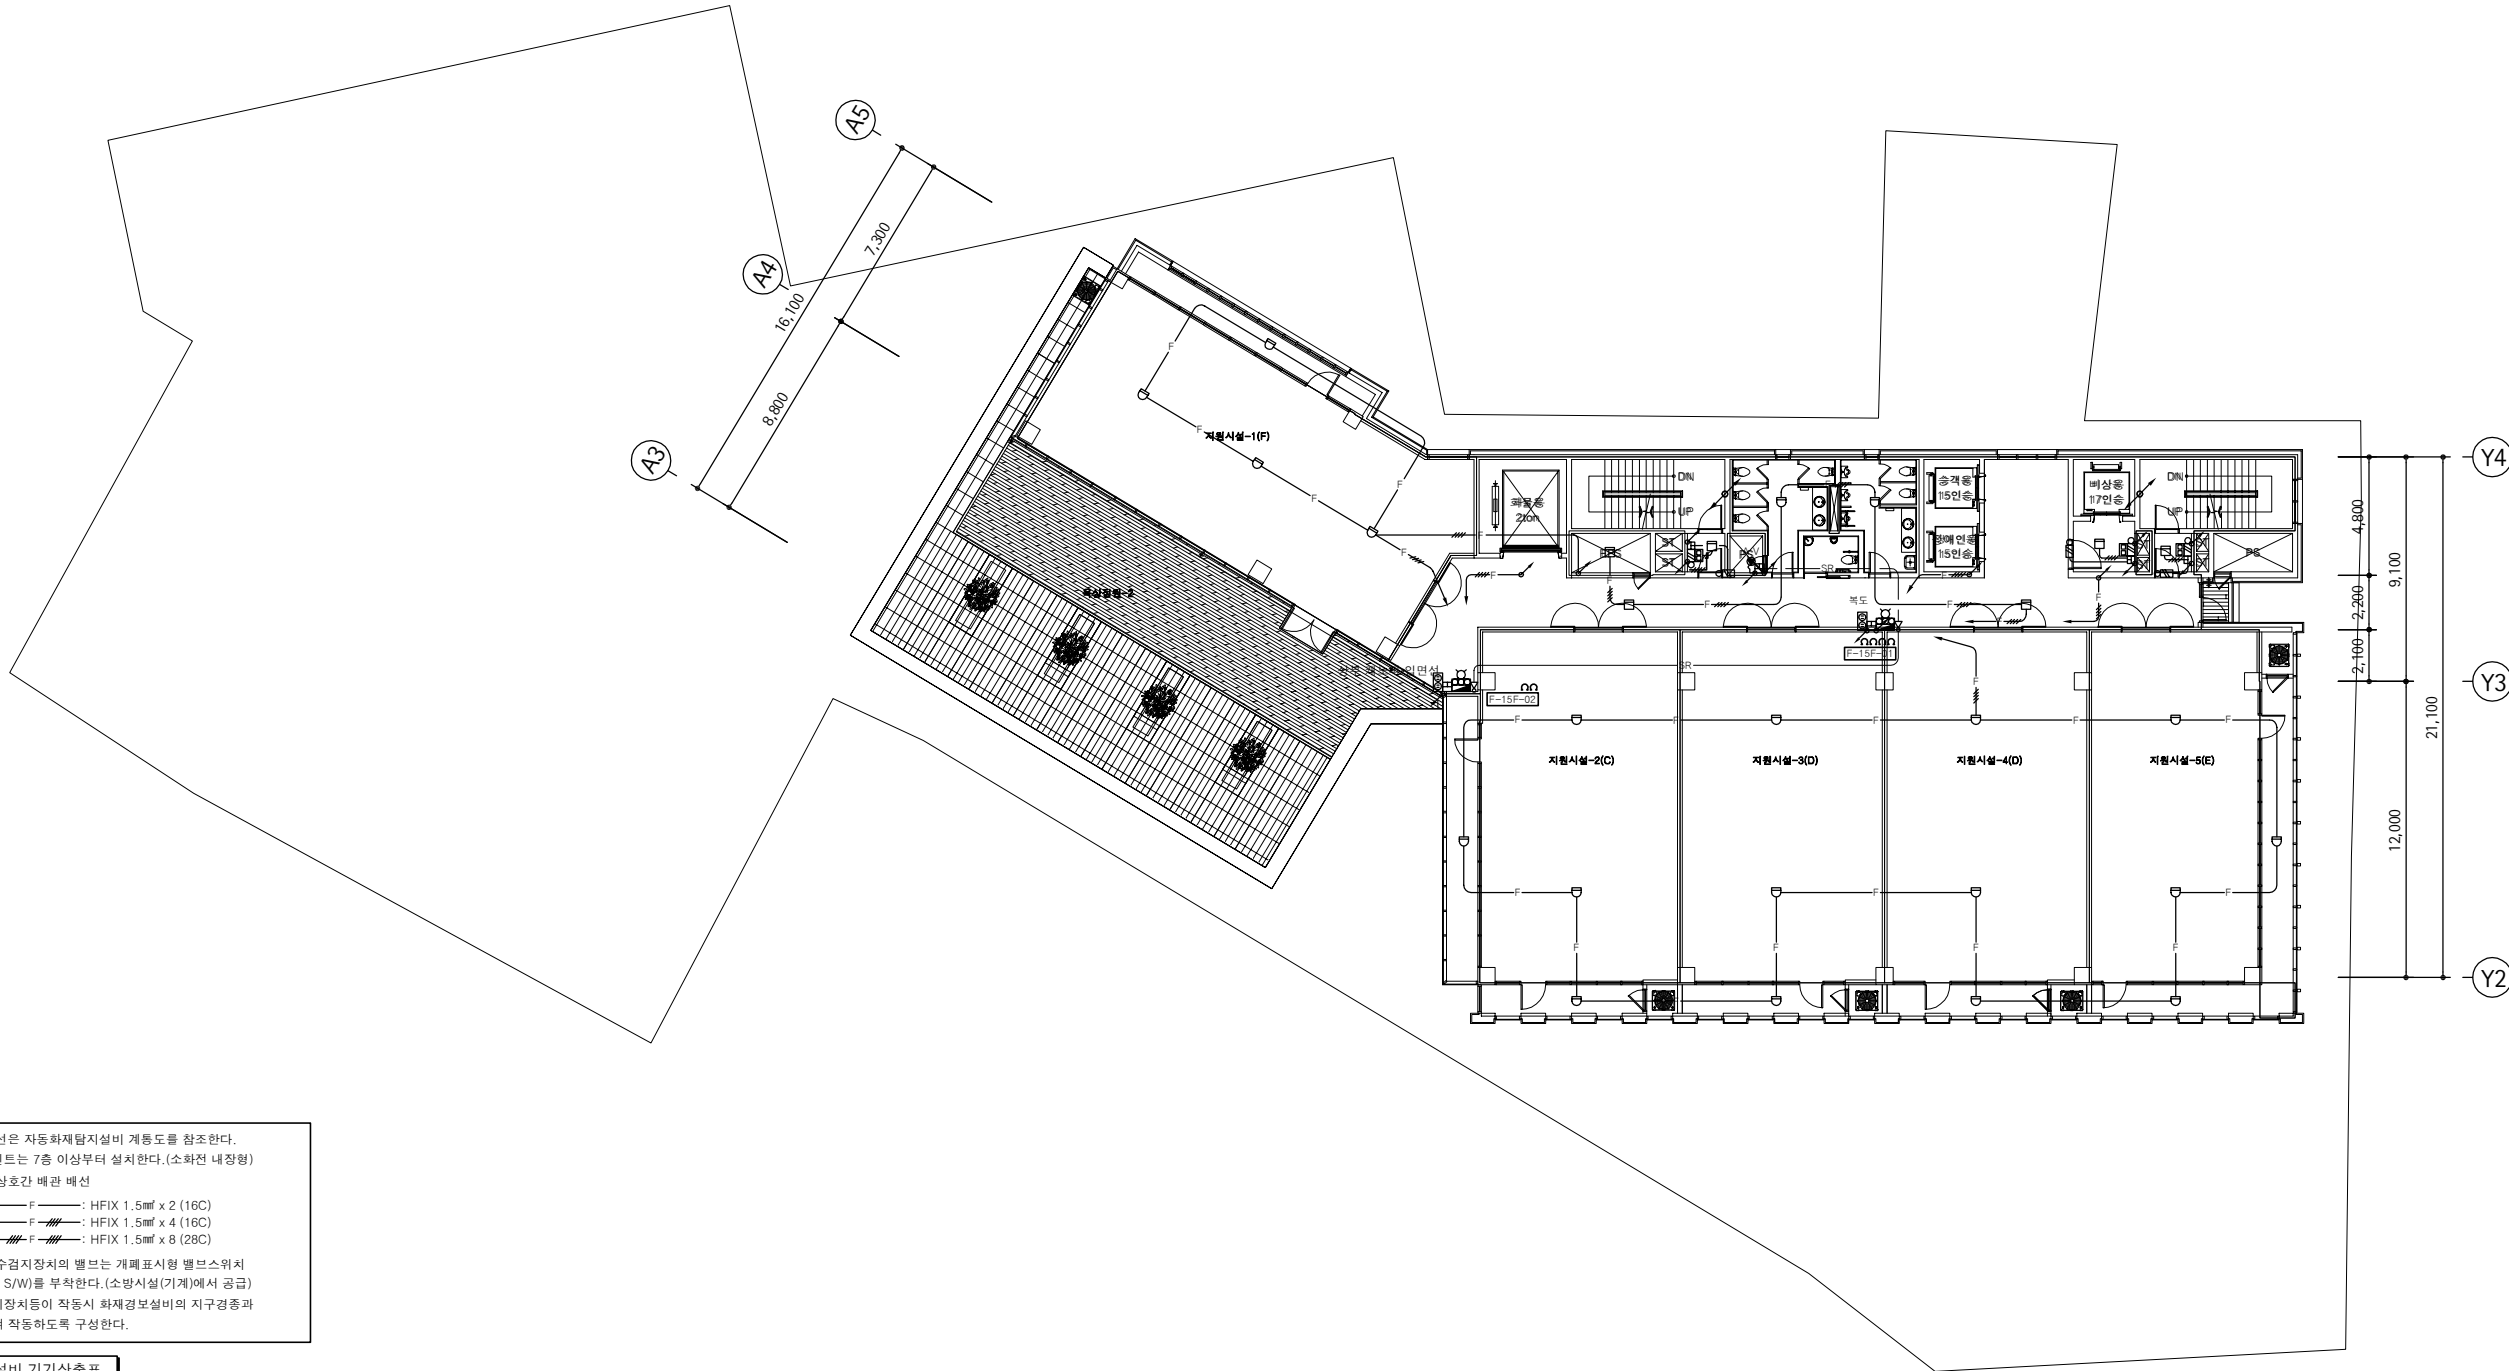

- NOTE
- 모든 간선은 자동화재탐지설비 계통도를 참조한다.
 - 비상콘센트는 7층 이상부터 설치한다.(소화전 내장형)
 - 감지기 상호간 배관 배선
가. — F — : HFIX 1.5mm² x 2 (16C)
나. — F — : HFIX 1.5mm² x 4 (16C)
다. — F — : HFIX 1.5mm² x 8 (28C)
 - 습식 유수검지장치와 벨브는 개폐표시형 벨브스위치 (Tamper S/W)를 부착한다.(소방시설(기계)에서 공급)
 - 유수검지장치들이 작동시 화재경보설비의 지구경종과 연동하여 작동하도록 구성한다.

화재경보설비 기기산출표

내역구분	심벌	수량	비고
발신기SET (소화전부착형)		2	P형1급발신기
감지기	준비작동식음		
	방화샷다음		
	자동화재탐지음	26	
	계단음		
휴대용 비상조명등			
전자사이렌		2	
전실제연		3	
시각경보기		2	
비상콘센트		2	
슈퍼비요리판넬			
알람벨브	A.V	1	
자동폐쇄장치			

15층 자동화재탐지설비 평면도

SCALE : 1/150

녹색 에너지 설계 약정업체
종합 전기 설계업체 서울E-1-002호
종합 전기 관리업체 서울S-1-006호
연지니아엔지니어링(주)(정보통신) 10-104호
주식회사 전기설계. 협인

REVISION	DESCRIPTION	DATE
ORDER ORGAN	티티벤처인베스트먼트	
INVESTMENT	대표전화021579-8361 팩시밀리021579-8364	
PROJECT OFFICE	ATEC(주)에이텍종합건축사사무소	
ARCHITECTS & ASSOCIATES	대표전화021462-6366 팩시밀리021462-6368	
DRAWING TITLE	15층 자동화재탐지설비 평면도	
SCALE	A1 : 1/150 A3 : 1/300	APPROVED ARCHITECT 김 상 길
DRAWN	남 창 모	DATE 2014. 03
CHECKED		DATE 2014. 03
CONSULTANT		
DRAWING NO.	EF-012	

PROJECT TITLE

성수동1가
지식산업센터
신축공사

NOTES

REVISION DESCRIPTION DATE

ORDER ORGAN

INVESTMENT T 터티벤처인베스트먼트
대표전화021579-8361
팩시밀리021579-8364

PROJECT OFFICE

ATEC(주)에이텍종합건축사사무소
ARCHITECTS & ASSOCIATES
대표전화0213462-6366
팩시밀리0213462-6368

DRAWING TITLE

옥탑층 자동화재탐지설비 평면도

SCALE A1 : 1/150 A3 : 1/300



APPROVED ARCHITECT 김 상 길

DRAWN 남 창 모 DATE 2014. 03

CHECKED DATE 2014. 03

CONSULTANT

DRAWING NO. EF-013

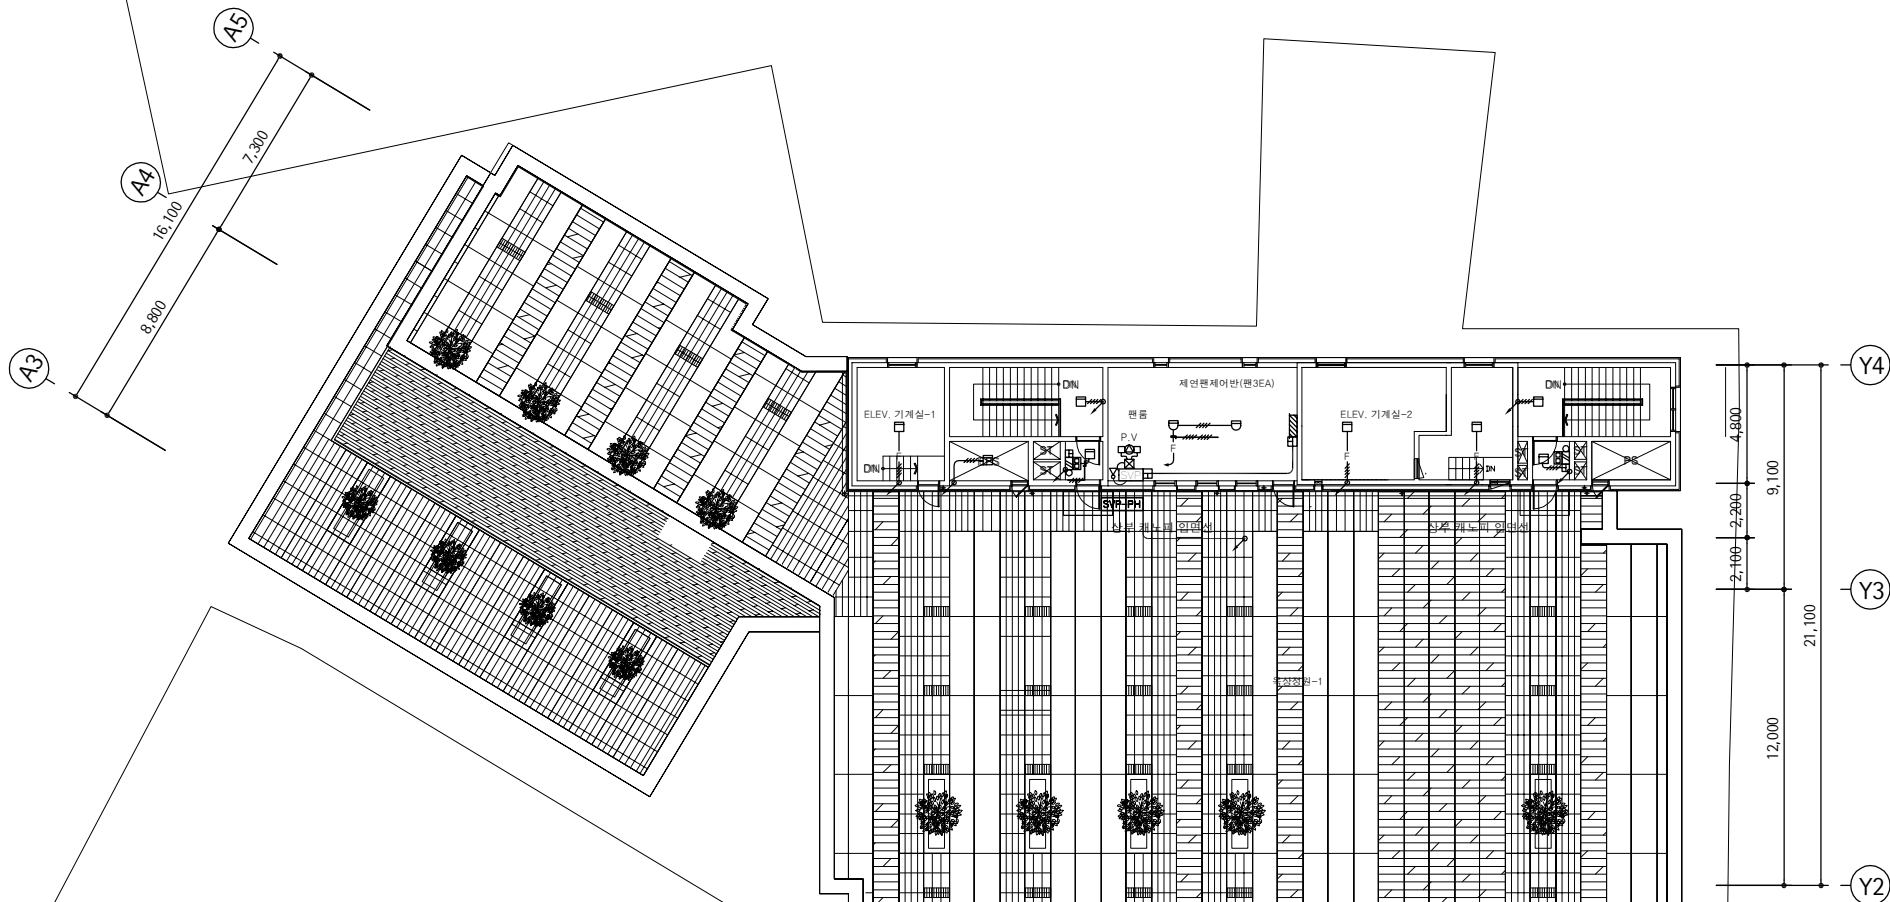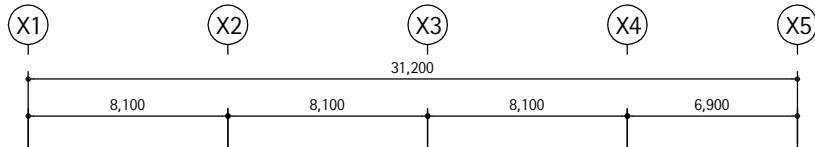

NOTE

- 모든 간선은 자동화재탐지설비 계통도를 참조한다.
- 비상콘센트는 7층 이상부터 설치한다.(소화전 내장형)
- 감지기 상호간 배관 배선
가. — F — : HFIX 1.5mm² x 2 (16C)
나. — F — : HFIX 1.5mm² x 4 (16C)
나. — F — : HFIX 1.5mm² x 8 (28C)
- 습식 유수검지장치와 별브는 개폐표시형 별브스위치 (Tamper S/W)를 부착한다.(소방시설(기계)에서 공급)
- 유수검지장치들이 작동시 화재경보설비의 지구경종과 연동하여 작동하도록 구성한다.

화재경보설비 기기산출표

내역구분	신발	수량	비고
발신기SET (소화전부착형)			P형1급발신기
감지기	준비작동식용	2	
	방화샷다용		
	자동화재탐지용	6	
	계단용	2	
휴대용 비상조명등			
전자사이렌		1	
전실제연			
시각경보기			
비상콘센트			
슈퍼비요리판넬		1	
알람벨브	A.V		
자동폐쇄장치	O		

옥탑층 자동화재탐지설비 평면도


SCALE : 1/150

녹색 에너지 설계 약정업체
종합 전기 설계업체 서울E-1-0023
종합 전기 감리업체 서울S-1-0063
연지니아엔지니어링주식(정보통신) 10-104호
주식회사 전기설계. 협인

PROJECT TITLE

성수동1가
지식산업센터
신축공사

NOTES

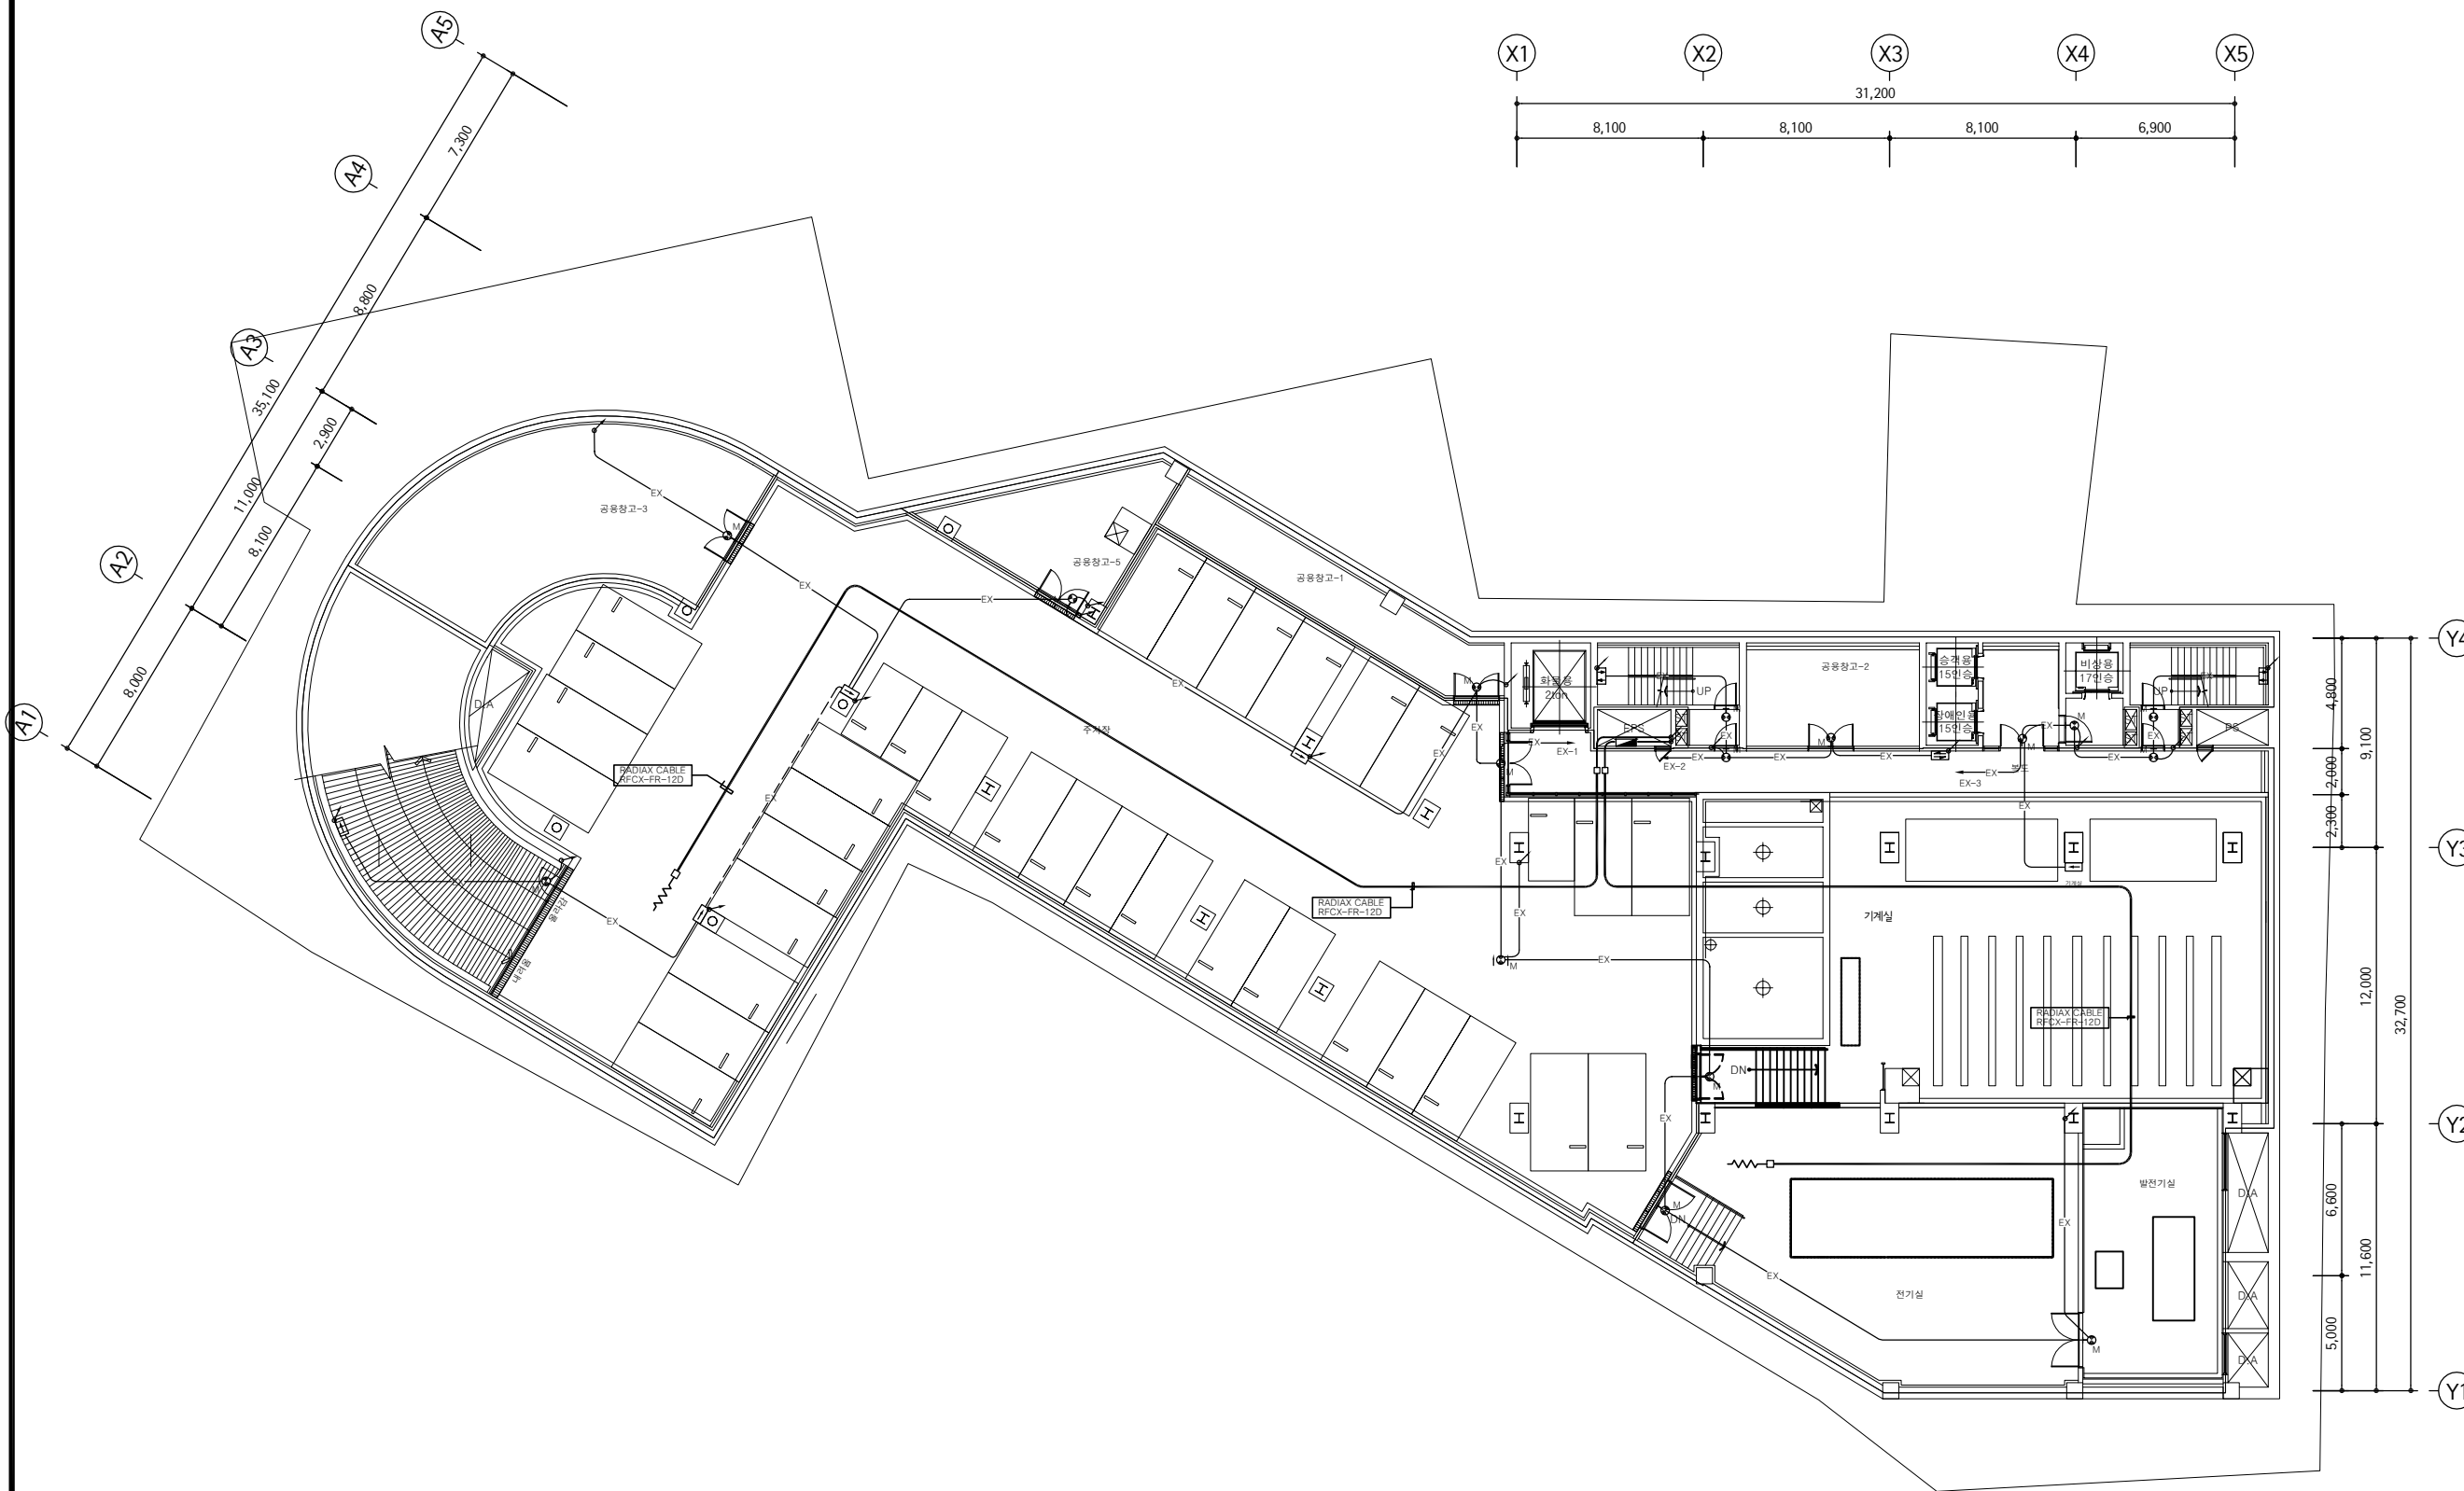

유도등설비 기가산출표

	종류	타입	규격	방향	수량
유도등	피난구	벽부형	중형		15
	피난구	천정형 앞면	중형	좌	1
	피난구	천정형 단면	중형		1
	복도등로	벽부형		양방	1
	기실등로	벽부형	중형	좌,우	3,2
	계단	벽부형		상,하	2

지하 4층 유도등 및 무선통신 보조설비 평면도

SCALE:1/150

녹색 에너지 설계 약정업체
종합 전기 설계업체 서울E-1-002호
종합 전기 강리업체 서울S-1-006호
연지니어링사무소(정보통신) 10-104호
주식회사 전기설계. 협인


REVISION	DESCRIPTION	DATE
ORDER ORGAN	티티벤처인베스트먼트	
INVESTMENT	대표전화(02)579-8361 팩시밀리(02)579-8364	
PROJECT OFFICE	ATEC(주)에이텍종합건축사사무소	
ARCHITECTS & ASSOCIATES	대표전화(02)3462-6366 팩시밀리(02)3462-6368	

DRAWING TITLE	
지하 4층 유도등 및 무선통신 보조설비 평면도	
SCALE	APPROVED
A1 : 1 / 150 A3 : 1 / 300	ARCHITECT 김 상 길
DRAWN 남 창 모	DATE 2014. 03
CHECKED	DATE 2014. 03
CONSULTANT	
DRAWING NO.	EF-014

PROJECT TITLE

성수동1가
지식산업센터
신축공사

NOTES

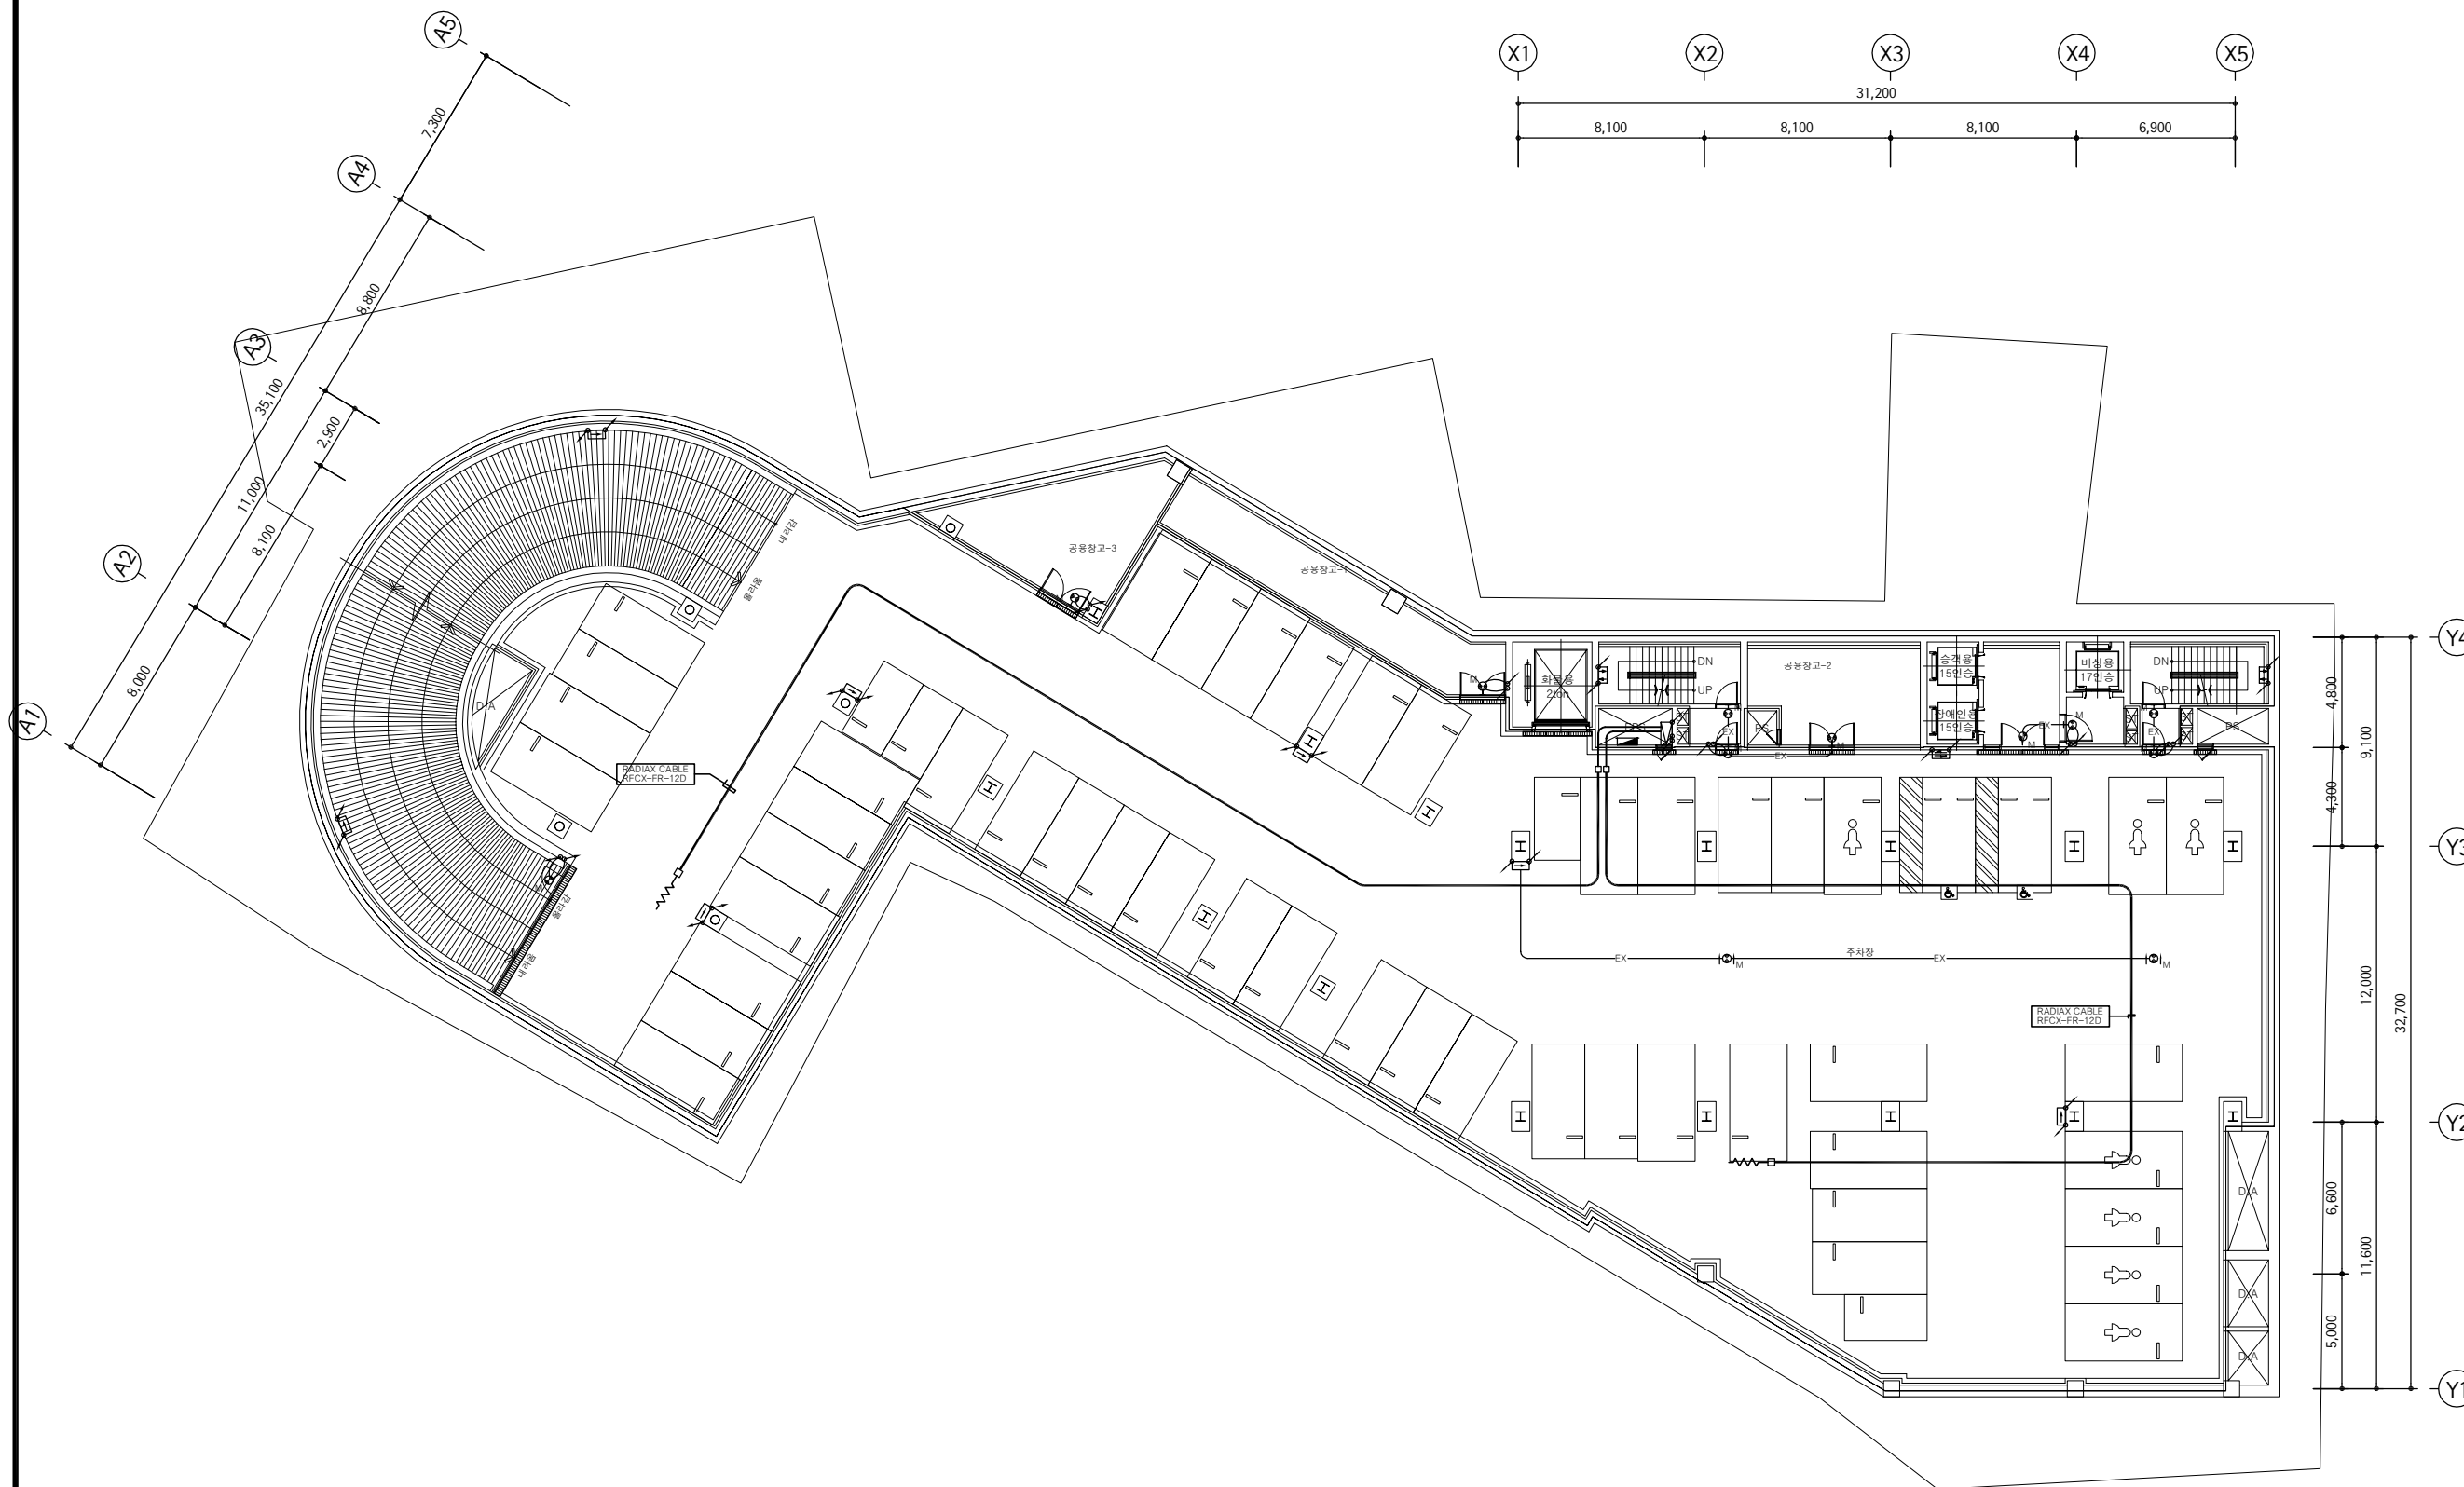

유도등설비 기기산출표

	종류	타입	규격	방향	수량
유도등	피난구	벽부형	중형		9
	피난구	천정형 양면	중형	좌	2
	피난구	천정형 단면	중형		1
	거실통로	벽부형		좌, 우, 양방	3,4,1
	계단	벽부형		상, 하	2

지하 3층 유도등 및 무선통신 보조설비 평면도

SCALE:1/150

녹색 에너지 설계 약정업체
종합 전기 설계업체 서울E-1-002호
종합 전기 감리업체 서울S-1-006호
연지니아종합건축(정보통선) 10-104호
주식회사 전기설계 협인


REVISION	DESCRIPTION	DATE
ORDER ORGAN	INVESTMENT	PROJECT OFFICE
티티벤처인베스트먼트		
대표전화(02)579-8361		
팩시밀리(02)579-8364		
ATEC(주)에이텍종합건축사사무소		
ARCHITECTS & ASSOCIATES		
대표전화(02)3462-6366		
팩시밀리(02)3462-6368		

DRAWING TITLE	
지하 3층 유도등 및 무선통신 보조설비 평면도	
SCALE	APPROVED
A1 : 1 / 150	ARCHITECT
A3 : 1 / 300	김 상 길
DRAWN	DATE
남 창 모	2014. 03
CHECKED	DATE
	2014. 03
CONSULTANT	
DRAWING NO.	EF-015

PROJECT TITLE

성수동1가
지식산업센터
신축공사

NOTES

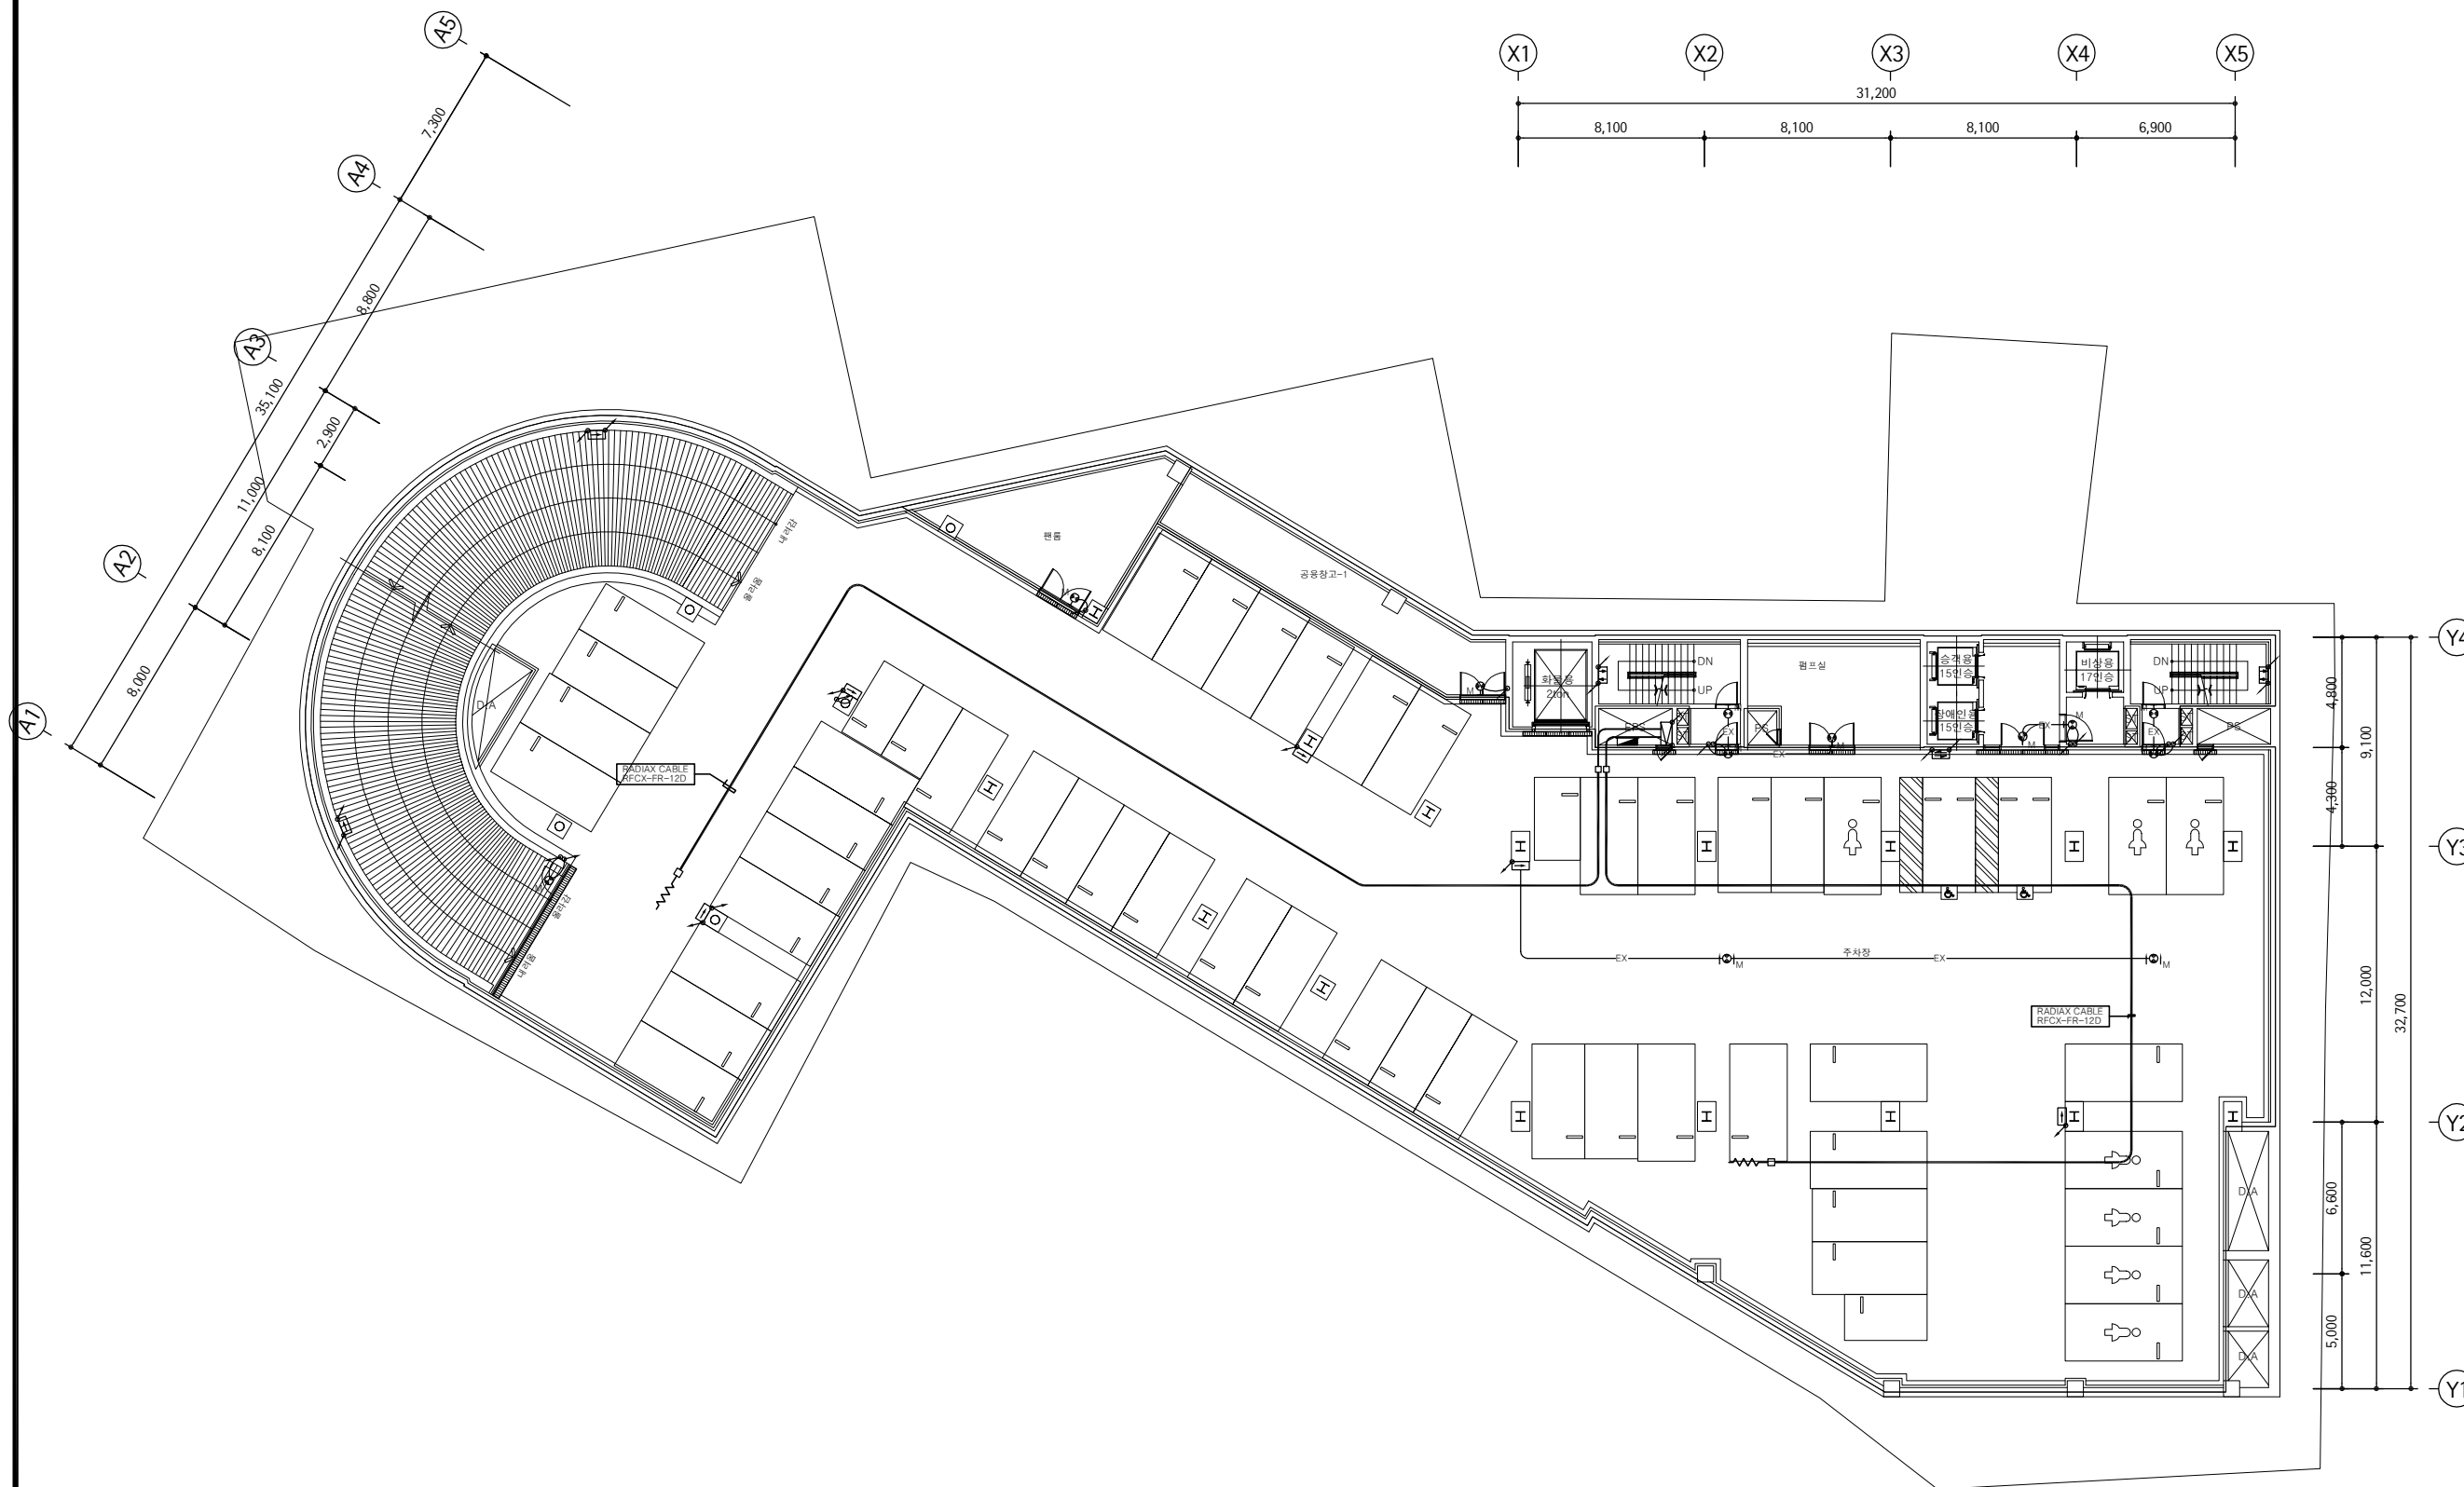

유도등설비 기기산출표

	종류	타입	규격	방향	수량
유도등	피난구	벽부형	중형		9
	피난구	천정형 양면	중형	좌	2
	피난구	천정형 단면	중형		1
	거실통로	벽부형		좌, 우, 양방	3,4,1
	계단	벽부형		상, 하	2

지하 2층 유도등 및 무선통신 보조설비 평면도


SCALE:1/150

녹색 에너지 설계 약정업체
종합 전기 설계업체 서울E-1-002호
종합 전기 강리업체 서울S-1-006호
연지니아종합건축(정보통신) 10-104호
주식회사 전기설계. 협인

REVISION	DESCRIPTION	DATE
ORDER ORGAN	INVESTMENT	PROJECT OFFICE
티티벤처인베스트먼트	대표전화(02)579-8361 팩시밀리(02)579-8364	ATEC(주)에이텍종합건축사사무소 ARCHITECTS & ASSOCIATES 대표전화(02)3462-6366 팩시밀리(02)3462-6366
DRAWING TITLE	지하 2층 유도등 및 무선통신 보조설비 평면도	
SCALE	A1 : 1 / 150 A3 : 1 / 300	APPROVED
ARCHITECT	김 상 길	
DRAWN	남 창 모	DATE 2014. 03
CHECKED		DATE 2014. 03
CONSULTANT		
DRAWING NO.	EF-016	

성수동1가
지식산업센터
신축공사

NOTES

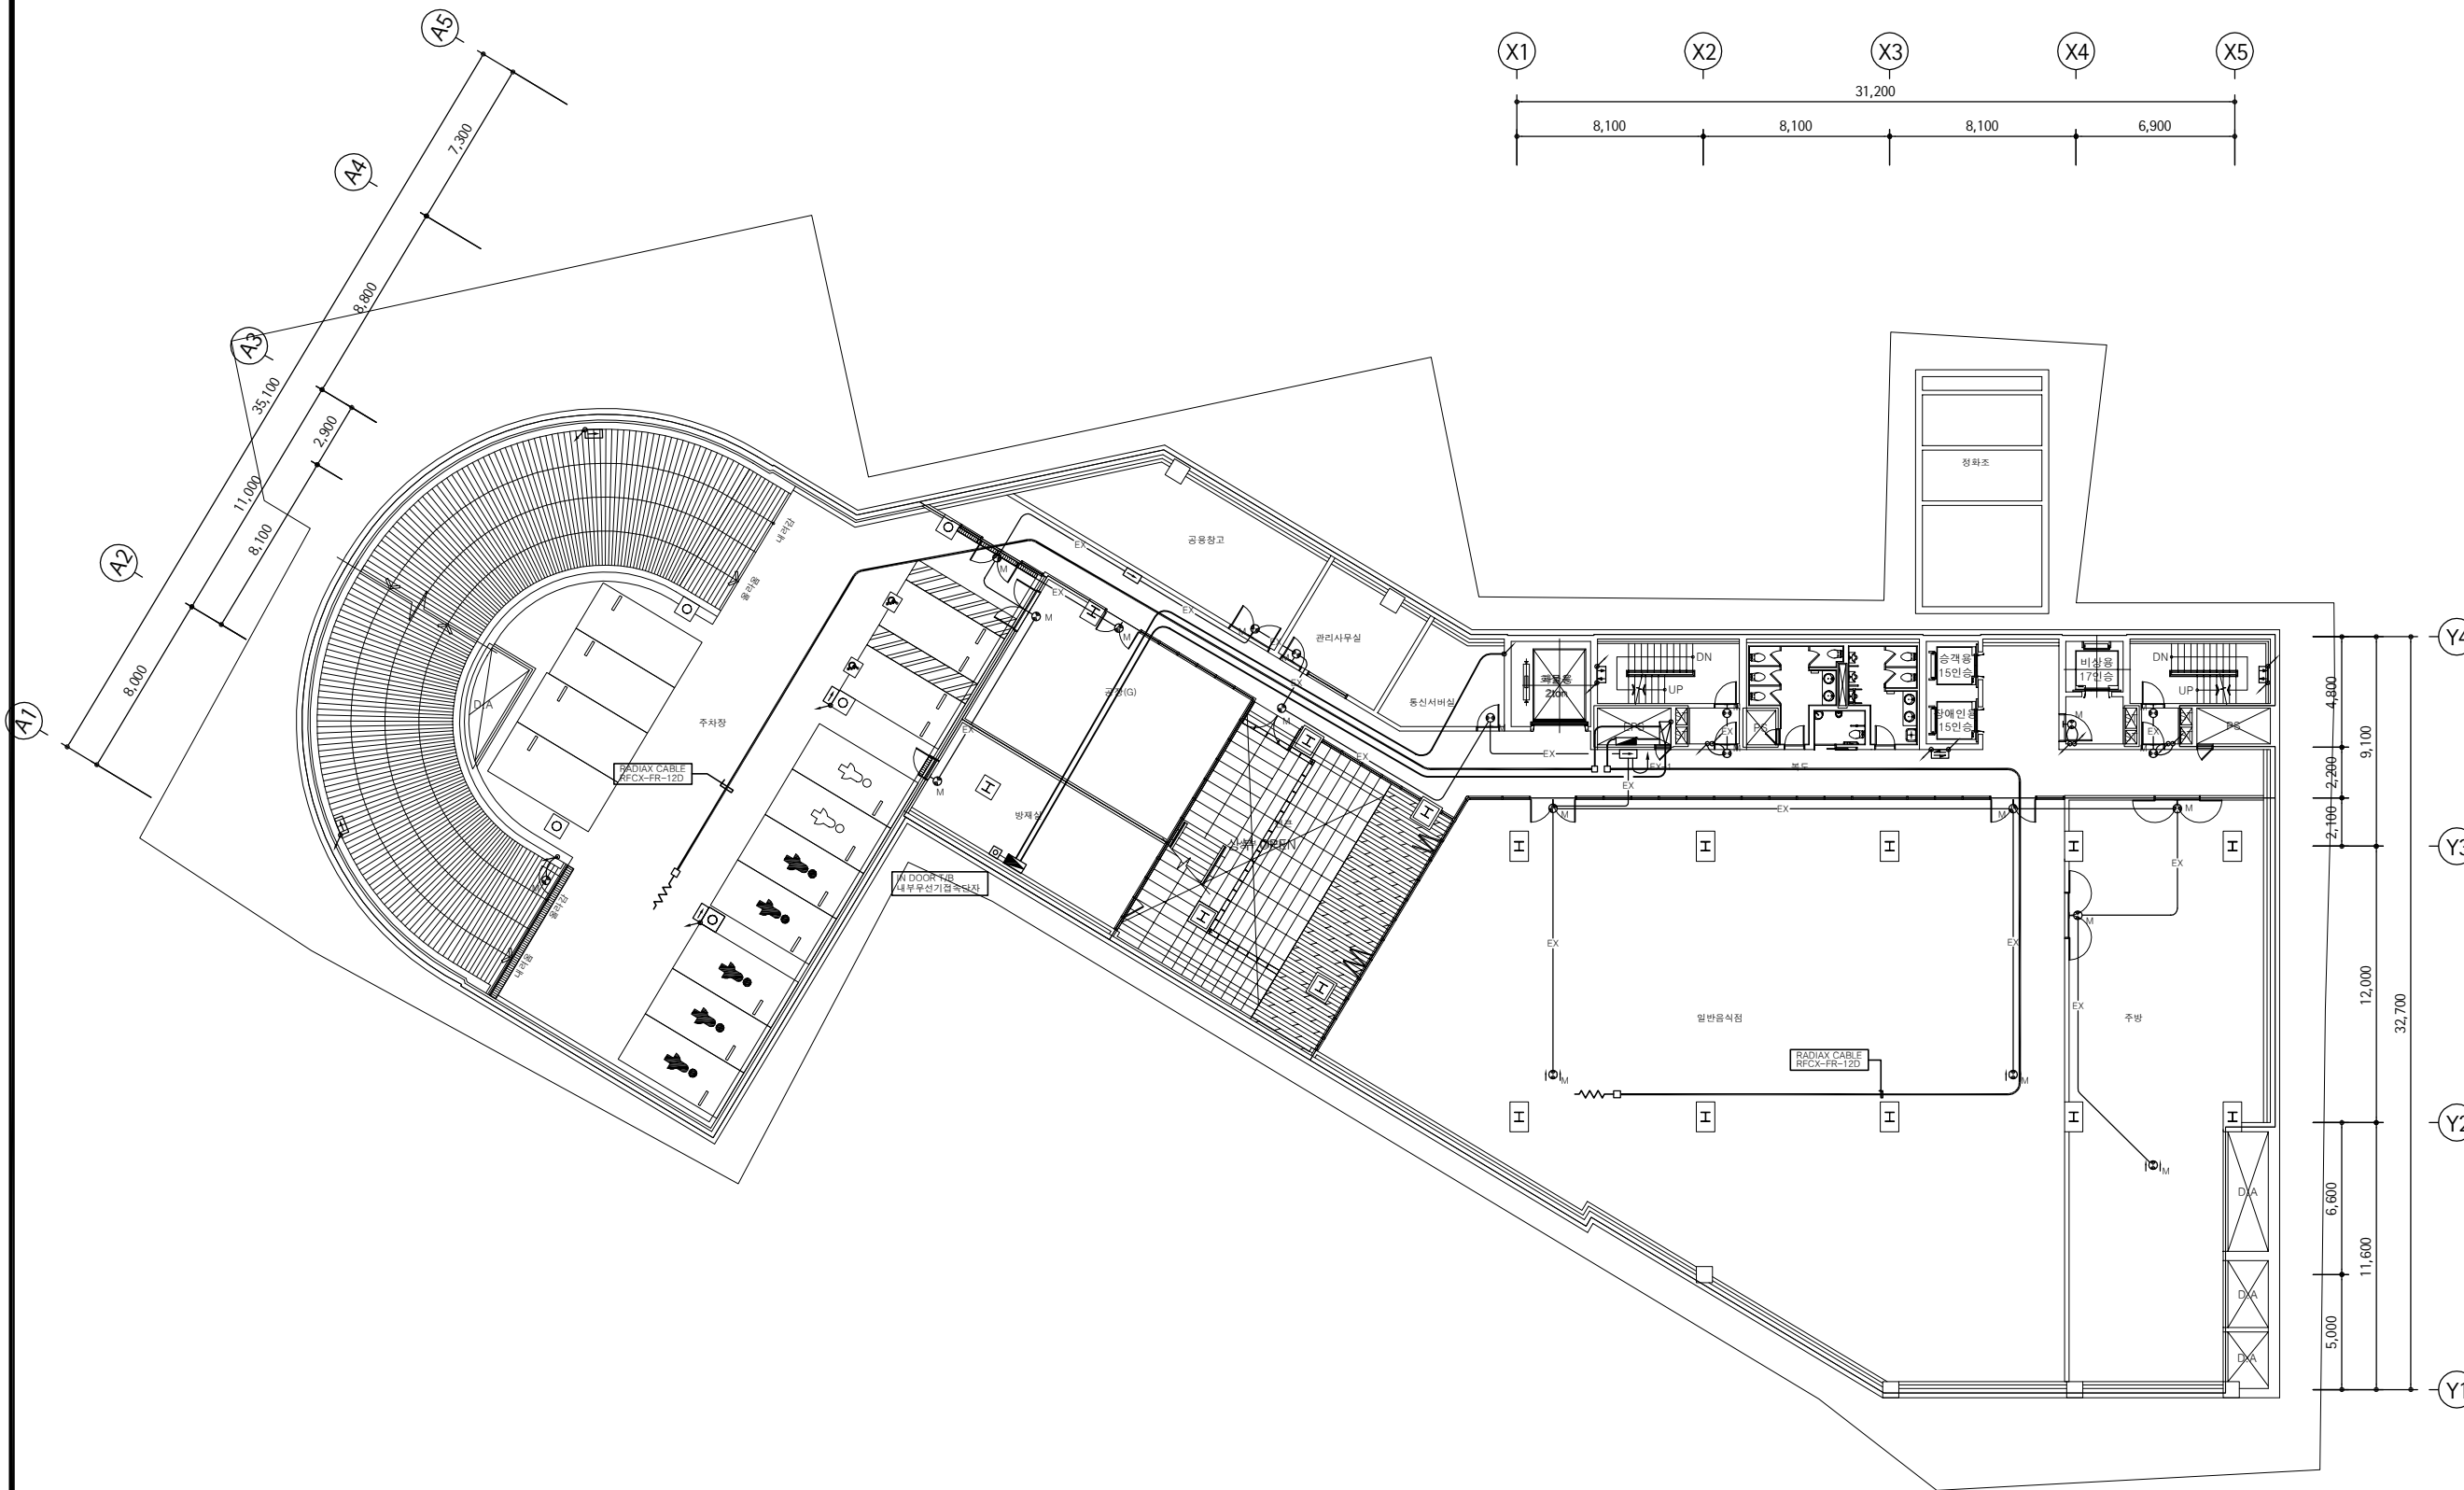

유도등설비 기기산출표

	종류	타입	규격	방향	수량
유도등	피난구	벽부형	중형		13
	피난구	천정형 앞면	중형	좌	3
	피난구	천정형 단면	중형		4
	복도등로	벽부형		우,양방	2,1
	거실등로	벽부형		좌,우	2,2
	계단	벽부형		상,하	6

지하 1층 유도등 및 무선통신 보조설비 평면도

SCALE:1/150


녹색 에너지 설계 약정업체
종합 전기 설계업체 서울E-1-002호
종합 전기 감리업체 서울S-1-006호
연지니아종합건축(정보통선) 10-104호
주식회사 전기설계 협인

REVISION	DESCRIPTION	DATE
ORDER ORGAN	티티벤처인베스트먼트	
INVESTMENT	대표전화(02)579-8361 팩시밀리(02)579-8364	
PROJECT OFFICE	ATEC(주)에이텍종합건축사사무소	
ARCHITECTS & ASSOCIATES	대표전화(02)3462-6366 팩시밀리(02)3462-6368	

지하 1층 유도등 및
무선통신 보조설비 평면도

SCALE	APPROVED
A1 : 1 / 150 A3 : 1 / 300	ARCHITECT 김 상 길
DRAWN 남 창 모	DATE 2014. 03
CHECKED	DATE 2014. 03
CONSULTANT	

DRAWING NO. EF-017

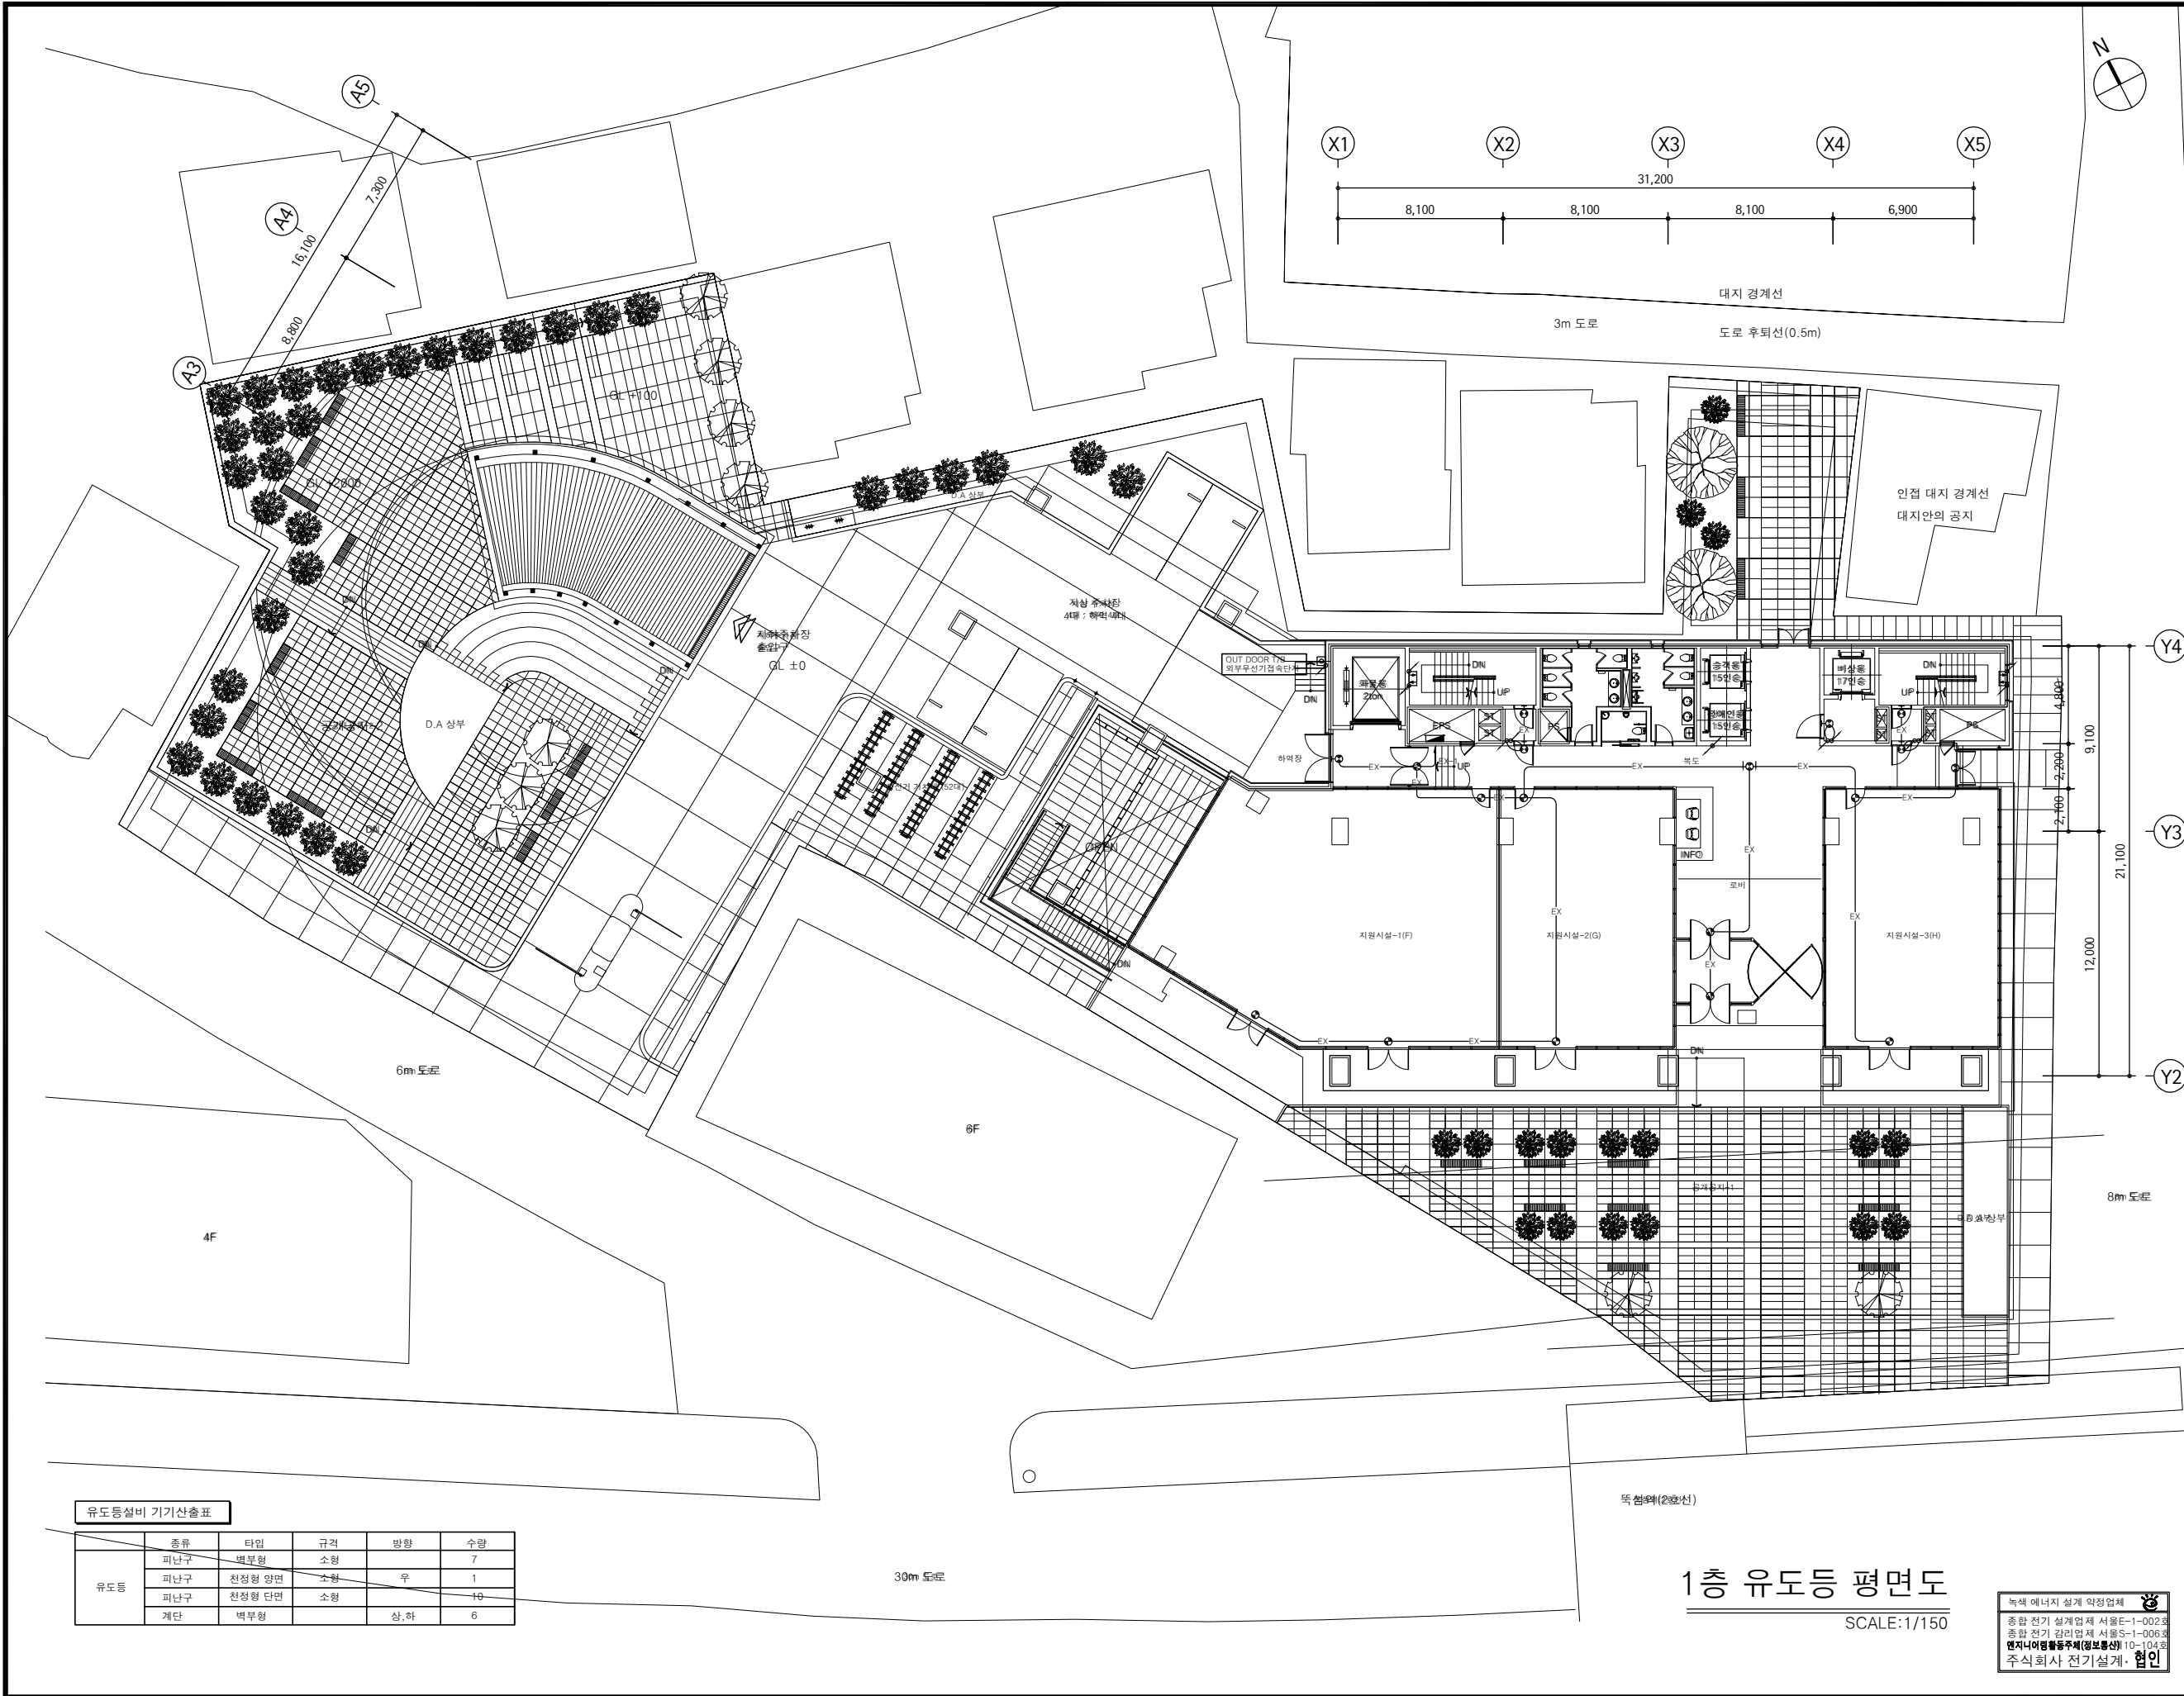

PROJECT TITLE

성수동1가
지식산업센터
신축공사

NOTES

REVISION	DESCRIPTION	DATE

ORDER ORGAN

INVESTMENT

PROJECT OFFICE

ARCHITECTS & ASSOCIATES

터티벤처인베스트먼트

대표전화(02)579-8361
팩시밀리(02)579-8364

ATEC(주)에이텍종합건축사사무소

대표전화(02)3462-6366
팩시밀리(02)3462-6368

DRAWING TITLE

1층 유도등 평면도

SCALE	A1 : 1 / 150 A3 : 1 / 300	APPROVED	ARCHITECT
DRAWN	남 창 모	DATE	2014. 03
CHECKED		DATE	2014. 03
CONSULTANT			

DRAWING NO.

EF-018

유도등설비 기기산출표

유도등	종류	타입	규격	방향	수량
	피난구	벽부형	소형		7
	피난구	천정형 양면	소형	우	1
	피난구	천정형 단면	소형		10
	계단	벽부형		상,하	6

1층 유도등 평면도

SCALE:1/150

녹색 에너지 설계 약정업체
종합 전기 설계업체 서울E-1-0023
종합 전기 감리업체 서울S-1-0063
연지니아종합건축(정보통선) 10-104호
주식회사 전기설계. 협인

PROJECT TITLE

성수동1가
지식산업센터
신축공사

NOTES



1. 배관배선 및 심법
- HFIX 6mm x 5 (28C)
 - P1 : HFIX 6mm x 2, E6mm (28C)

REVISION	DESCRIPTION	DATE
ORDER ORGAN	INVESTMENT	PROJECT OFFICE
터티벤처인베스트먼트	대표전화(02)579-8361 팩시밀리(02)579-8364	ATEC(주)에이텍종합건축사사무소 ARCHITECTS & ASSOCIATES 대표전화(02)3462-6366 팩시밀리(02)3462-6368

2층 유도등 및 배연창설비 평면도

SCALE	APPROVED
A1 : 1 / 150 A3 : 1 / 300	ARCHITECT 김 상 길
DRAWN 남 창 모	DATE 2014. 03
CHECKED	DATE 2014. 03
CONSULTANT	

DRAWING NO. EF-019

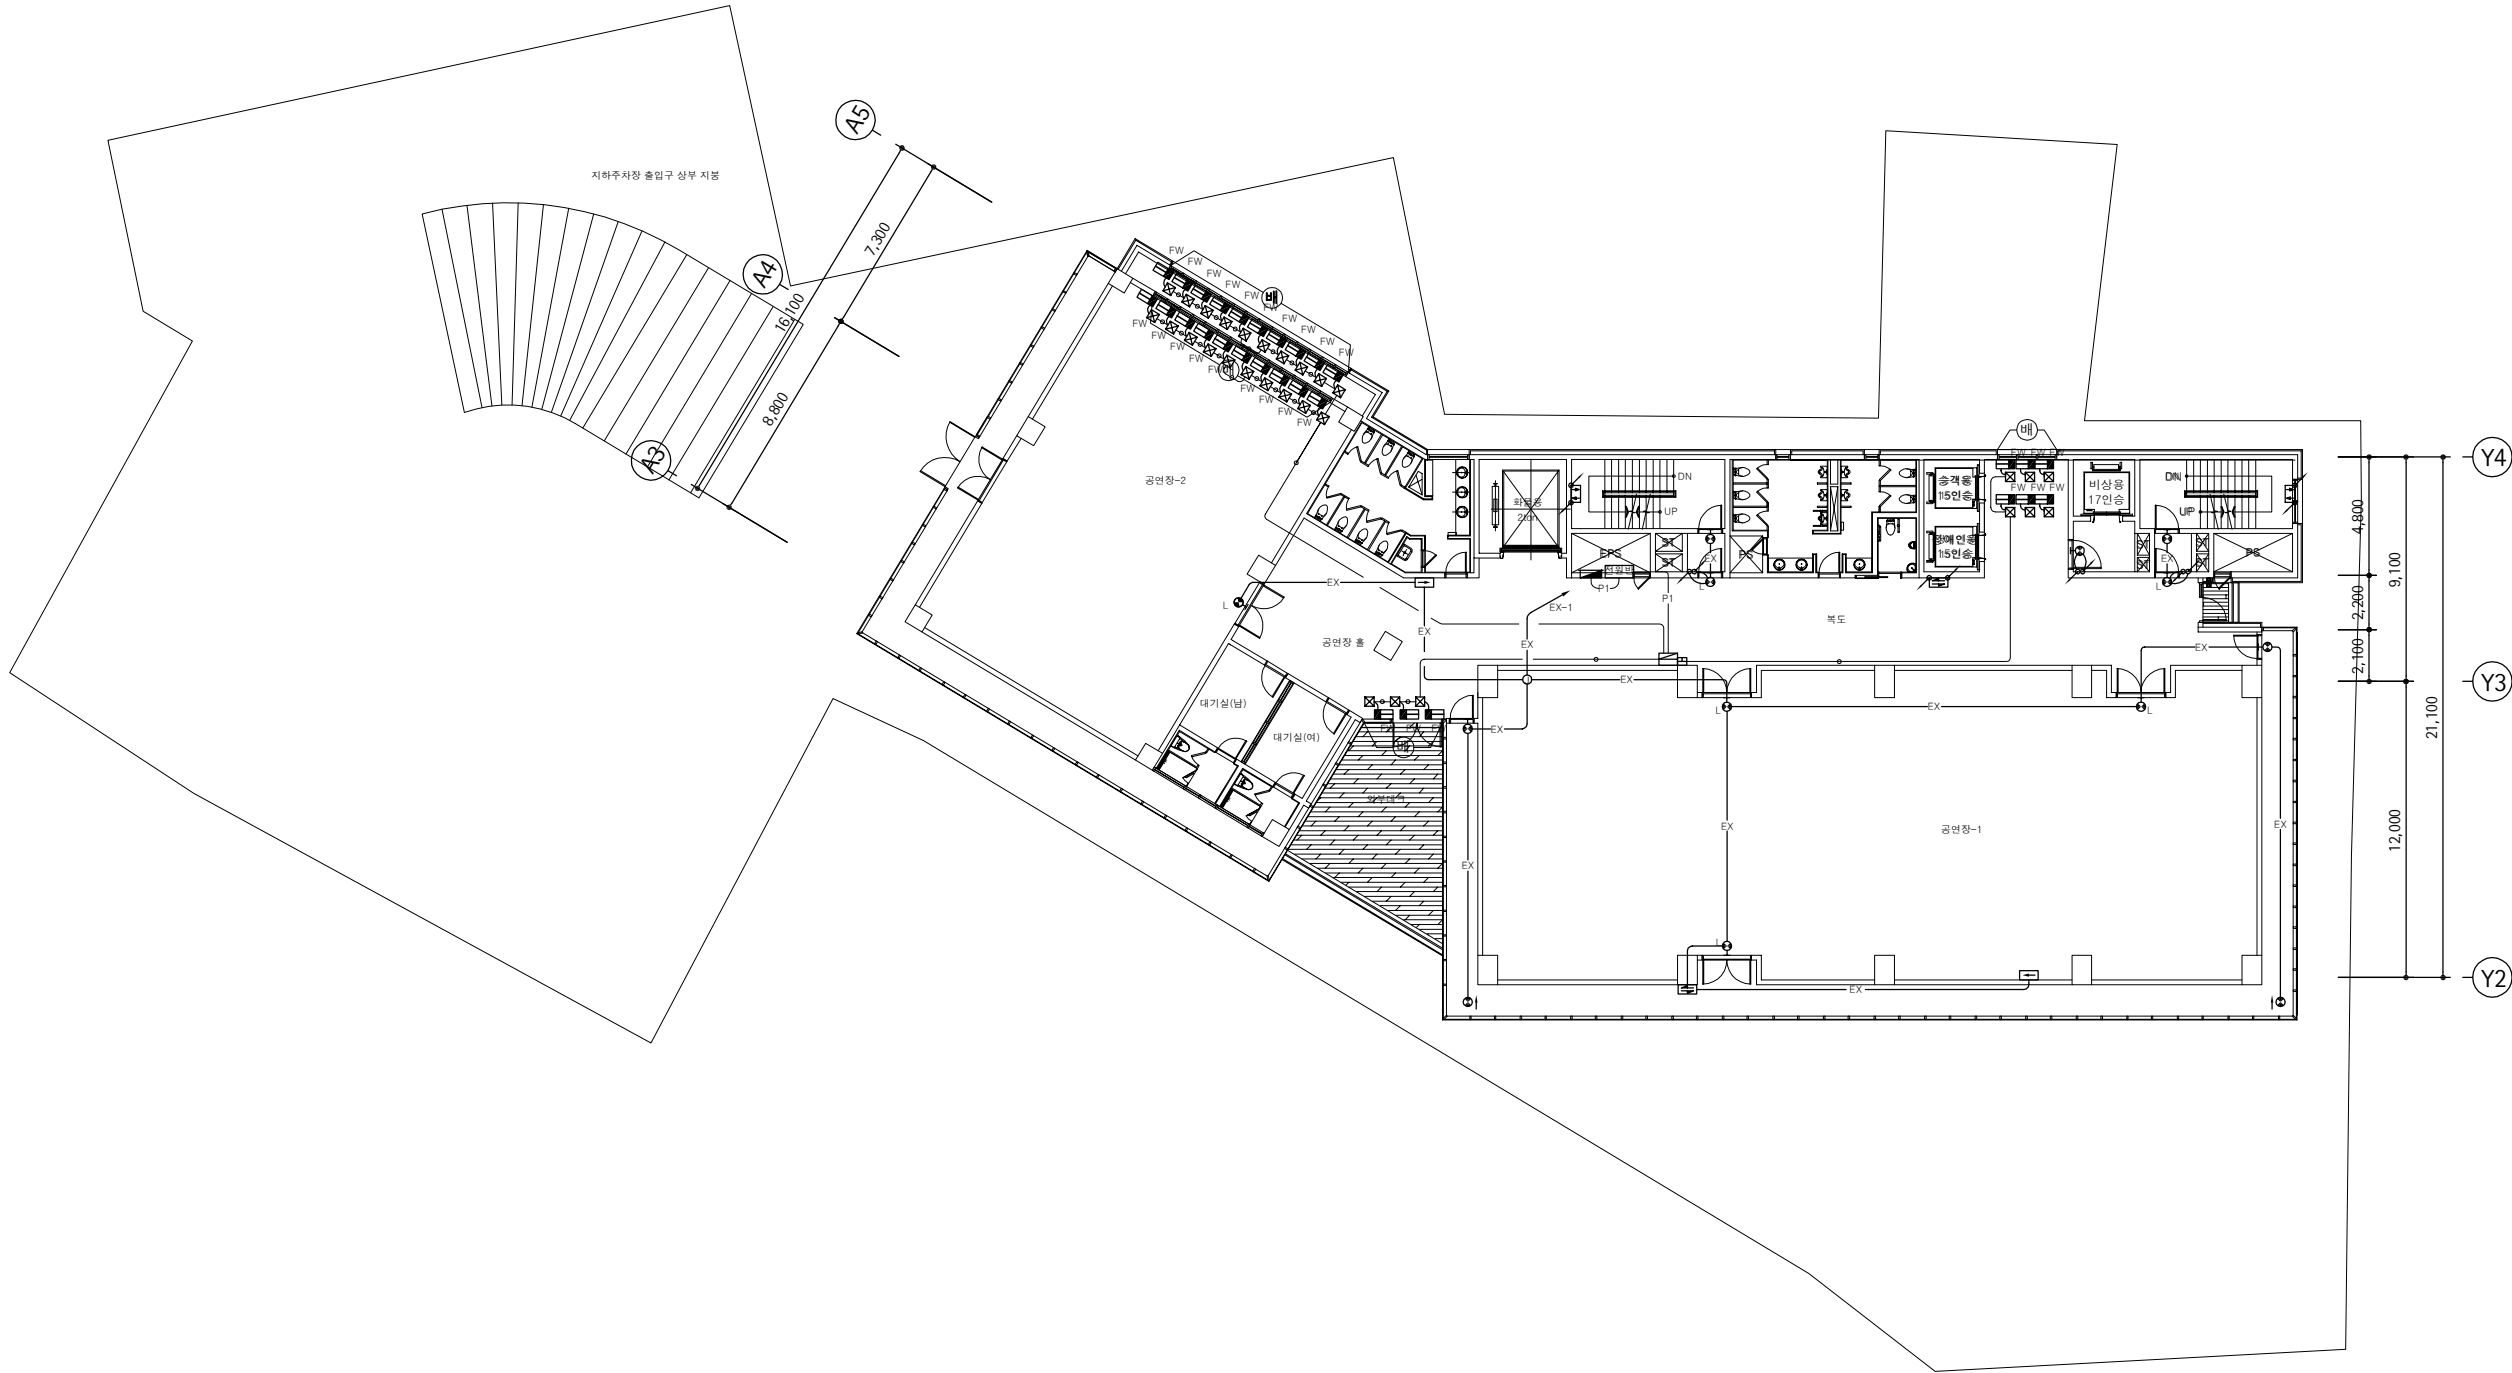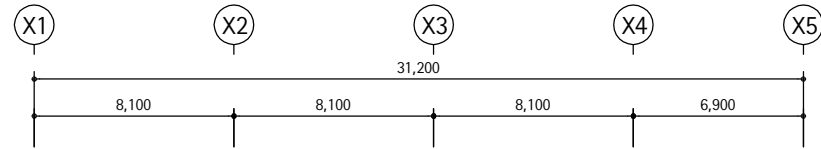

유도등설비 기기산출표

	종	타입	규격	방향	수량
유도등	피난구	벽부형	대형		6
	피난구	벽부형	소형		5
	피난구	천정형 단면	소형	좌,우	1,1
	복도통로	벽부형		우,양방	1,2
	거실통로	벽부형		우	1
	계단			상,하	6

2층 유도등 및 배연창설비 평면도

SCALE:1/150

녹색 에너지 설계 약정업체
종합 전기 설계업체 서울E-1-0023
종합 전기 감리업체 서울S-1-0063
연지니아종합건축(정보통상) 10-104호
주식회사 전기설계 협인

PROJECT TITLE

성수동1가
지식산업센터
신축공사

NOTES

1. 배관배선 및 심법

FW : HFIX 6mm x 5 (28C)
P1 : HFIX 6mm x 2, E6mm (28C)

REVISION	DESCRIPTION	DATE

ORDER ORGAN

INVESTMENT T 터티벤처인베스트먼트
대표전화(02)579-8361
팩시밀리(02)579-8364

PROJECT OFFICE

ATEC(주)에이텍종합건축사사무소
ARCHITECTS & ASSOCIATES
대표전화(02)3462-6366
팩시밀리(02)3462-6368



DRAWING TITLE

3~14층 유도등 평면도

SCALE	APPROVED
A1 : 1 / 150 A3 : 1 / 300	ARCHITECT 김 상 길
DRAWN 남 창 모	DATE 2014. 03

CHECKED	DATE 2014. 03
CONSULTANT	

DRAWING NO.	EF-020
-------------	--------

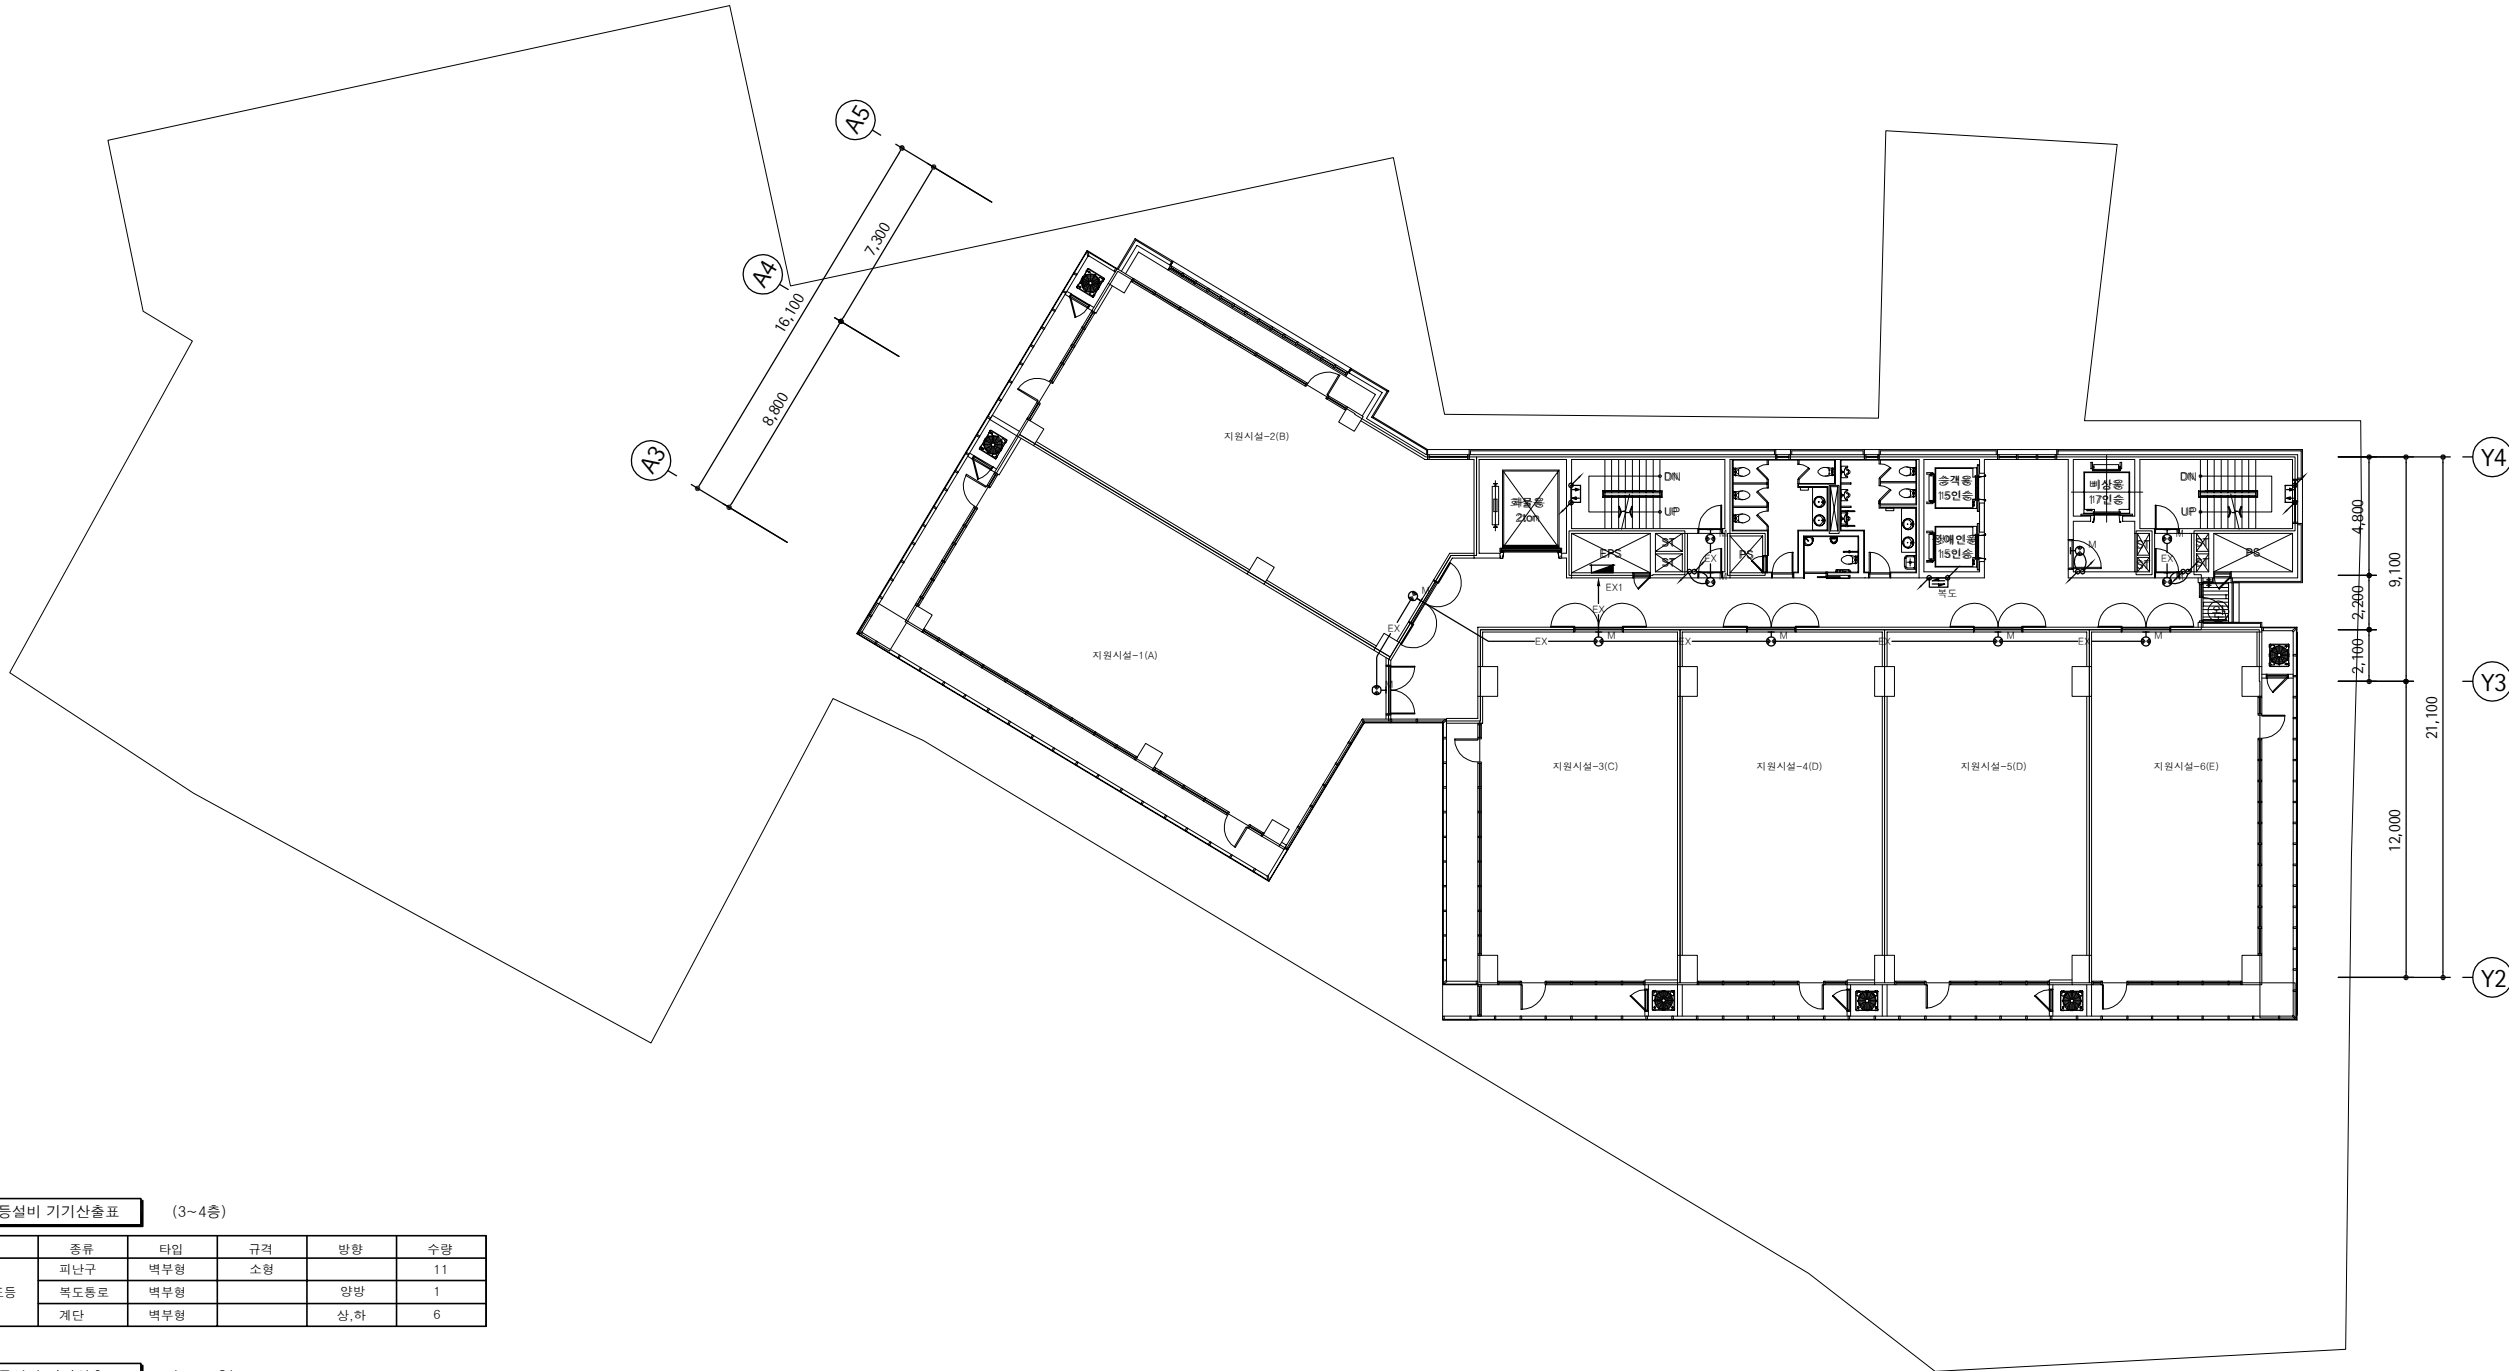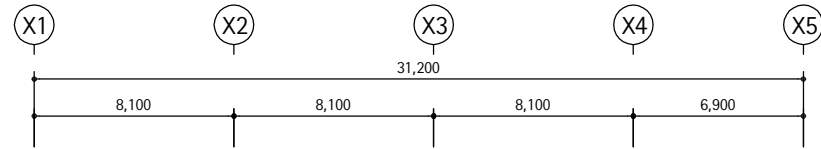

유도등설비 기기산출표 (3~4층)

	종류	타입	규격	방향	수량
유도등	피난구	벽부형	소형		11
	복도통로	벽부형		양방	1
	계단	벽부형		상,하	6

유도등설비 기기산출표 (5~10층)

	종류	타입	규격	방향	수량
유도등	피난구	벽부형	소형		11
	복도통로	벽부형		양방	1
	계단	벽부형		상,하	2

유도등설비 기기산출표 (11~14층)

	종류	타입	규격	방향	수량
유도등	피난구	벽부형	중형		11
	복도통로	벽부형		양방	1
	계단	벽부형		상,하	2

3~14층 유도등 평면도

SCALE:1/150

녹색 에너지 설계 약정업체
종합 전기 설계업체 서울E-1-0023
종합 전기 감리업체 서울S-1-0063
엔지니어링활동주체(정보통신) 10-104호
주식회사 전기설계 협인

PROJECT TITLE

성수동1가
지식산업센터
신축공사

NOTES

REVISION DESCRIPTION DATE

ORDER ORGAN

INVESTMENT TOWER INVESTMENT 대표전화(02)579-8361
팩시밀리(02)579-8364

PROJECT OFFICE ATEC(주)에이텍종합건축사사무소
ARCHITECTS & ASSOCIATES 대표전화(02)3462-6366
팩시밀리(02)3462-6368

DRAWING TITLE

15층 유도등 평면도

SCALE APPROVED

A1 : 1 / 150 ARCHITECT 김 상 길



A3 : 1 / 300

DRAWN 남 창 모 DATE 2014. 03

CHECKED DATE 2014. 03

CONSULTANT

DRAWING NO. EF-021

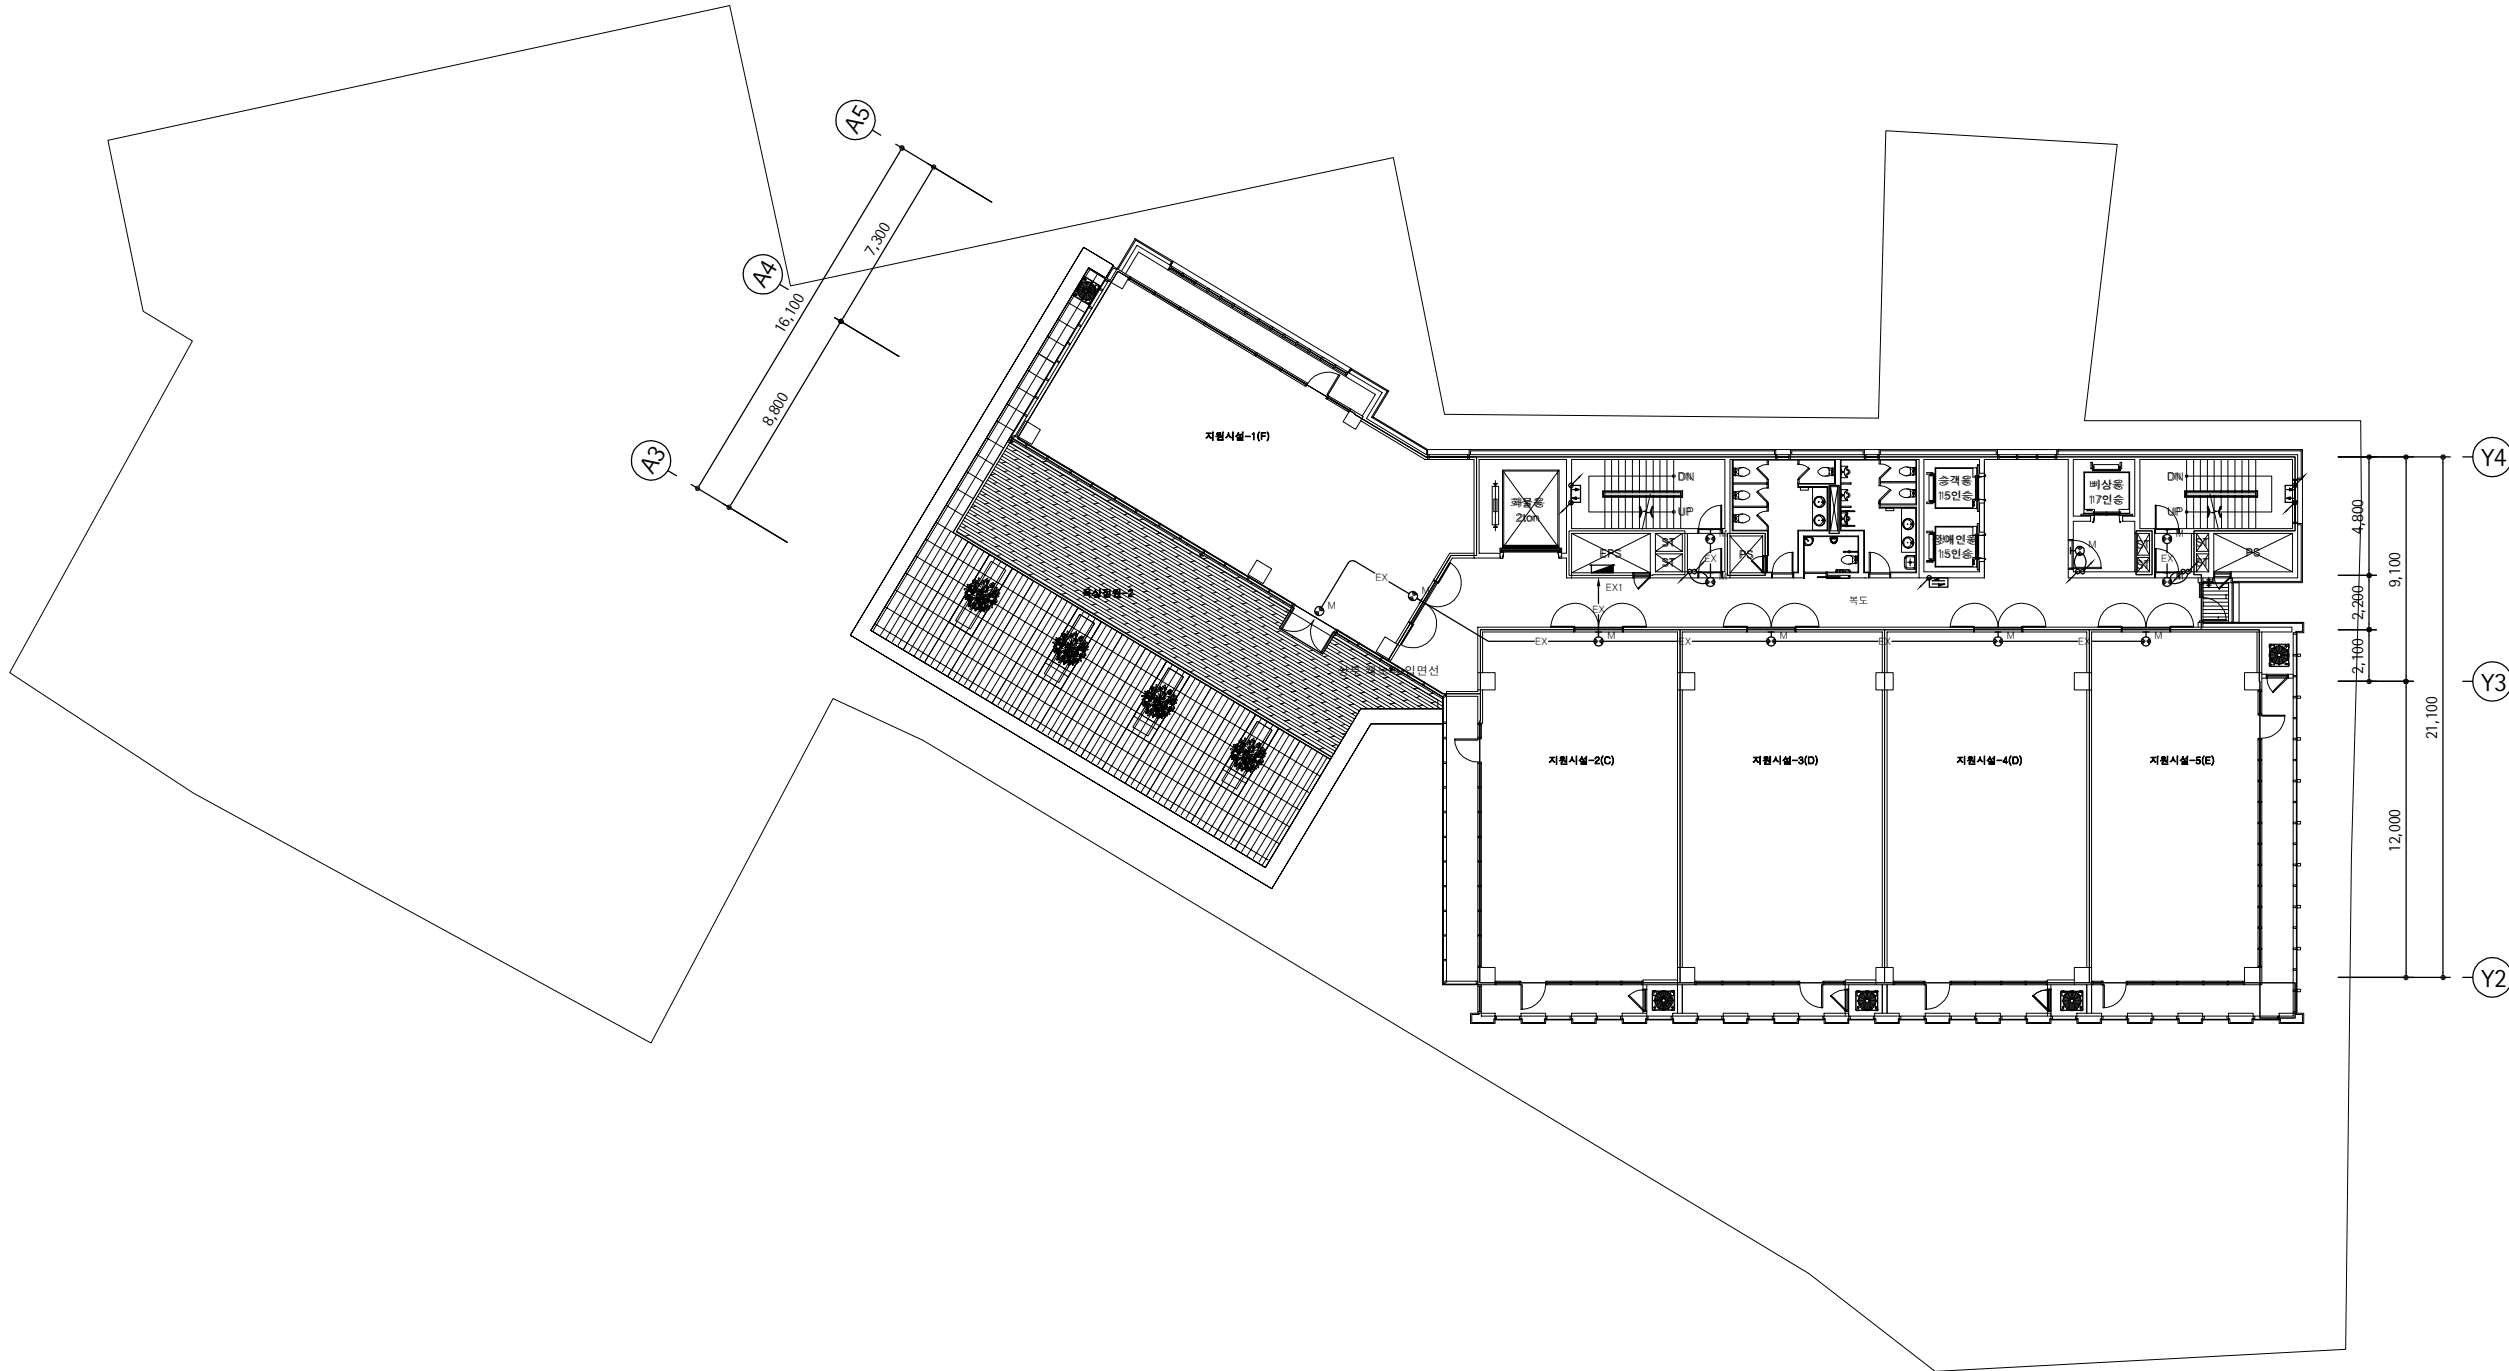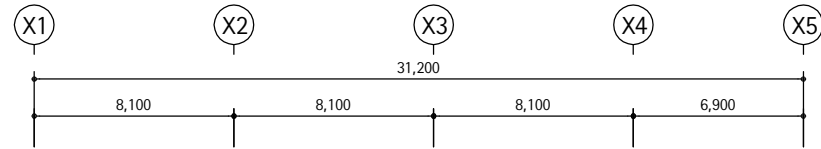

유도등설비 기기산출표

	종류	타입	규격	방향	수량
유도등	피난구	벽부형	중형		10
	피난구	천정형 단면	중형		1
	복도통로	벽부형		양방	1
	계단	벽부형		상,하	2

15층 유도등 평면도

SCALE:1/150

녹색 에너지 설계 약정업체
종합 전기 설계업체 서울E-1-0023
종합 전기 감리업체 서울S-1-0063
연지니아종합등주세(정보통신) 10-104호
주식회사 전기설계 협인

PROJECT TITLE

성수동1가
지식산업센터
신축공사

NOTES

REVISION	DESCRIPTION	DATE

ORDER ORGAN

T 터티벤처인베스트먼트
INVESTMENT 대표전화(02)579-8361
팩시밀리(02)579-8364

PROJECT OFFICE

ATEC (주)에이텍종합건축사사무소
ARCHITECTS & ASSOCIATES 대표전화(02)3462-6366
팩시밀리(02)3462-6368

DRAWING TITLE




옥탑층 유도등 평면도

SCALE	A1 : 1 / 150 A3 : 1 / 300	APPROVED	ARCHITECT
DRAWN	남 창 모	DATE	2014. 03

CHECKED	DATE
	2014. 03

CONSULTANT

DRAWING NO. EF-022

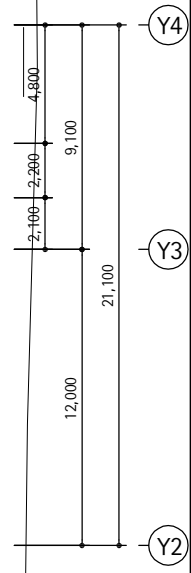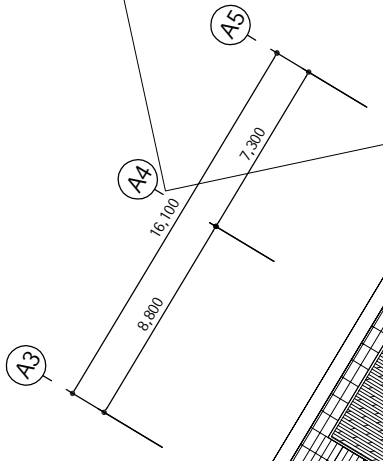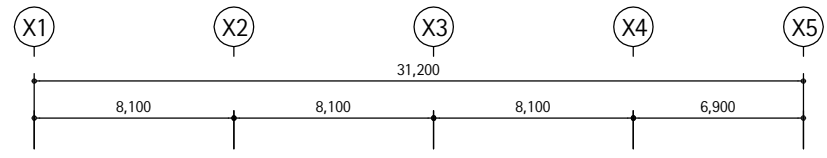



유도등설비 기기산출표					
	종류	타입	규격	방향	수량
유도등	피난구	벽부형	중형		8

옥탑층 유도등 평면도

SCALE:1/150

녹색 에너지 설계 약정업체
종합 전기 설계업체 서울E-1-002호
종합 전기 강리업체 서울S-1-006호
연지니아명물동주세(정보통신) 10-104호
주식회사 전기설계. 협인

	N O T E
Ⓐ	RADIAX CABLE : RFCX-22D(FR)
Ⓑ	FEEDER CABLE : HFC-12D (36C)
Ⓒ	FEEDER CABLE : ECX-10D-2V
▶	SPLITTER
◀	DISTRIBUTOR
□	TERMINAL BOARD
□~~~~	DUMMY LOAD (DL-50)
□	CONNECTOR
단, CABLE TRAY내 배관제외	

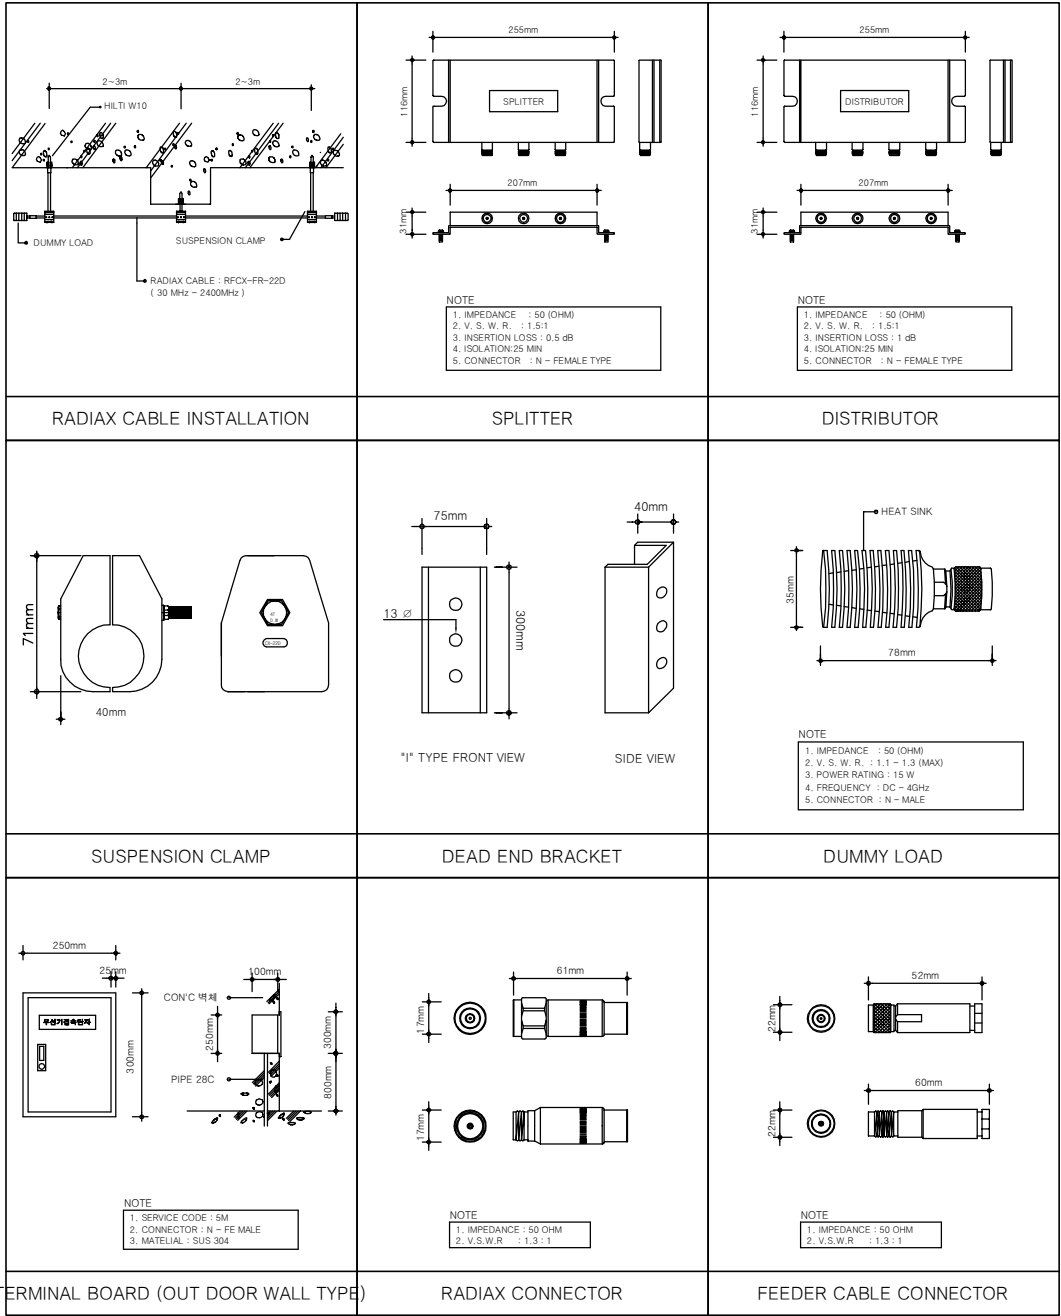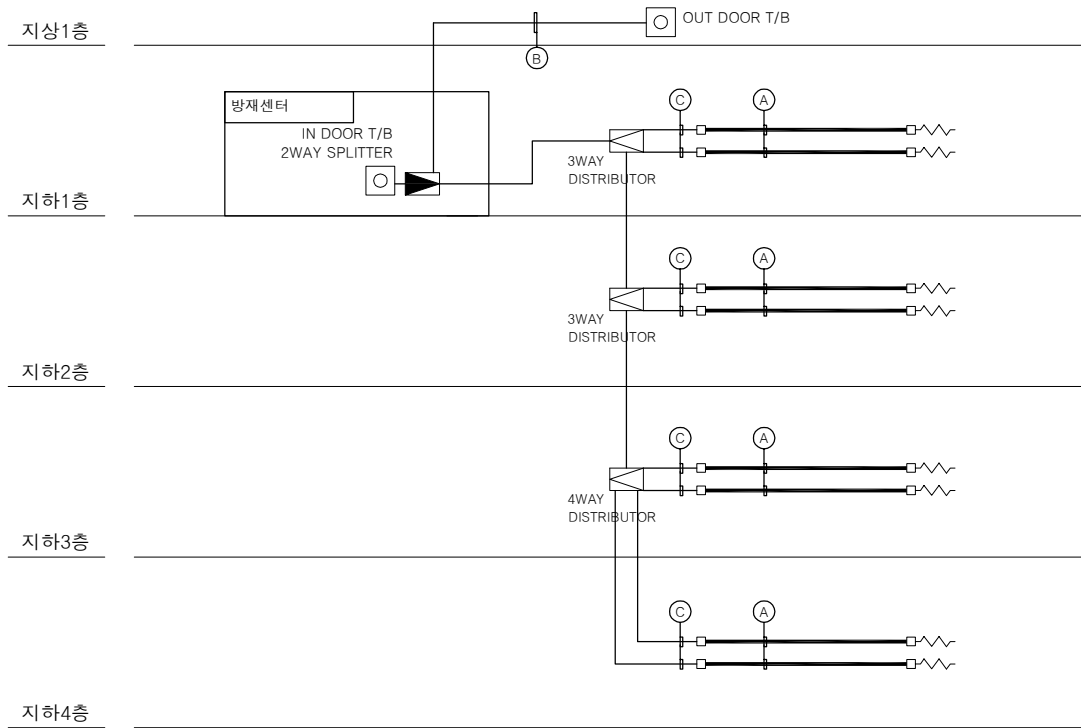

성수동1가
지식산업센터
신축공사

NOTES

REVISION	DESCRIPTION	DATE
ORDER ORGAN		
INVESTMENT		
PROJECT OFFICE		
ARCHITECTS & ASSOCIATES		
DRAWING TITLE		

무선통신보조설비 계통도 및 상세도

SCALE	A1 : NONE A3 : NONE	APPROVED	ARCHITECT	김 상 길
DRAWN	남 창 모	DATE	2014. 03	
CHECKED		DATE	2014. 03	
CONSULTANT				
DRAWING NO.	EF-023			

무선통신보조설비 계통도 및 상세도

SCALE : NONE

녹색 에너지 설계 약정업체
종합 전기 설계업체 서울E-1-002호
종합 전기 감리업체 서울S-1-006호
연지니아평화동주세(정보통선) 10-104호
주식회사 전기설계. 협인

PROJECT TITLE












성수동1가
지식산업센터
신축공사


NOTES

REVISION	DESCRIPTION	DATE

ORDER ORGAN	티티벤처인베스트먼트
INVESTMENT	대표전화(02)579-8361 팩시밀리(02)579-8364
PROJECT OFFICE	
ARCHITECTS & ASSOCIATES	ATEC(주)에이텍종합건축사사무소 대표전화(02)3462-6366 팩시밀리(02)3462-6368


DRAWING TITLE	
소방설비 기기 상세도	
SCALE	APPROVED
A1 : NONE A3 : NONE	ARCHITECT 김 상 길
DRAWN 남 창 모	DATE 2014. 03
CHECKED	DATE 2014. 03
CONSULTANT	
DRAWING NO.	EF-024

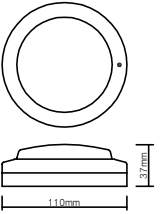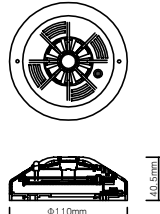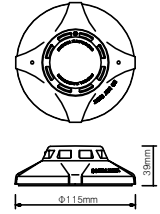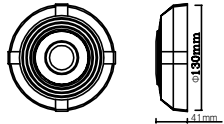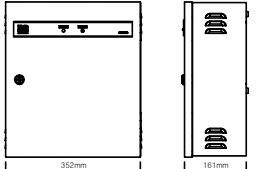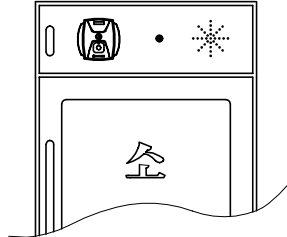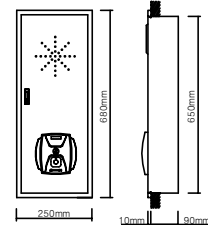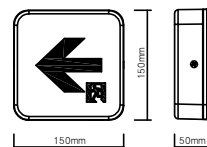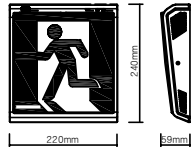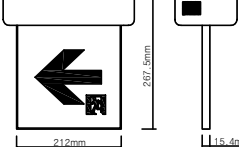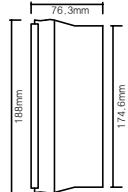 일반사양 1. 종 별 : 차동식 스포트형 감지기 2. 형 식 : 2중, 보통형, 재용형, 비방수형 3. 정 격 : DC 24V, 0.1A 4. 온 도 : -10℃ ~ +50℃	 일반사양 1. 종 별 : 정온식 스포트형 감지기 2. 형 식 : 1중, 보통형, 재용형, 비방수형(60℃ ~ 120℃) 3. 정 격 : DC 24V, 0.1A 4. 온 도 : -10℃ ~ +50℃	 일반사양 1. 종 별 : 광전식 연기 감지기 2. 형 식 : 2중, 비촉직형, 재용형 3. 정 격 : DC 24V, 35mA 4. 온 도 : -10℃ ~ +50℃	 일반사양 1. 종 별 : 전자싸이렌 2. 정 격 : DC 24V 3. 온 도 : -10℃ ~ +50℃ 4. 소비전류 : 280mA
차동식 스포트형 감지기	정온식 스포트형 감지기	광전식 연기 감지기	전자싸이렌
 일반사양 1. 종 별 : 전원공급반 2. 온 도 : -10℃ ~ +50℃ 3. 정 격 : AC 220V / 60Hz 4. 상대습도 : 0 ~ 90% 5. 회로전원 : DC 24V 6. 예비전원 : DC 24V, 4Ah / 5Ah / 7Ah	 소 화 경 상 단 부	 일반사양 1. 재 질 : DOOR-S.U.S-1.2t 메릴BOX-STEEL-1.2t 2. 발신기함은 소화전공급체와 협의하여 위치표시등의 취부홀을 앞에도록 한다.	 일반사양 1. 종 별 : 벽부형 통로유도등 2. 형 식 : LED형 3. 정 격 : AC220V ± 60Hz 4. 온 도 : -10℃ ~ +50℃ 5. 소비전력 : 2.5W 6. 예비전원 : DC 3.6V 0.6Ah / Ni-Cd 축전지 내장
전원공급반	소 화 경 상 단 부	수동발신기세트	벽부형 통로유도등
 일반사양 1. 종 별 : 벽부형 피난구유도등 2. 형 식 : LED형 3. 정 격 : AC220V ± 60Hz 4. 온 도 : -10℃ ~ +50℃ 5. 소비전력 : 3.7W 6. 예비전원 : DC 3.6V 0.6Ah / Ni-Cd 축전지 내장	 일반사양 1. 종 별 : 천정형 통로유도등(중형) 2. 형 식 : 돌출형,LED형, 단면, 양면 3. 정 격 : AC220V ± 60Hz 4. 온 도 : -10℃ ~ +50℃ 5. 소비전력 : 단면-3.7W / 양면-5.2W 6. 예비전원 : DC 3.6V 0.9Ah / Ni-Cd 축전지 내장	 일반사양 1. 종 별 : 계단통로유도등 2. 형 식 : LED형 3. 정 격 : AC220V ± 60Hz 4. 온 도 : -10℃ ~ +50℃ 5. 소비전력 : 평상시 16W 충전시 25W 6. 예비전원 : DC 24V 0.9Ah Ni-Cd 축전지 내장	
벽부형 피난구유도등	천정형 피난구유도등	계단통로 유도등	

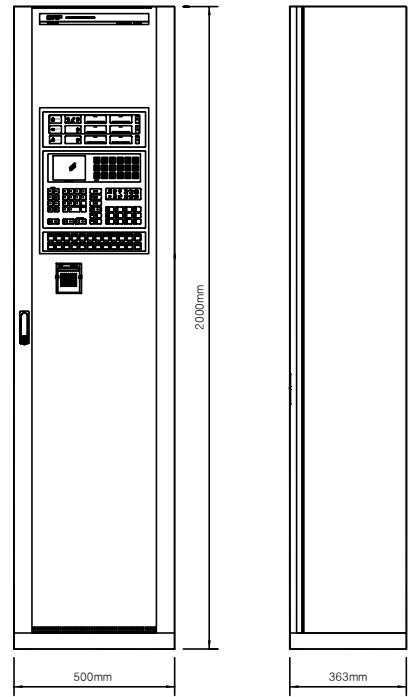

1. 종 별 : GR형 복합 수신기
2. 주 전 원 : AC 110V/220V
3. 접속중계기 : R형 중계기
4. 외 함 : 일반압연강판제 2.0mmt

R 형 수 신 기

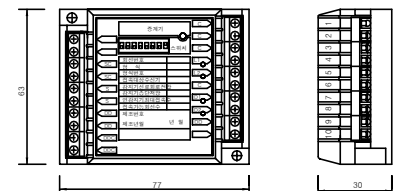

1. 종 별 : R형 중계기
2. 회선용량 : 1감시/1제어, 2감시/2제어
3. 입력전원 : DC 26V
4. 감시시소비전류 : DC 26V 900μA
5. 출력용량 : DC 24V
6. 외 함 : 일반압연강판제 2.0mmt

R 형 중 계 기

소방설비 기기 상세도
SCALE : NONE

녹색 에너지 설계 약정업체
종합 전기 설계업체 서울E-1-0023
종합 전기 감리업체 서울S-1-0063
연지니아종합건축사(정보통신) 10-104호
주식회사 전기설계. 협인

PROJECT TITLE

성수동1가
지식산업센터
신축공사

NOTES

NO.	ITEM	MATERIAL & SIZE	Q'TY
1	OUTLET BOX	100 x 100 x 54	1
2	FLEXIBLE CONDUIT	ZPC	AS REQ'D
3	FLEXIBLE CONNECTOR	ZPC	2
4	SCREW BOLT	STEEL	2

NO.	ITEM	MATERIAL & SIZE	Q'TY
1	OUTLET BOX	100 x 100 x 54	1
2	SCREW BOLT	STEEL	2

NO.	ITEM	MATERIAL & SIZE	Q'TY
1	노출용 박스	100 x 100 x 54	1
2	STRONG ANCHOR	φ6mm	6
3	SCREW BOLT	STEEL	2
4	UNISTRUT CHANNEL	41 x 41 x 2.6 - 1	AS REQ'D
5	CONDUIT CLAMP/BOLT & NUT	ZPC	2
6	UNION	ZPC	2

NO.	ITEM	MATERIAL & SIZE	Q'TY
1	노출용 박스	100 x 100 x 54	1
2	STRONG ANCHOR	φ6mm	6
3	SCREW BOLT	STEEL	2
4	UNISTRUT CHANNEL	41 x 41 x 2.6 - 1	AS REQ'D
5	CONDUIT CLAMP/BOLT & NUT	ZPC	2
6	UNION	ZPC	2

NO.	ITEM	MATERIAL & SIZE	Q'TY
1	OUTLET BOX	100 x 100 x 54	1
2	SCREW BOLT	STEEL	2

감지기 설치 상세도(매입형)

감지기 설치 상세도(매입형)

감지기 설치 상세도(노출형)

감지기 설치 상세도(노출형)

발신기 설치 상세도(매입형)

NO.	ITEM	MATERIAL & SIZE	Q'TY
1	OUTLET BOX	100 x 100 x 54	1
2	CONDUIT CLAMP	STEEL	1
3	STRONG ANCHOR	φ6mm	6
4	UNION	STEEL	1

NO.	ITEM	MATERIAL & SIZE	Q'TY
1	UNISTRUT CHANNEL	41 x 41 x 2.6 - 1	AS REQ'D
2	CONDUIT CLAMP	STEEL	1
3	STRONG ANCHOR	φ6mm	6
4	UNION	STEEL	1

NO.	ITEM	MATERIAL & SIZE	Q'TY
1	UNISTRUT CHANNEL	41 x 41 x 2.6 - 1	AS REQ'D
2	CONDUIT CLAMP	STEEL	1
3	STRONG ANCHOR	φ6mm	6
4	UNION	STEEL	1

NO.	ITEM	MATERIAL & SIZE	Q'TY
1	OUTLET BOX	100 x 100 x 54	1
2	SCREW BOLT	STEEL	4

NO.	ITEM	MATERIAL & SIZE	Q'TY
1	OUTLET BOX	100 x 100 x 54	1
2	UNISTRUT CHANNEL	41 x 41 x 2.6 - 1	AS REQ'D
3	CONDUIT CLAMP/BOLT & NUT	ZPC	1
4	SCREW BOLT	STEEL	4
5	STRONG ANCHOR	φ6mm	4
6	UNION	ZPC	1

시각경보장치(스트로브)

슈퍼 비조리 패널 (매입형)

슈퍼 비조리 패널 (노출형)

고효율 피난구 유도등(매입형)

고효율 피난구 유도등(노출형)

NO.	ITEM	MATERIAL & SIZE	Q'TY
1	OUTLET BOX	100 x 100 x 54	1
2	FLEXIBLE CONDUIT	ZPC	AS REQ'D
3	FLEXIBLE CONNECTOR	ZPC	2
4	SCREW BOLT	STEEL	2

NO.	ITEM	MATERIAL & SIZE	Q'TY
1	UNISTRUT CHANNEL	41 x 41 x 2.6	AS REQ'D
2	CONDUIT CLAMP/BOLT & NUT	ZPC	1
3	UNION	ZPC	1
4	STRONG ANCHOR	φ6mm	6

고효율 피난구 유도등(천정형)

통로 유도등(노출형)

- 위 상세도는 일반 설치 상세도이며, 현장여건에 따라 변경될 수 있음.

소방설비 기기설치 상세도

SCALE : NONE

녹색 에너지 설계 약정업체

종합 전기 설계업체 서울E-1-002호
종합 전기 관리업체 서울S-1-006호
연지니아엔지니어링주식(정보통상) 10-104호
주식회사 전기설계

협인

REVISION	DESCRIPTION	DATE
ORDER ORGAN		
T T 터티벤쳐인베스트먼트		
INVESTMENT		
PROJECT OFFICE		
ATEC (주)에이텍종합건축사사무소		
DRAWING TITLE		
소방설비 기기설치 상세도		
SCALE	APPROVED	
A1 : NONE	ARCHITECT	김 상 길
A3 : NONE		
DRAWN	DATE	2014. 03
남 창 모		
CHECKED	DATE	2014. 03
CONSULTANT		
DRAWING NO.	EF-025	