


NOTES

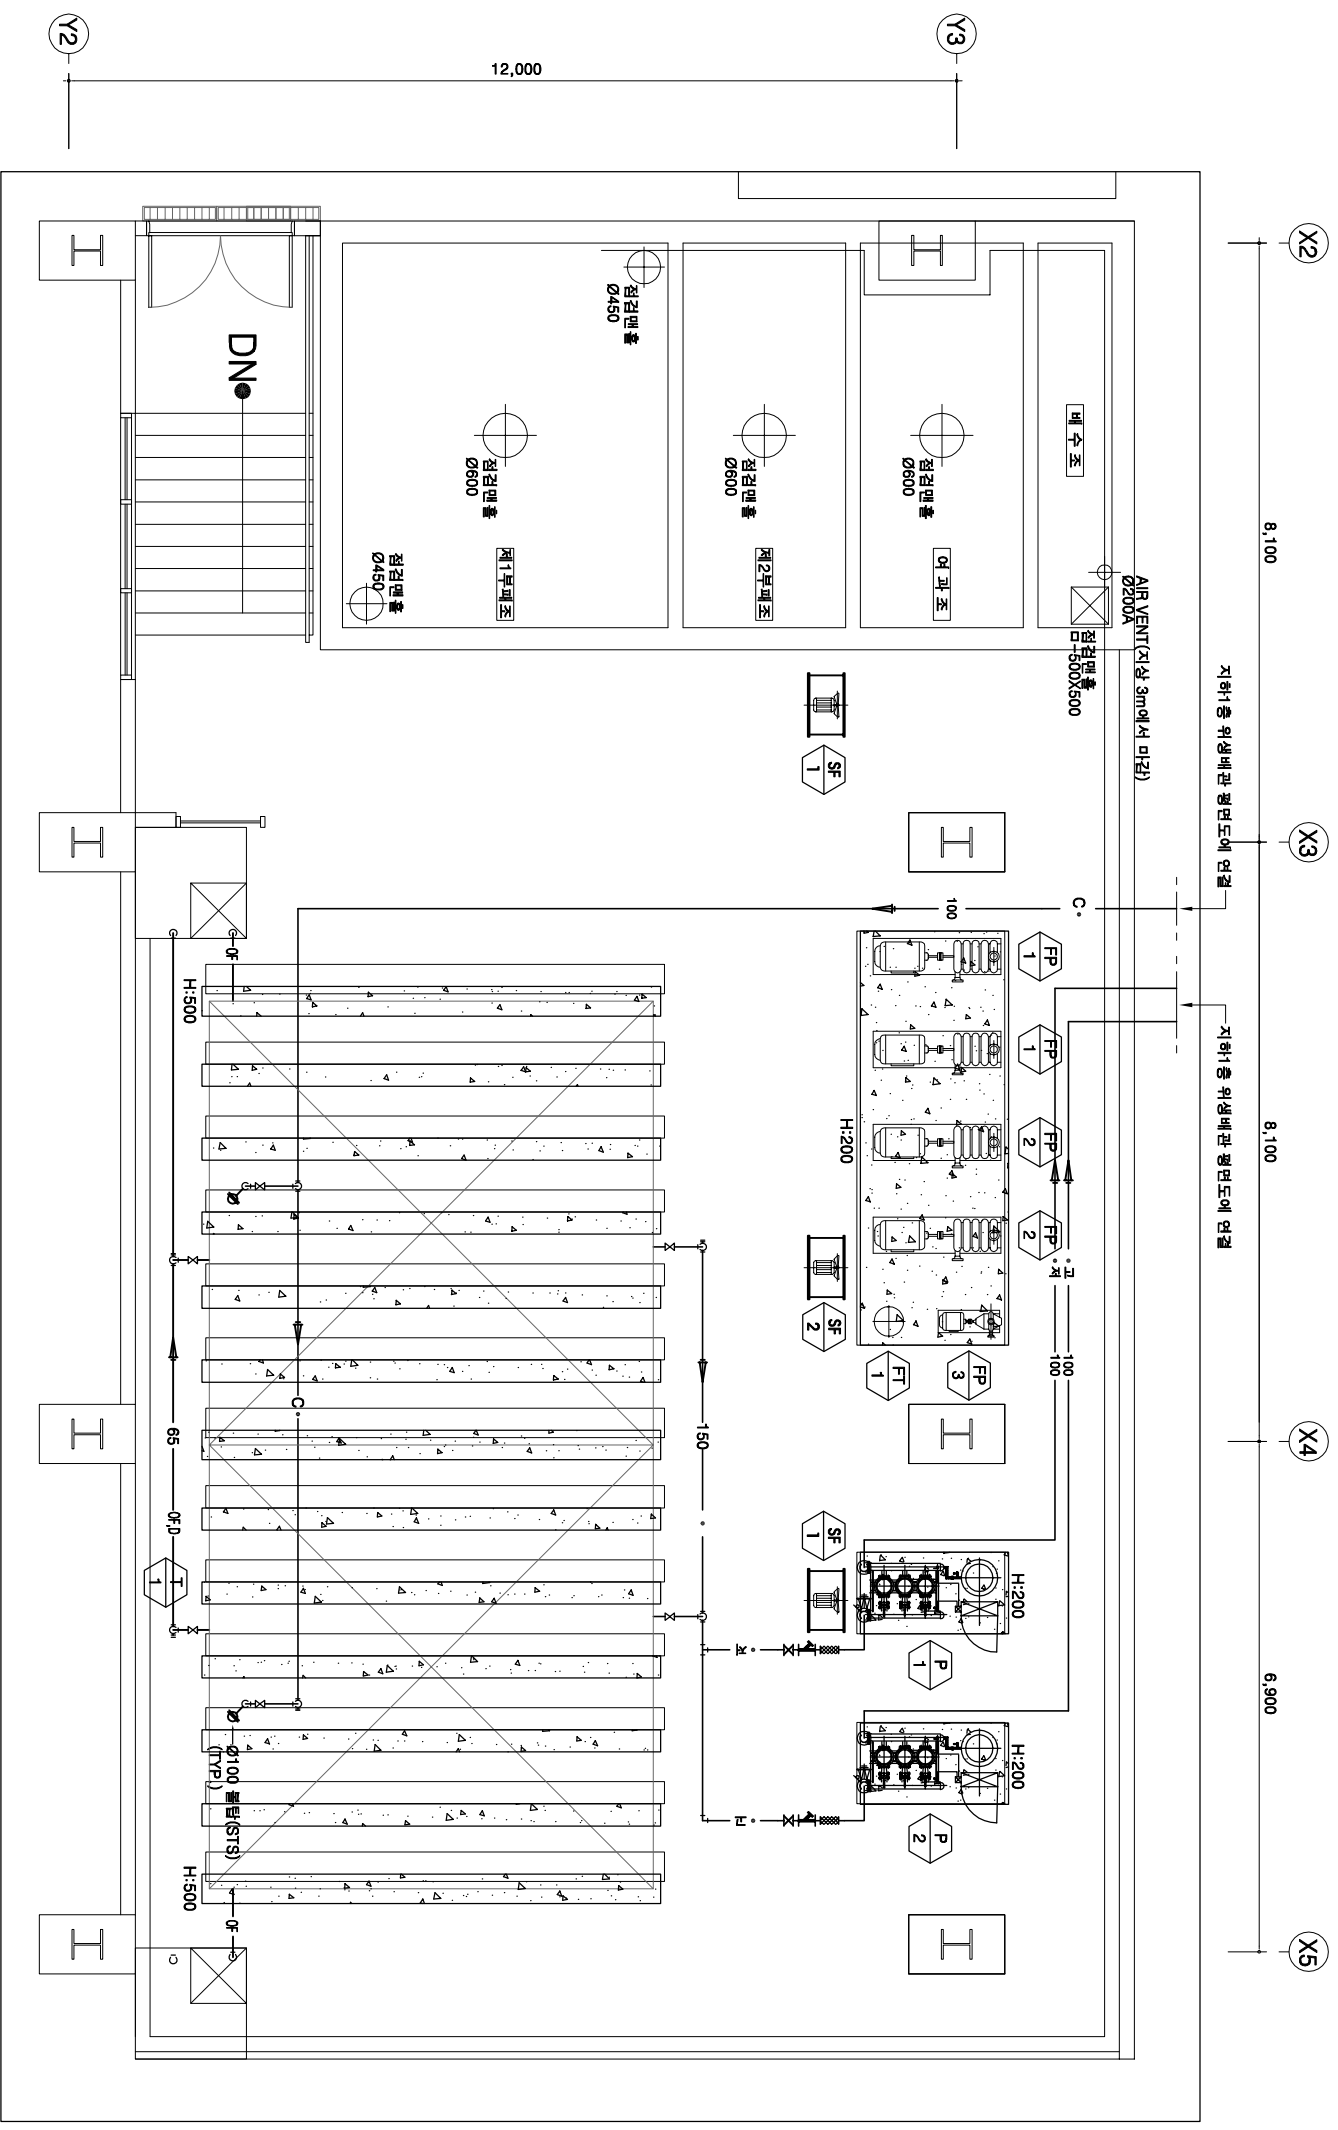

기계실 확대 위생배관 평면도

축척 : A1:1/50, A3:1/100

DRAWING NO.		M-007
CHECKED		DATE
CONSULTANT		2014. 03
SCALE		APPROVED
A1 : 1 / 50		ARCHITECT
A3 : 1 / 100		김 상 길
DRAWN		DATE
하 진 태		2014. 03
PROJECT OFFICE		DATE
ATEC(주)에이텍종합건축사사무소		2014. 03
ARCHITECT		2014. 03
INVESTMENT		2014. 03
ORDER ORIGIN		2014. 03
REVISION		2014. 03
DESCRIPTION		2014. 03
DATE		2014. 03
PROJECT TITLE		2014. 03
DRAWING TITLE		2014. 03
기계실 확대 위생배관 평면도		2014. 03

NOTES

REVISION

DESCRIPTION

DATE

ORDER DRAWN

DATE

INVESTMENT

DATE

PROJECT OFFICE

DATE

ARCHITECT

DATE

DRAWING TITLE

DATE

SCALE

APPROVED

DRAWN

DATE

CHECKED

DATE

CONSULTANT


DATE

DRAWING NO.

DATE

지하4층
위생배관 평면도

2014. 03

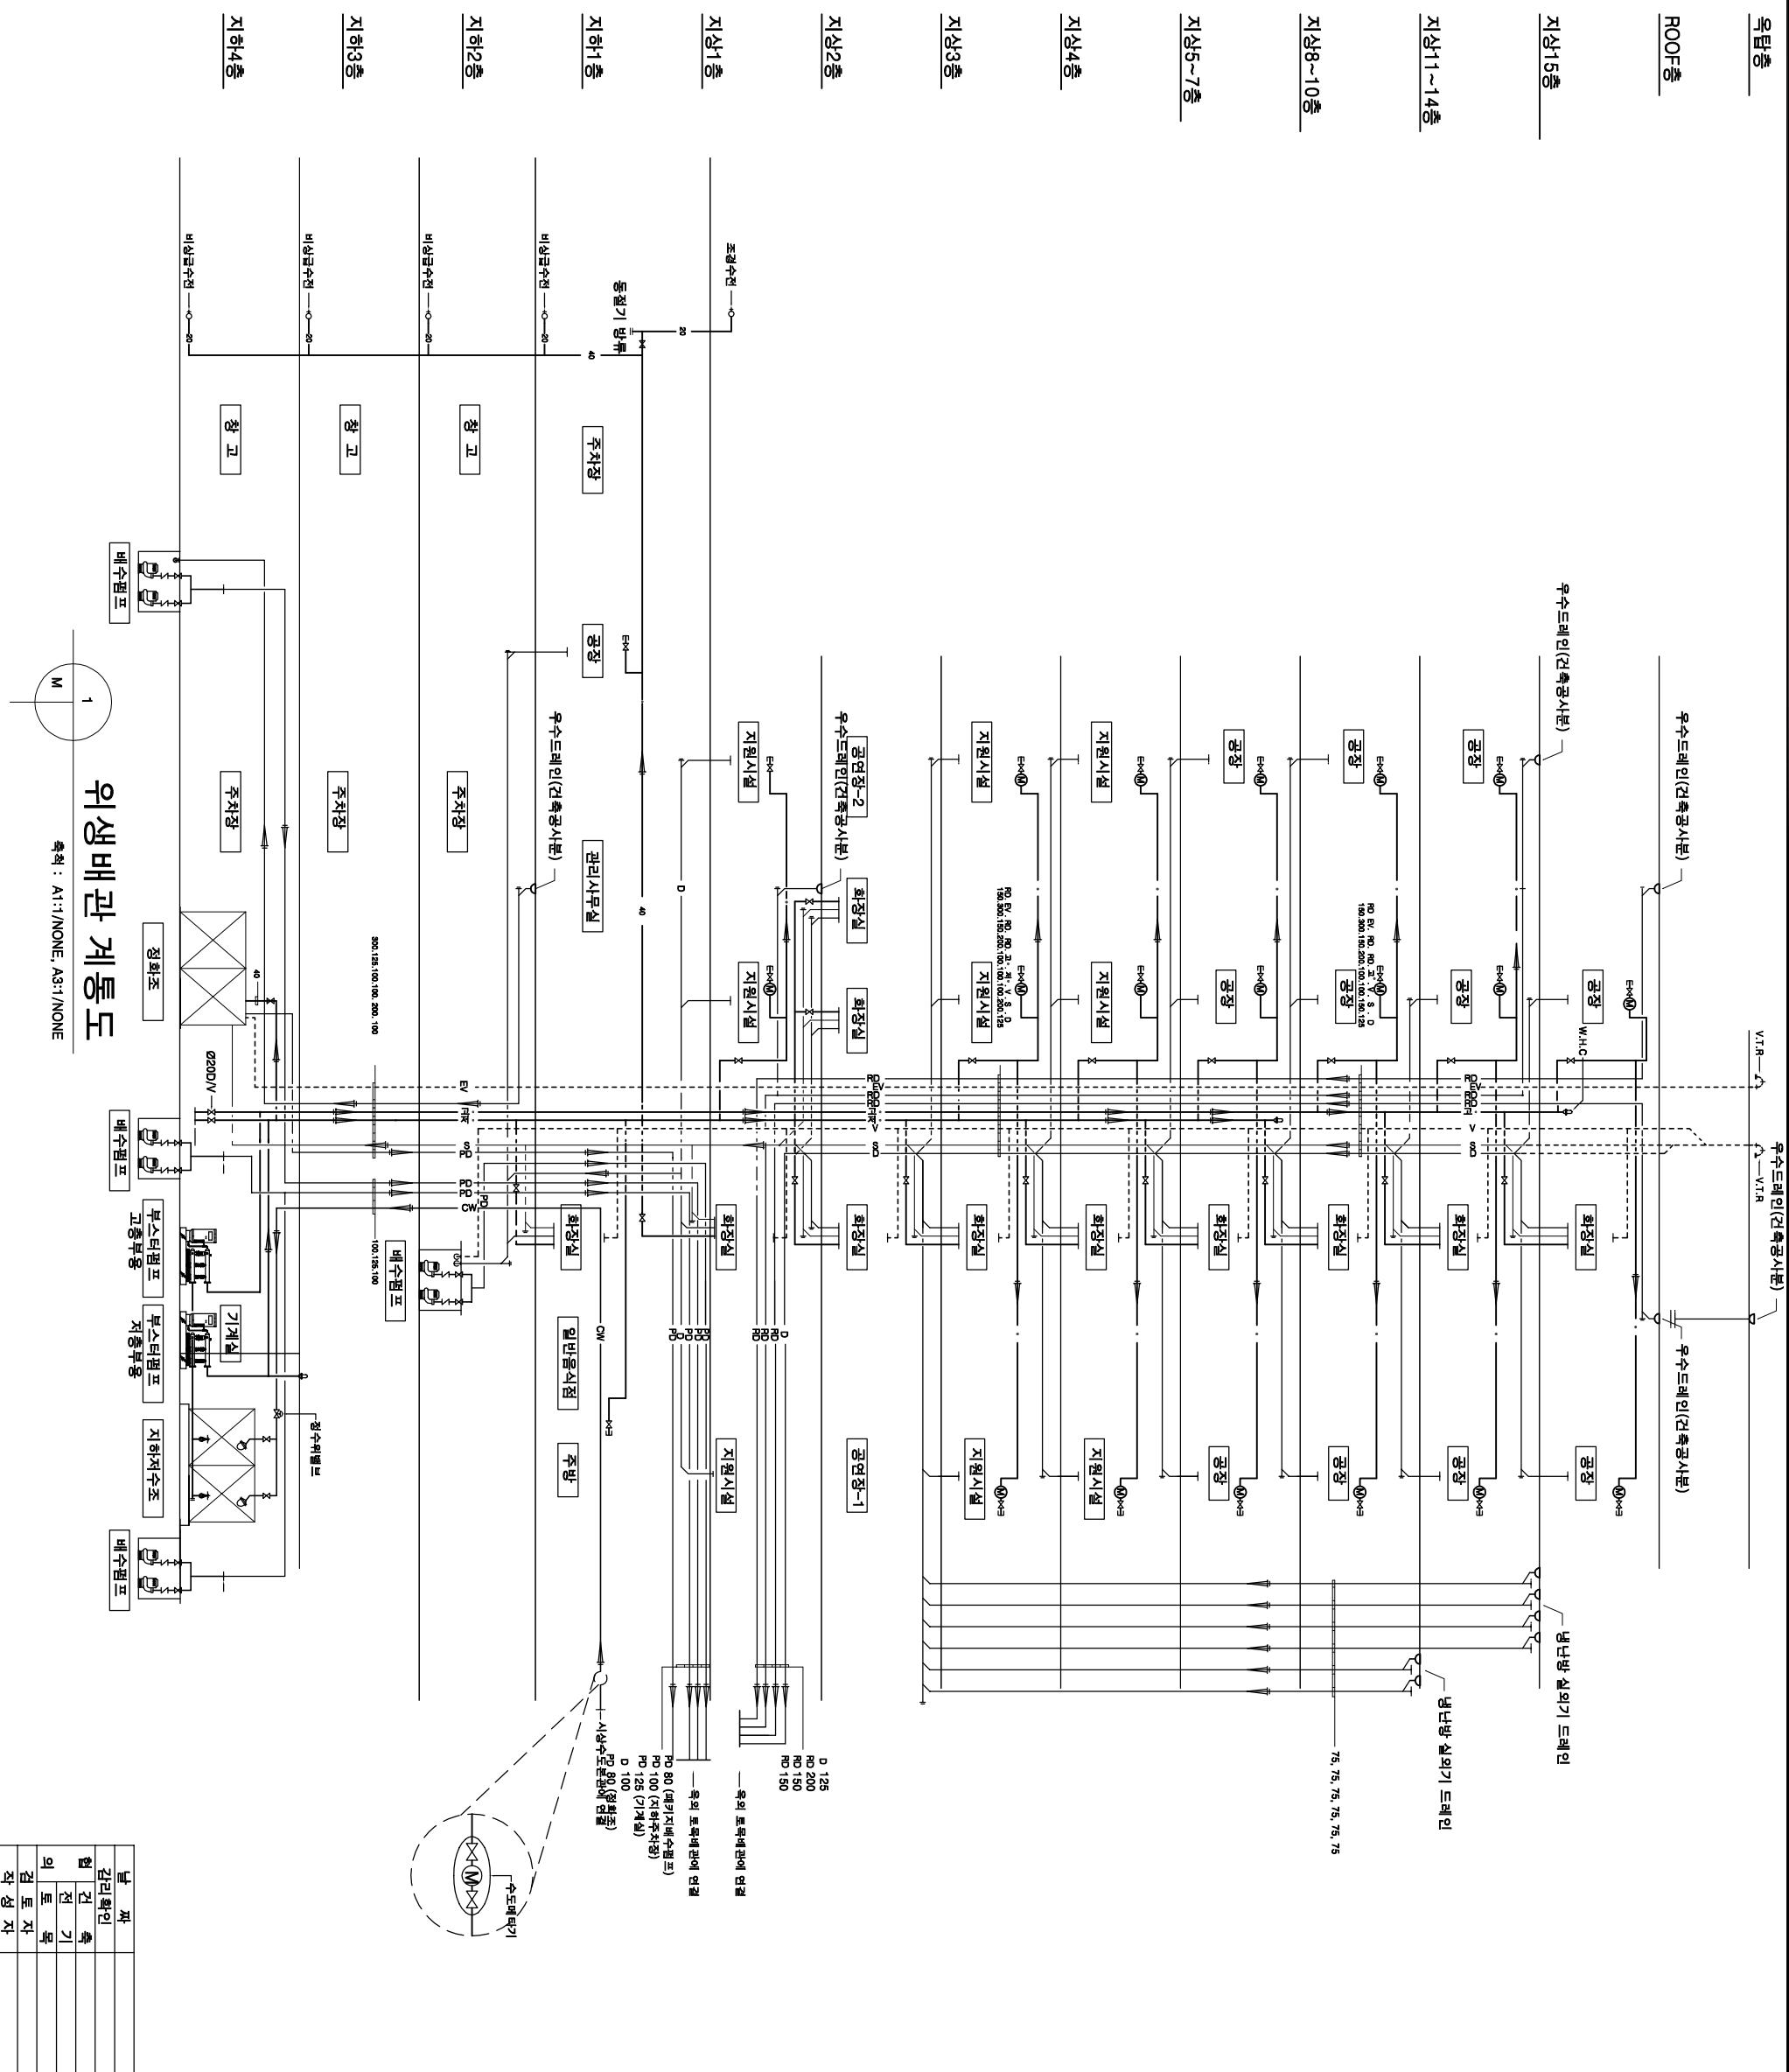

우담층

ROOF층

지상15층

지상11~14층

지상8~10층

지상5~7층

지상4층

지상3층

지상2층

지상1층

지하1층

지하2층


지하3층

지하4층

PROJECT TITLE

성수동1가
지식산업센터
신축공사

NOTES

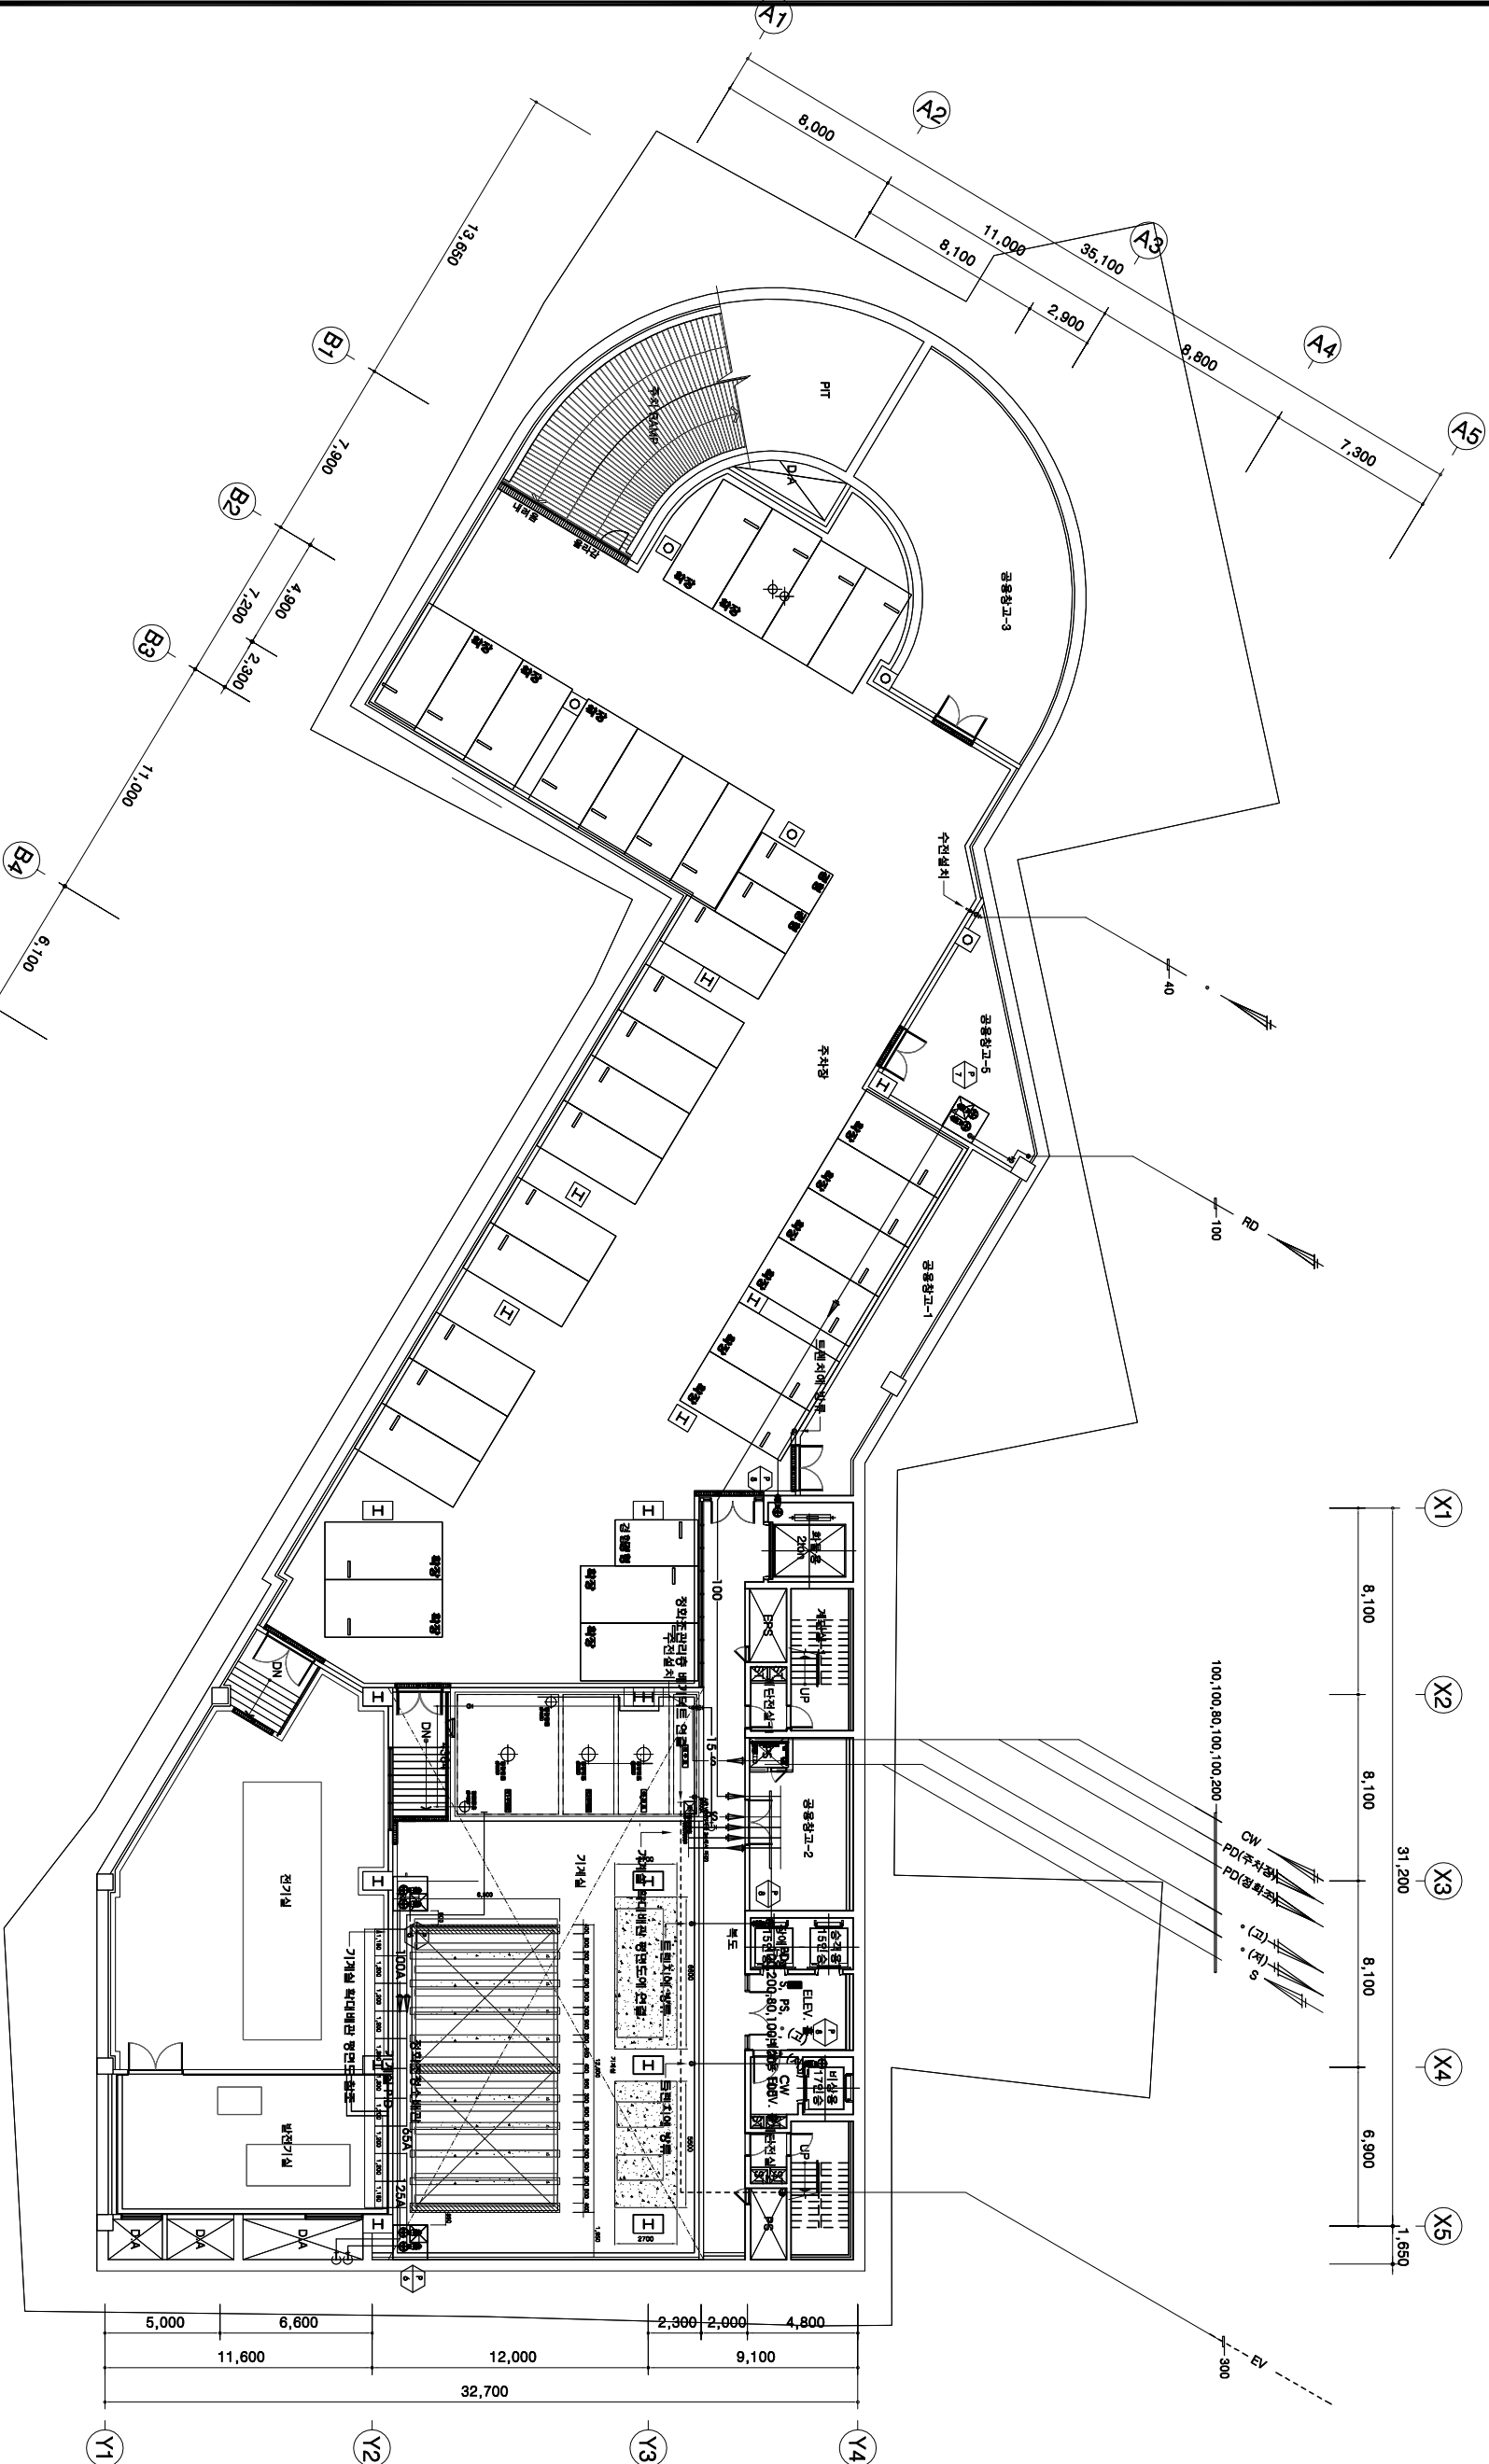

지하4층 위생배관 평면도

축척 : A1:1/150, A3:1/300

날 짜	
관리확인	
설 계	
전 기	
의 토	
목	
검 토 자	
작 성 자	

CHECKED	DATE	2014. 03
CONSULTANT		
DRAWING NO.		M-202

REVISION	DESCRIPTION	DATE
ORDER ORIGIN		
INVESTMENT		
PROJECT OFFICE		
ARCHITECT		
DESIGNER		
DATE		


SCALE	APPROVED
A1 : 1 / 150	ARCHITECT
A3 : 1 / 300	DESIGNER
DATE	2014. 03

PROJECT TITLE	
ARCHITECT	
DESIGNER	
DATE	

SCALE	APPROVED
A1 : 1 / 150	ARCHITECT
A3 : 1 / 300	DESIGNER
DATE	2014. 03

CHECKED	DATE	2014. 03
CONSULTANT		
DRAWING NO.		M-202

성수동1가
지식산업센터
신축공사



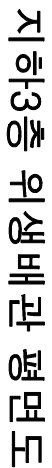


날짜	2014. 03
검리확인	CORREL.YMNT
출	
기	
전	
록	
의	
검토자	
작성자	
	DRAWING NO. M-203

PROJECT TITLE

성수동1가
지식산업센터
신축공사

NOTES

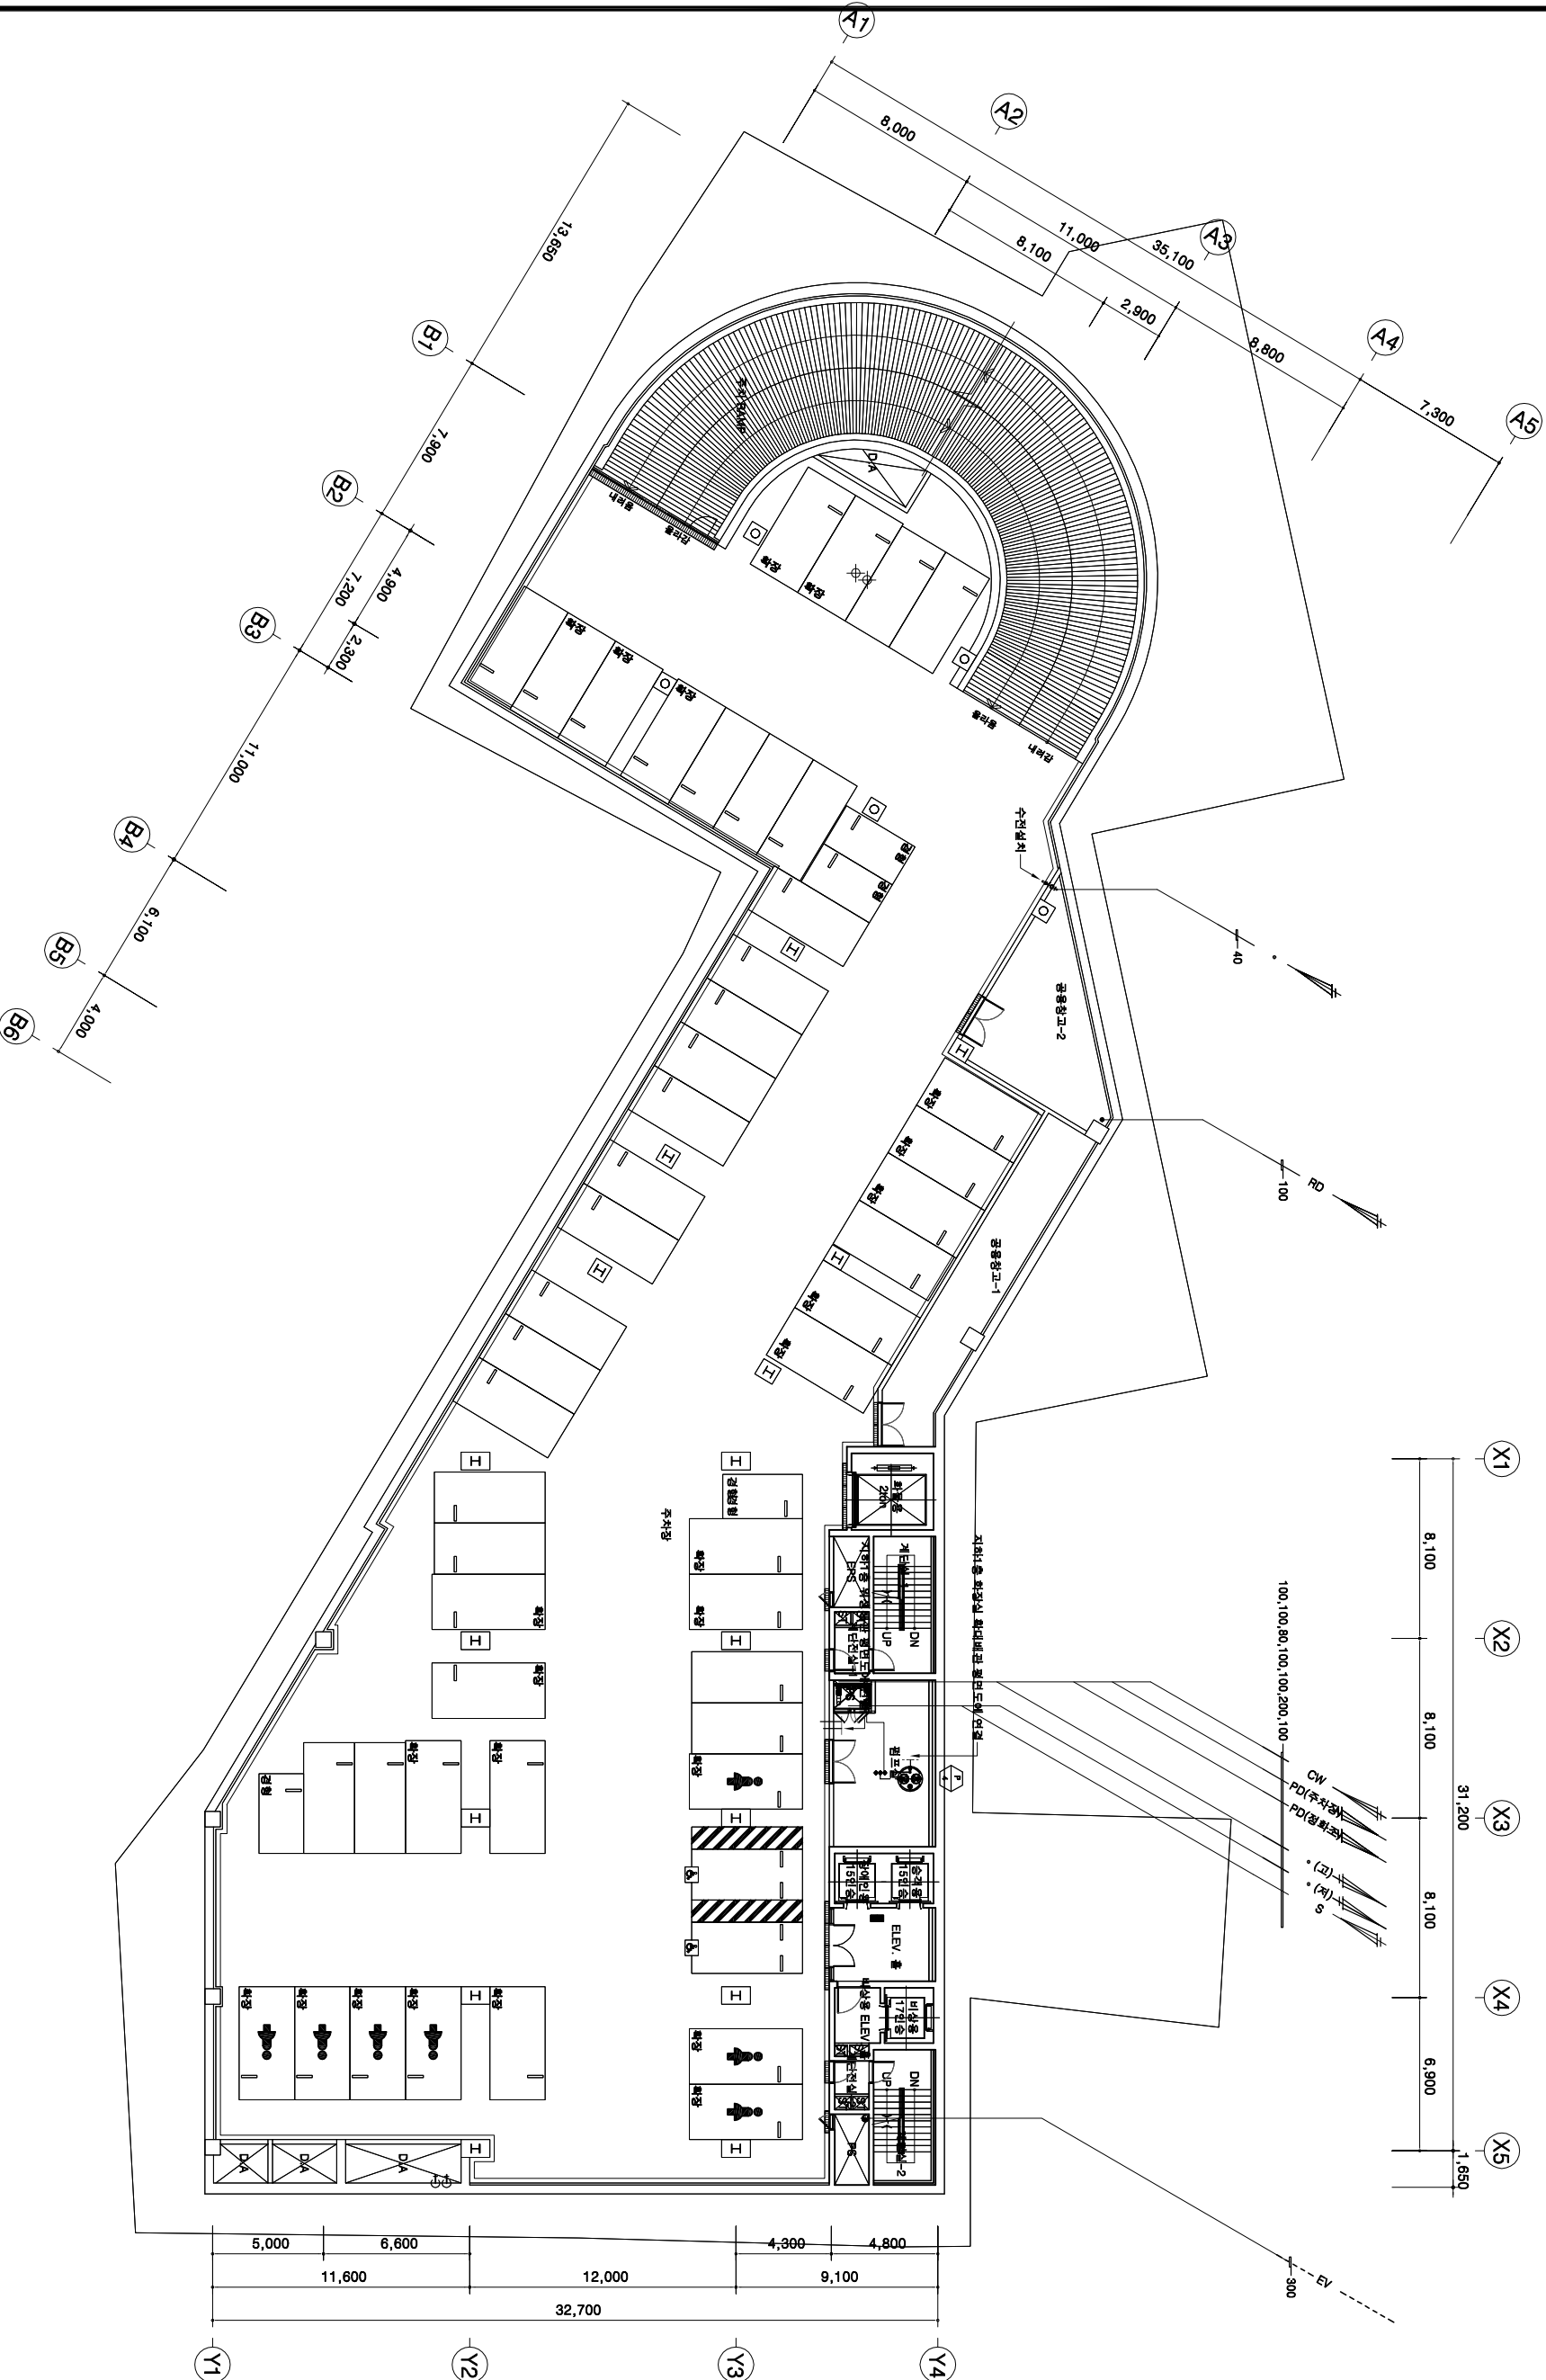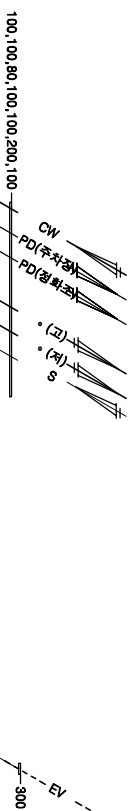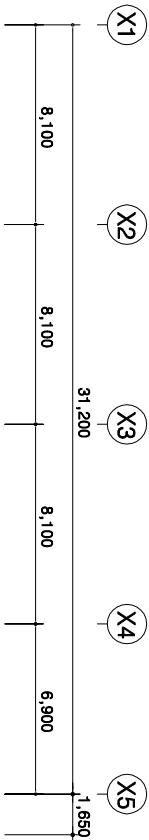

지하2층 위생배관 평면도

축척 : A1:1/150, A3:1/300

날짜	2014. 03
검리확인	
협조	
의견	
검토	
작성	


CHECKED	DATE
CONSULTANT	2014. 03
DRAWING NO.	M-204

REVISION	DESCRIPTION	DATE
ORDER ORIGIN		
INVESTMENT		
PROJECT OFFICE		
ARCHITECT		
DESIGNER		
DATE		

지하2층
위생배관 평면도

SCALE	APPROVED
A1 : 1 / 150	ARCHITECT
A3 : 1 / 300	DESIGNER
DATE	DATE
2014. 03	

성수동1가
지식산업센터
신축공사

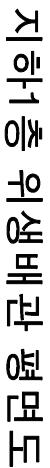

날		CHECKED	DATE	2014. 03
간리확인				
철		CONSULTANT		
진				
전				
기				
록				
의				
검 토 자		DRAWING NO.		
작성 자		M-205		


REASON	DESCRIPTION	DATE
ORDER ORGAN	VEN TURE	티라백창업에스트먼트 INVESTMENT
PROJECT ORIGIN	ATEC (주)에이텍종합건축사사무소	대표전화(02)932-4368 팩시밀리(02)932-4368
ARCHITECTS ASSOCIATES		대표전화(02)932-4368 팩시밀리(02)932-4368

성수동1가
지식산업센터
신축공사



SCALE	APPROVED
A1 : 1 / 150	ARCHITECT
A3 : 1 / 300	김상걸
DRAWN	DATE
하진태	2014. 03
CHECKED	DATE
CONSULTANT	2014. 03
DRAWING NO.	
M-206	

성수동1가
지식산업센터
신축공사

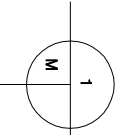

지상2층 위생배관 설치


속성 : A1:1/150, A3:1/300

날 짜	CHECKED	DATE	2014. 03
김리화인	CONSULTANT		
설 계			
검 토			
의 료			
검 토 자	DRAWING NO.		
자 성 장			
M-207			

PROJECT TITLE

성수동1가
지식산업센터
신축공사

NOTES

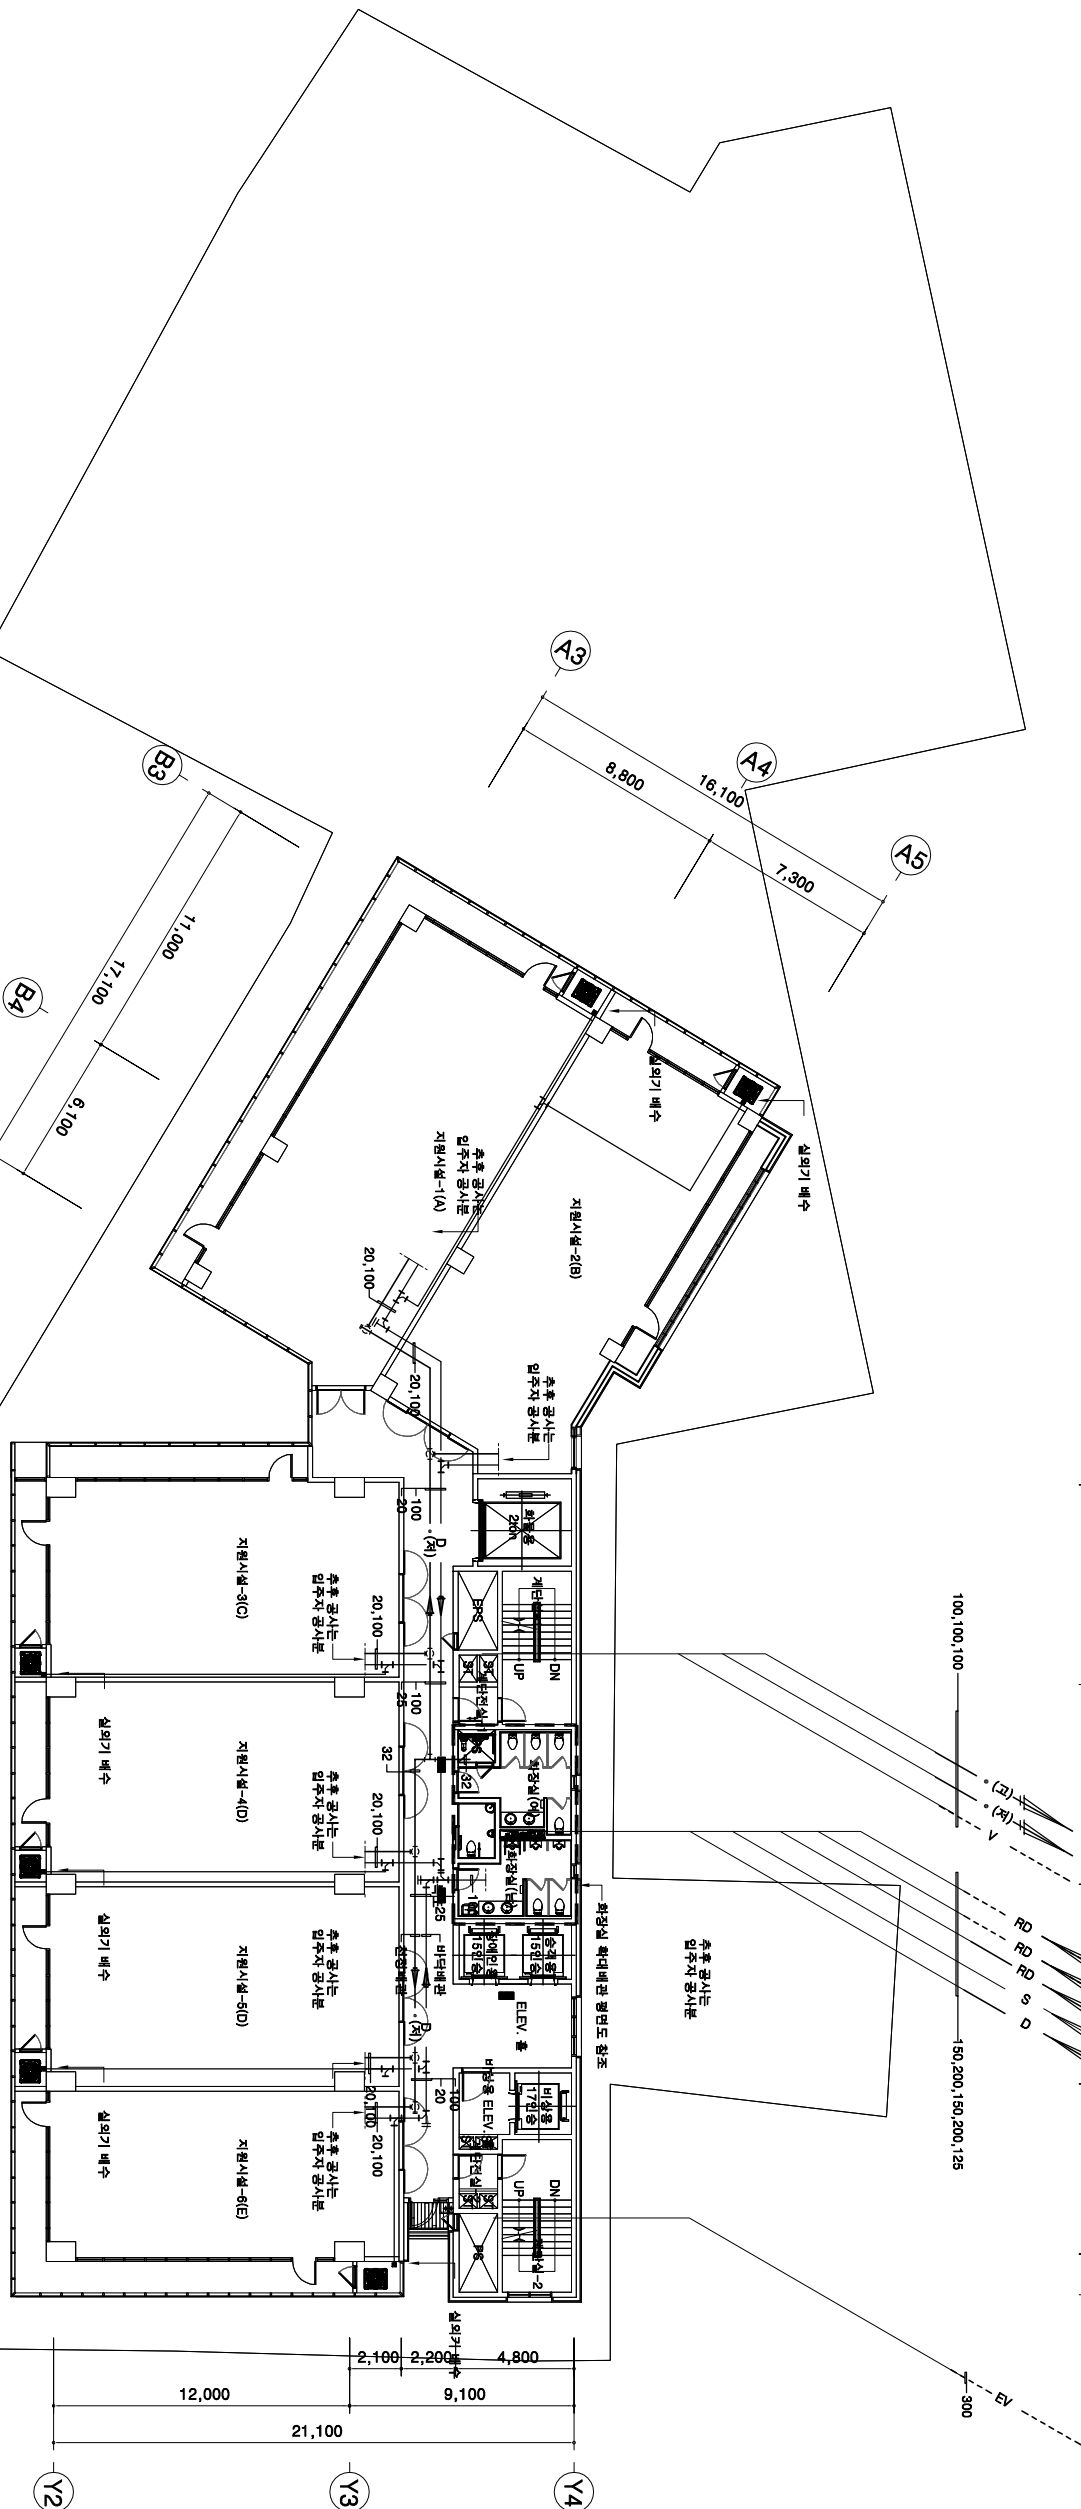

REVISION	DESCRIPTION	DATE
ORDER ORIGIN		
INVESTMENT	티티엘치인베스트먼트	대표전화(02)579-8381 팩시밀리(02)579-8384
PROJECT OFFICE	ATEC(주)에이텍종합건축사사무소	대표전화(02)5482-6396 팩시밀리(02)5482-6392
DRAWING TITLE	지상3층 위생배관 평면도	

SCALE	APPROVED
A1 : 1 / 150	ARCHITECT
A3 : 1 / 300	김상길
DRAWN	DATE
하진태	2014. 03

CHECKED	DATE
김리현인	2014. 03
CONSULTANT	
DRIVING NO.	M-208

지상3층 위생배관 평면도


축척 : A1:1/150, A3:1/300

날짜	확인
검토	확인
의견	확인
검토	확인
작성	확인

PROJECT TITLE

성수동1가
지식산업센터
신축공사

NOTES

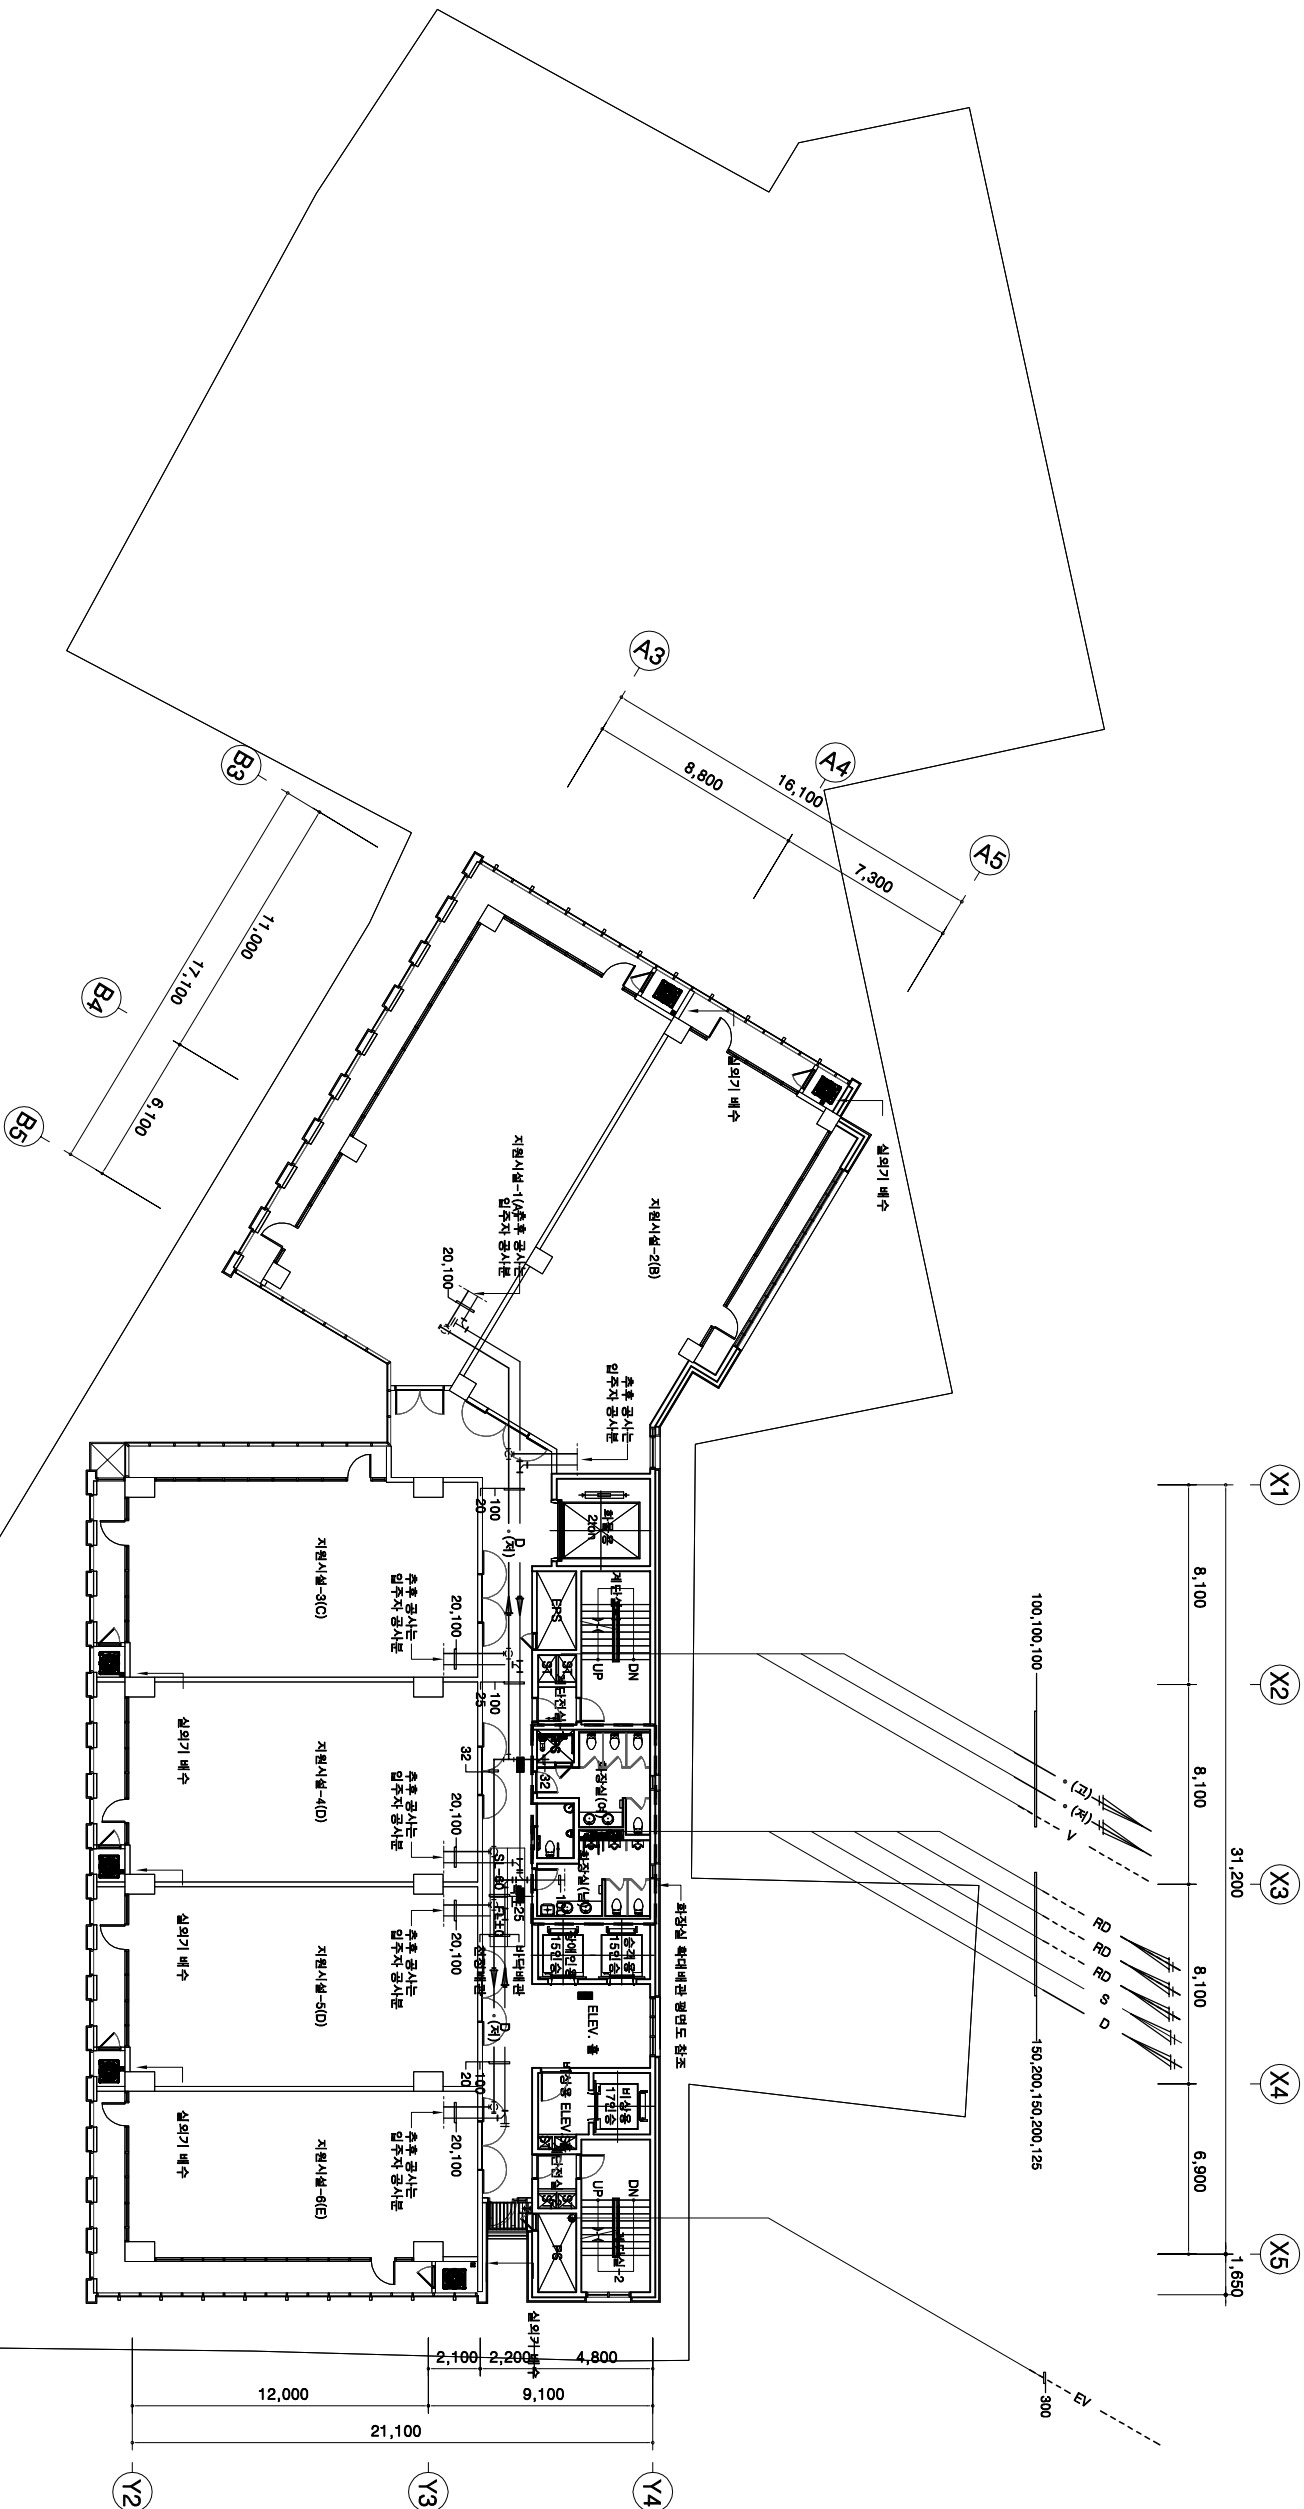

ORDER ORGAN
INVESTMENT
PROJECT OFFICE
ARCHITECTS
DRAWING TITLE

SCALE
A1 : 1 / 150
A3 : 1 / 300
DRAWN
DATE

CHECKED
DATE
CONSULTANT
DRAWING NO.
M-209

지상4층 위생배관 평면도


축척 : A1:1/150, A3:1/300

남	쪽
관리	확인
설	계
의	토
목	록
검	토
정	자

PROJECT TITLE

성수동1가
지식산업센터
신축공사



NOTES

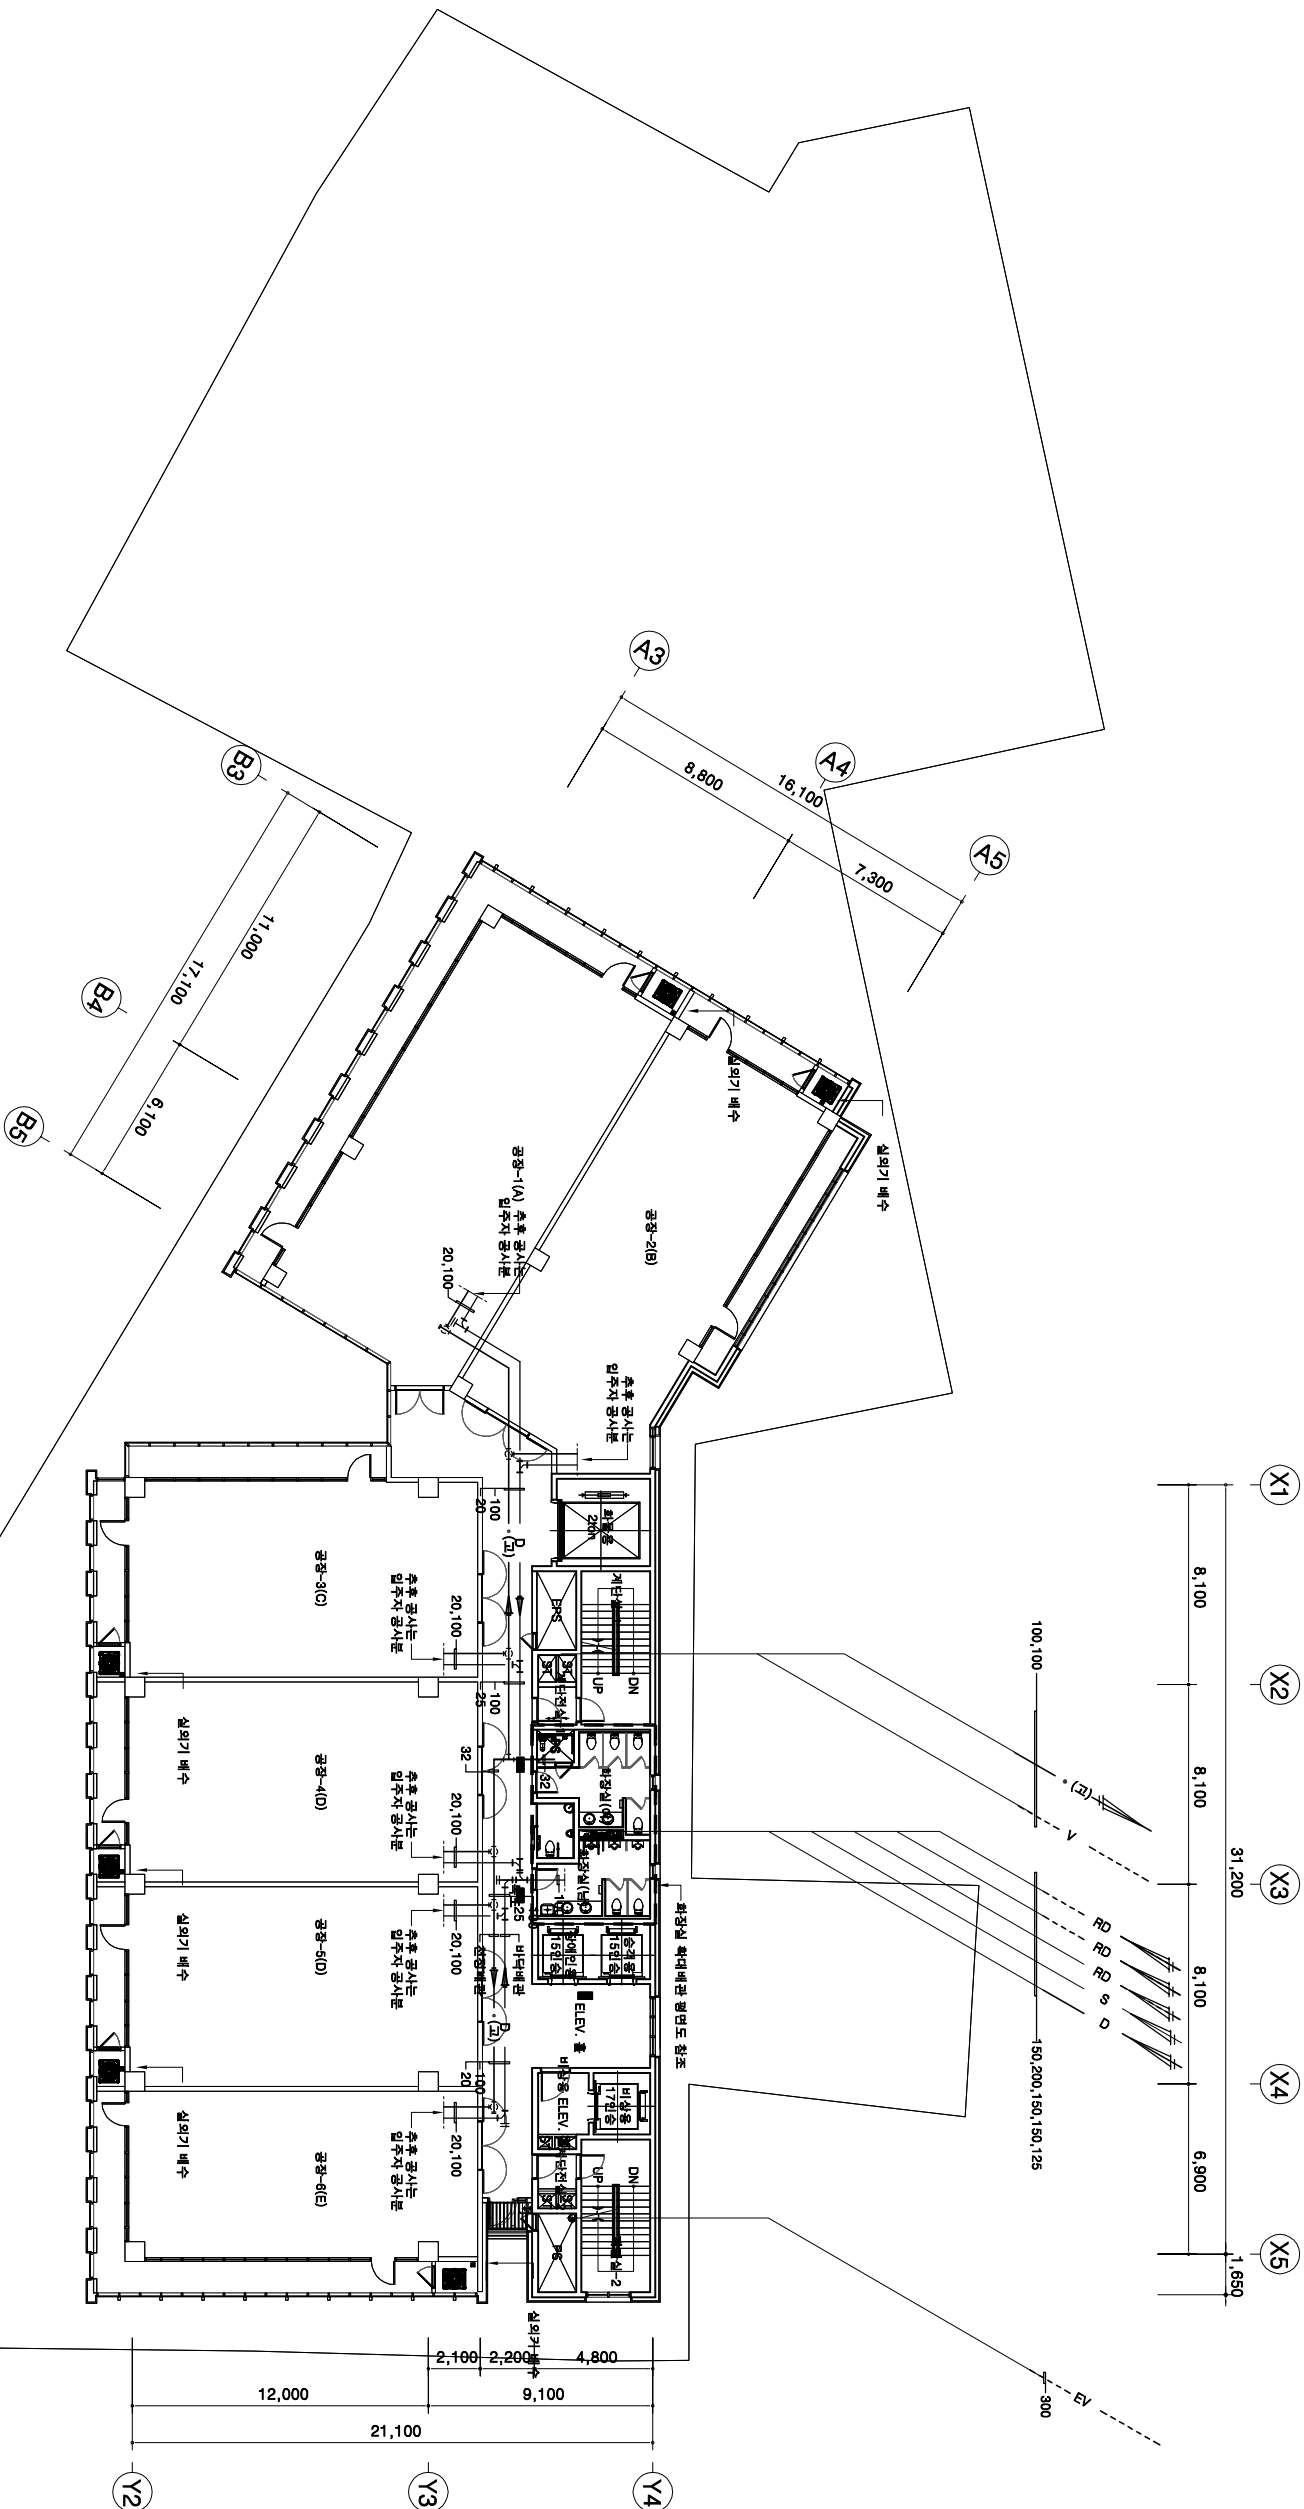

지상8~10층
위생배관 평면도

SCALE		APPROVED	
A1 : 1 / 150	ARCHITECT	김상길	
A3 : 1 / 300	DATE		
하진태	2014. 03		



CHECKED	DATE	2014. 03
CONSULTANT		
DRAWING NO.		M-211

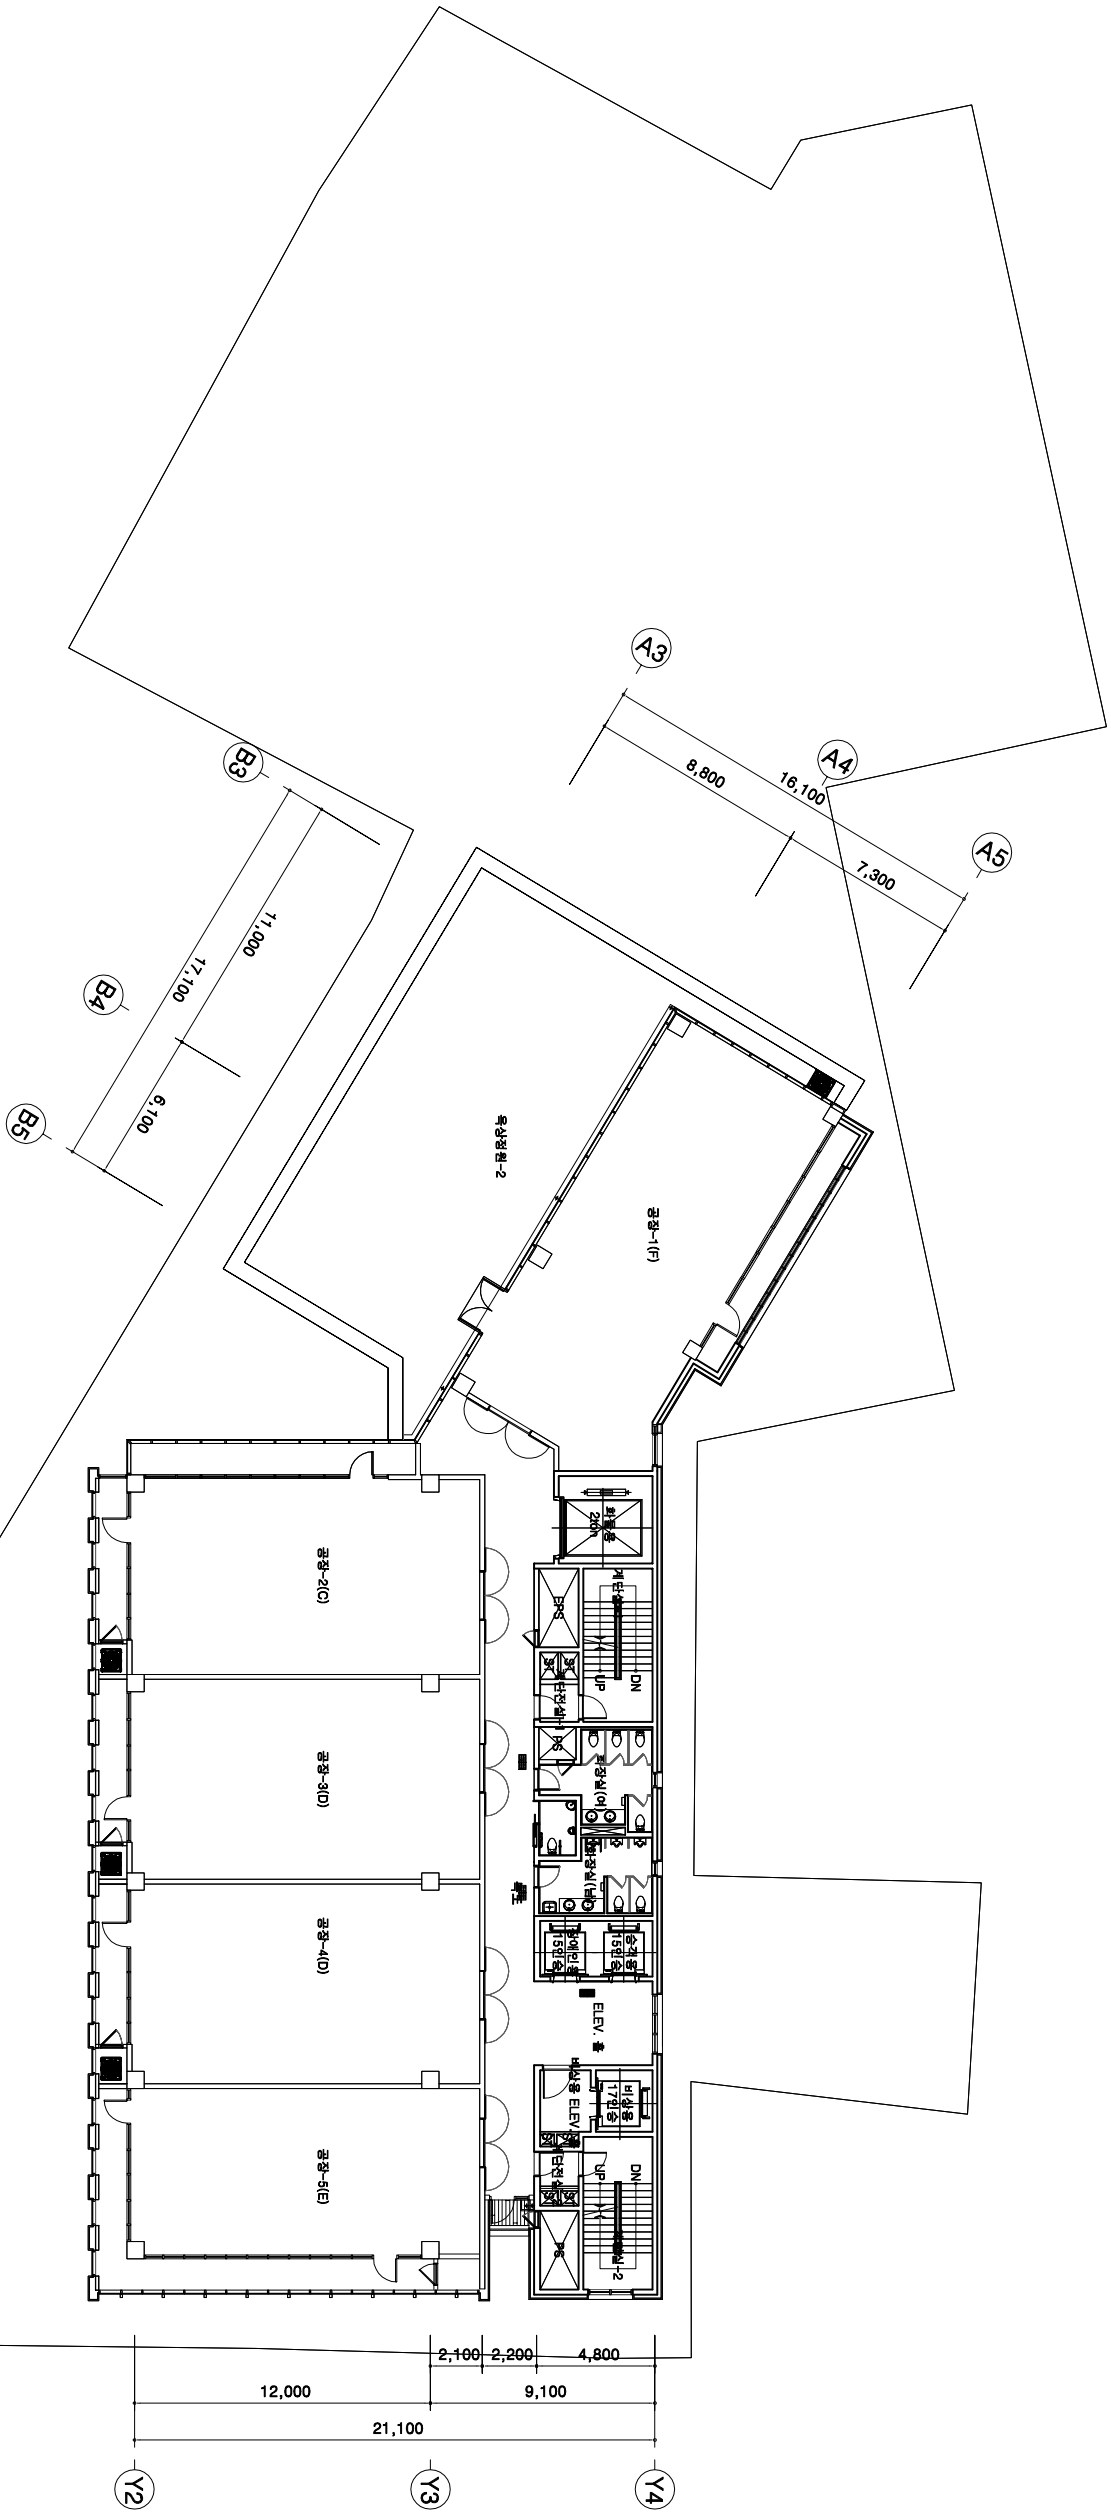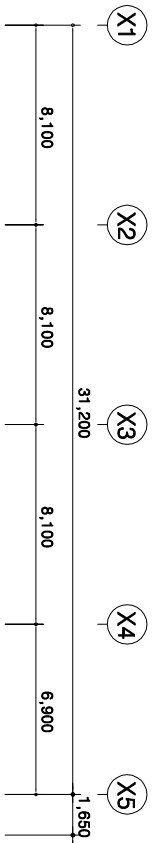

PROJECT TITLE

성수동1가
지식산업센터
신축공사

NOTES

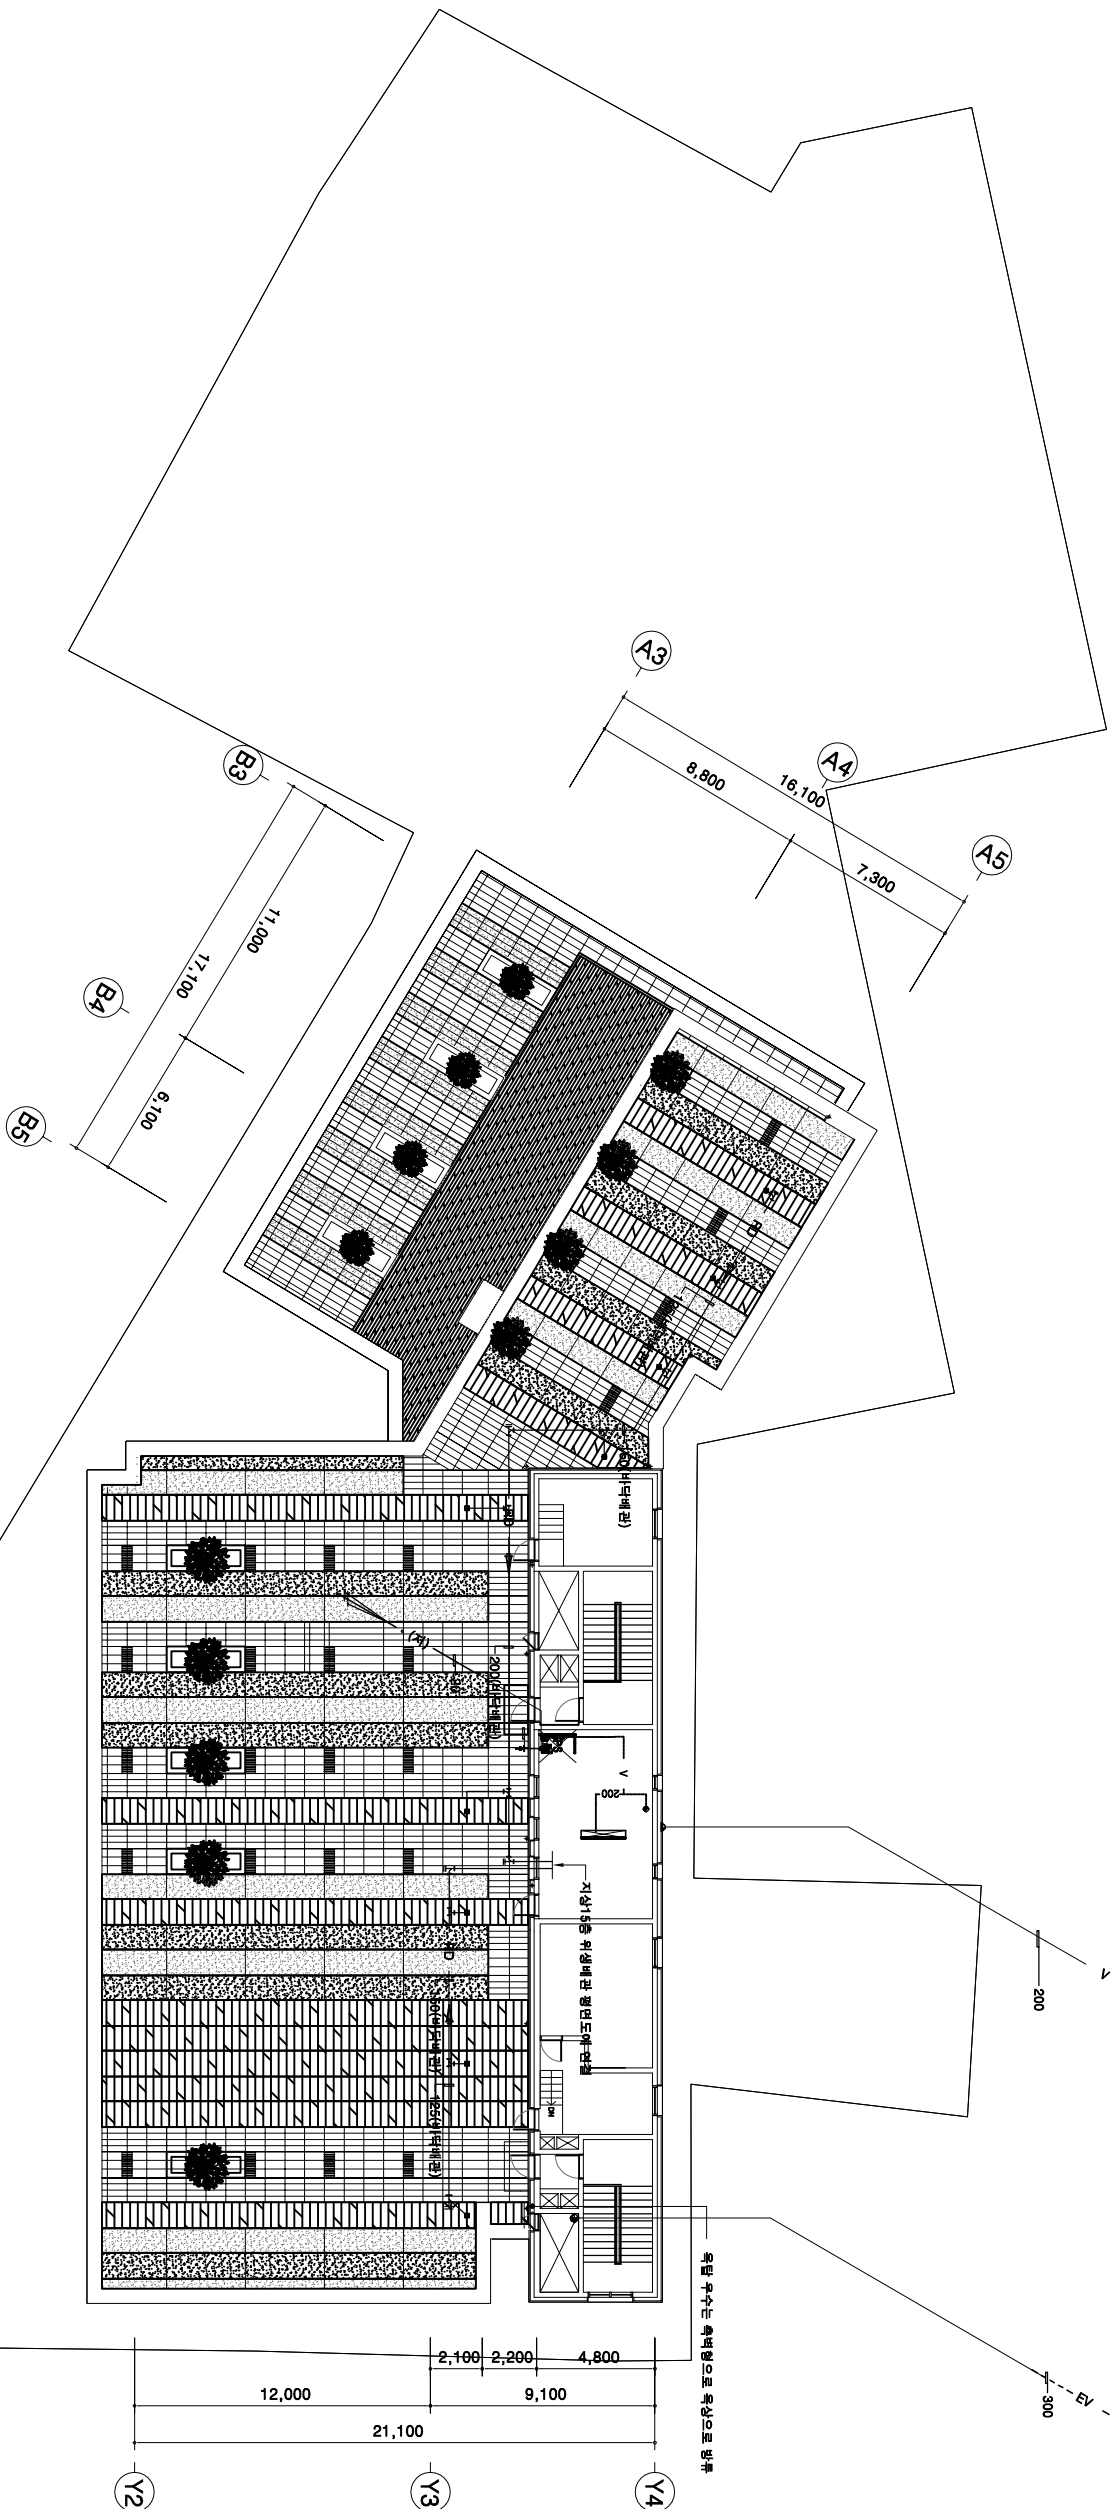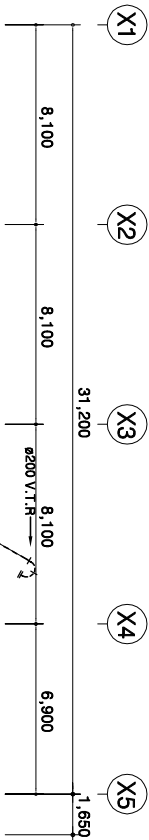

옥탑층 위생배관 평면도

축척 : A1:1/150, A3:1/300

날 짜	
검리확인	
협 건 측	
의 전 기	
의 토 목	
검 토 자	
작 성 자	

DRAWING NO.
M-215

옥탑층
위생배관 평면도

SCALE	A1 : 1 / 150 A3 : 1 / 300
ARCHITECT	김 상 결
DATE	2014. 03

PROJECT OFFICE
ATEC (주)에이텍종합건축사사무소
ARCHITECTS
대표전화(02)3402-6399
팩시밀리(02)3402-6392

INVESTMENT
TENTURE
티티벤처인베스트먼트
대표전화(02)579-8381
팩시밀리(02)579-8384

ORDER ORIGIN
DESCRIPTION
DATE

REVISION
DATE

DATE

DATE