


PROJECT TITLE

성수동1가
지식산업센터
신축공사

NOTES

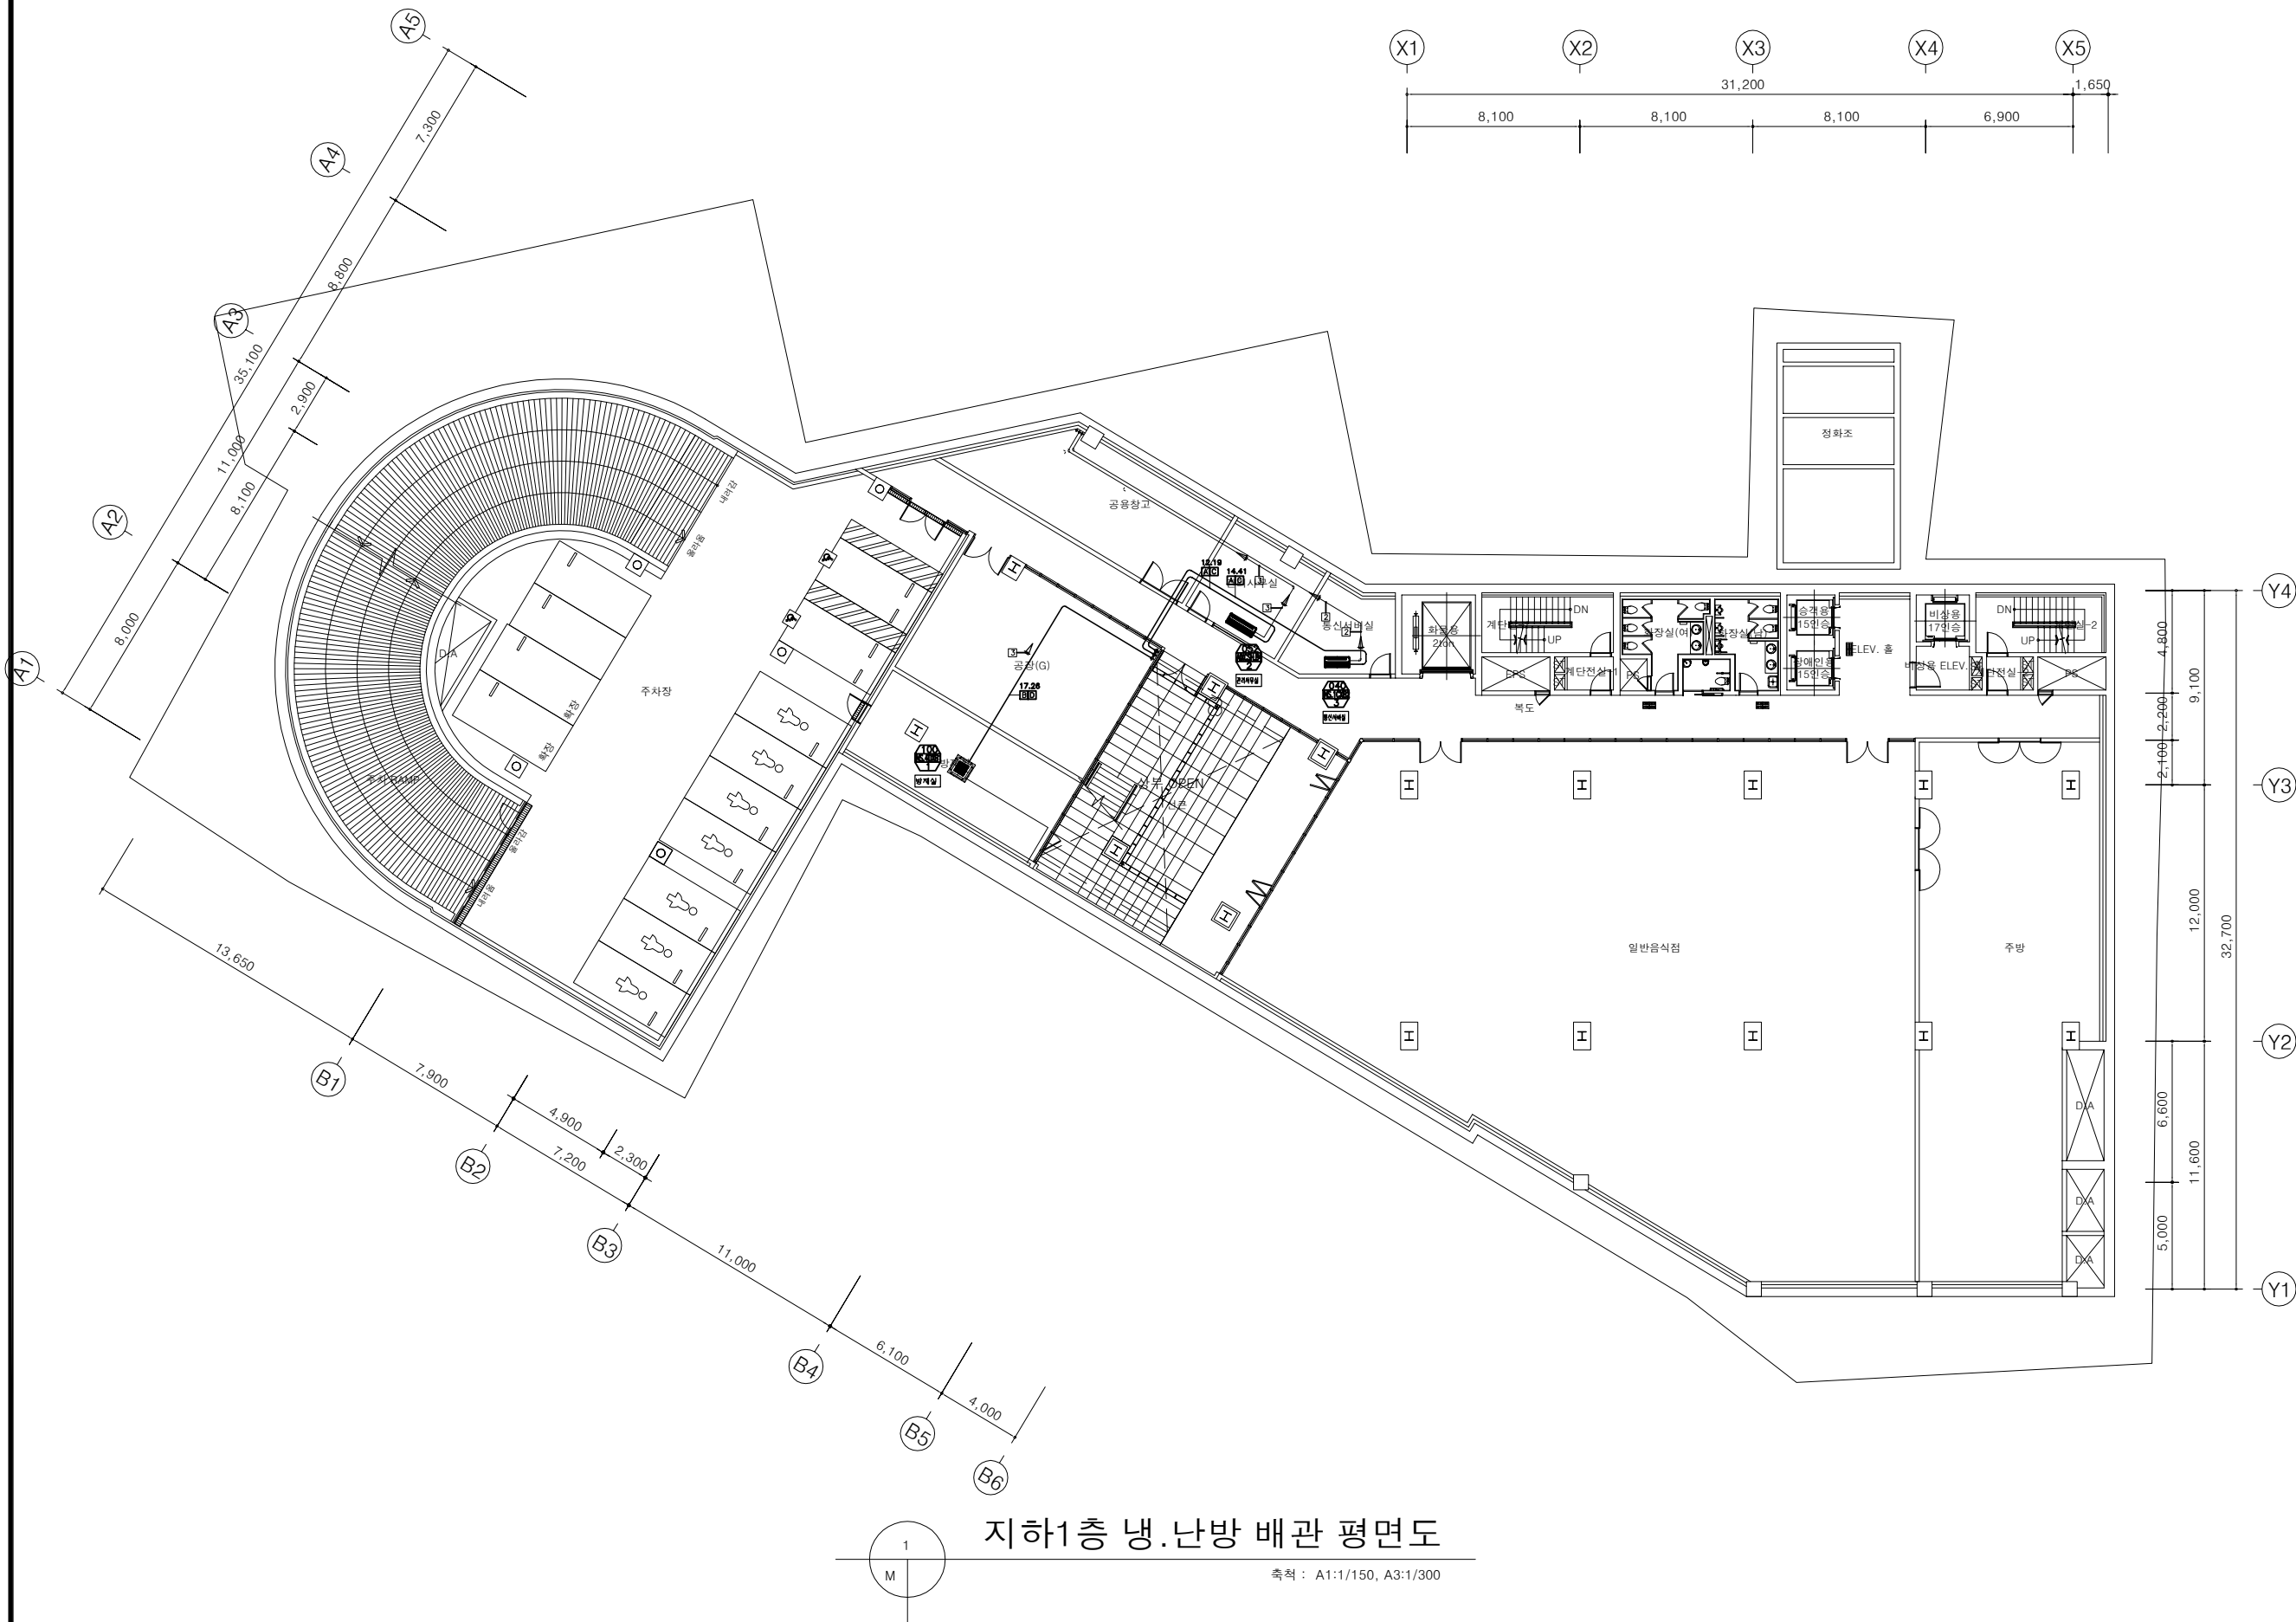

지하1층 냉.난방 배관 평면도

축척 : A1:1/150, A3:1/300

REVISION	DESCRIPTION	DATE


ORDER ORGAN
TT 티티벤처인베스트먼트
INVESTMENT
대표전화(02)579-8361
팩시밀리(02)579-8364
PROJECT OFFICE
ATEC 에이텍종합건축사사무소
ARCHITECTS & ASSOCIATES
대표전화(02)3462-6361
팩시밀리(02)3462-6362

DRAWING TITLE
지하1층
냉.난방배관 평면도

SCALE A1 : 1 / 150 A3 : 1 / 300	APPROVED ARCHITECT 김 상 길
DRAWN 하 진 태	DATE 2014. 03
CHECKED	DATE 2014. 03

CONSULTANT

DRAWING NO.
M-301

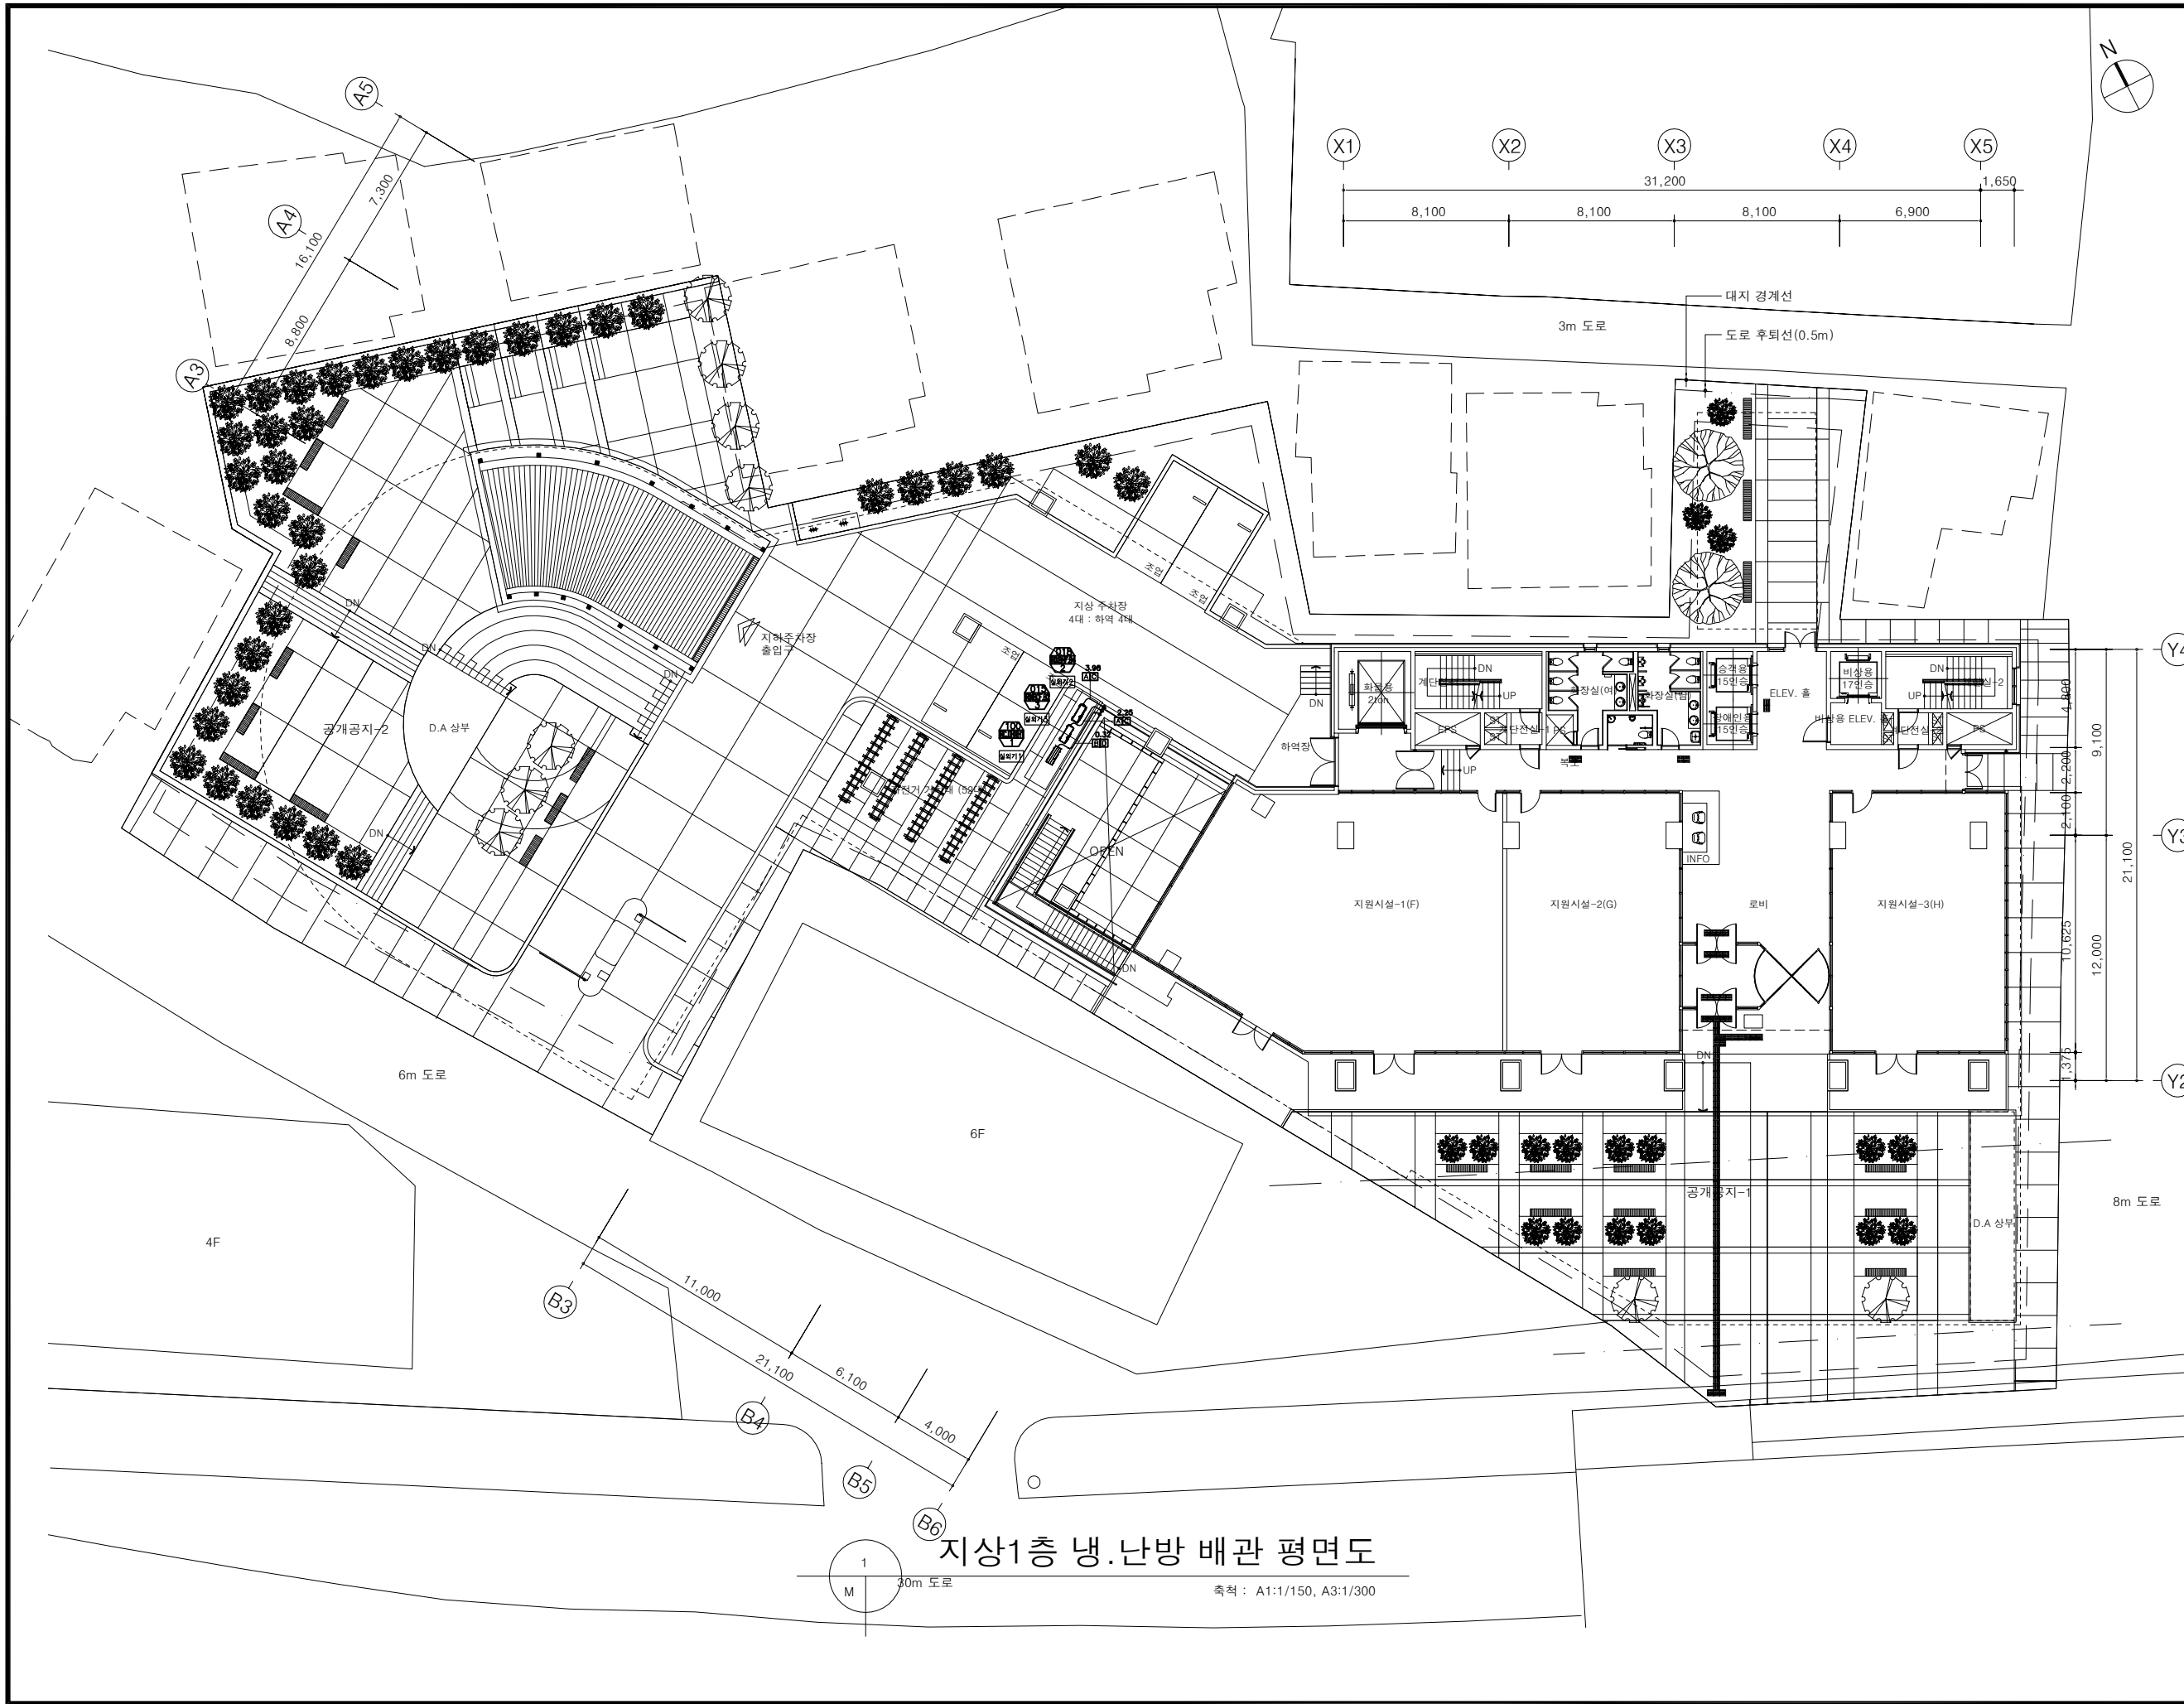

PROJECT TITLE

성수동1가
지식산업센터
신축공사

NOTES

REVISION	DESCRIPTION	DATE

ORDER ORGAN

INVESTMENT

PROJECT OFFICE

ARCHITECTS & ASSOCIATES

티티벤처인베스트먼트

대표전화(02)579-8361
팩시밀리(02)579-8364

에이텍종합건축사사무소

대표전화(02)3462-6361
팩시밀리(02)3462-6362

DRAWING TITLE

지상1층
냉.난방배관 평면도

SCALE	APPROVED
A1 : 1 / 150 A3 : 1 / 300	ARCHITECT 김 상 길
DRAWN 하 진 태	DATE 2014. 03
CHECKED	DATE 2014. 03
CONSULTANT	

DRAWING NO.

M-302