


PROJECT TITLE

성수동1가
지식산업센터
신축공사

NOTES

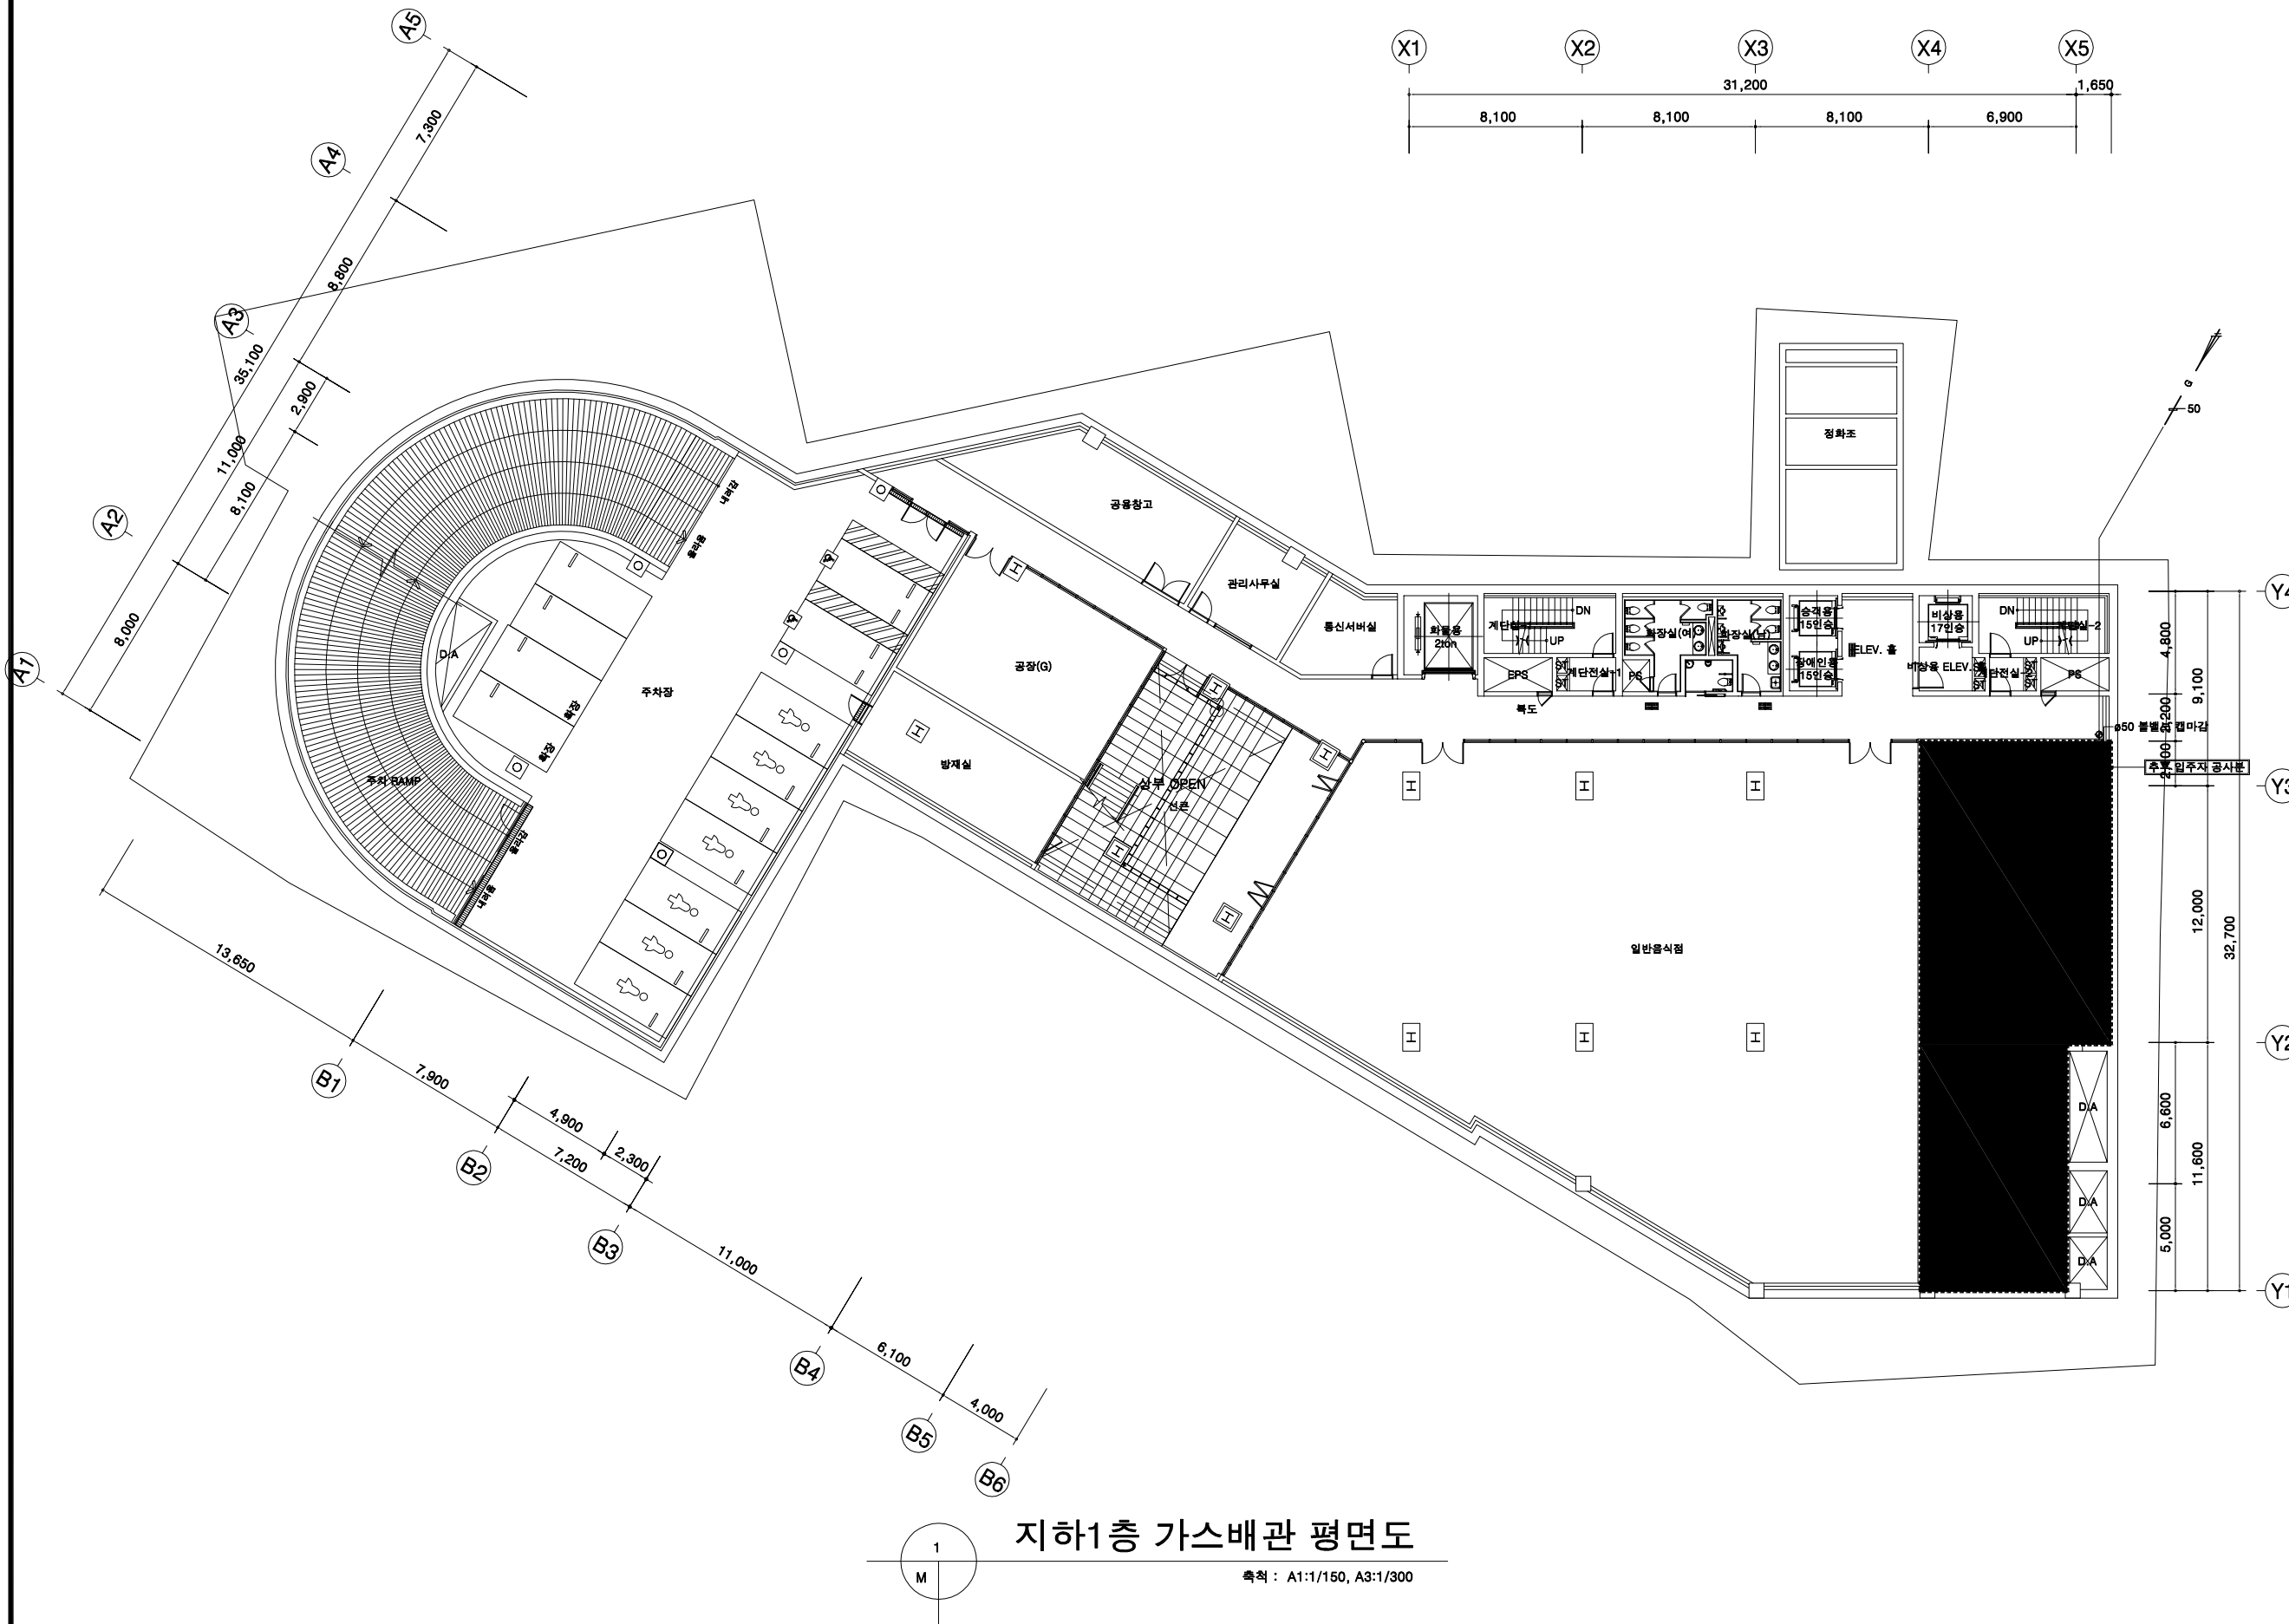

지하1층 가스배관 평면도

축척 : A1:1/150, A3:1/300

REVISION DESCRIPTION DATE

ORDER ORGAN

INVESTMENT TIT VENTURE
대표전화(02)579-8361
팩시밀리(02)579-8364

PROJECT OFFICE

ATEC (주)에이텍종합건축사사무소
ARCHITECTS & ASSOCIATES
대표전화(02)3462-6361
팩시밀리(02)3462-6362

DRAWING TITLE

지하1층
가스배관 평면도

SCALE

A1 : 1 / 150
A3 : 1 / 300

DRAWN

하진태

CHECKED


DATE

2014. 03

CONSULTANT

DRAWING NO.

M-401

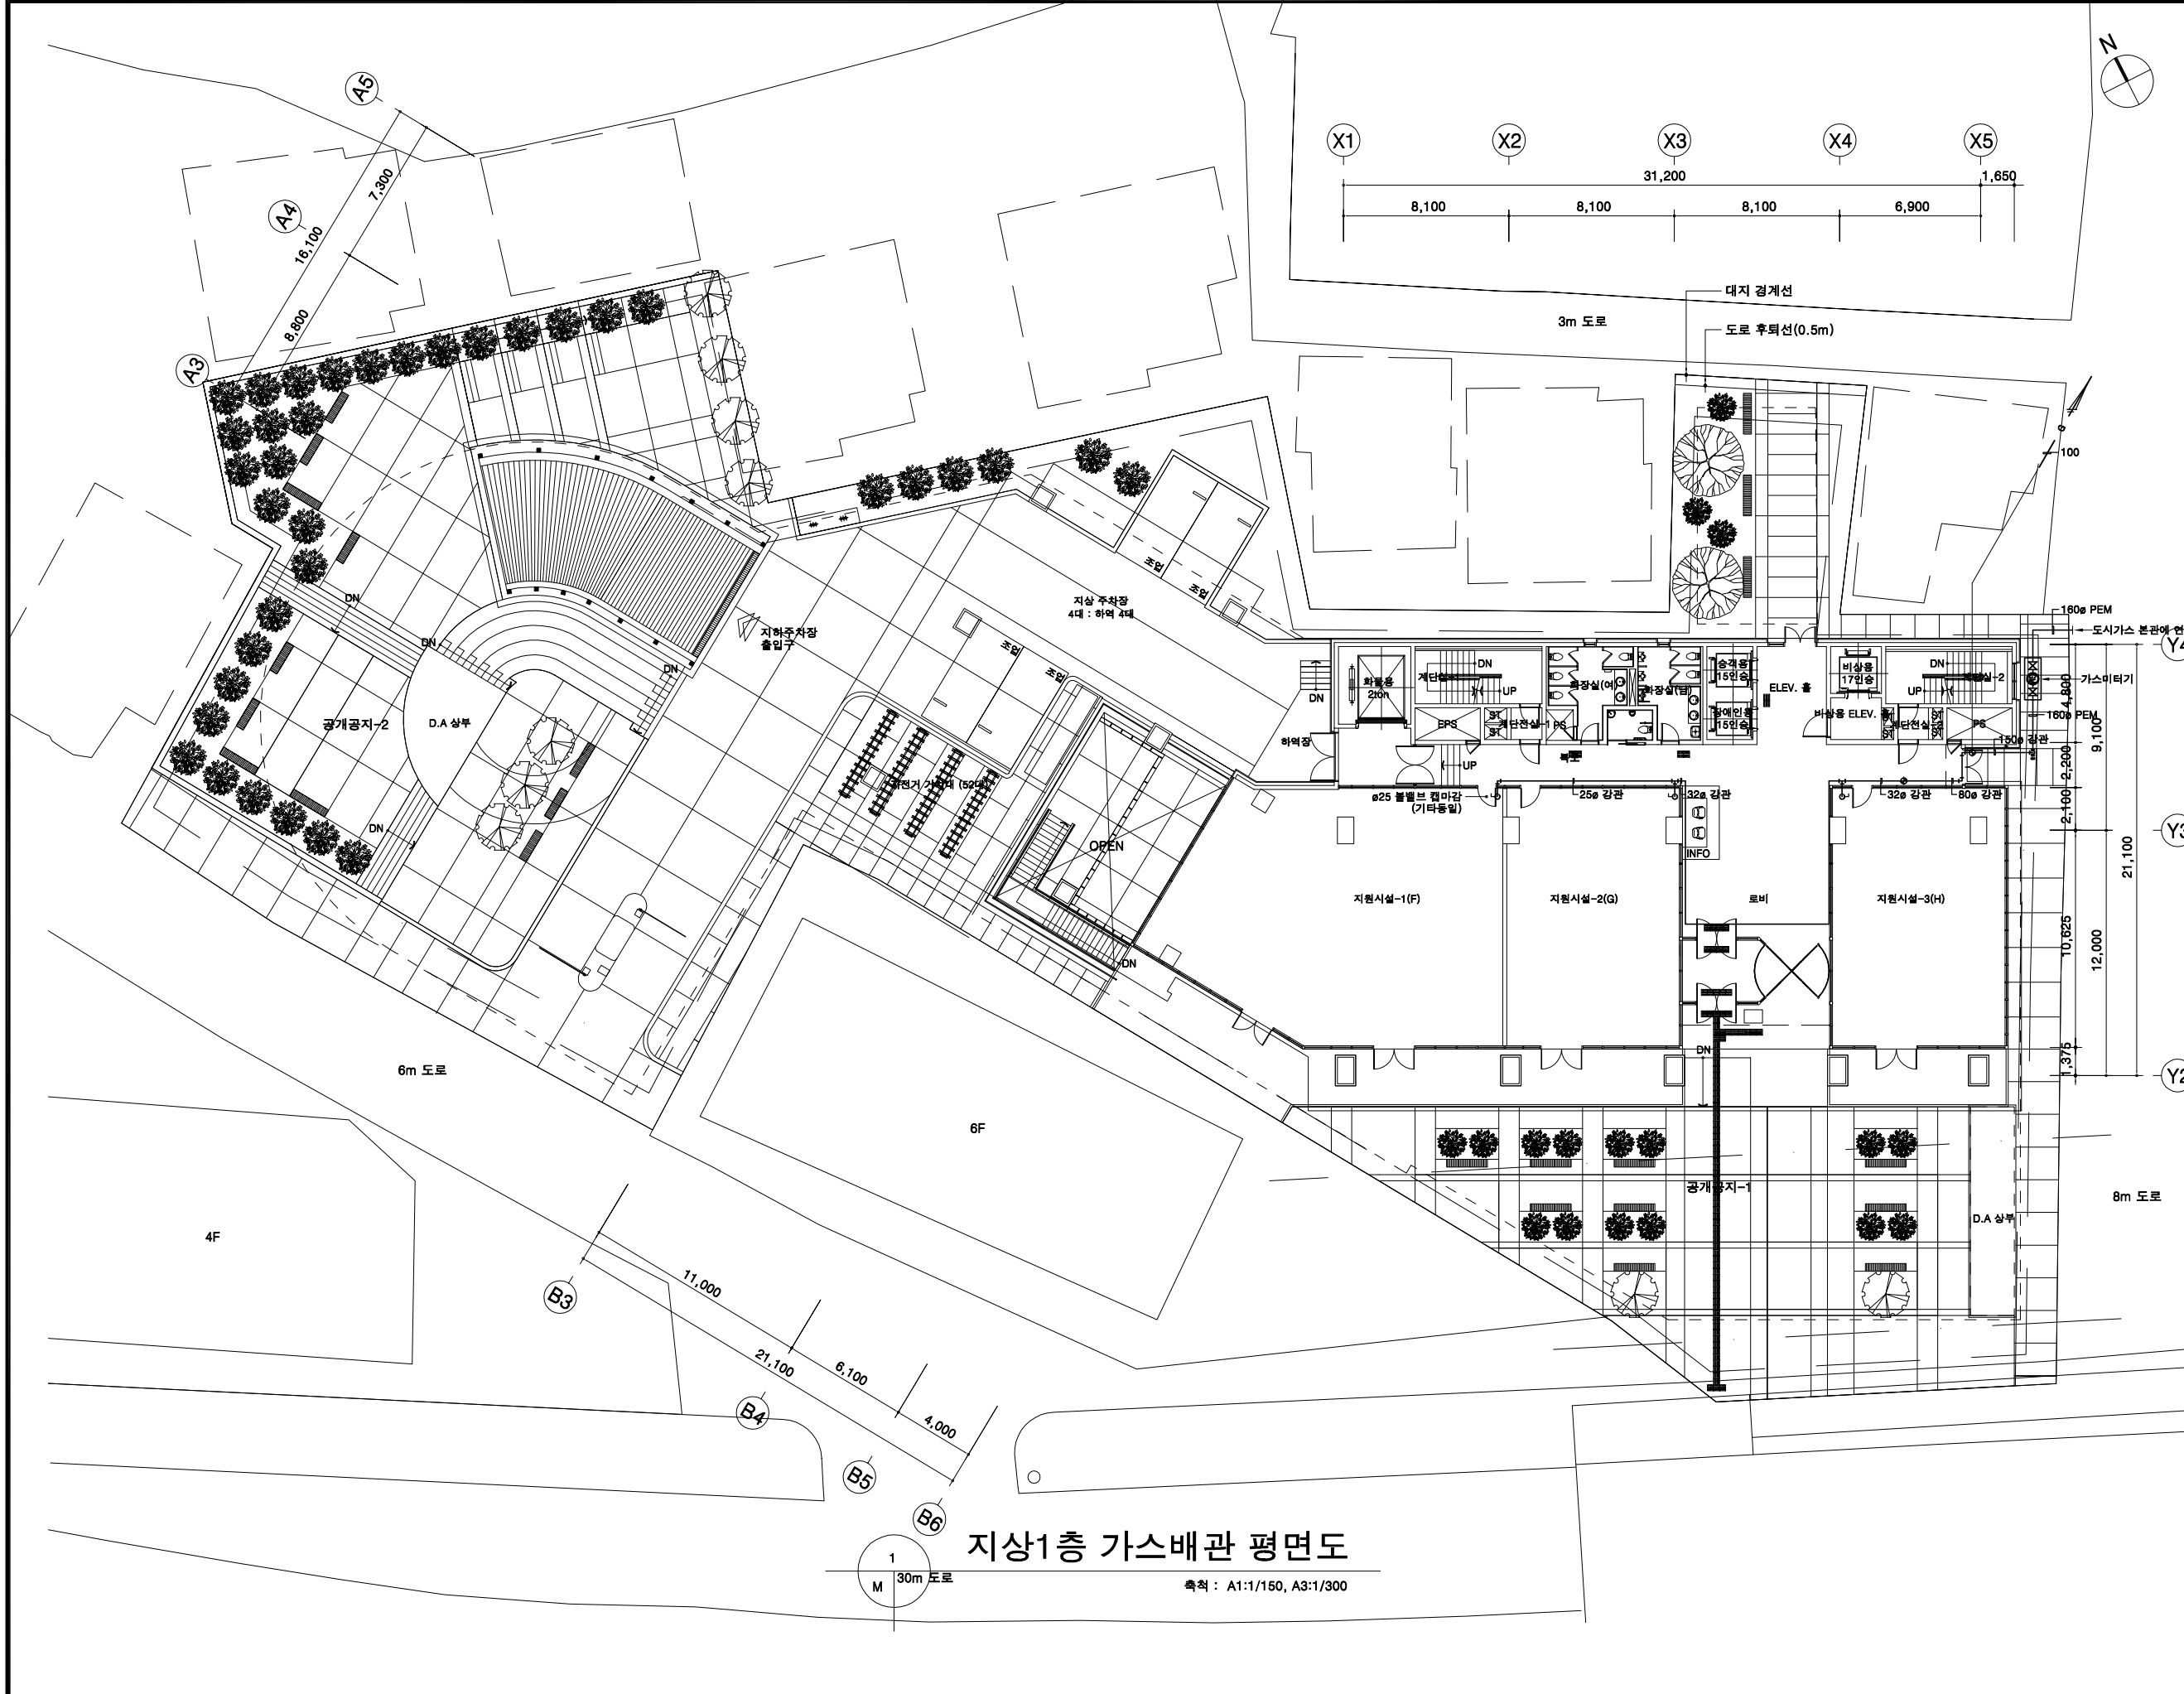

PROJECT TITLE
**성수동1가
지식산업센터
신축공사**

NOTES

REVISION	DESCRIPTION	DATE

ORDER ORGAN
T T
INVESTMENT
대표전화(02)579-8361
팩시밀리(02)579-8364
PROJECT OFFICE
ATEC (주)에이텍종합건축사사무소
ARCHITECTS & ASSOCIATES
대표전화(02)3462-6361
팩시밀리(02)3462-6362

DRAWING TITLE
**지상1층
가스배관 평면도**



SCALE A1 : 1 / 150 A3 : 1 / 300	APPROVED ARCHITECT 김 상 길
DRAWN 하 진 태	DATE 2014. 03
CHECKED	DATE 2014. 03
CONSULTANT	

DRAWING NO.
M-402

PROJECT TITLE

성수동1가
지식산업센터
신축공사

NOTES

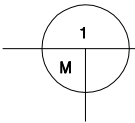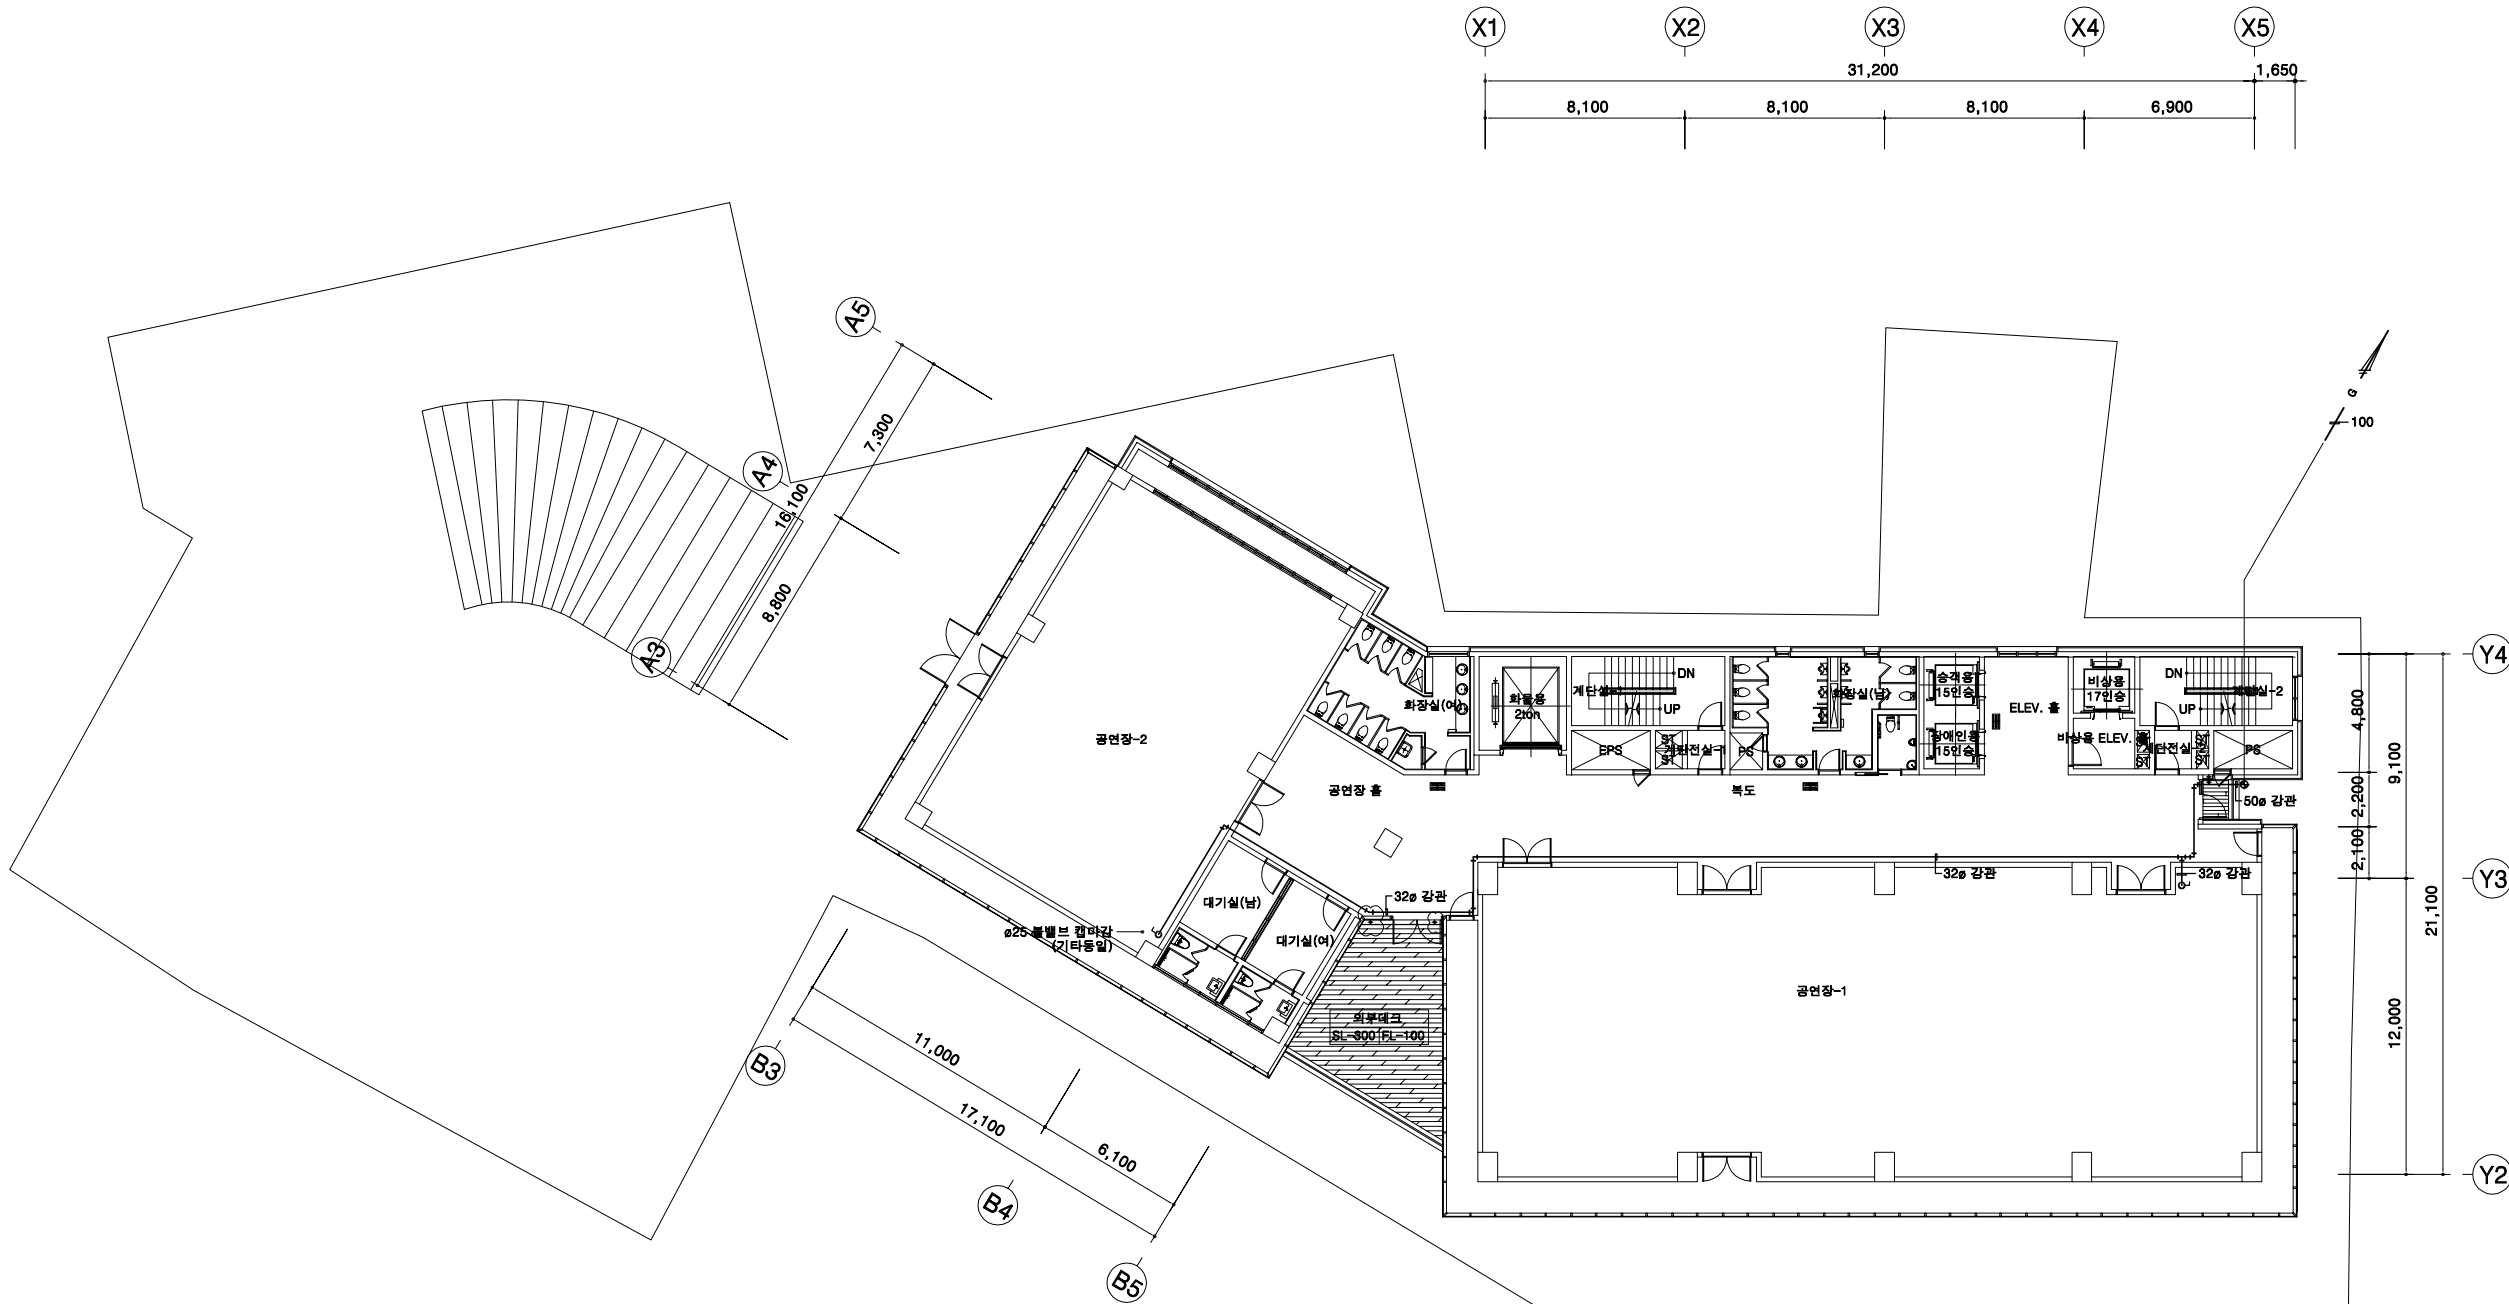

지상2층 가스배관 평면도

축척 : A1:1/150, A3:1/300

REVISION DESCRIPTION DATE

ORDER ORGAN

INVESTMENT TIT VENTURE 대표전화(02)579-8361
팩시밀리(02)579-8364

PROJECT OFFICE

ATEC(주)에이텍종합건축사사무소 대표전화(02)3462-6361
팩시밀리(02)3462-6362

DRAWING TITLE

지상2층
가스배관 평면도

SCALE

A1 : 1 / 150
A3 : 1 / 300

APPROVED ARCHITECT 김 상 길

DRAWN 하 진 태

DATE 2014. 03

CHECKED

DATE 2014. 03

CONSULTANT



DRAWING NO.

M-403

PROJECT TITLE

성수동1가
지식산업센터
신축공사

NOTES

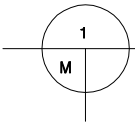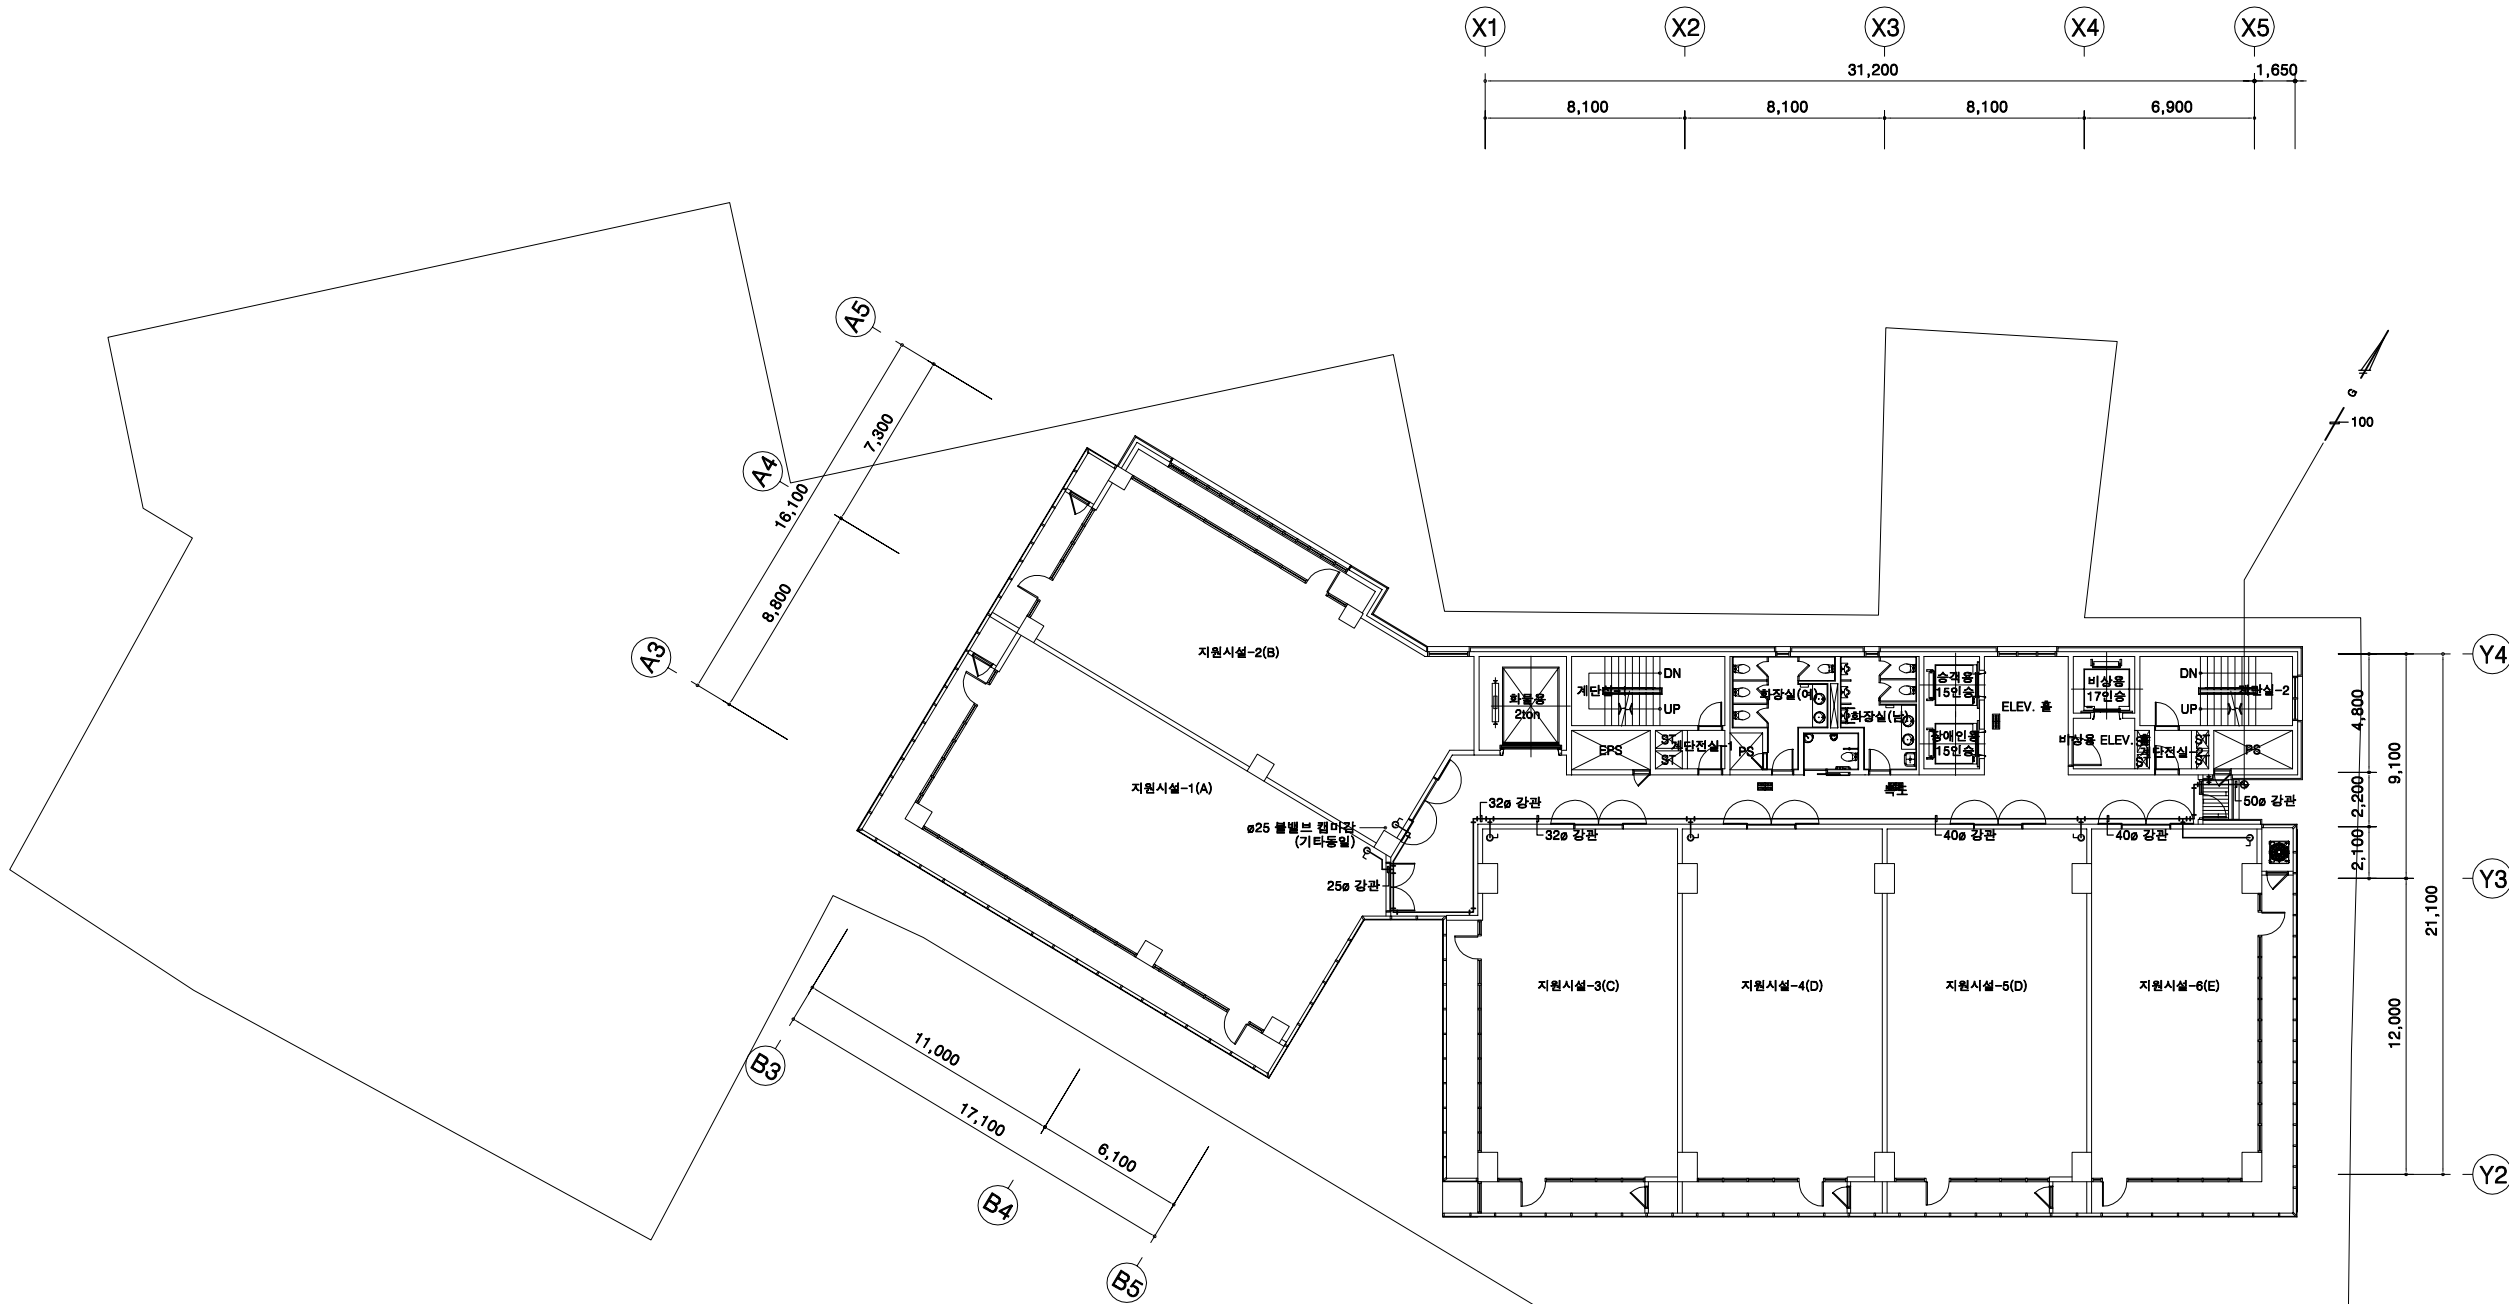

지상3층 가스배관 평면도

축척 : A1:1/150, A3:1/300

REVISION DESCRIPTION DATE

ORDER ORGAN

INVESTMENT TIT VENTURE 대표전화(02)579-8361
팩시밀리(02)579-8364

PROJECT OFFICE

ATEC (주)에이텍종합건축사사무소 대표전화(02)3462-6361
팩시밀리(02)3462-6362

DRAWING TITLE

지상3층
가스배관 평면도

SCALE

A1 : 1 / 150
A3 : 1 / 300

APPROVED

ARCHITECT 김 상 길

DRAWN 하 진 태

DATE 2014. 03

CHECKED

DATE 2014. 03

CONSULTANT



DRAWING NO.

M-404

PROJECT TITLE

성수동1가
지식산업센터
신축공사

NOTES

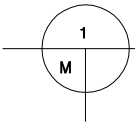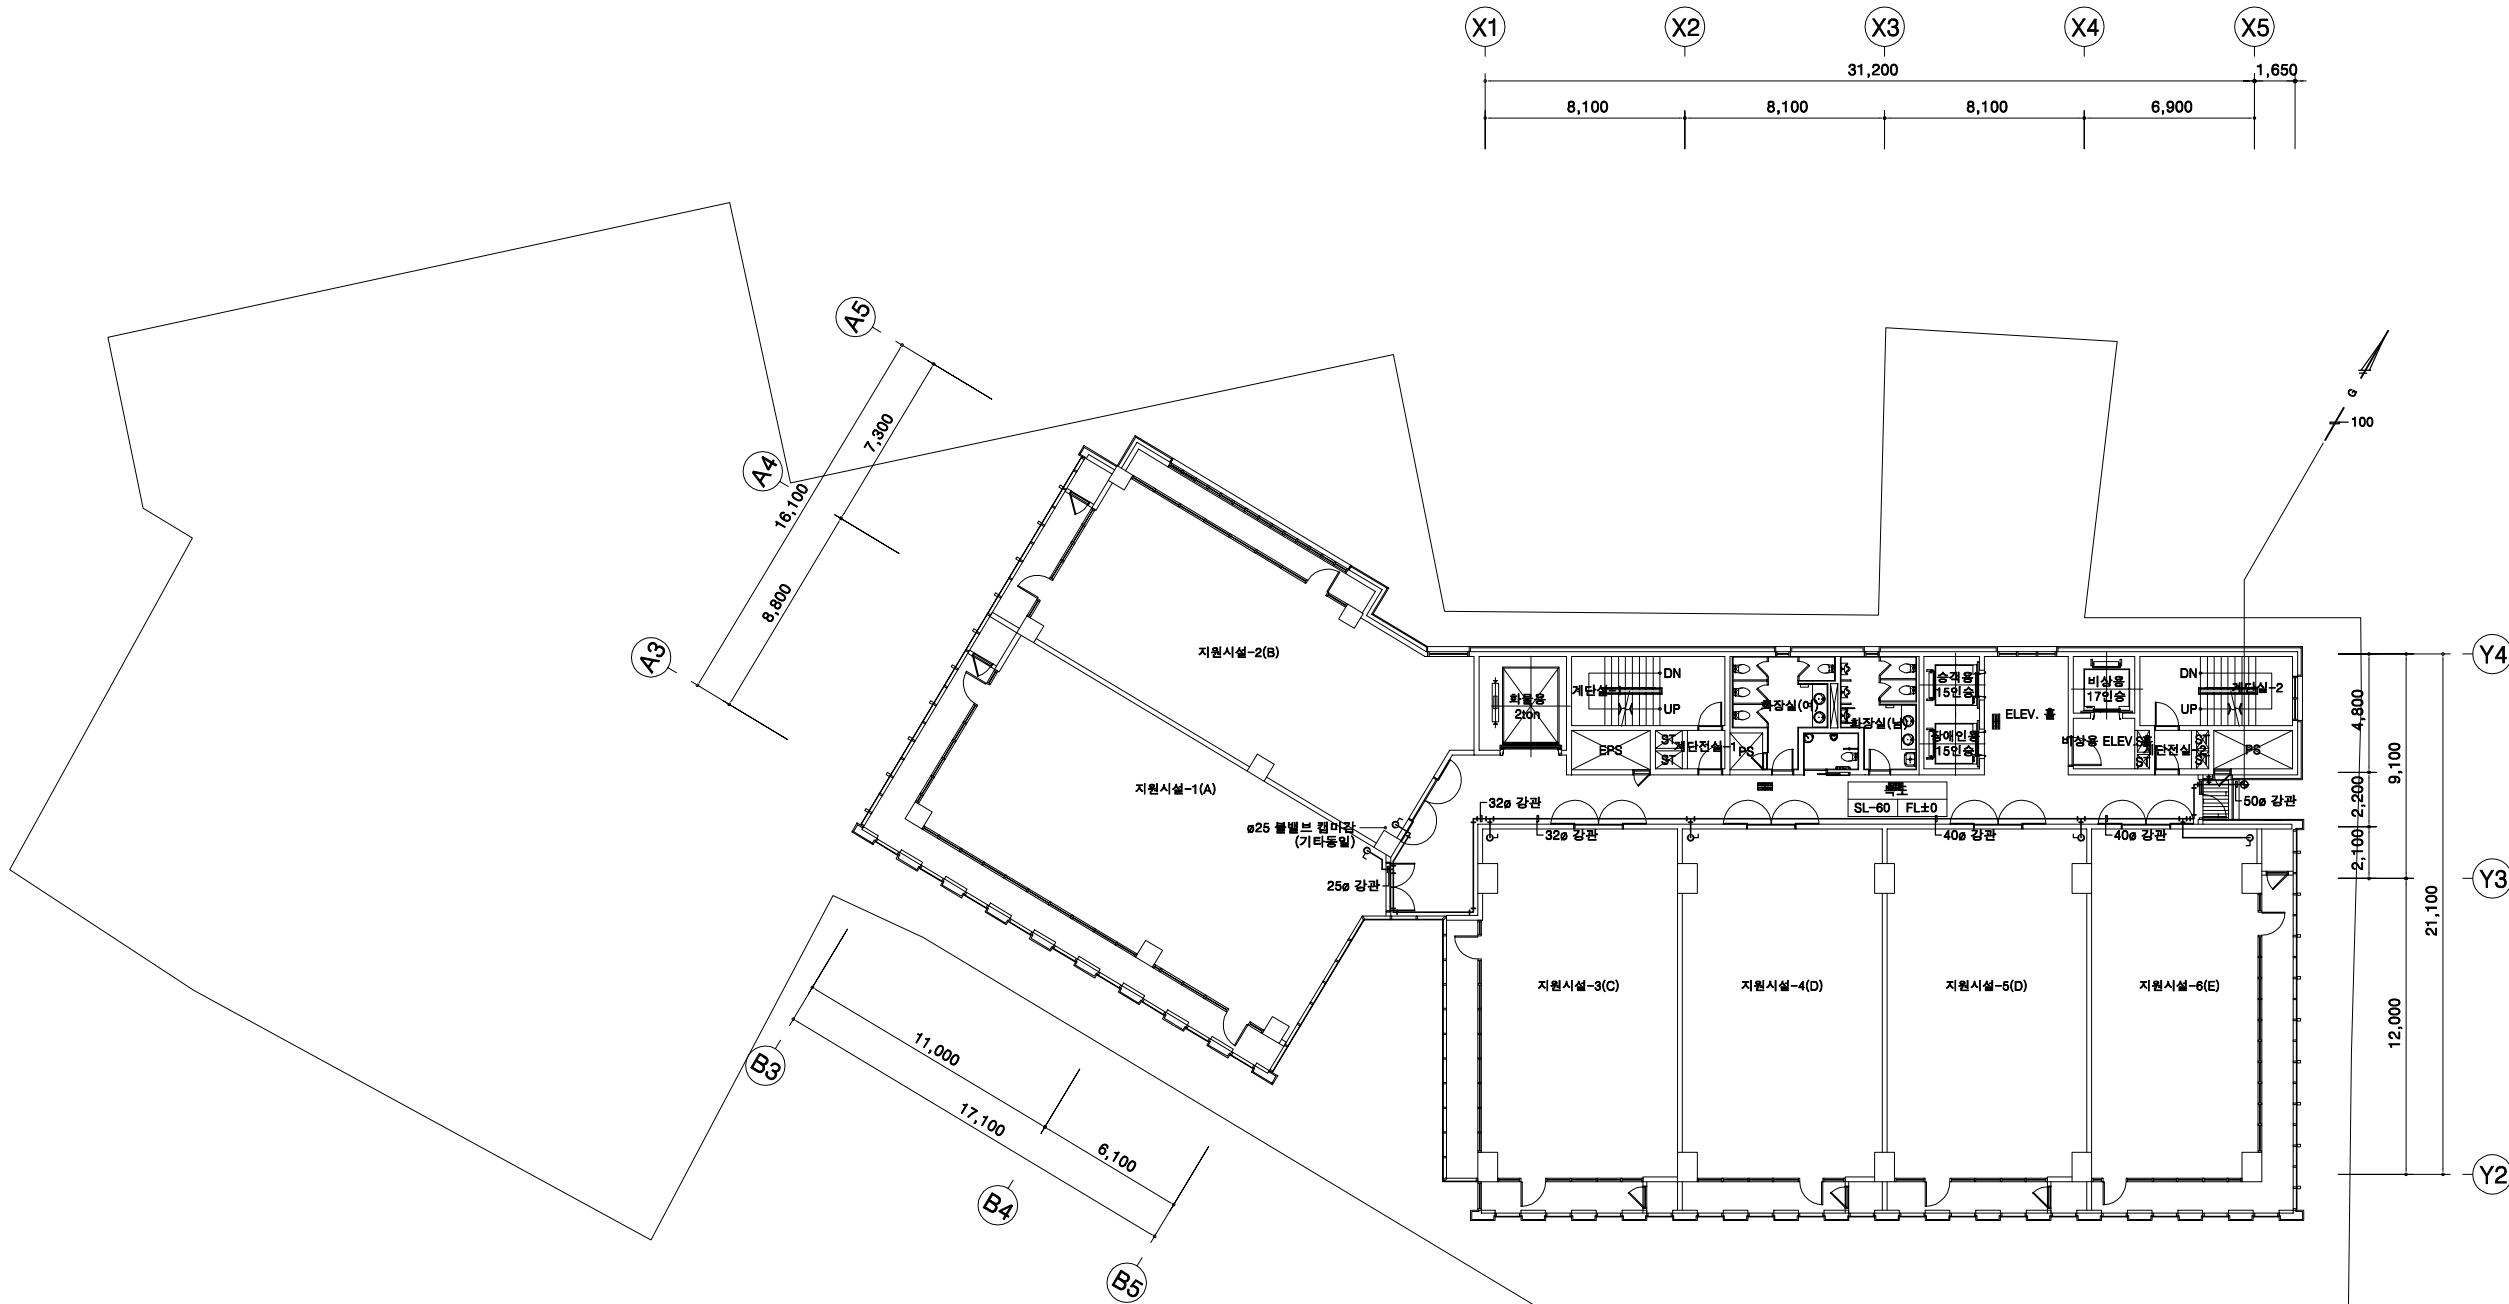

지상4층 가스배관 평면도



축척 : A1:1/150, A3:1/300

REVISION	DESCRIPTION	DATE
ORDER ORGAN	티티벤처인베스트먼트	
INVESTMENT	대표전화(02)579-8361 팩시밀리(02)579-8364	
PROJECT OFFICE	ATEC(주)에이텍종합건축사사무소	
ARCHITECTS & ASSOCIATES	대표전화(02)3462-6361 팩시밀리(02)3462-6362	
DRAWING TITLE	지상4층 가스배관 평면도	
SCALE	A1 : 1 / 150 A3 : 1 / 300	APPROVED
DRAWN	하진태	DATE
CHECKED		DATE
CONSULTANT		
DRAWING NO.	M-405	

PROJECT TITLE

성수동1가
지식산업센터
신축공사

NOTES

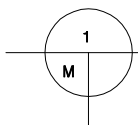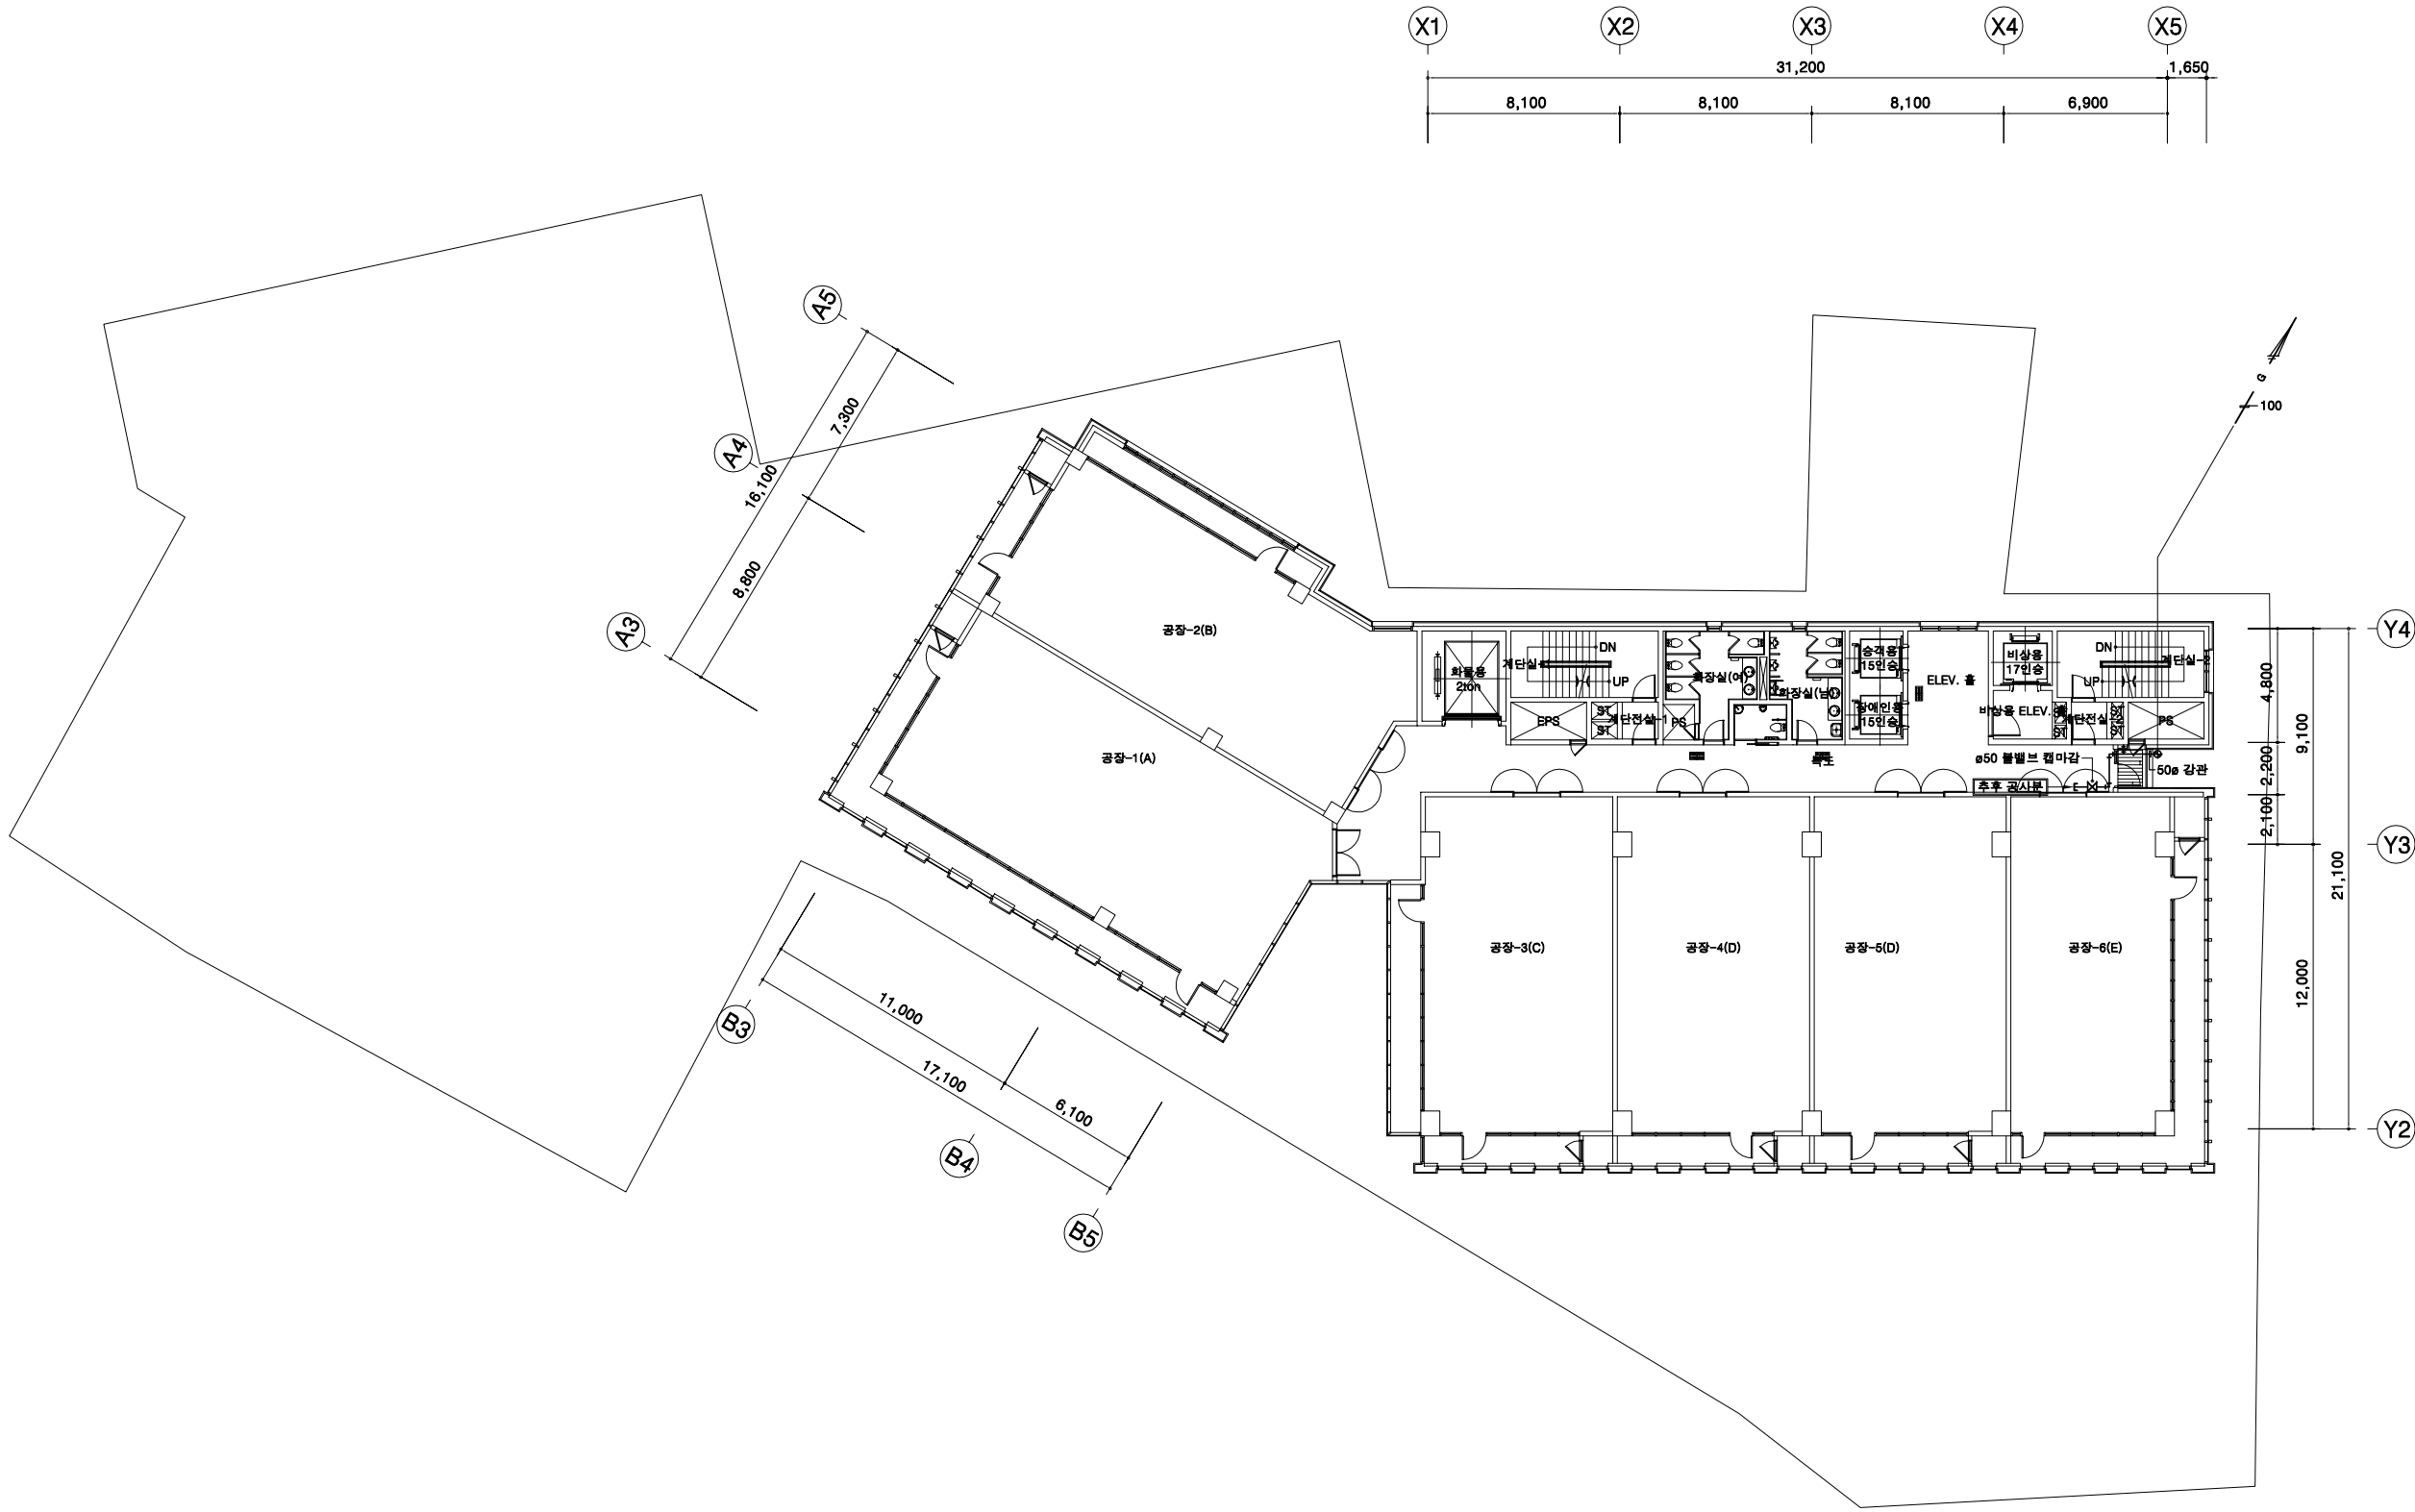

지상5~7층 가스배관 평면도

축척 : A1:1/150, A3:1/300

REVISION	DESCRIPTION	DATE

ORDER ORGAN

티티벤처인베스트먼트
대표전화(02)579-8361
팩시밀리(02)579-8364

PROJECT OFFICE

ATEC(주)에이텍종합건축사사무소
대표전화(02)3462-6361
팩시밀리(02)3462-6362

DRAWING TITLE

지상5~7층
가스배관 평면도

SCALE	APPROVED
A1 : 1 / 150 A3 : 1 / 300	ARCHITECT 김 상 길
DRAWN 하 진 태	DATE 2014. 03

CHECKED	DATE 2014. 03
---------	---------------

CONSULTANT

DRAWING NO. M-406

PROJECT TITLE

성수동1가
지식산업센터
신축공사

NOTES

REVISION DESCRIPTION DATE

ORDER ORGAN

INVESTMENT TOWER
대표전화(02)579-8361
팩시밀리(02)579-8364

PROJECT OFFICE

ATEC
ARCHITECTS & ASSOCIATES
대표전화(02)3462-6361
팩시밀리(02)3462-6362

DRAWING TITLE

지상8~10층
가스배관 평면도

SCALE
A1 : 1 / 150
A3 : 1 / 300

APPROVED
ARCHITECT 김 상 길

DRAWN
하 진 태




DATE
2014. 03

CHECKED DATE
2014. 03

CONSULTANT

DRAWING NO.

M-407

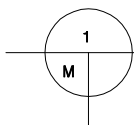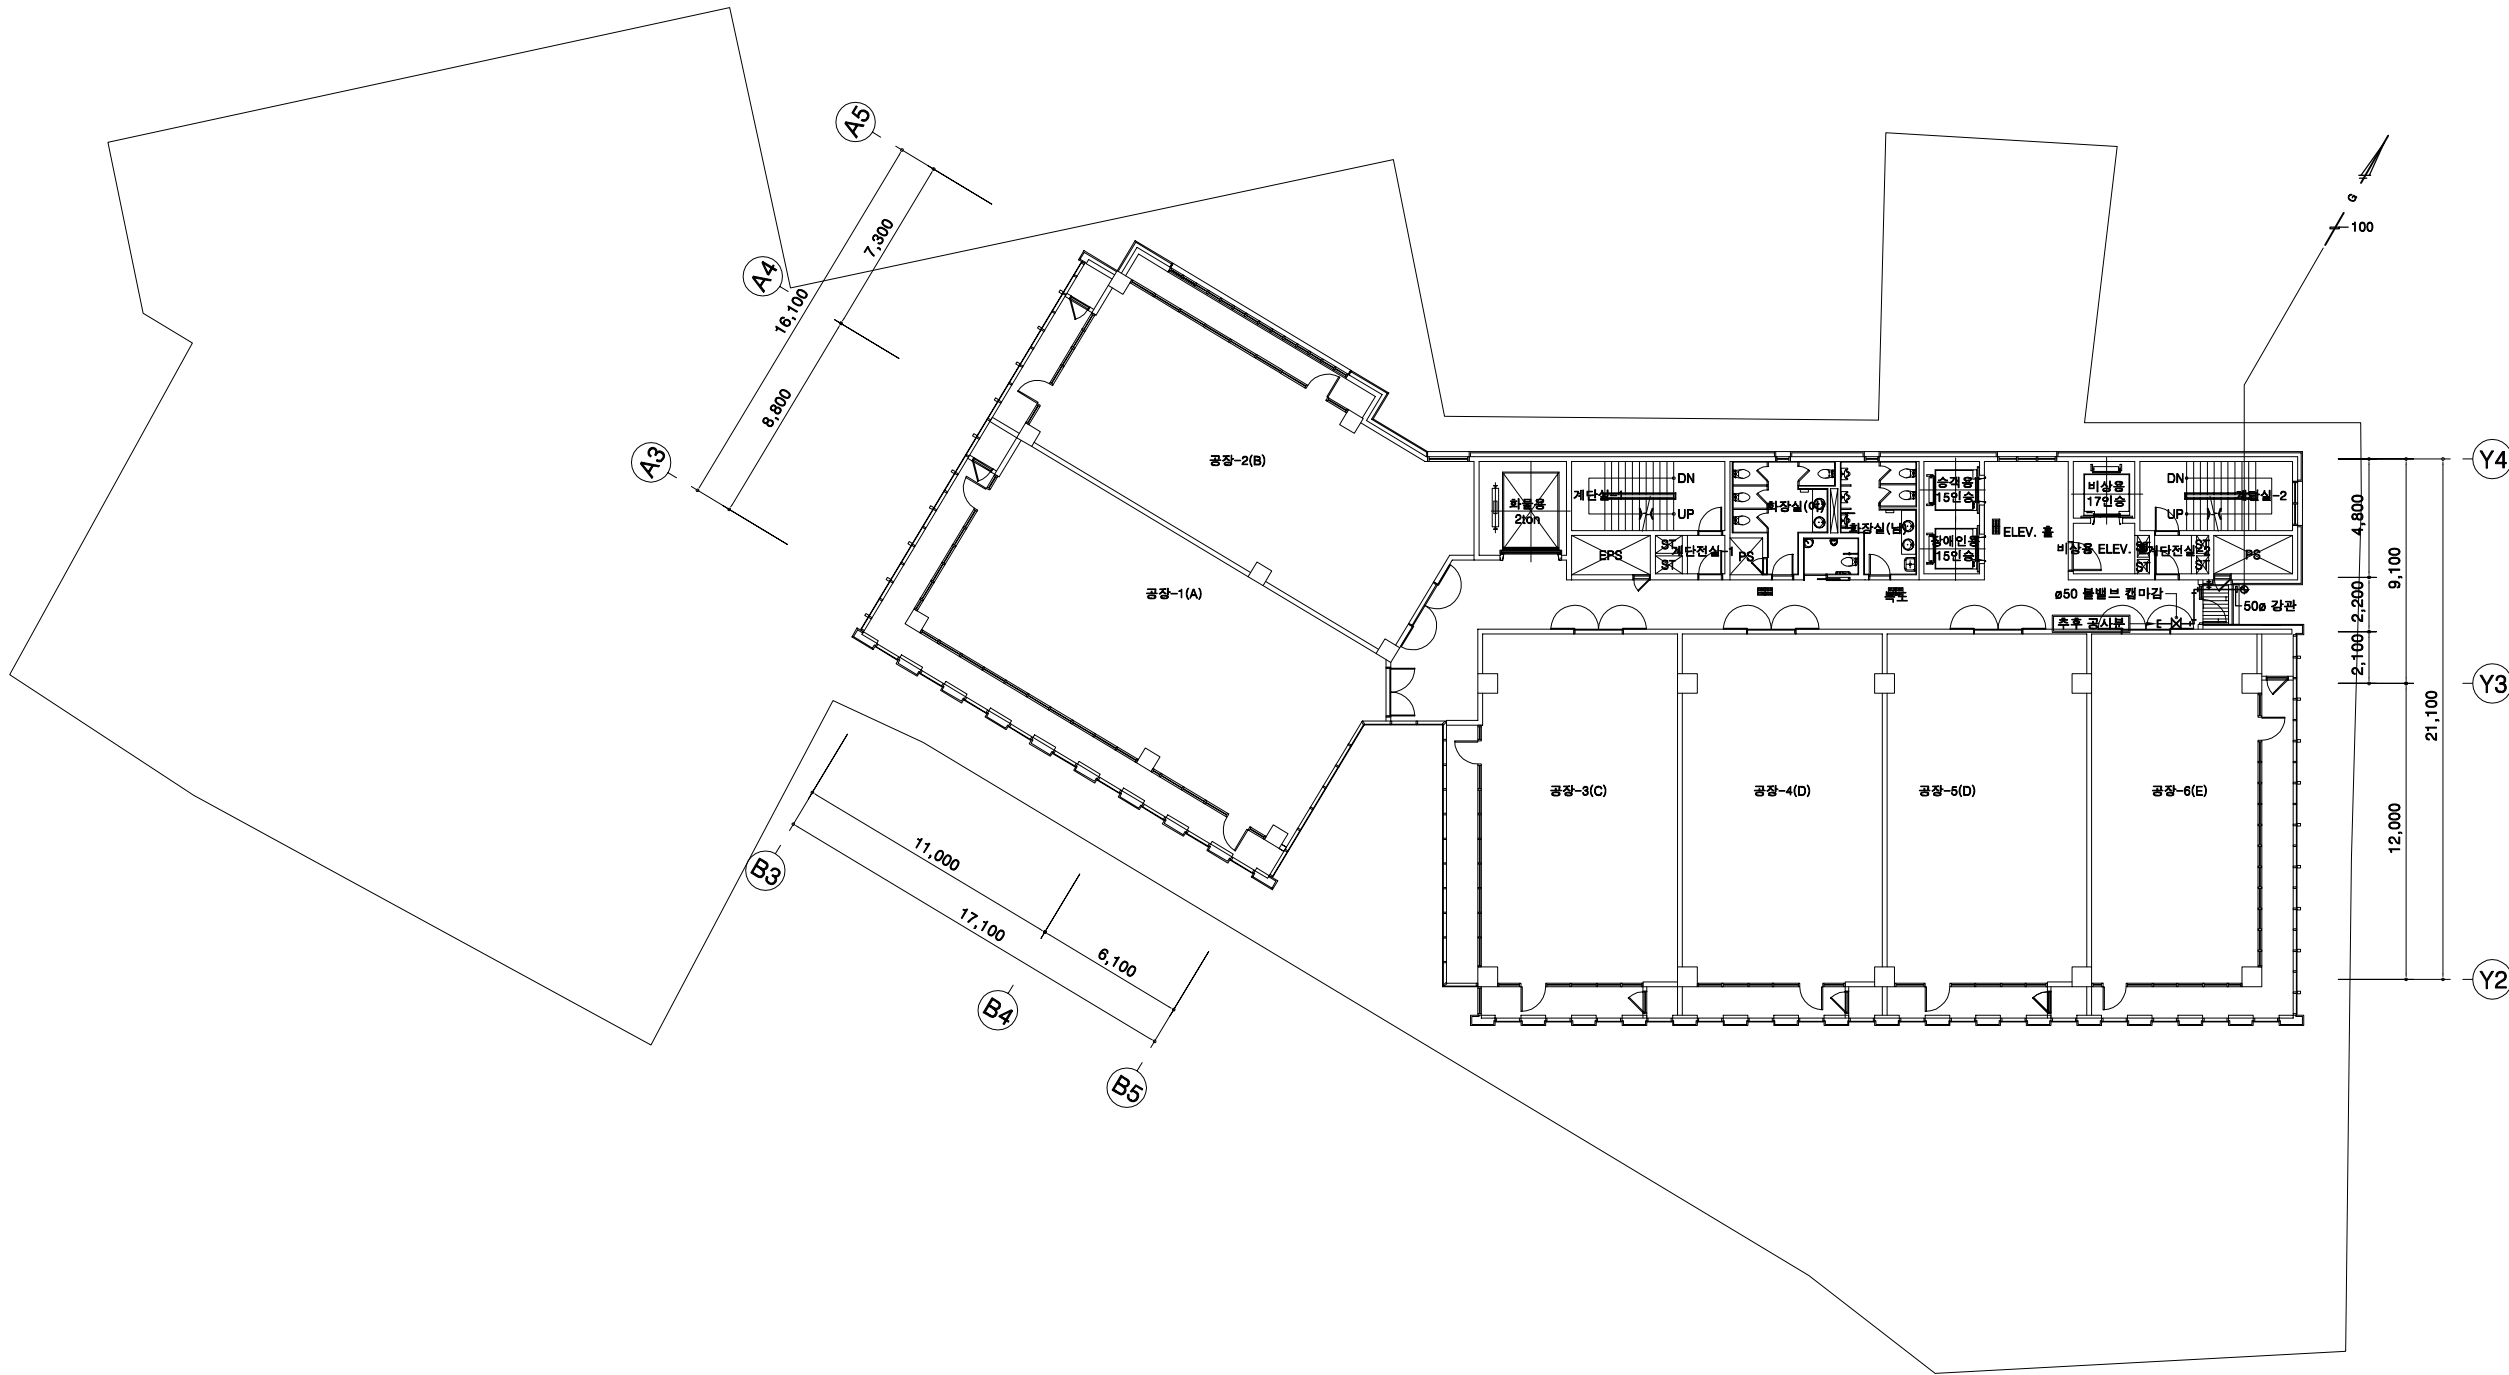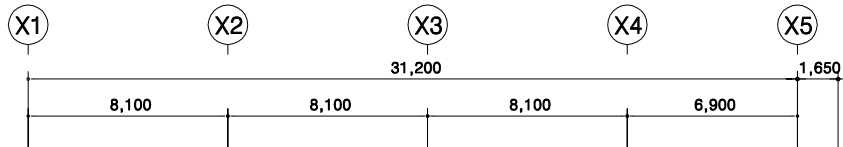



지상8~10층 가스배관 평면도

축척 : A1:1/150, A3:1/300

PROJECT TITLE

성수동1가
지식산업센터
신축공사

NOTES

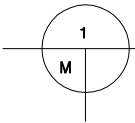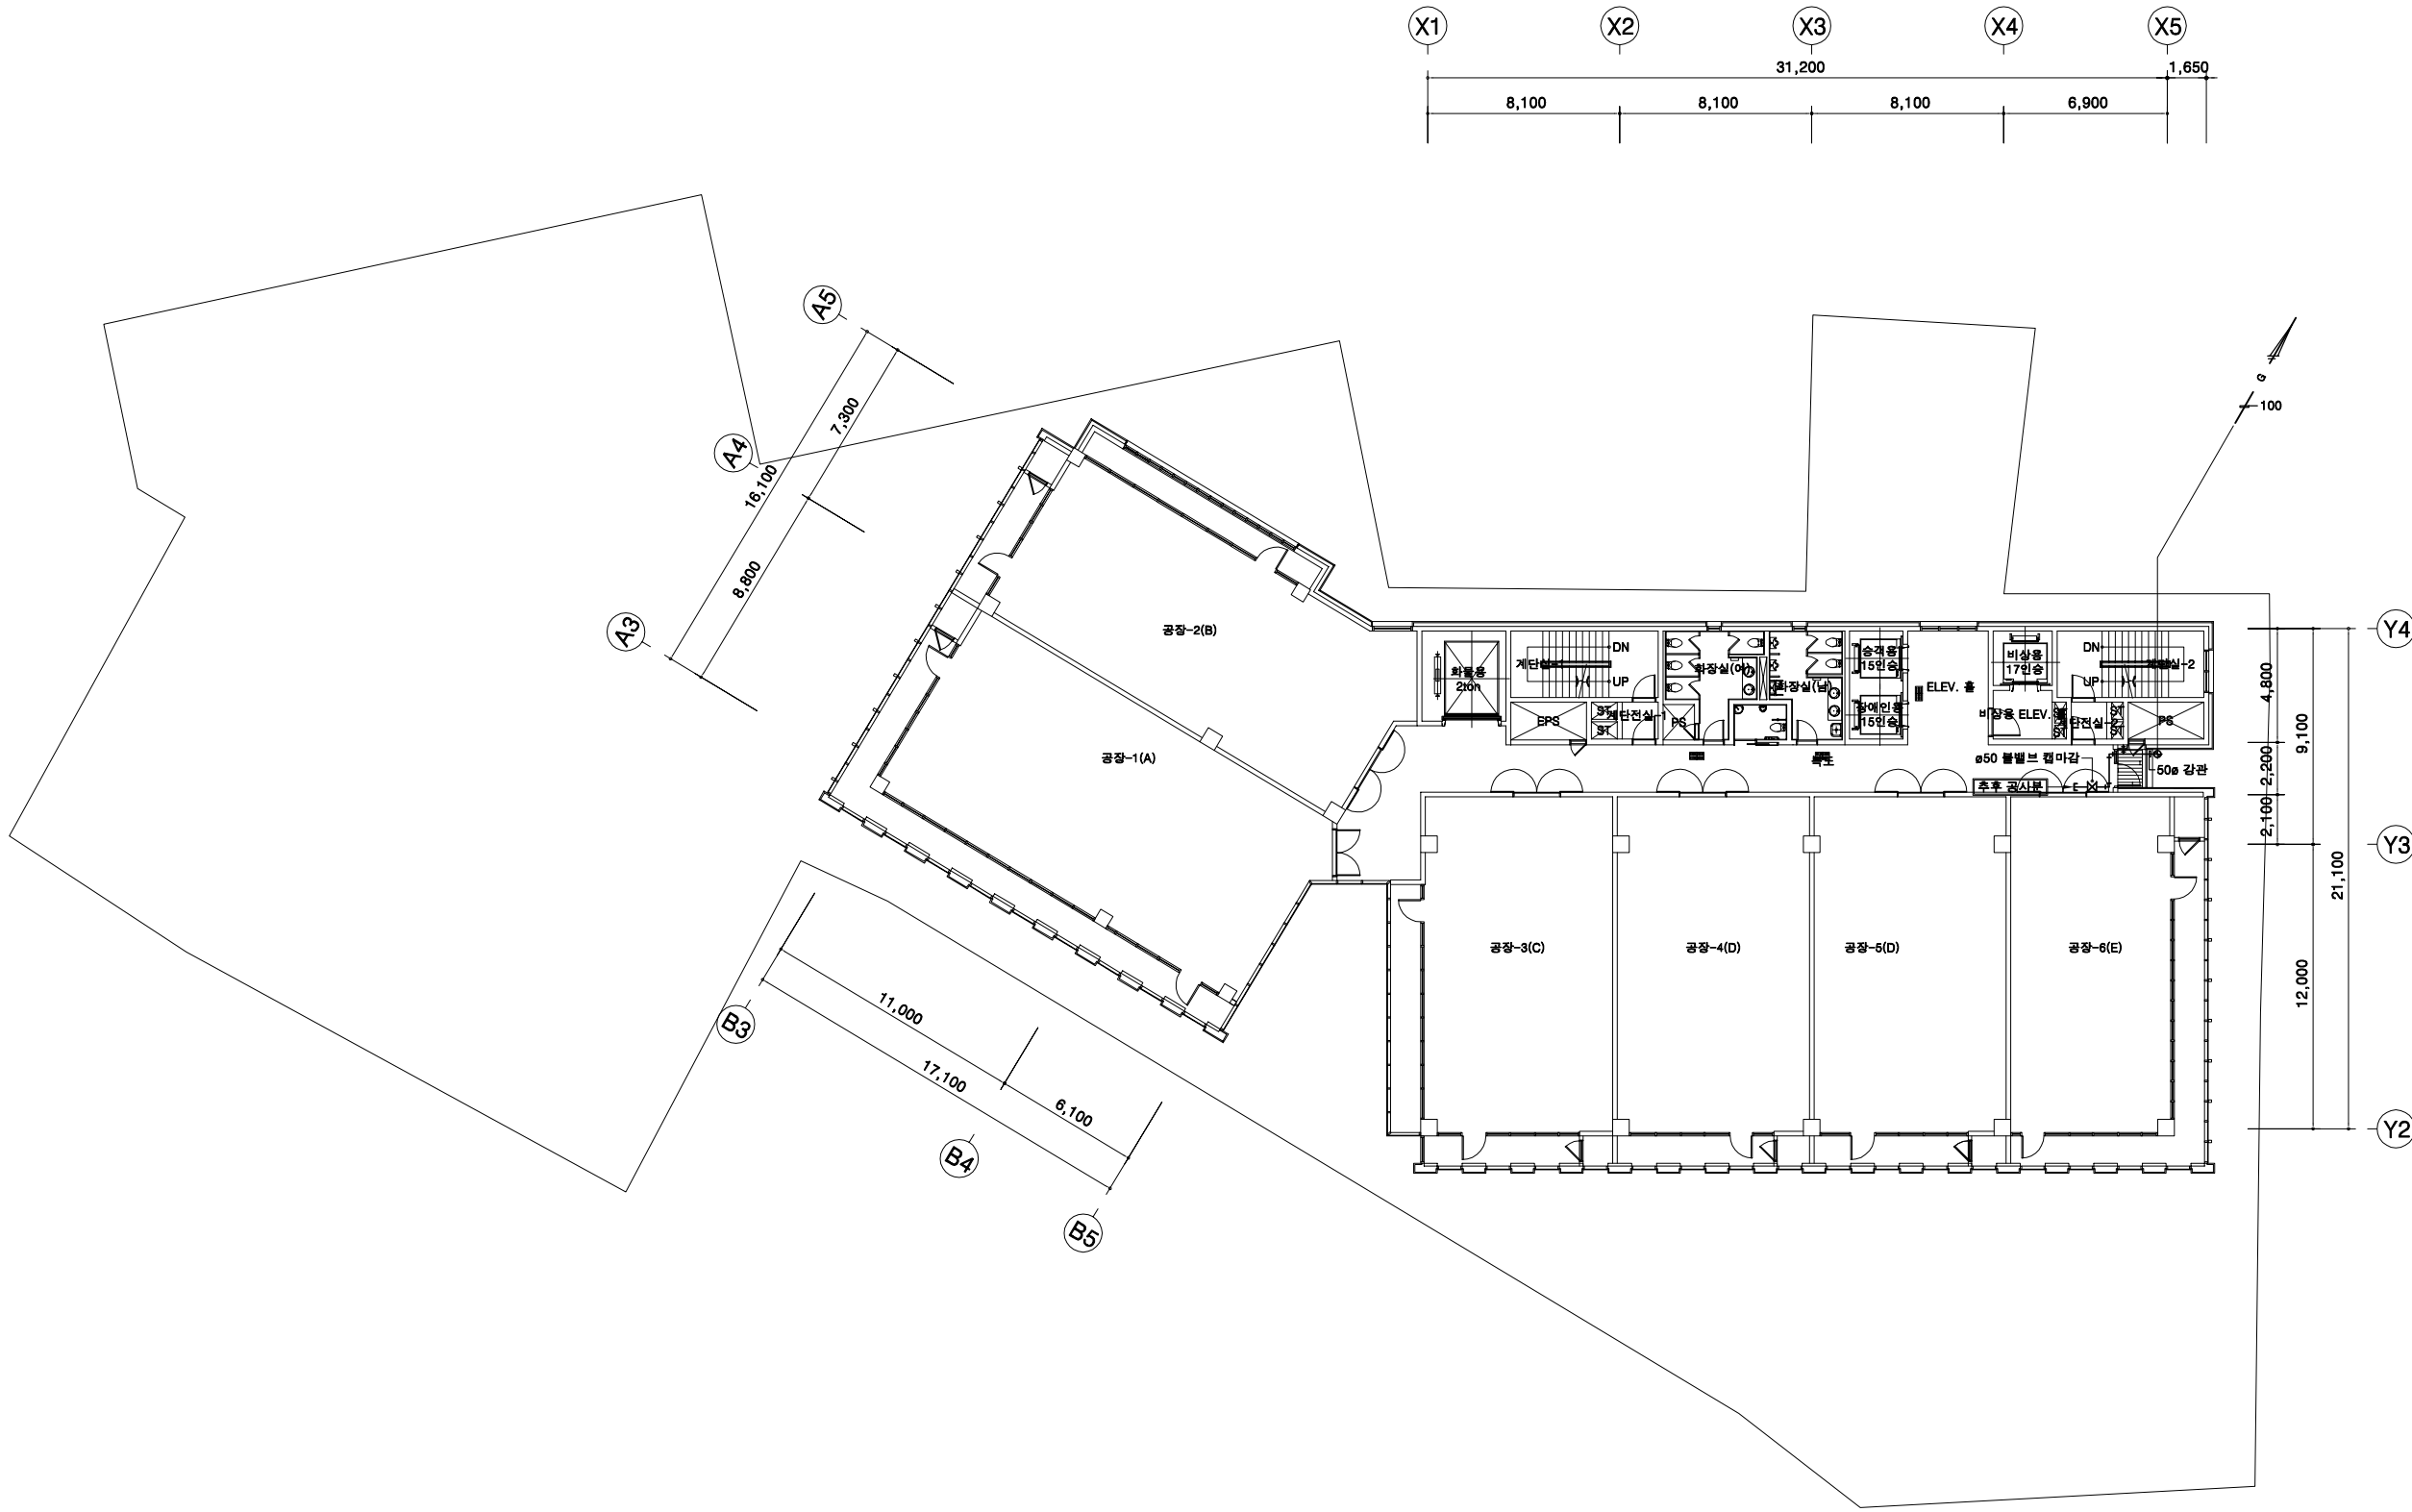

지상11~12층 가스배관 평면도



축척 : A1:1/150, A3:1/300

REVISION	DESCRIPTION	DATE
ORDER ORGAN		
T T 티티벤처인베스트먼트 INVESTMENT 대표전화(02)579-8361 팩시밀리(02)579-8364		
PROJECT OFFICE		
ATEC(주)에이텍종합건축사사무소 ARCHITECTS & ASSOCIATES 대표전화(02)3462-6361 팩시밀리(02)3462-6362		
DRAWING TITLE		
지상11~12층 가스배관 평면도		
SCALE	APPROVED	
A1 : 1 / 150 A3 : 1 / 300	ARCHITECT	김 상 길
DRAWN	DATE	2014. 03
하 진 태		
CHECKED	DATE	
	2014. 03	
CONSULTANT		
DRAWING NO.		
M-408		

PROJECT TITLE

성수동1가
지식산업센터
신축공사

NOTES

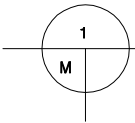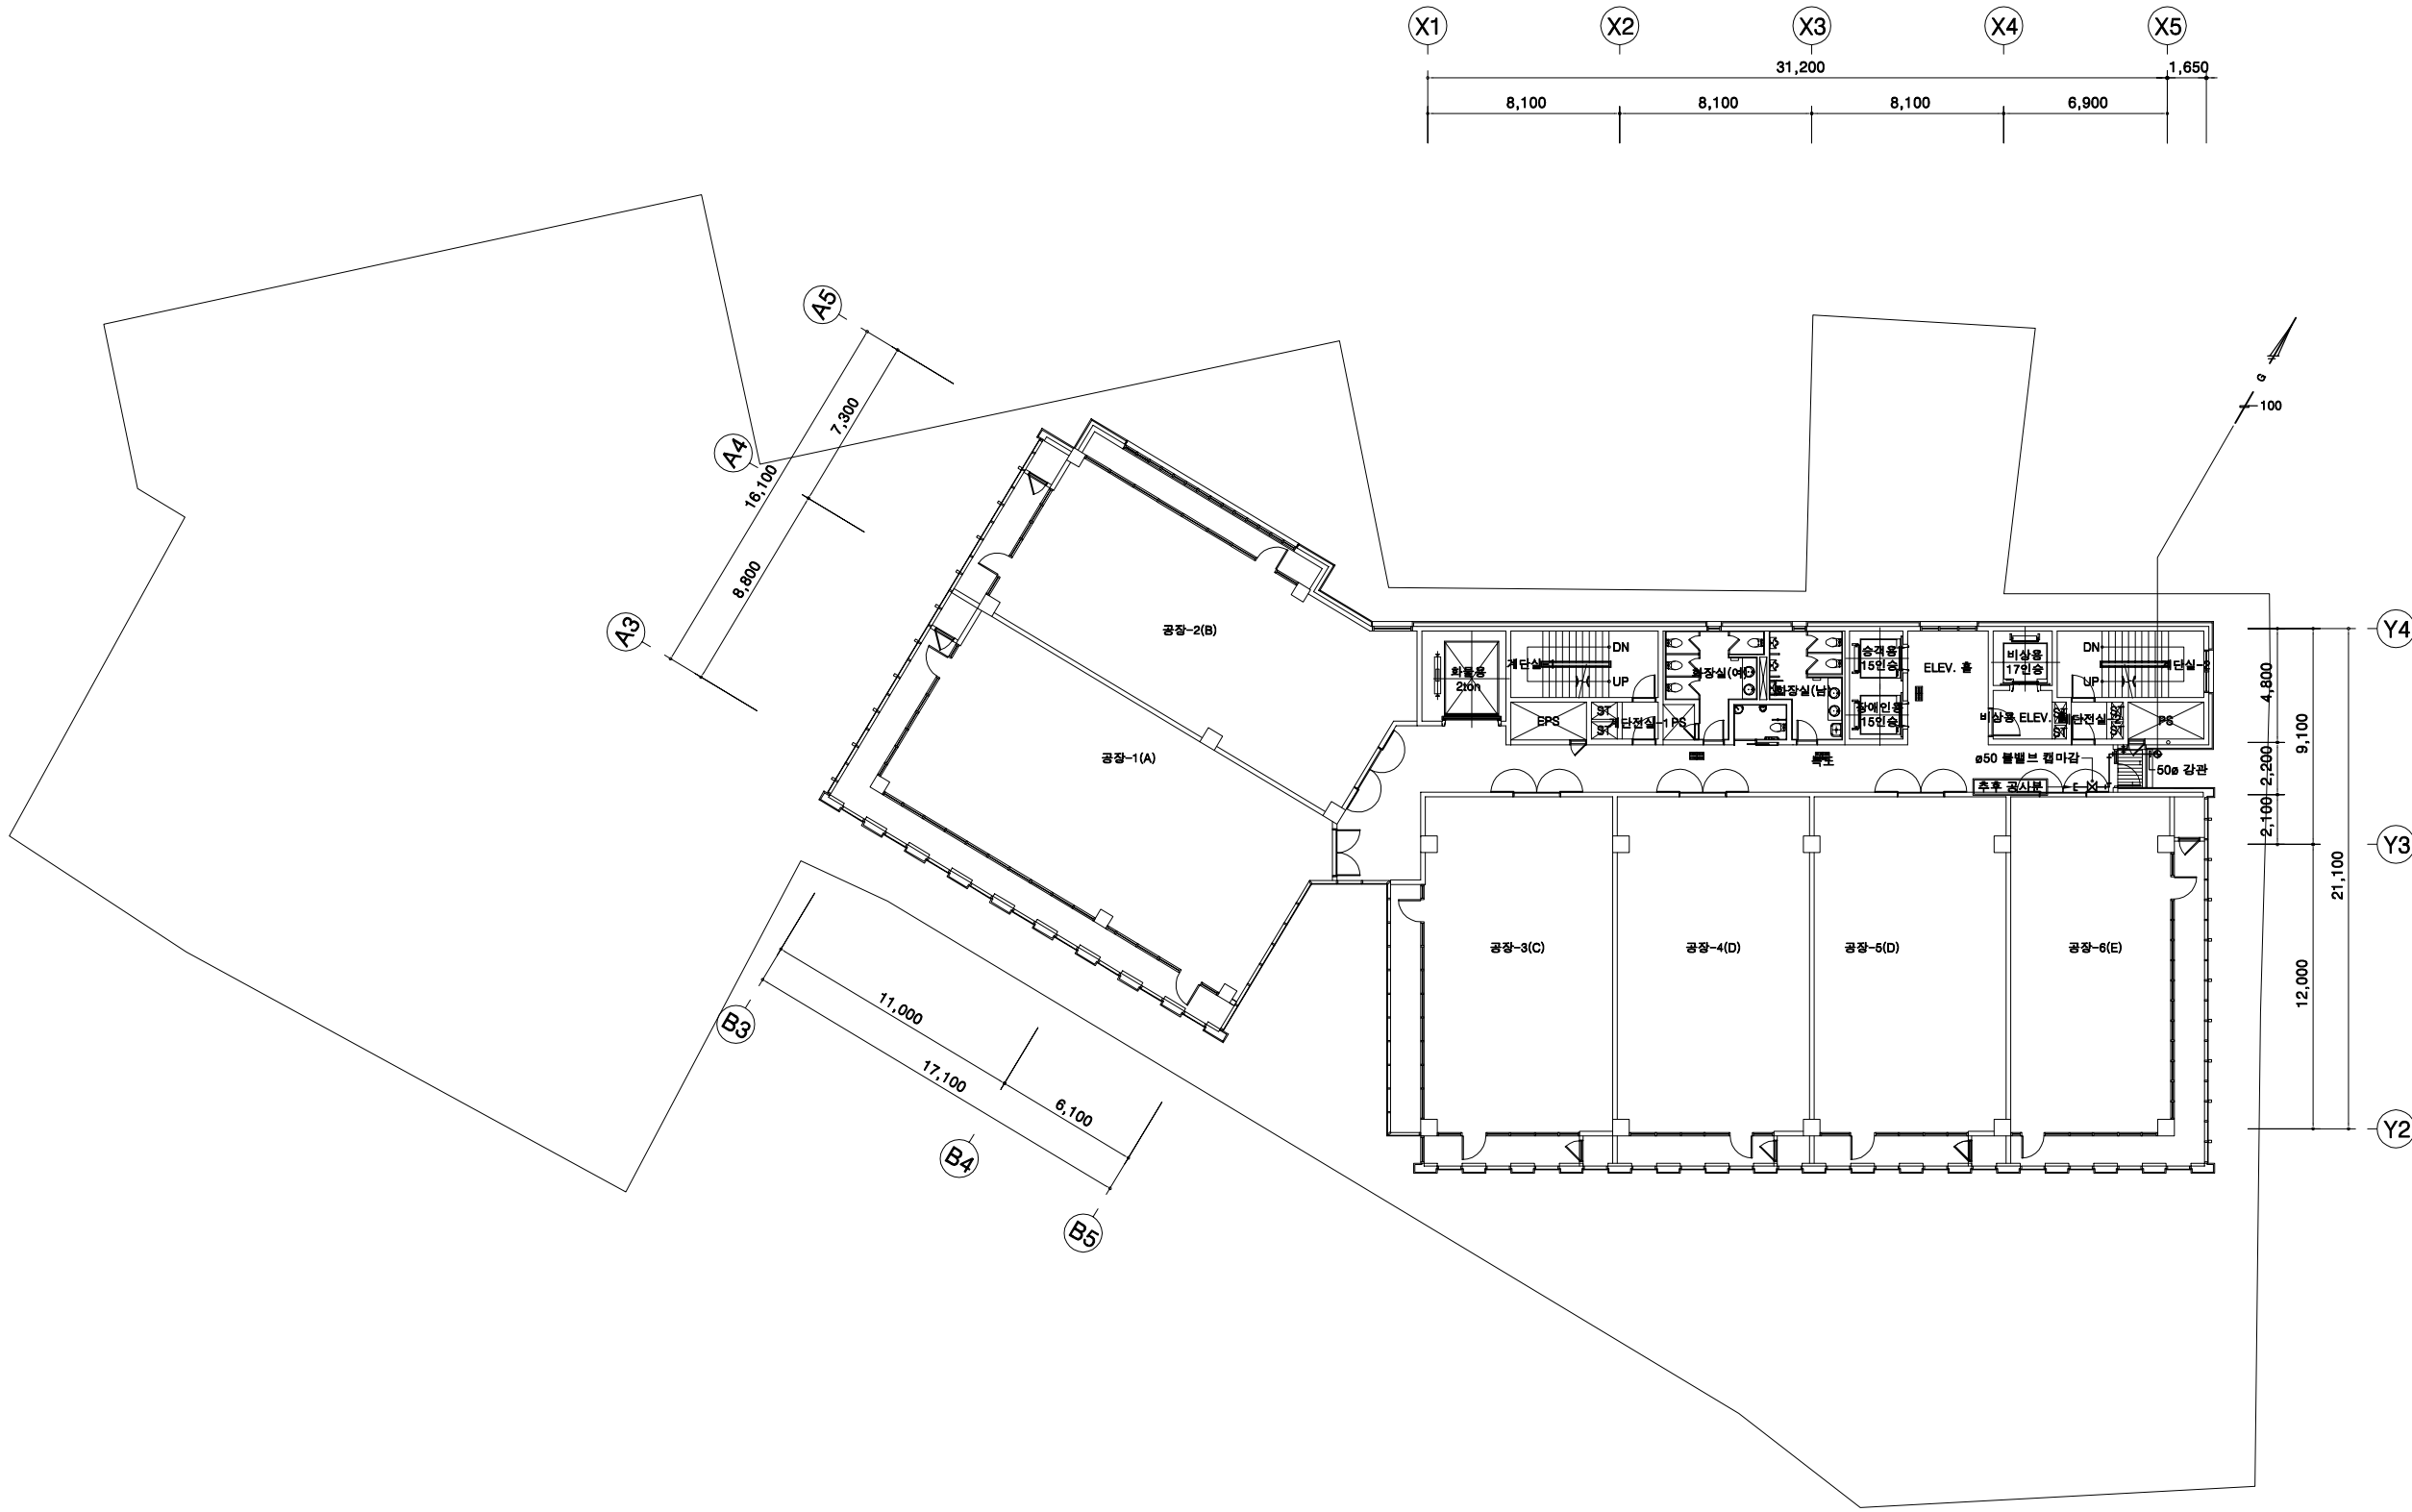

지상13~14층 가스배관 평면도

축척 : A1:1/150, A3:1/300

REVISION DESCRIPTION DATE

ORDER ORGAN

INVESTMENT TIT VENTURE 대표전화(02)579-8361
팩시밀리(02)579-8364

PROJECT OFFICE

ATEC (주)에이텍종합건축사사무소 대표전화(02)3462-6361
팩시밀리(02)3462-6362

DRAWING TITLE

지상13~14층
가스배관 평면도

SCALE

A1 : 1 / 150
A3 : 1 / 300

DRAWN

하진태

DATE

2014. 03

CHECKED

DATE

2014. 03

CONSULTANT



DRAWING NO.

M-409

PROJECT TITLE

성수동1가
지식산업센터
신축공사

NOTES

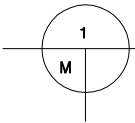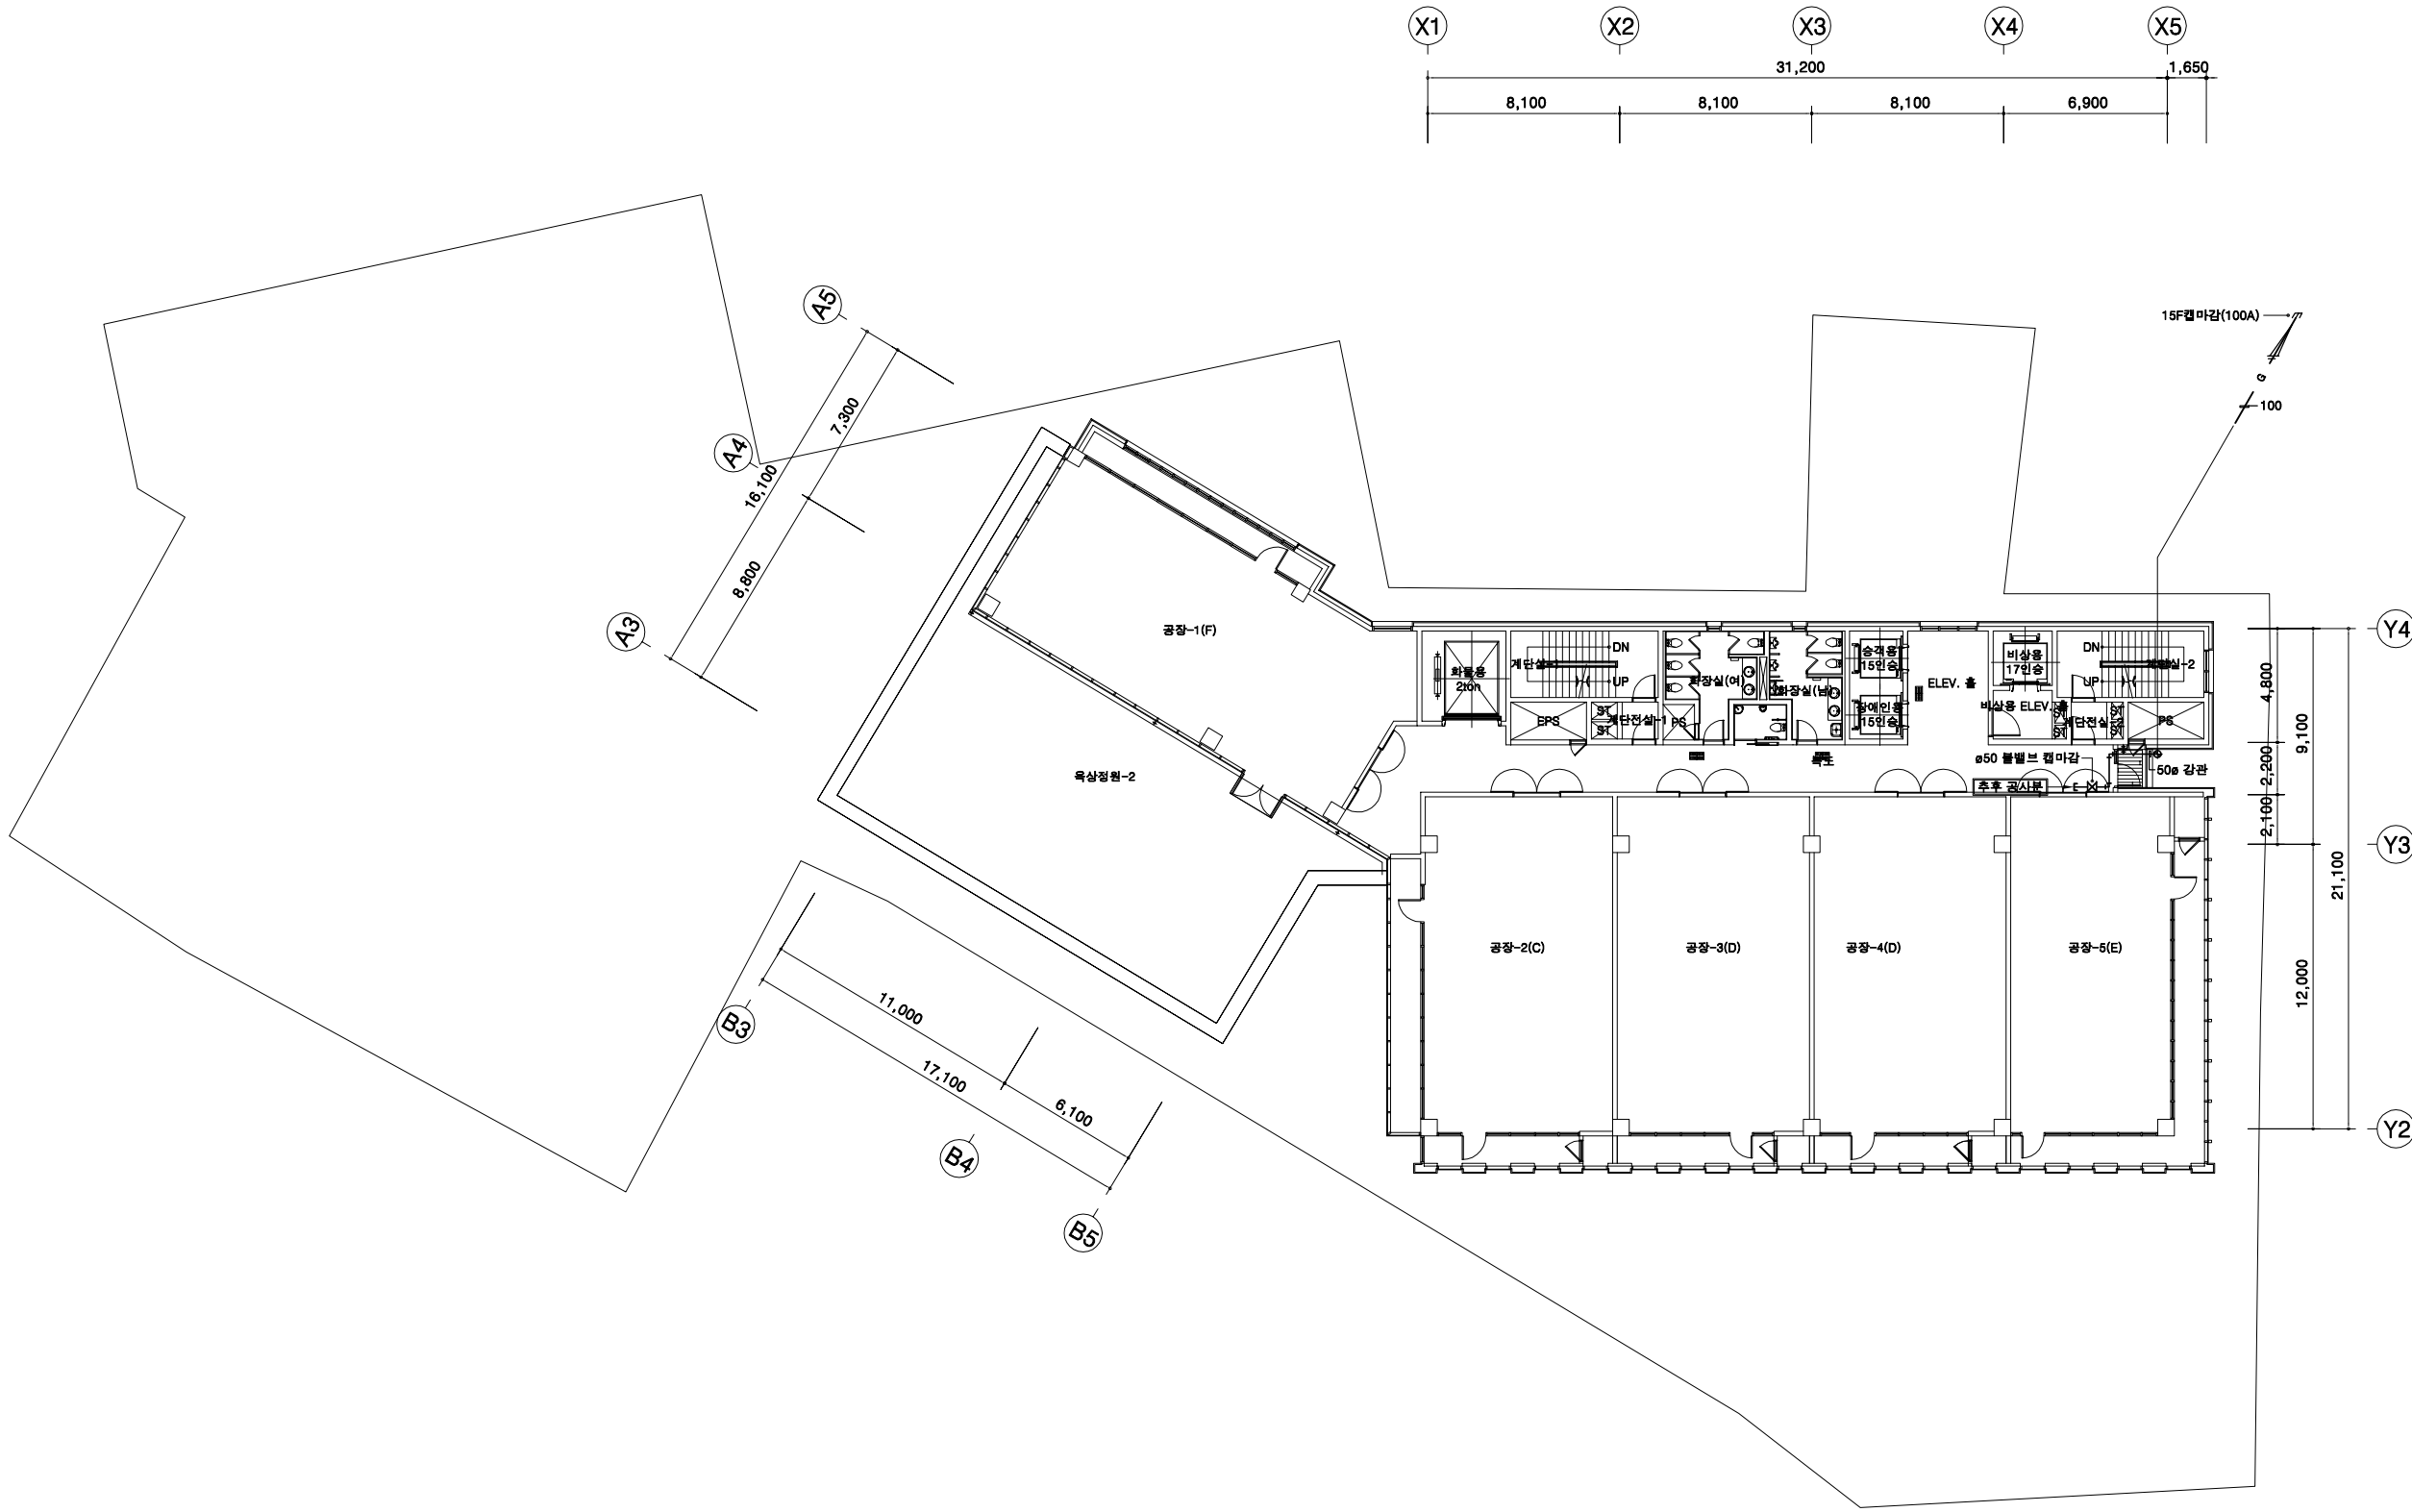

지상15층 가스배관 평면도

축척 : A1:1/150, A3:1/300

REVISION DESCRIPTION DATE

ORDER ORGAN

INVESTMENT TIT VENTURE 대표전화(02)579-8361
팩시밀리(02)579-8364

PROJECT OFFICE

ATEC (주)에이텍종합건축사사무소 대표전화(02)3462-6361
팩시밀리(02)3462-6362

DRAWING TITLE

지상15층
가스배관 평면도

SCALE

A1 : 1 / 150
A3 : 1 / 300

DRAWN

하진태

CHECKED

DATE

2014. 03

CONSULTANT

DRAWING NO.

M-410