



MARK	P.D.F 저수조
PRODUCT SIZE	(12,000-208) x 6,000 x 3,500 h
CAPACITY	247.6 TON (기동용적제외: - TON, 유효용량:203 TON, 만수율:82%)
QUANTITY	1 기
NOTE	NOZZLE 위치 및 구경은 현장시공시 감독관 설정 위치 취부

성수동1가
지식산업센터
신축공사

NOTES

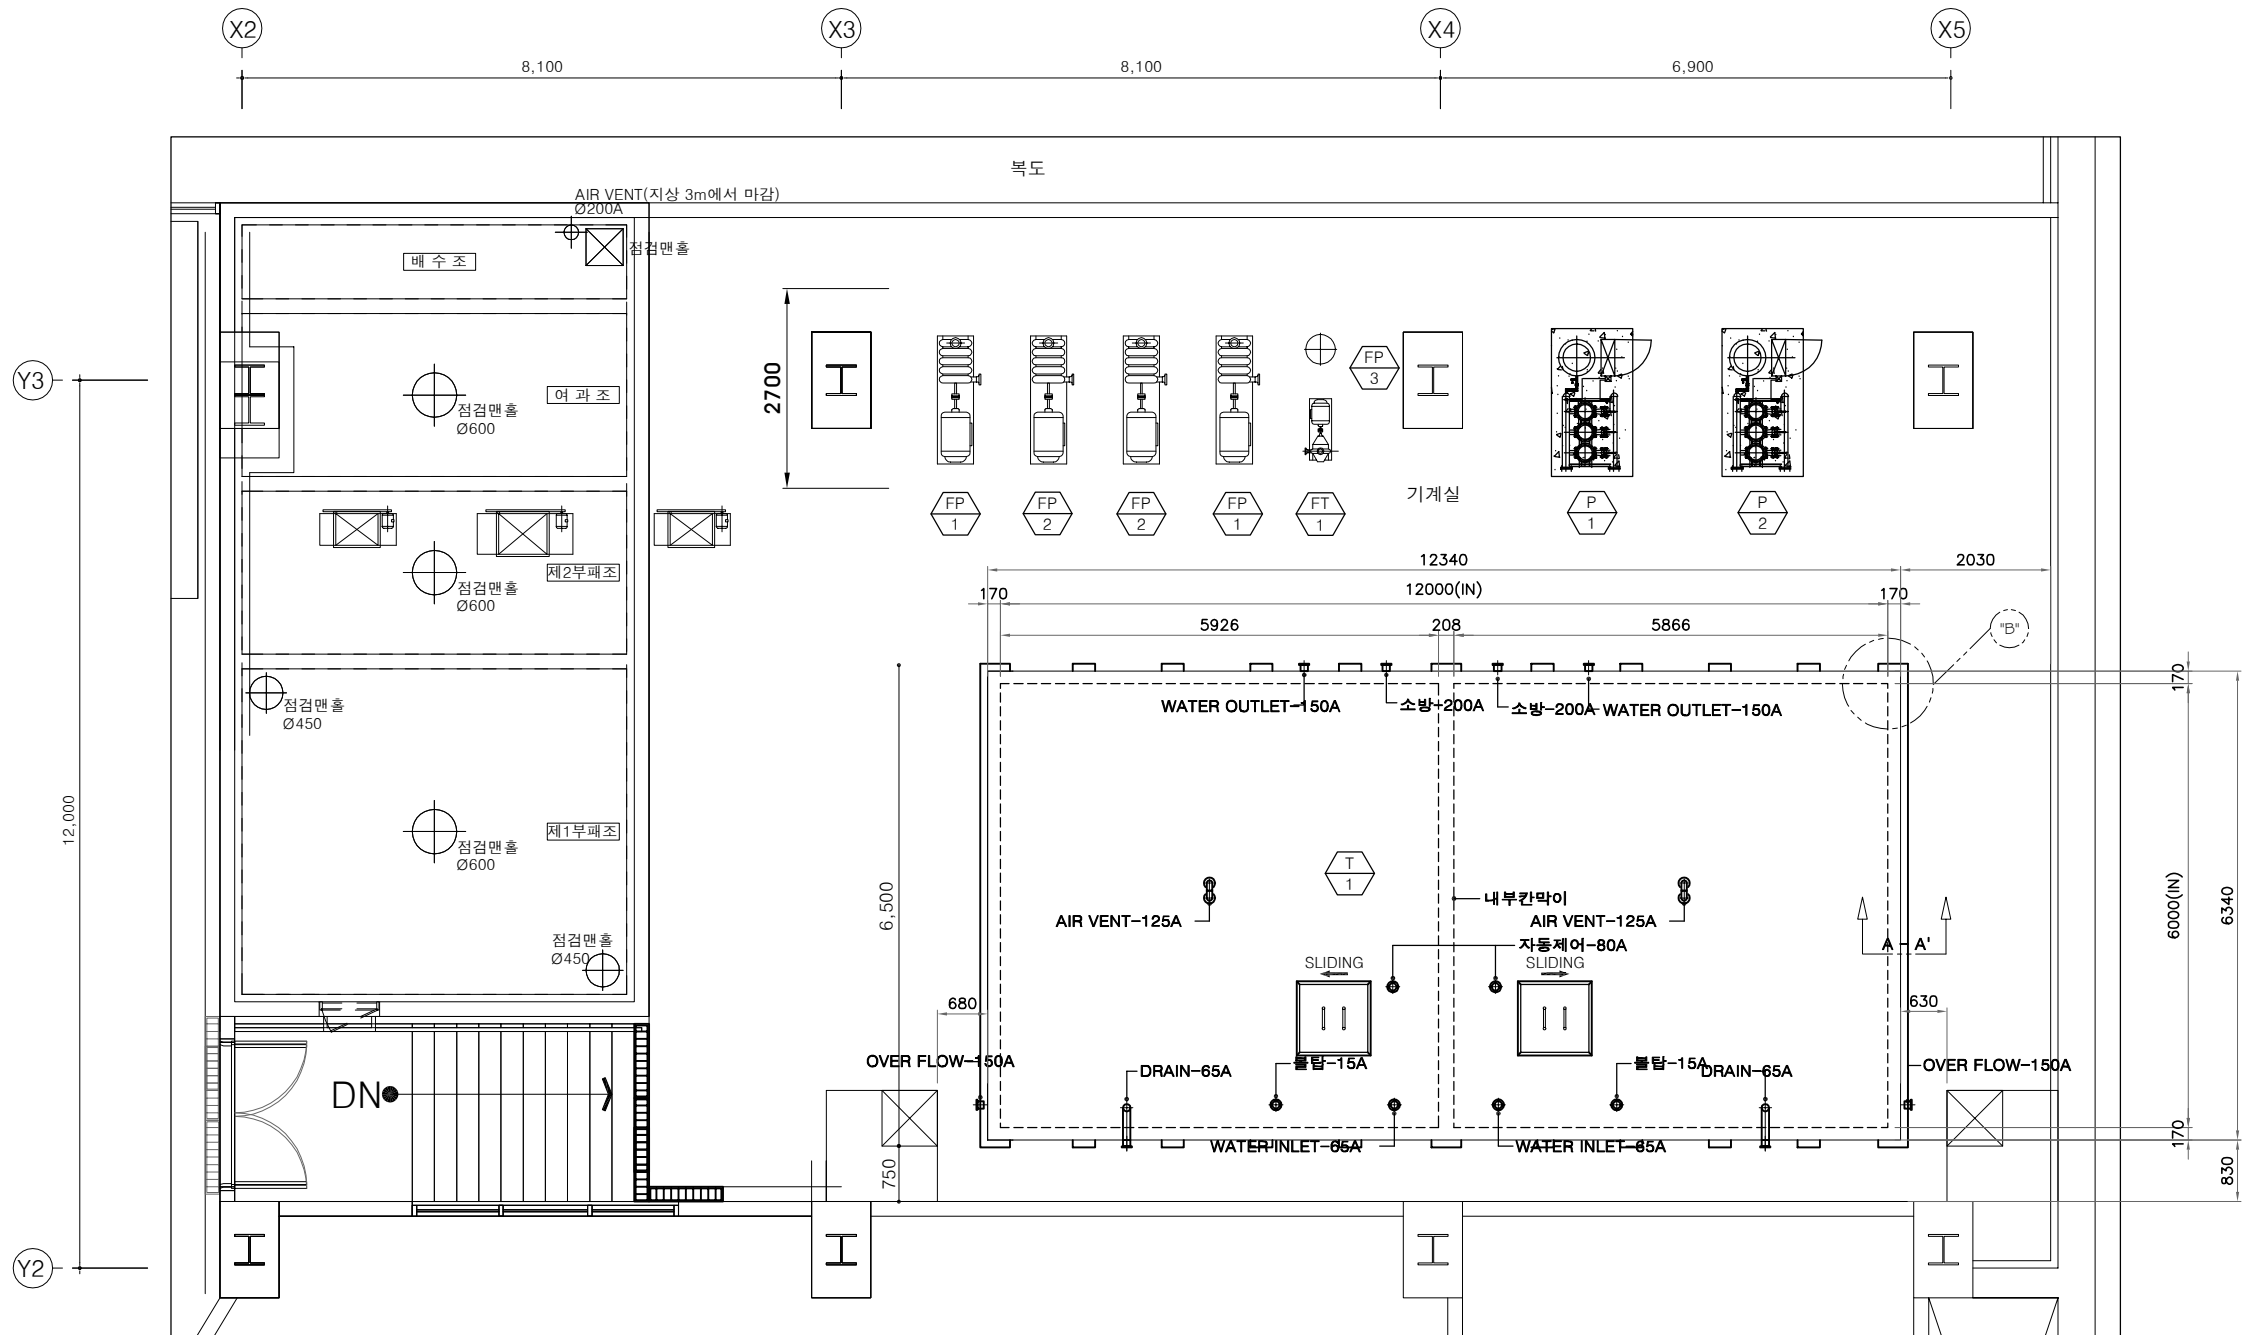

저수조 설치 평면도

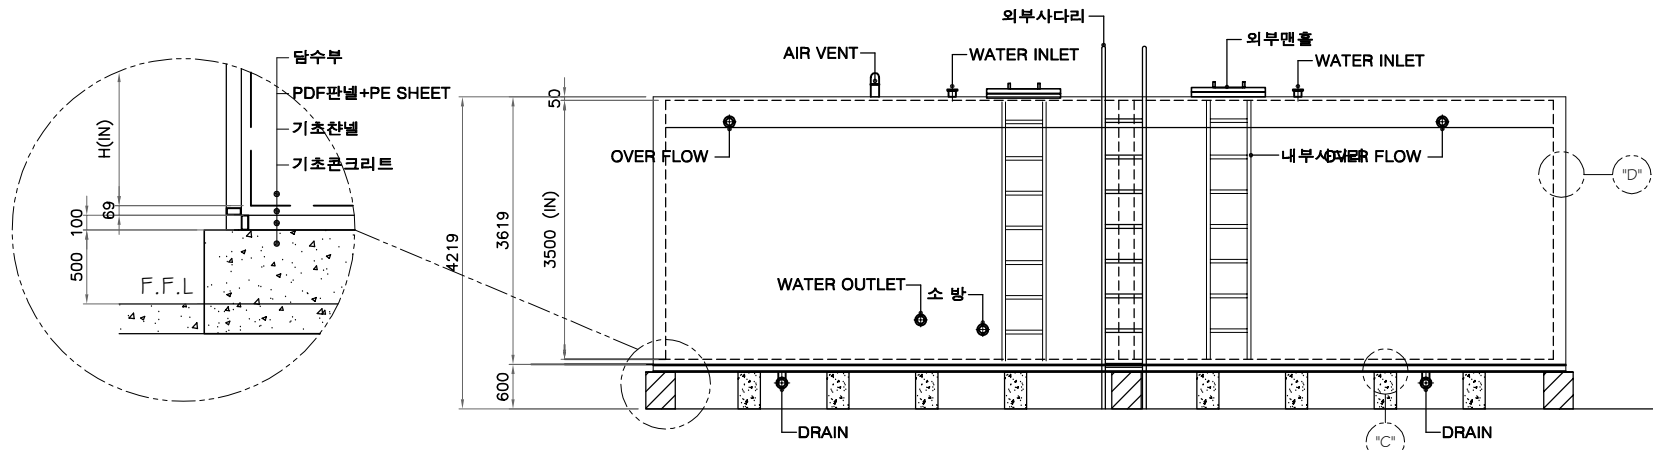

저수조 설치 단면도

REVISION	DESCRIPTION	DATE

ORDER ORGAN
티티벤처인베스트먼트
INVESTMENT
대표전화(02)579-8361
팩시밀리(02)579-8364
PROJECT OFFICE
ATEC (주)에이텍종합건축사사무소
ARCHITECTS & ASSOCIATES
대표전화(02)3462-6361
팩시밀리(02)3462-6362

DRAWING TITLE
저수조상세도 - 1


SCALE A1 : 1 / 50 A3 : 1 / 100	APPROVED ARCHITECT 김 상 길
DRAWN 함 현 미	DATE 2014. 03
CHECKED	DATE 2014. 03
CONSULTANT	

DRAWING NO.
M-501

MARK	P.D.F 저수조
PRODUCT SIZE	(12,000-208) x 6,000 x 3,500 h
CAPACITY	247.6 TON (기동용적제외: - TON, 유효용량:203 TON, 만수율:82%)
QUANTITY	1 기
NOTE	NOZZLE 위치 및 구경은 현장시공시 감독관 설정 위치 취부

성수동1가
지식산업센터
신축공사

NOTES

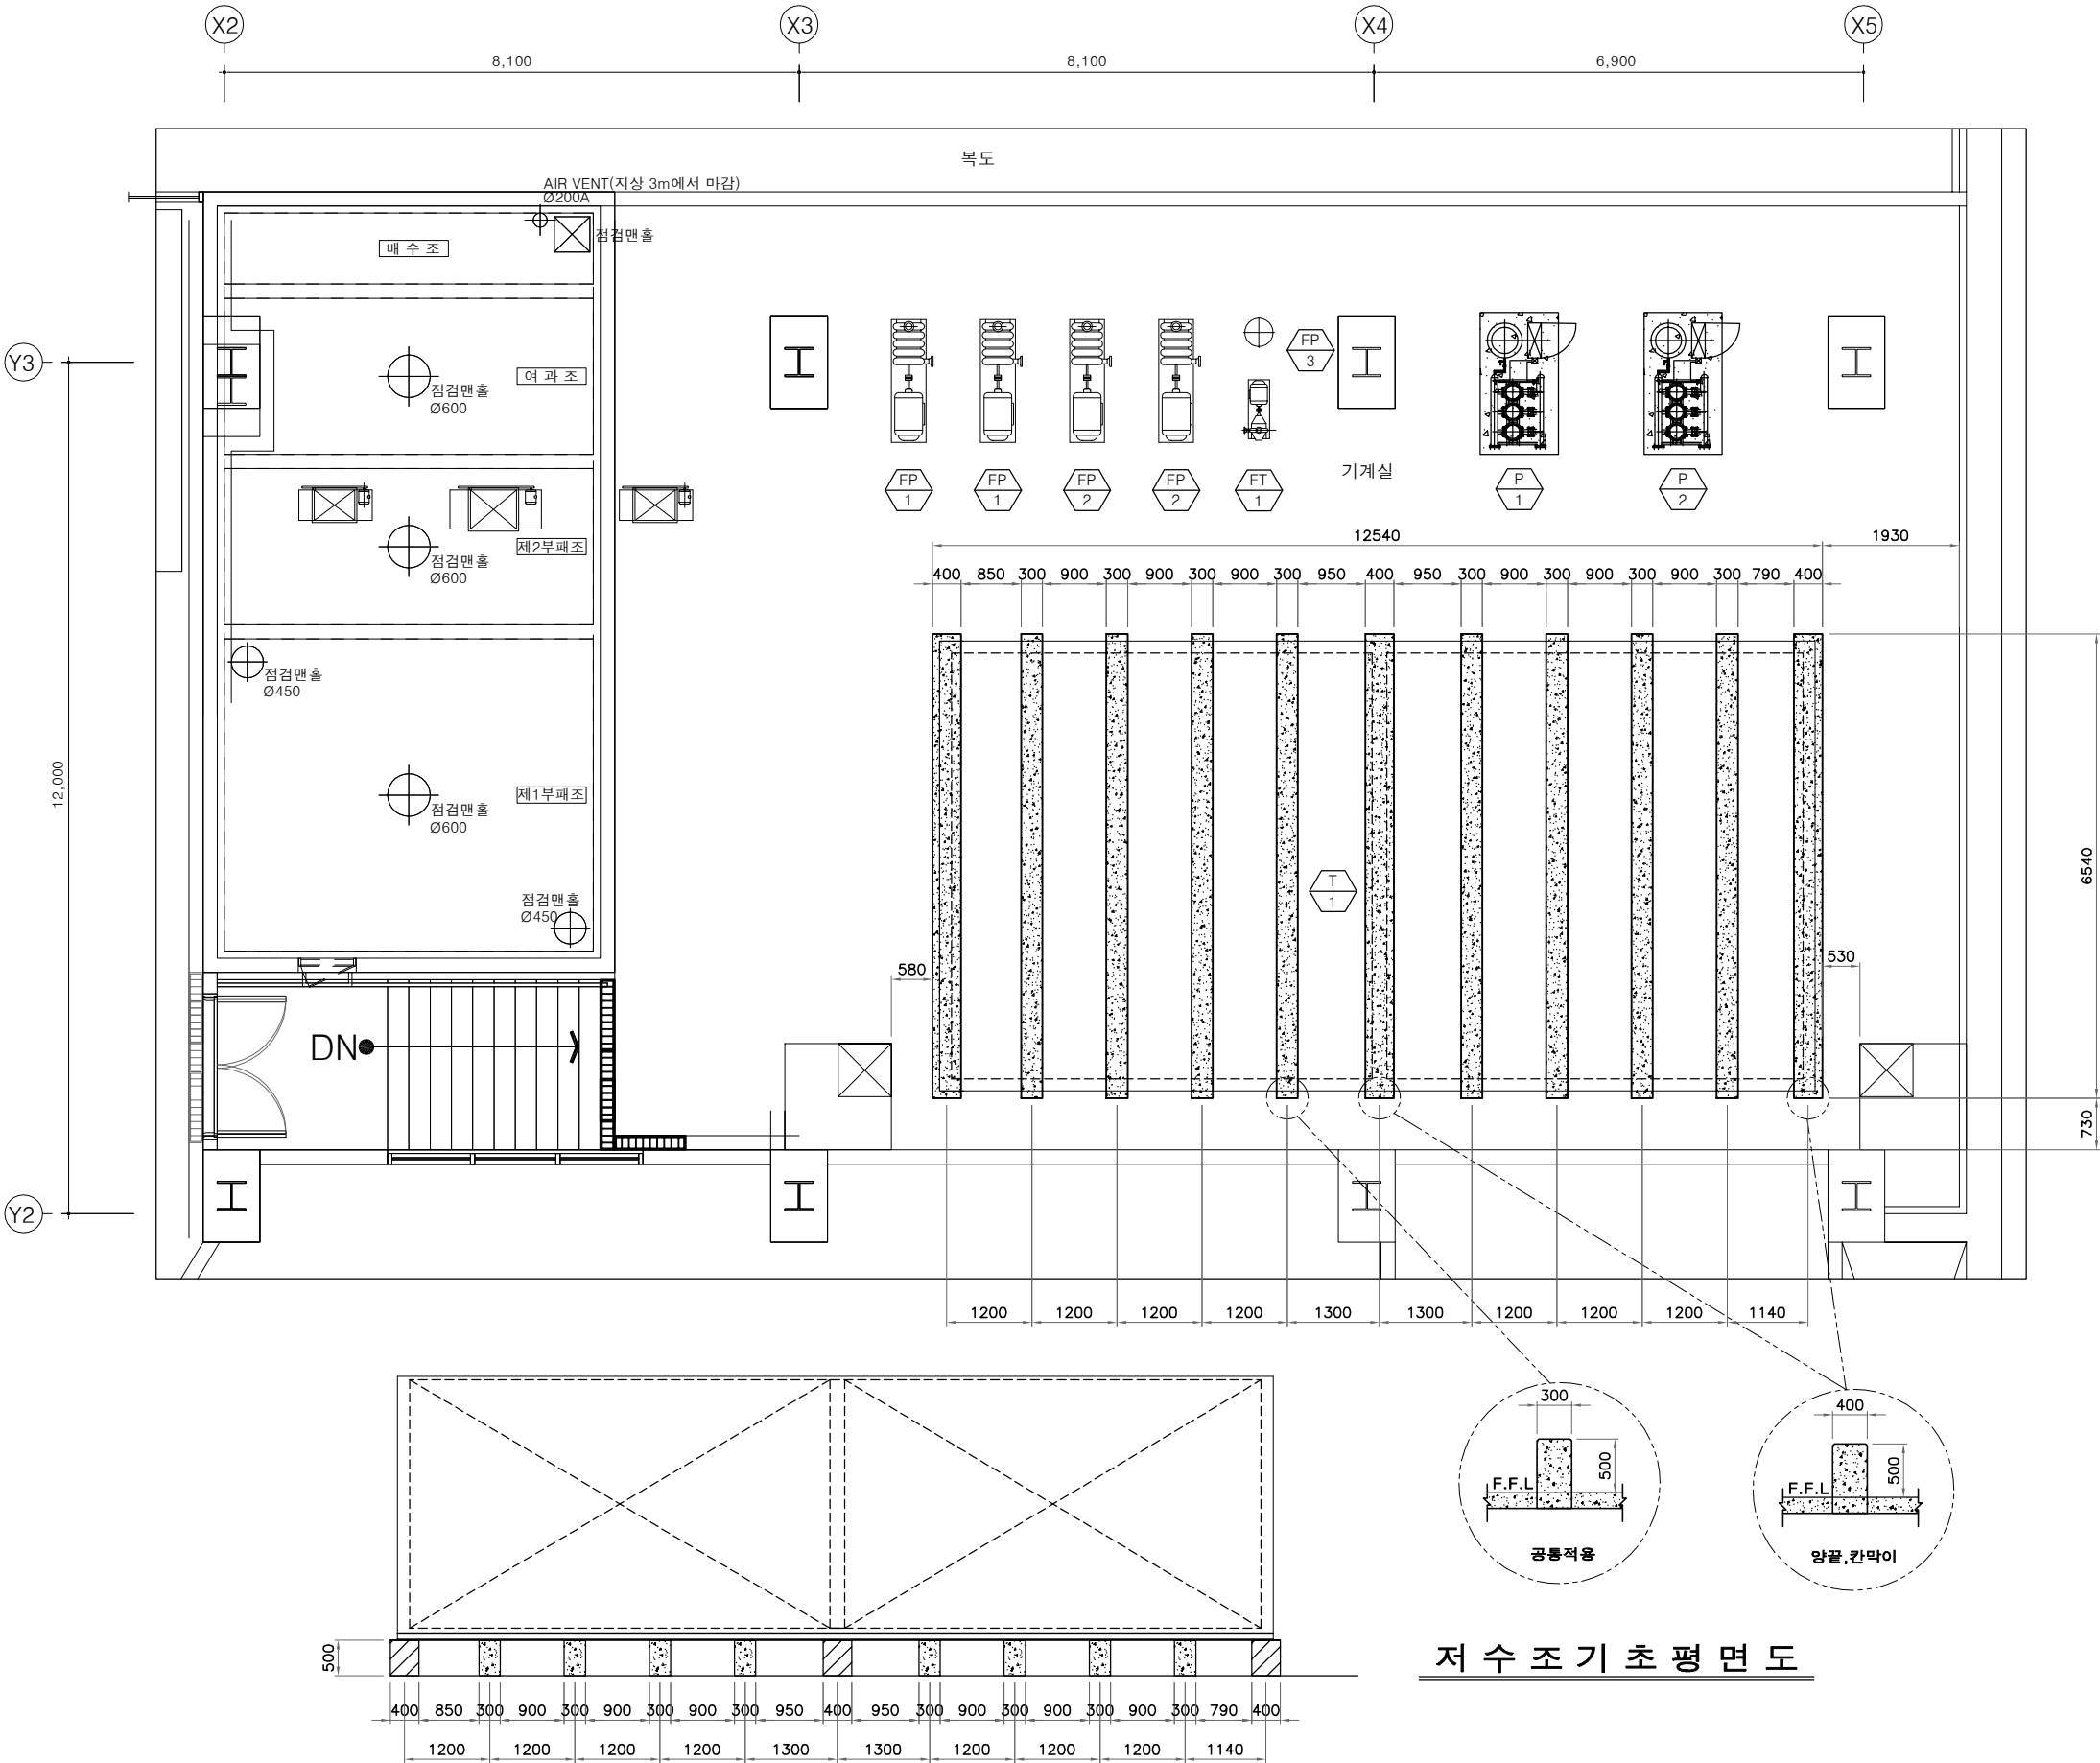

저수조기초평면도

REVISION	DESCRIPTION	DATE

ORDER ORGAN
티티벤처인베스트먼트
INVESTMENT
대표전화(02)579-8361
팩시밀리(02)579-8364
PROJECT OFFICE
ATEC (주)에이텍종합건축사사무소
ARCHITECTS & ASSOCIATES
대표전화(02)3462-6361
팩시밀리(02)3462-6362

저수조상세도 - 2

SCALE A1 : 1 / 50 A3 : 1 / 100	APPROVED ARCHITECT 김 상 길
DRAWN 한 현 이	DATE 2014. 03
CHECKED	DATE 2014. 03
CONSULTANT	

DRAWING NO. M-502

Technical drawing of a cable tray assembly. The drawing shows a cross-section of the assembly. Key components labeled include:

- H-BEAM** (100x100x6x8)
- PDF PANEL**
- PE Pipe Cover**
- Turnbuckle**
- INSIDE LINING** (4t PE SHEET)
- OUT JACKET** (0.45t COLOR JACKET)
- 사각 Pipe** (100x50x3.2t)

Technical drawing of the bottom panel assembly. The drawing shows a cross-section of the panel with the following layers and components labeled:

- 내부 바닥마감 PE Sheet 4.0t (Internal floor finish PE Sheet 4.0t)
- BOTTOM P.D.F PANEL
- 외부-각파이프 100 X 50 X 5t (External-angle pipe 100 X 50 X 5t)
- 내부-CHANNEL 100 X 50 X 5t X 7.5t (Internal-CHANNEL 100 X 50 X 5t X 7.5t)
- F.L (Floor Level)
- Con'C Pad (Concrete Pad)
- " ∇ " ANGLE(SS400) 50 x 50 x 4t (Angle (SS400) 50 x 50 x 4t)

내부 측면마감(PE Sheet 4.0t)

PDF PANEL

H-Beam 100x100x6x8t

(Color Sheet 0.45t)

200

50

200

Top Panel 50t


PE Pipe

Flanges

9

Technical drawing of the '시건장차' (Shikganjangcha) model. The drawing includes a top view and a side view. The top view shows a square frame with two horizontal bars, with dimensions of 1100mm by 1100mm. The side view shows a cross-section of the frame, with a width of 1000mm. A circular inset provides a detailed view of the corner joint, labeled '시건장차'.

MARK	P.D.F 저수조
PRODUCT SIZE	(12,000~208) x 6,000 x 3,500 h
CAPACITY	247.6 TON (기동용적제외: - TON, 유효용량:203 TON, 만수율:82%)
QUANTITY	1 기
NOTE	NOZZLE 위치 및 구경은 현장시공시 감독관 설정 위치 취부

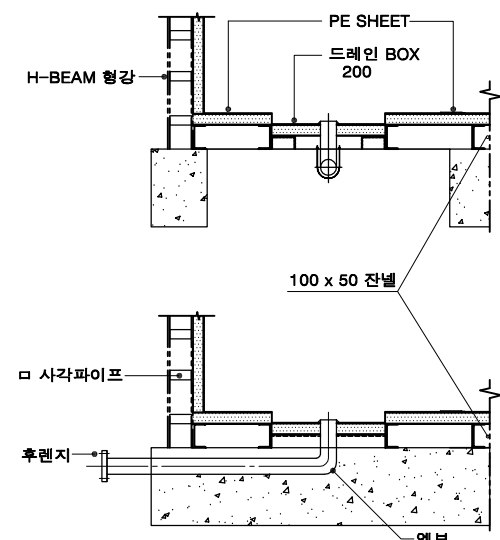

Technical drawing of a PE-elbow. The drawing shows a side view of the elbow with a 90-degree bend. Labels include:

- 동망 #40 매쉬 (40 Mesh Screen) pointing to the mesh on the top and bottom flanges.
- PE-ELBOW pointing to the main body of the elbow.
- A dimension line indicating a length of 6.
- A circular cross-section view on the right showing a mesh pattern.
- A scale bar at the bottom right indicating a length of 50.

PROJECT TITLE

성수동1가
지식산업센터
신축공사

■NOTES

REVISION	DESCRIPTION			DATE	
ORDER ORGAN					
		티터벤처인베스트먼트			
INVESTMENT		대표전화(02)579-8361			
		팩스밀리(02)579-8364			
PROJECT OFFICE					
		에이텍축합건축사사무소			
ARCHITECTS & ASSOCIATES		대표전화(02)3462-6361			
		팩스밀리(02)3462-6364			
DRAWING TITLE					
저수조상세도 - 3					
SCALE		APPROVED			
A1 : NONE					
A3 : NONE					
DRAWN		DATE		2014. 03	
					
CHECKED		DATE		2014. 03	
CONSULTANT					
DRAWING NO.					
M-503					